


Ведомость рабочих чертежей		
Лист	Наименование	Примечание
0	Ведомость рабочих чертежей	
1	Обмерный план	
2	План демонтажа перегородок	
3	План монтажа перегородок	
4	3D Вид монтажа	
5	План расстановки мебели	
6	План расстановки мебели 3D	
7	План расстановки мебели с размерами	
8	Расположение ВК_Кухня и Санузел №8	
9	Расположение ВК_Санузел № 9 и спецификация сантехнических приборов	
10	План отопления	
11	План напольных покрытий	
12	План потолка	
13	План расстановки осветительного оборудования	
14	План расстановки розеток	
15	План привязки приборов освещения к выключателям	
16	План обозначения разверток стен	
17	Прихожая	
18	Прихожая	
19	Прихожая 3D Вид	
20	Гостиная	
21	Гостиная	
22	Гостиная	
23	Кухня	

Ведомость рабочих чертежей		
Лист	Наименование	Примечание
24	Кухня	
25	Кухня 3D ВИД	
26	Коридор	
27	Коридор	
28	Спальня №5	
29	Спальня №5	
30	Спальня №6	
31	Спальня №6	
32	Спальня №6	
33	Спальня №7	
34	Спальня №7	
35	Спальня 3D Вид	
36	Санузел №8	
37	Санузел №8	
38	Санузел №9	
39	Санузел №9	
40	Санузел 1-2,3D Вид	
41	Двери	
42	Спецификация_План монтажа перегородок	
43	Общая спецификация_Стены	
44	Общая спецификация_Полы, Потолки, Отопительные приборы	
45	Общая спецификация_Сантехника	
46	Общая спецификация_Электрика и Бытовая техника	
47	Общая спецификация_Электроника и Бытовая техника	

Ведомость рабочих чертежей		
Лист	Наименование	Примечание
48	Спецификация План расстановки мебели	
49	Спецификация План напольного покрытия	
50	Спецификация План расстановки осветительного оборудования	
51	Спецификация План расстановки розеток	
52	Спецификация сантехнического оборудования и аксессуаров	
53	Коллаж гостиная	
54	Коллаж спальня	
55	Коллаж прихожая	

Стадия	Лист	Листов
АИ		
ВЕДОМОСТЬ РАБОЧИХ ЧЕРТЕЖЕЙ		
Luxhouse_studio		

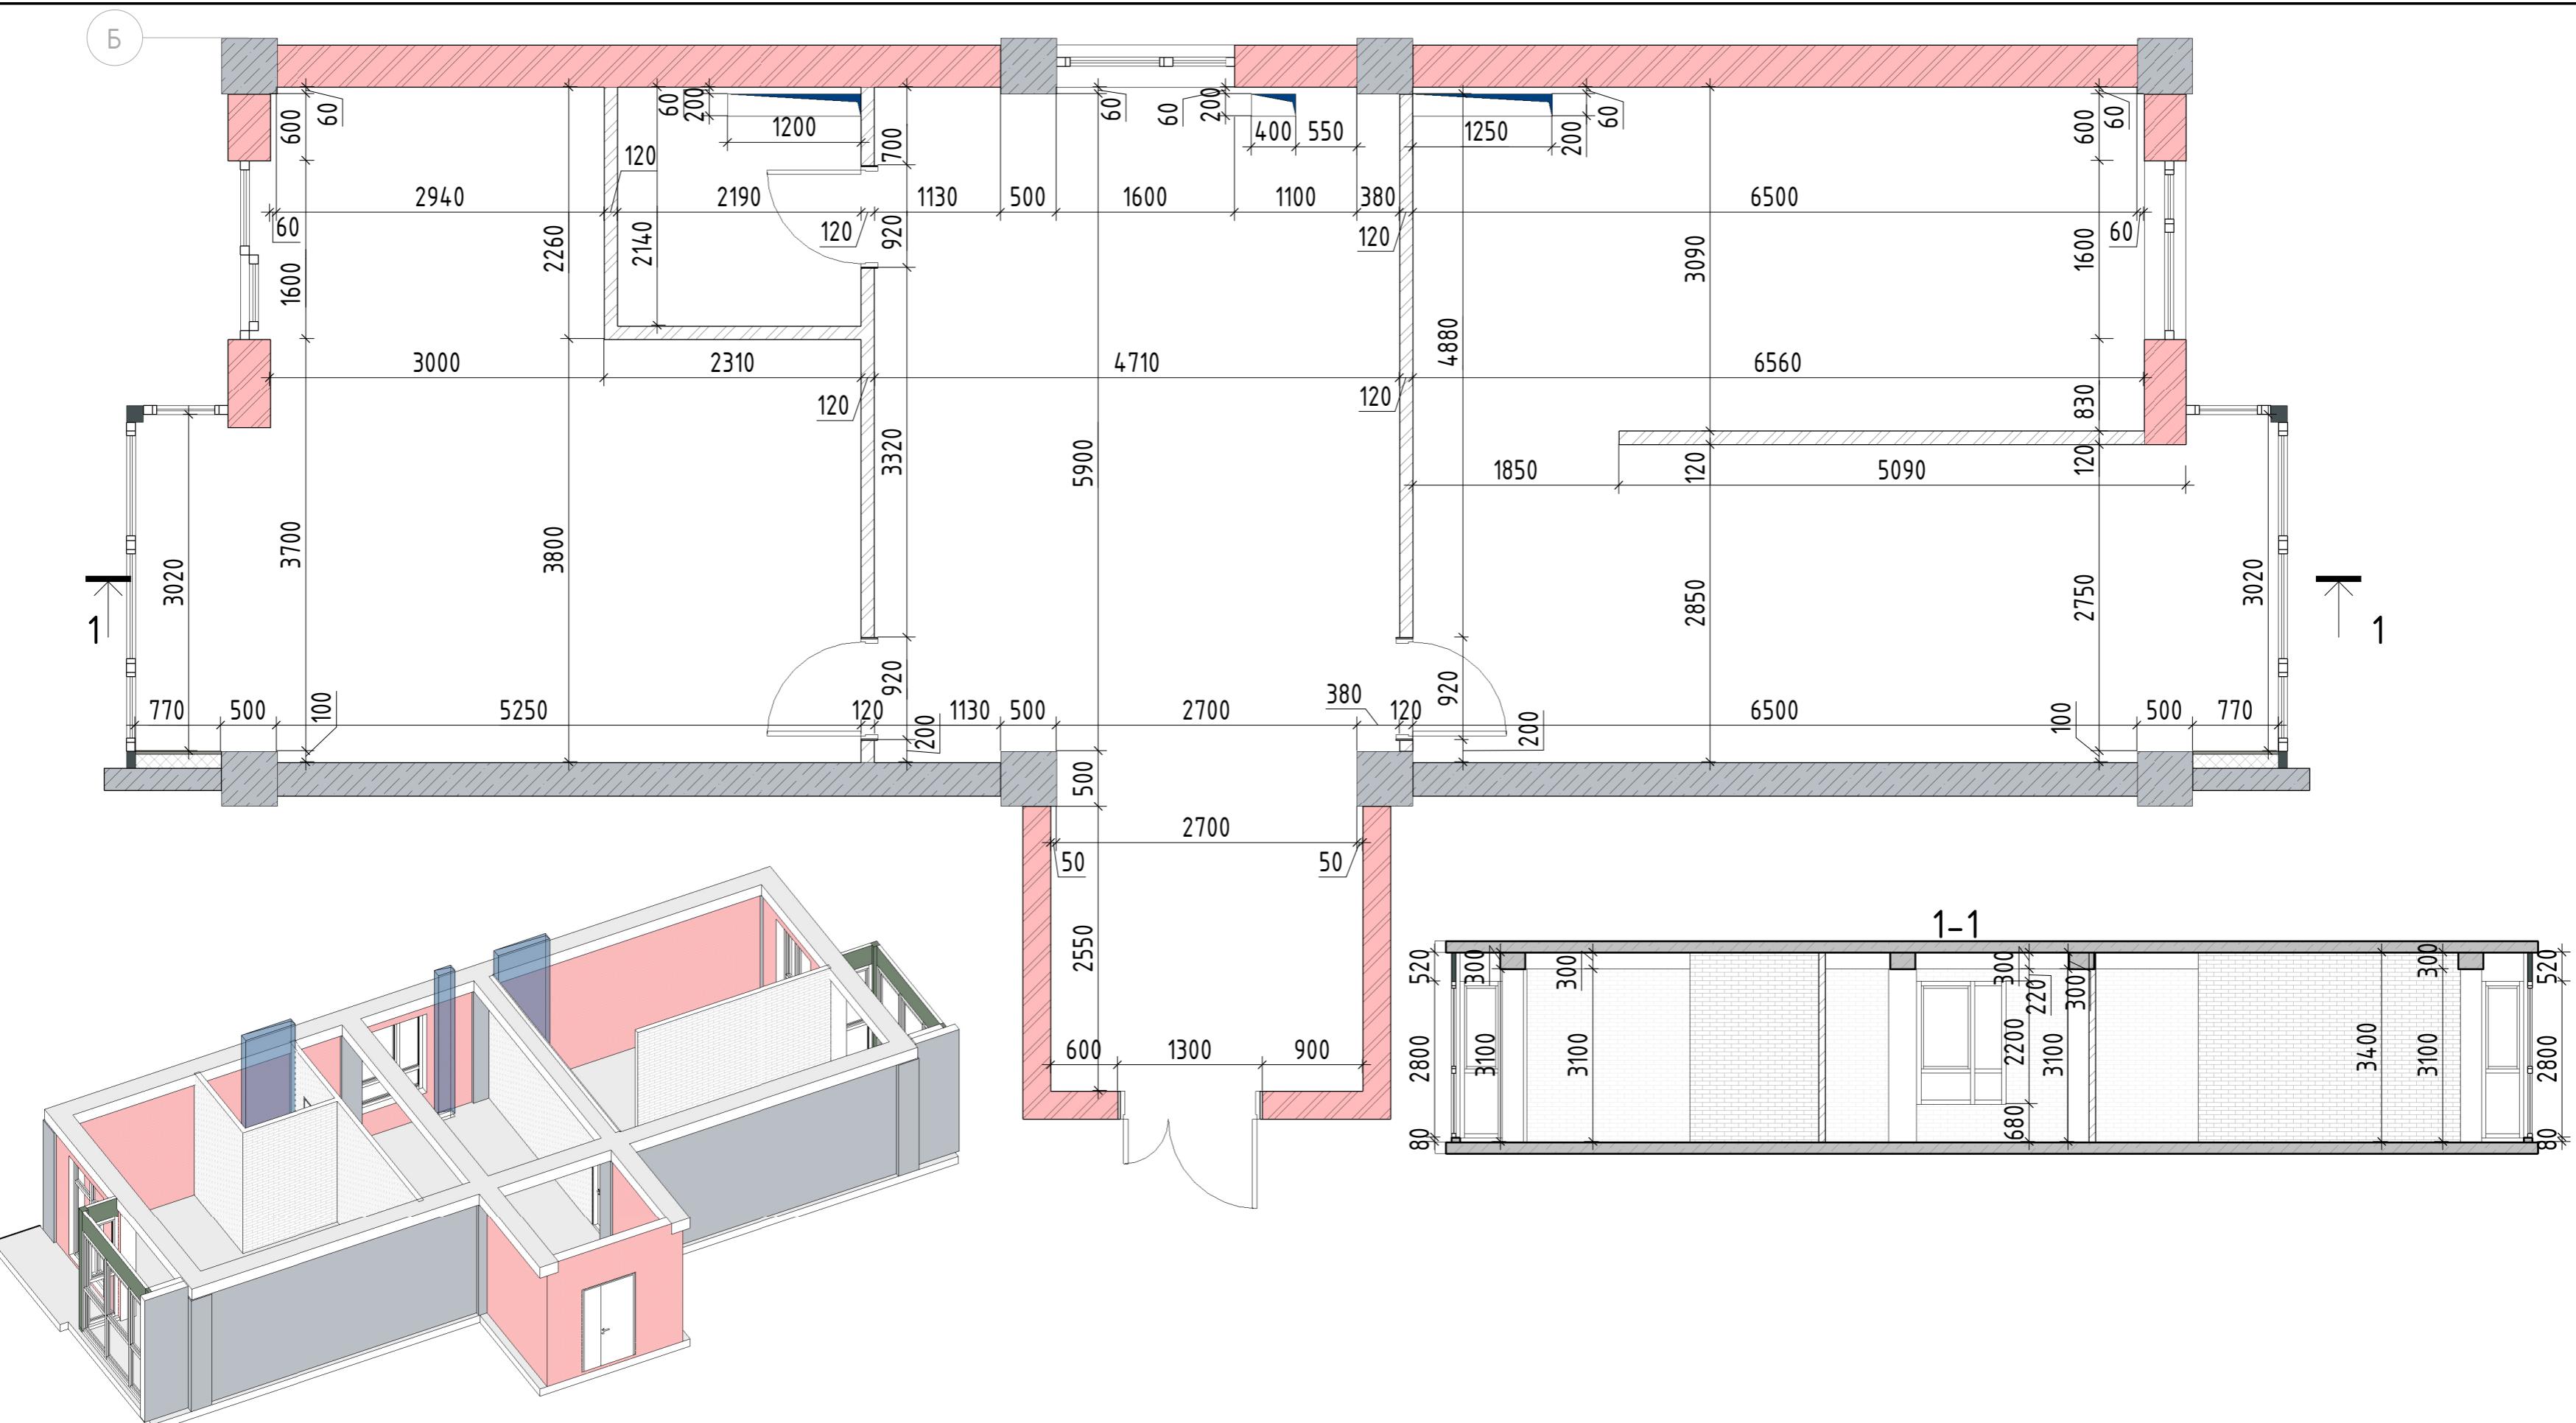



Примечания:

1. За отмечку 0.000 принята отмечка чистого пола проектируемых помещений.
2. Размеры указаны в миллиметрах.
3. Размеры уточнять по месту.

Дизайнер			
Заказчик			

ОБМЕРНЫЙ ПЛАН

Б

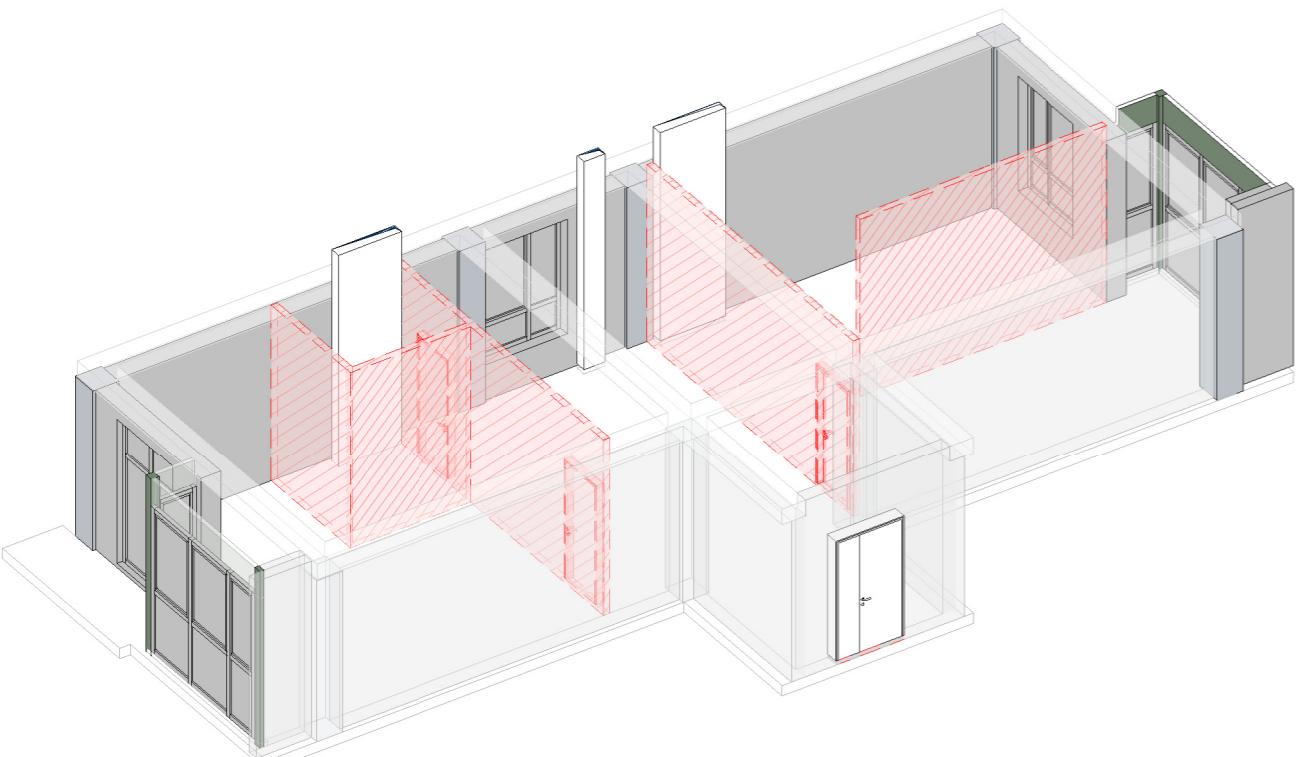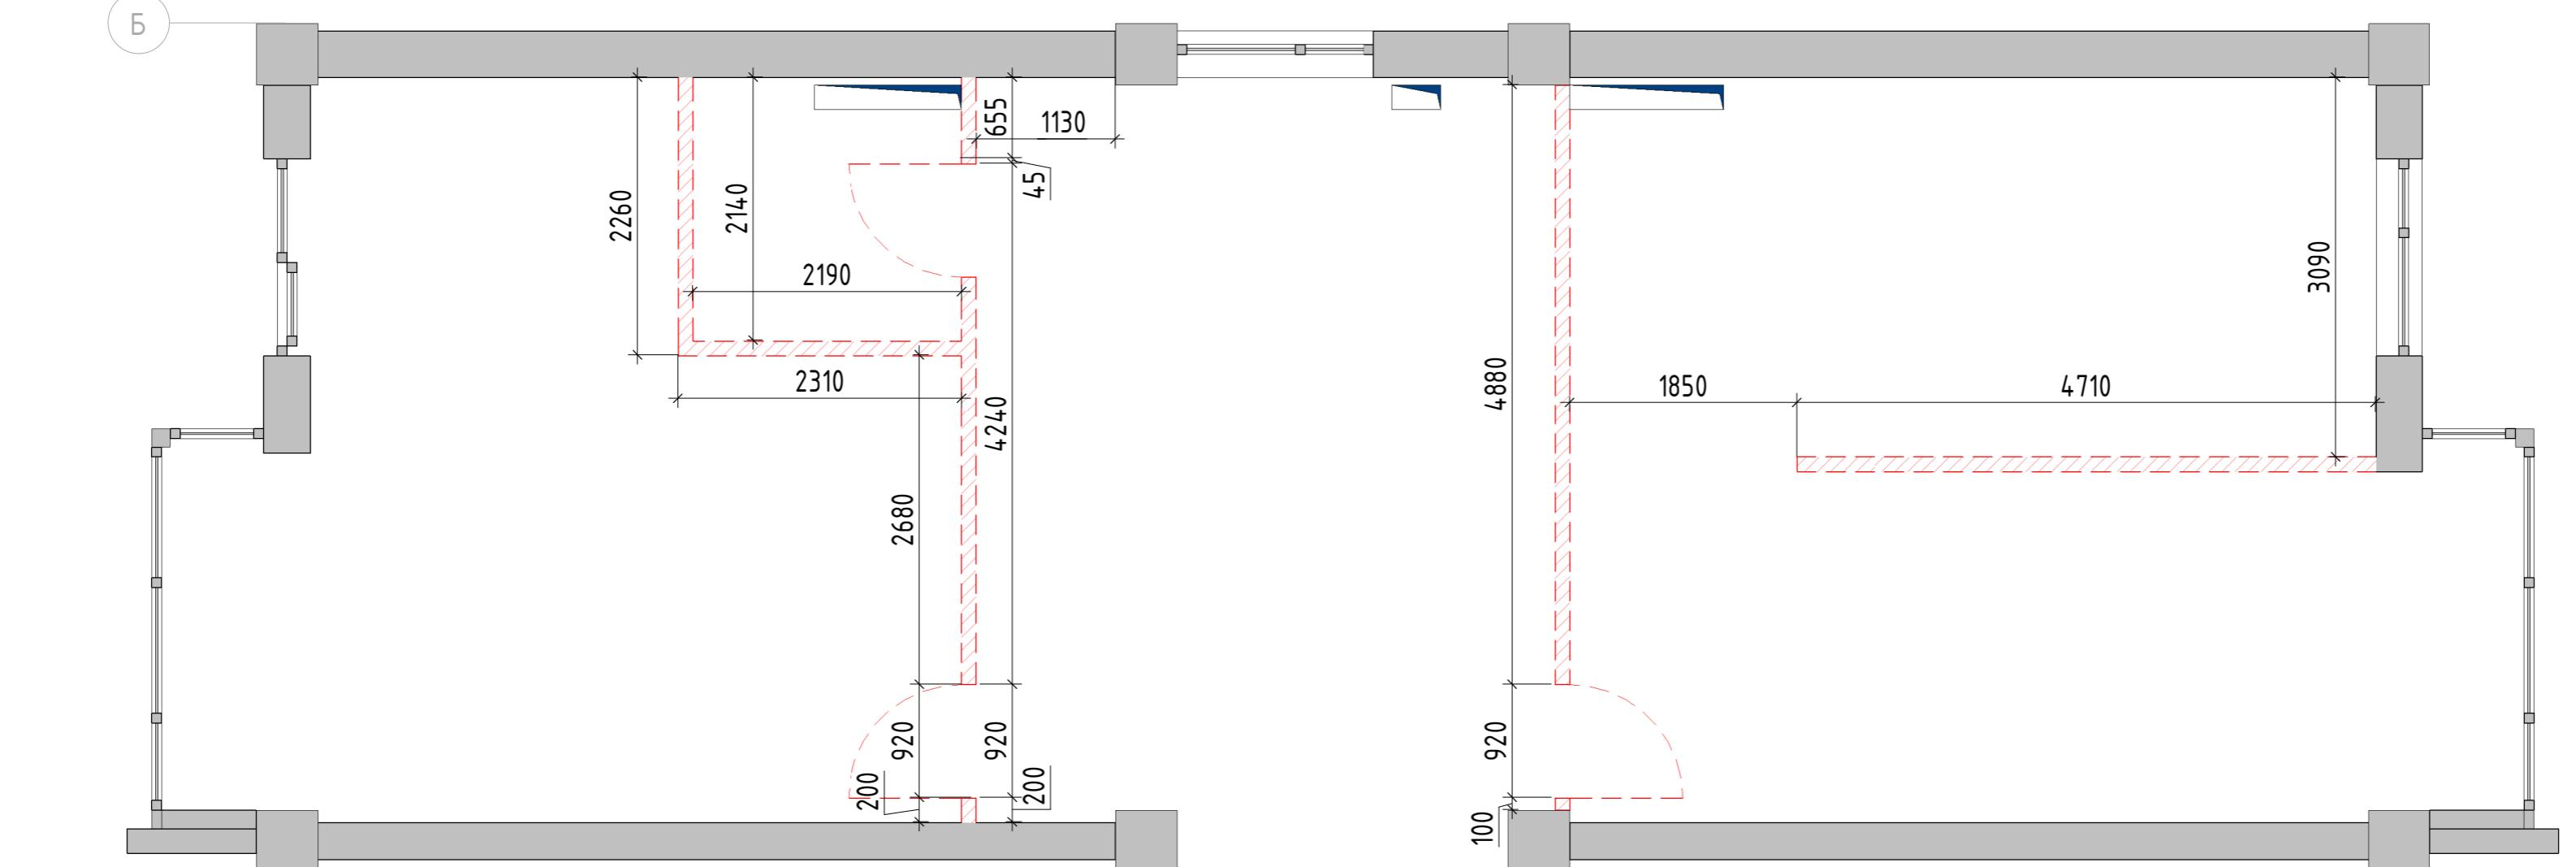

Условные обозначения:

- Существующие стены
- Демонтируемые перегородки

Примечания:

1. За отметку 0.000 принята отметка чистого пола проектируемых помещений.
2. Высота потолков _____.
3. Размеры даны в миллиметрах.
4. Фактические размеры могут незначительно отличаться. Проверить по месту.


Дизайнер			
Заказчик			

ПЛАН ДЕМОНТАЖА
ПЕРЕГОРОДОК

Luxhouse_studio

Формат: А3

Стадия	Лист	Листов
АИ		

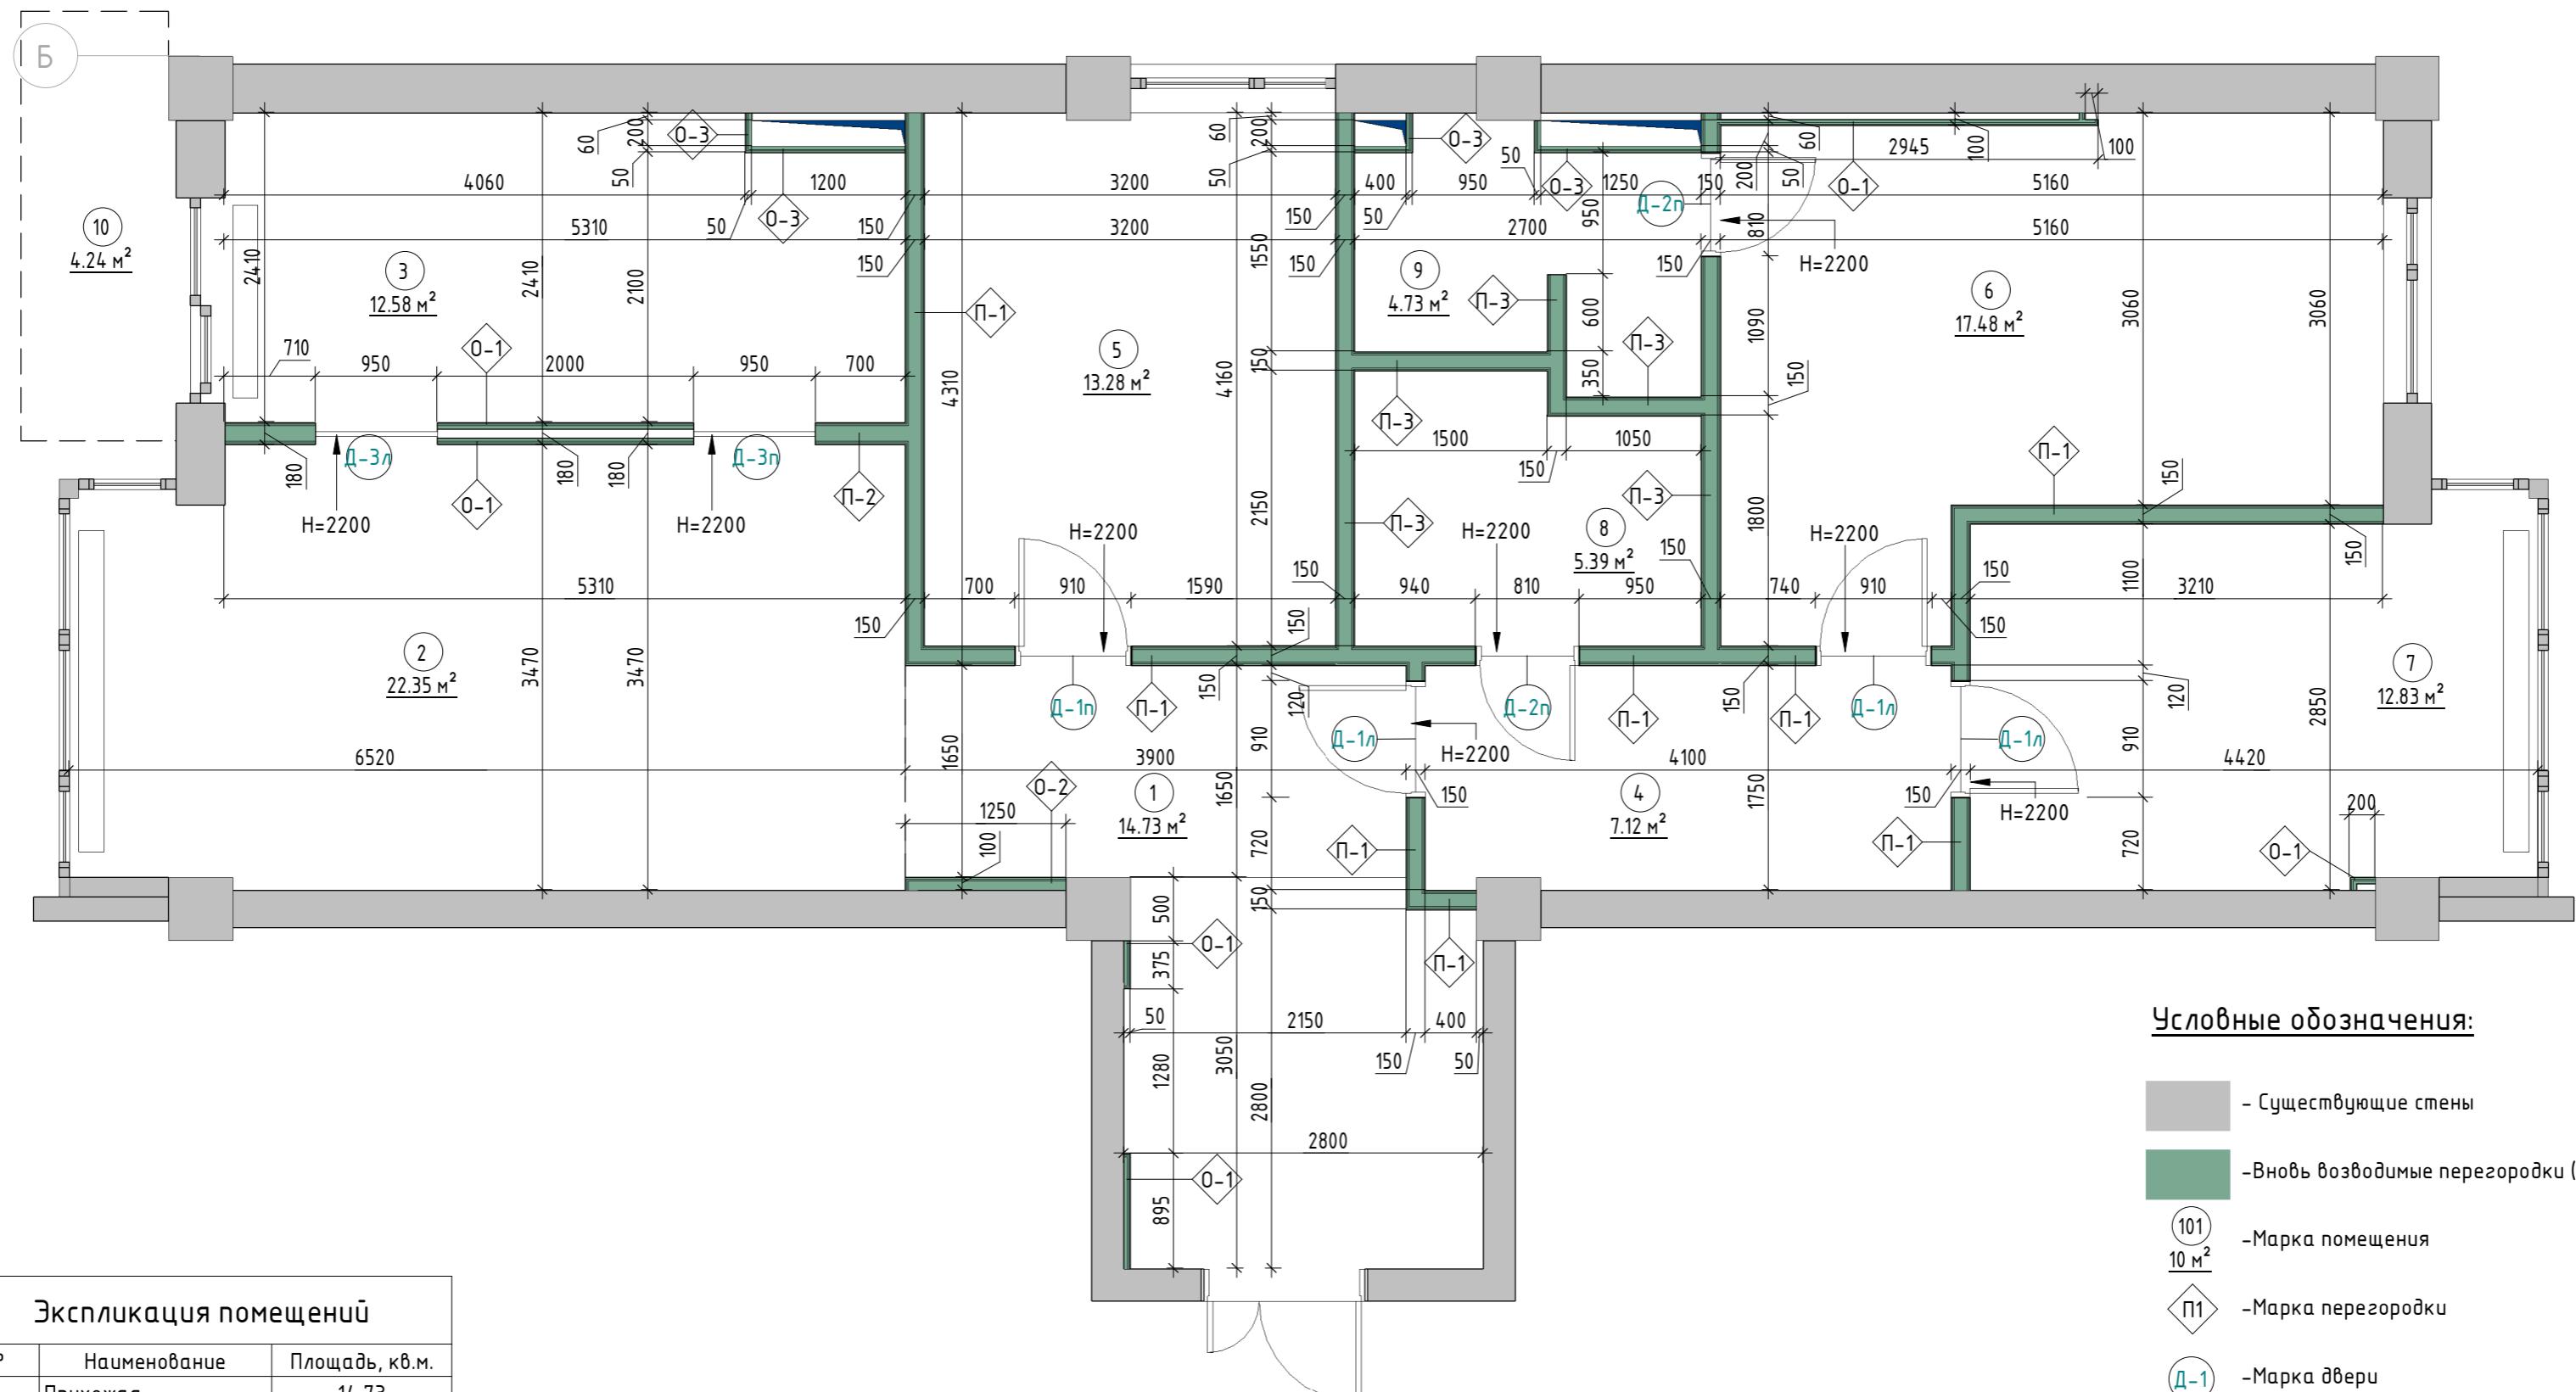

Экспликация помещений		
№	Наименование	Площадь, кв.м.
1	Прихожая	14.73
2	Гостинная	22.35
3	Кухня	12.58
4	Коридор	7.12
5	Спальня	13.28
6	Спальня	17.48
7	Спальня	12.83
8	Санузел	5.39
9	Санузел	4.73
10	Балкон	4.24
		114.73



Примечания:

- За отметку 0.000 принята отметка чистого пола проектируемых помещений.
- Размеры указаны в миллиметрах.
- Размеры уточнять по месту.

Дизайнер	Лист	Листов
АИ		

ПЛАН МОНТАЖА
ПЕРЕГОРОДОК

Luxhouse_studio

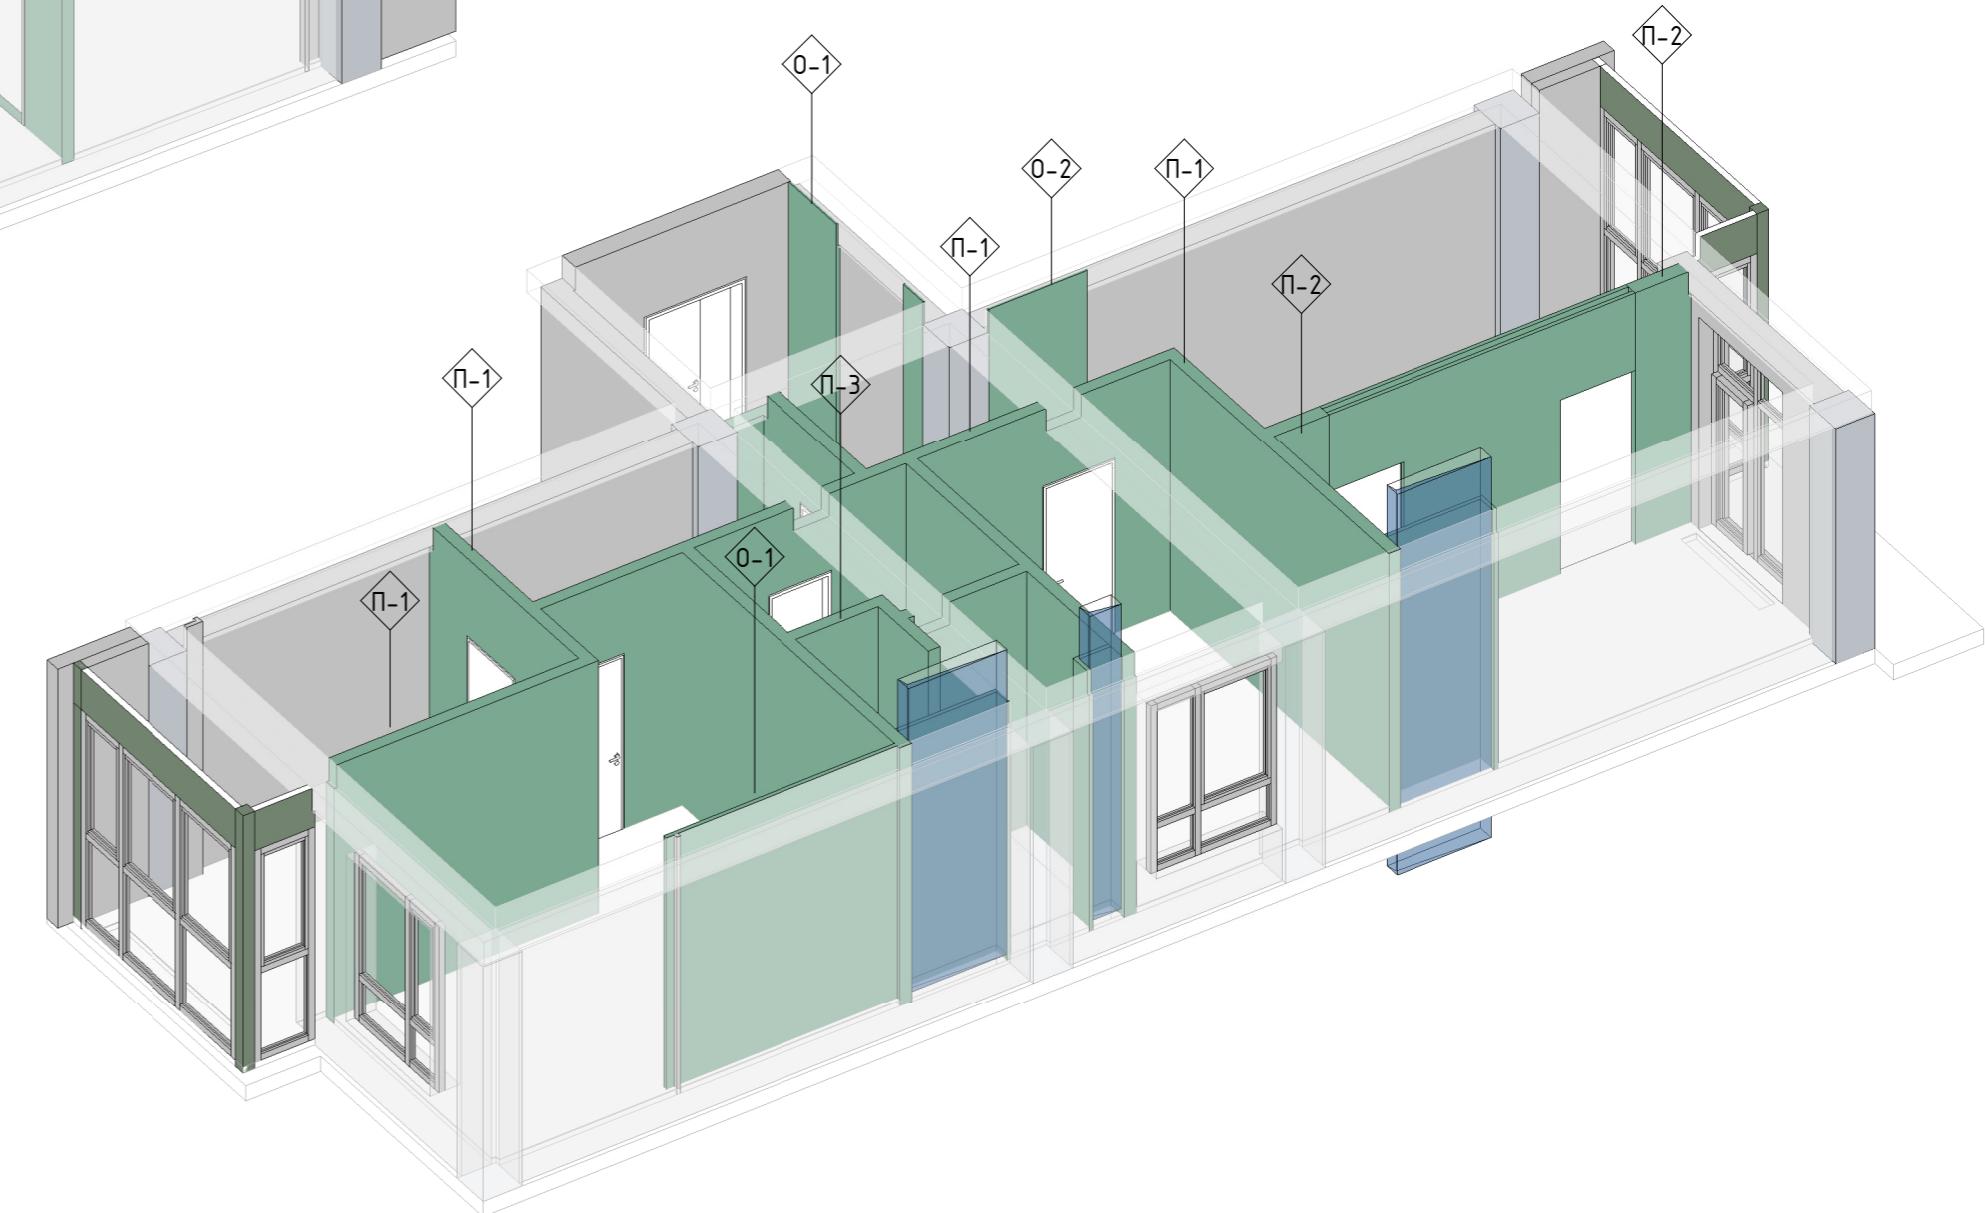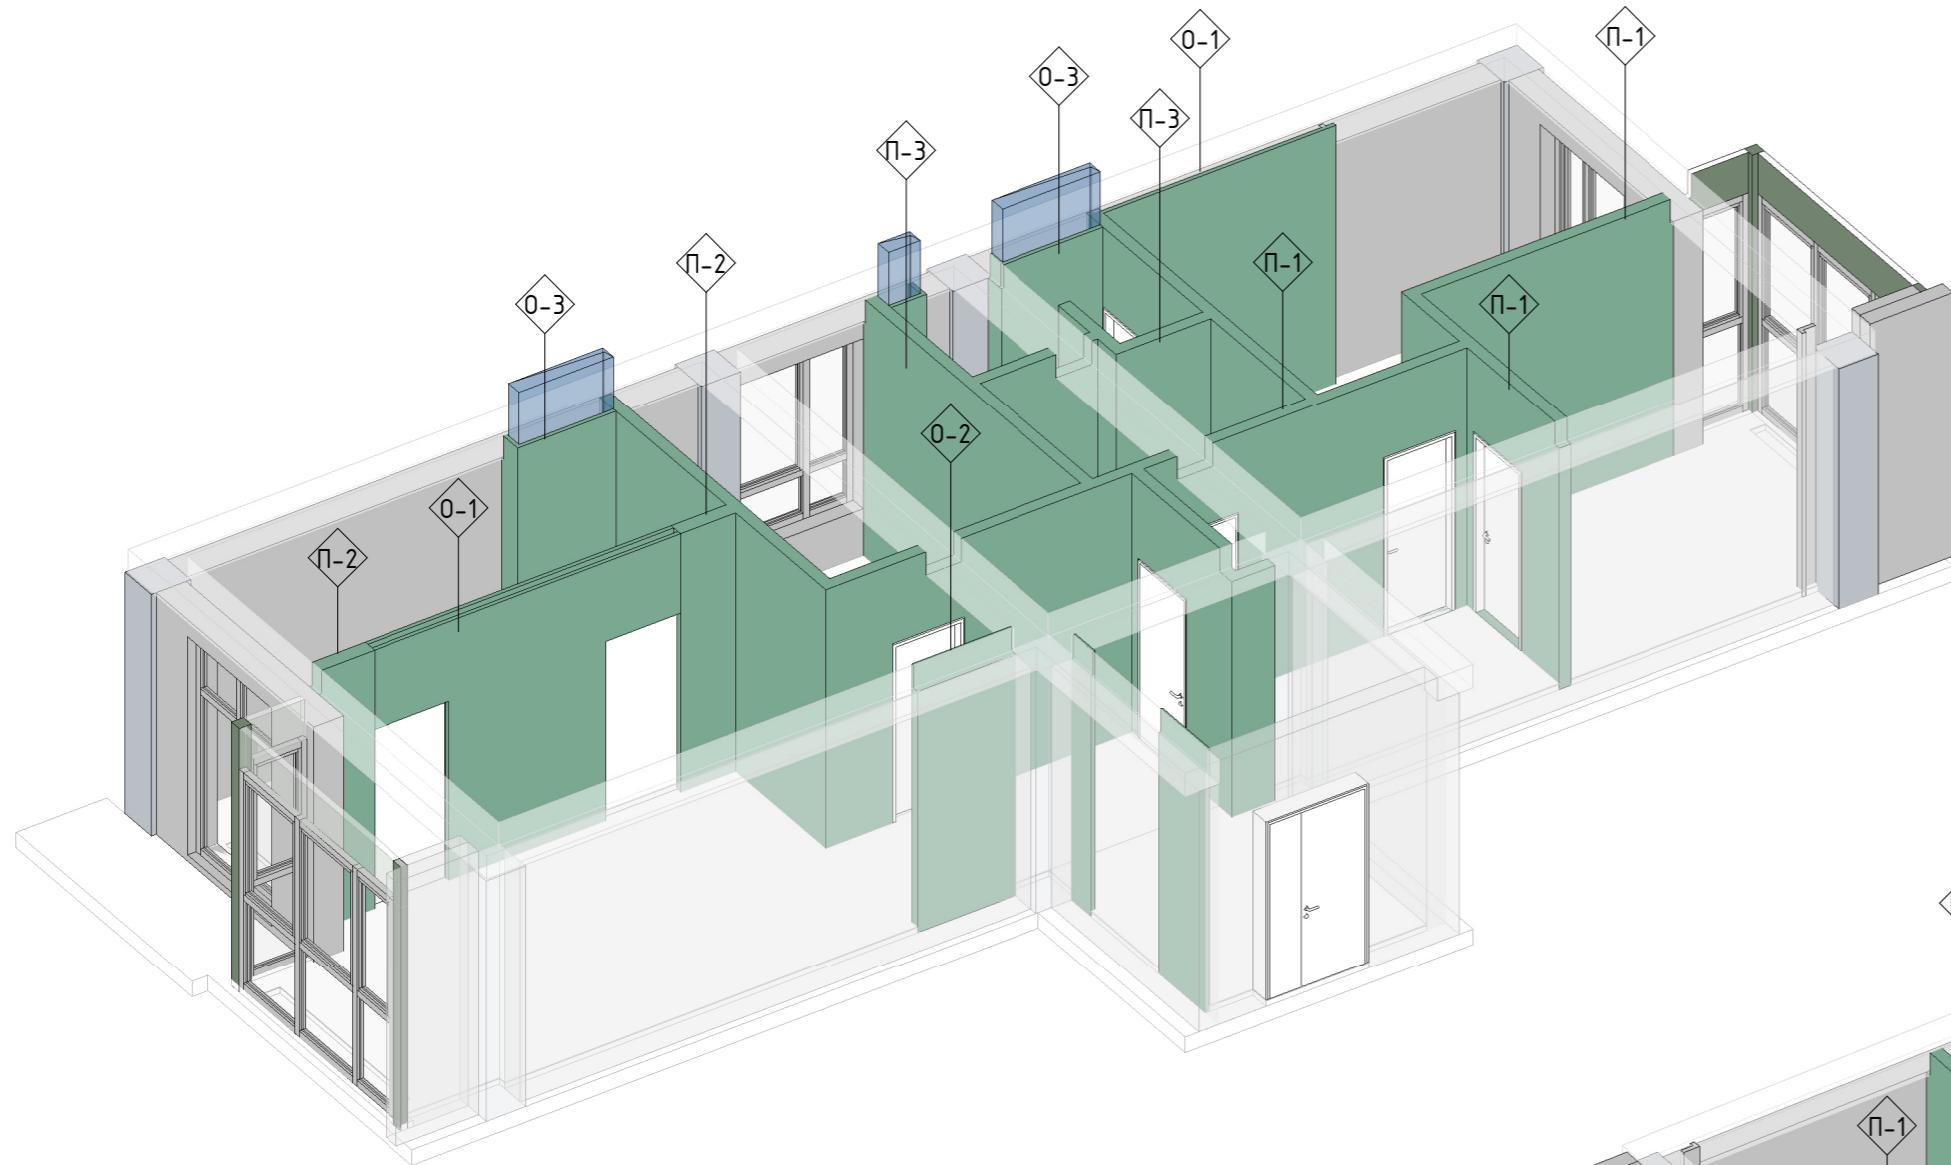

Условные обозначения:

- - Существующие стены
- - Вновь возводимые перегородки (ГКЛ)
- (101)
10 м² - Марка помещения
- П11 - Марка перегородки
- Д-1 - Марка двери


Дизайнер			
Заказчик			

3D ВИД ПЛАН МОНТАЖА
ПЕРЕГОРОДОК

Luxhouse_studio

Формат: А3

Стадия	Лист	Листов
АИ		

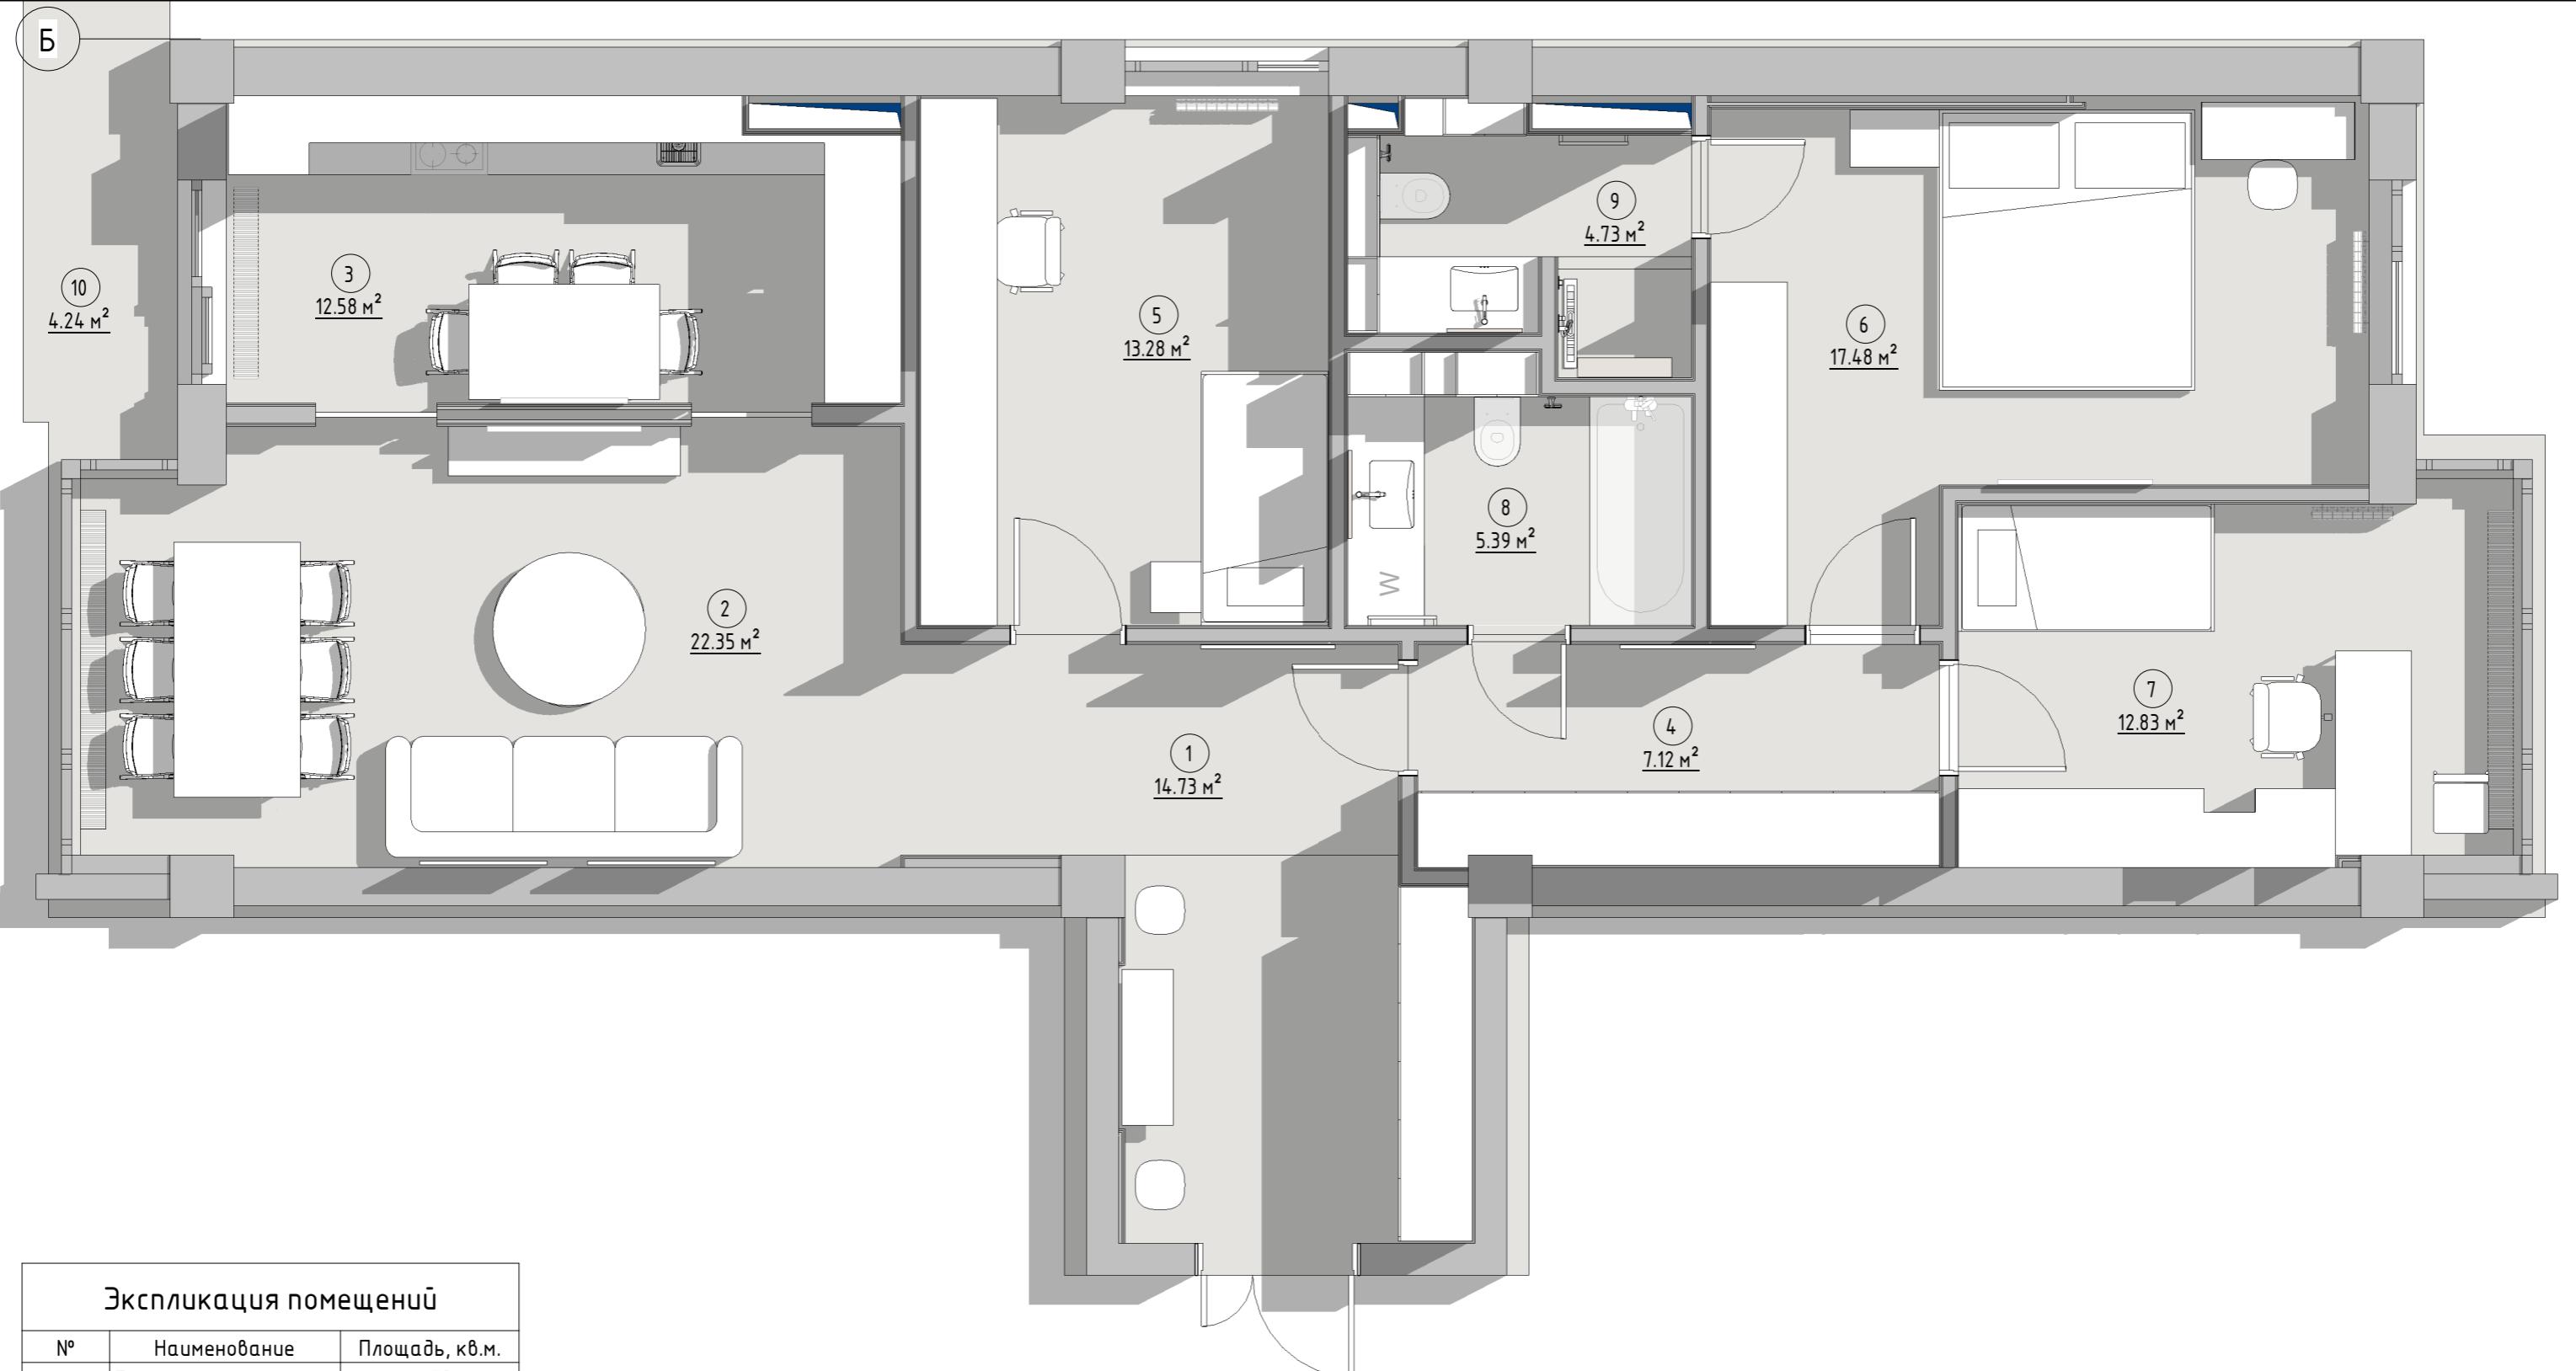


Экспликация помещений

№	Наименование	Площадь, кв.м.
1	Прихожая	14.73
2	Гостиная	22.35
3	Кухня	12.58
4	Коридор	7.12
5	Спальня	13.28
6	Спальня	17.48
7	Спальня	12.83
8	Санузел	5.39
9	Санузел	4.73
10	Балкон	4.24
		114.73

Стадия	Лист	Листов
Дизайнер		
Заказчик		
АИ		

ПЛАН РАССТАНОВКИ МЕБЕЛИ

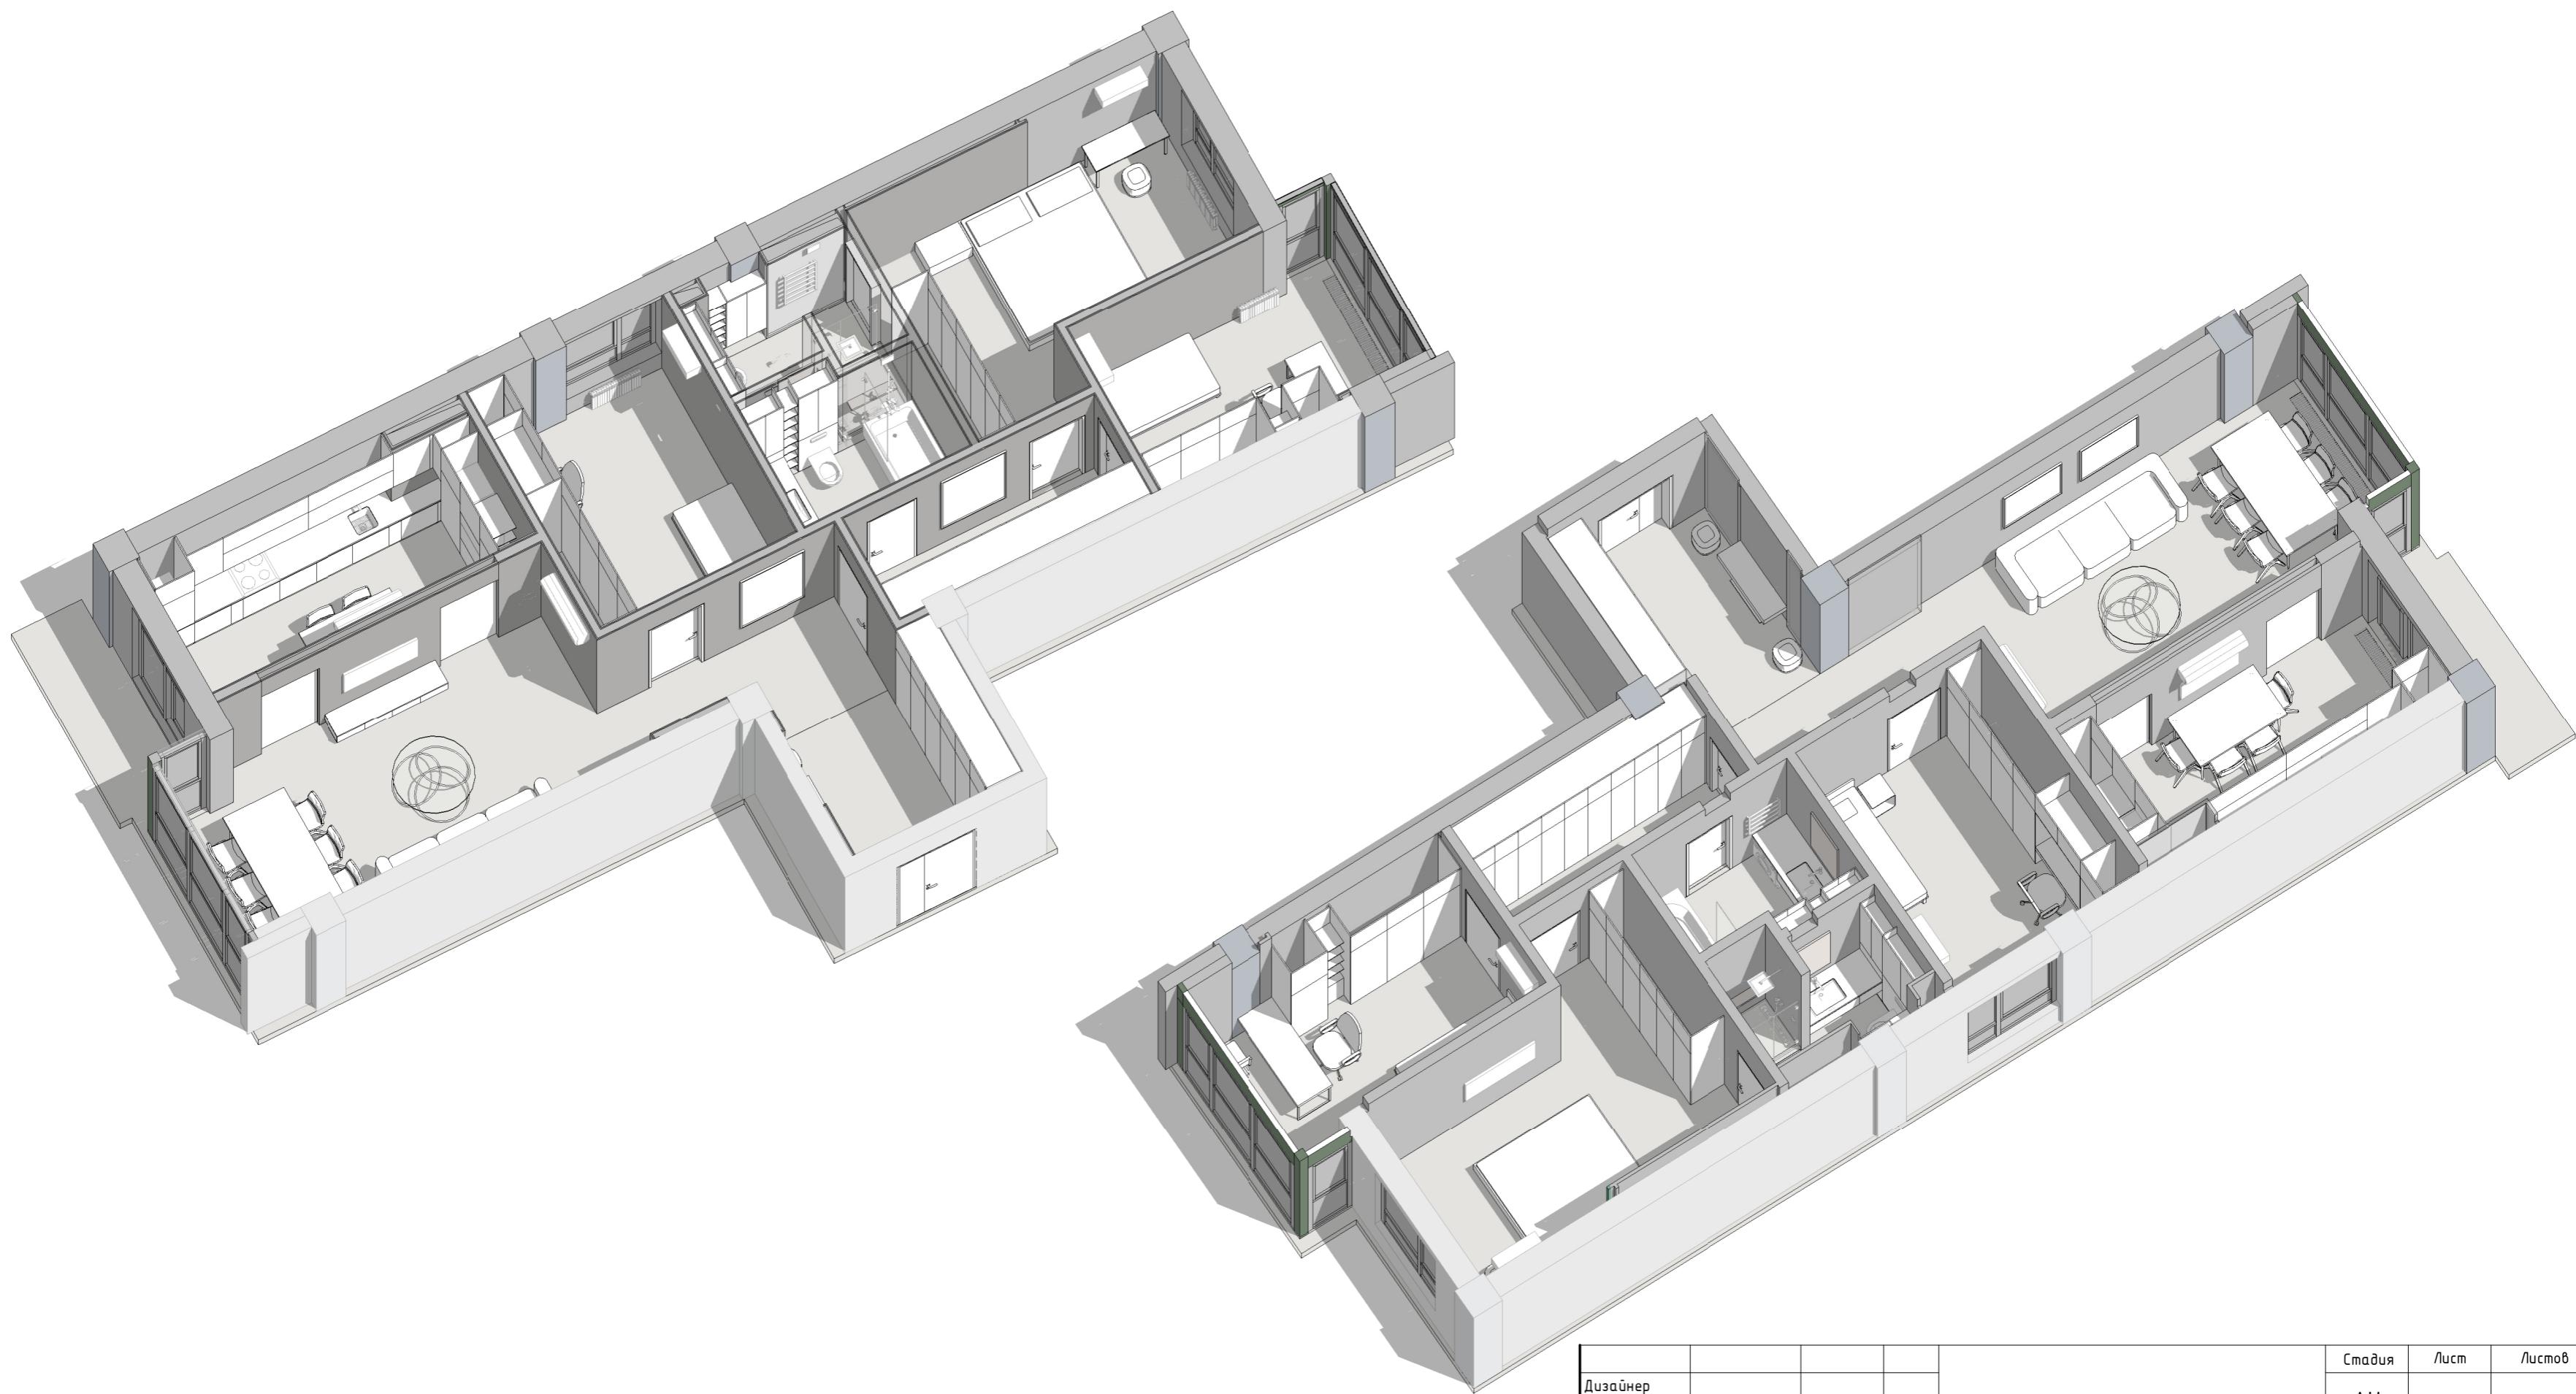

Дизайнер			
Заказчик			


3D ВИД РАССТАНОВКИ
МЕБЕЛИ

Luxhouse_studio

Формат: А3

Стадия Лист Листов

АИ

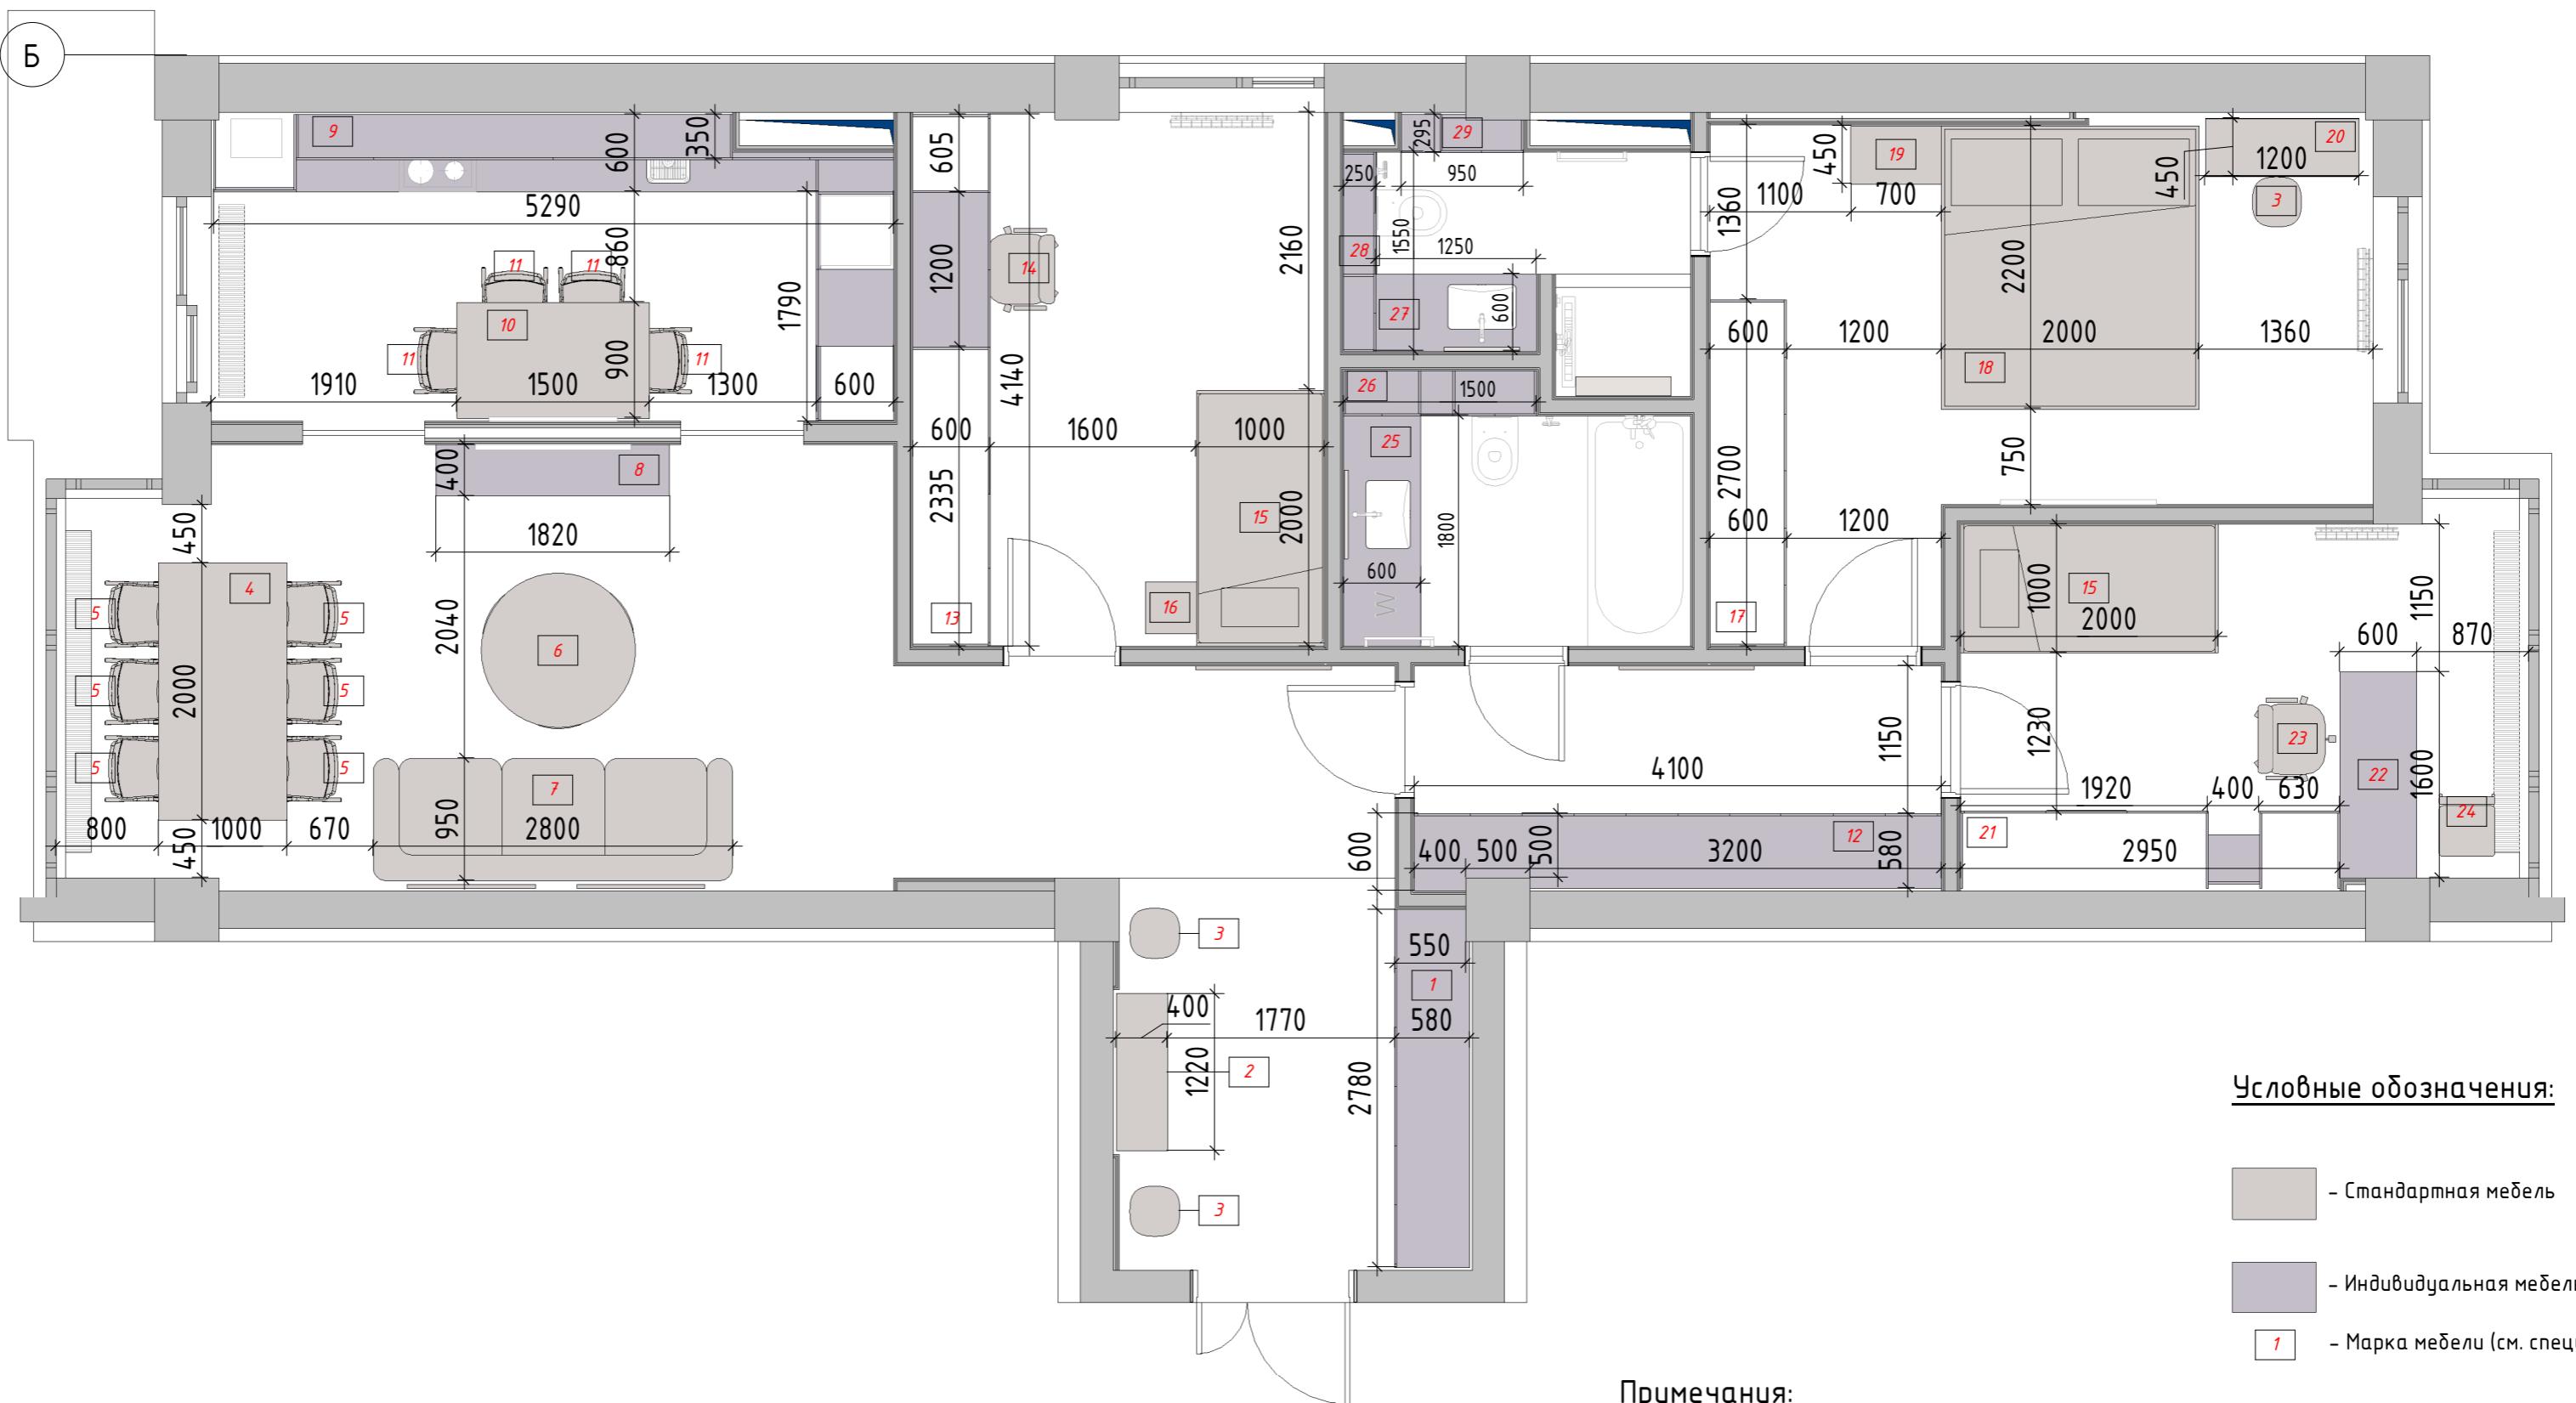

Примечания:

- За отметку 0.000 принята отметка чистого пола проектируемых помещений.
- Размеры указаны в миллиметрах.
- Размеры уточнять по месту.
- Смотреть совместно с развертками помещений.

Дизайнер			
Заказчик			


ПЛАН РАССТАНОВКИ МЕБЕЛИ
С РАЗМЕРАМИ

Luxhouse_studio


Формат: А3

Стадия	Лист	Листов
AI		


Расположение ВК_Санузел №8

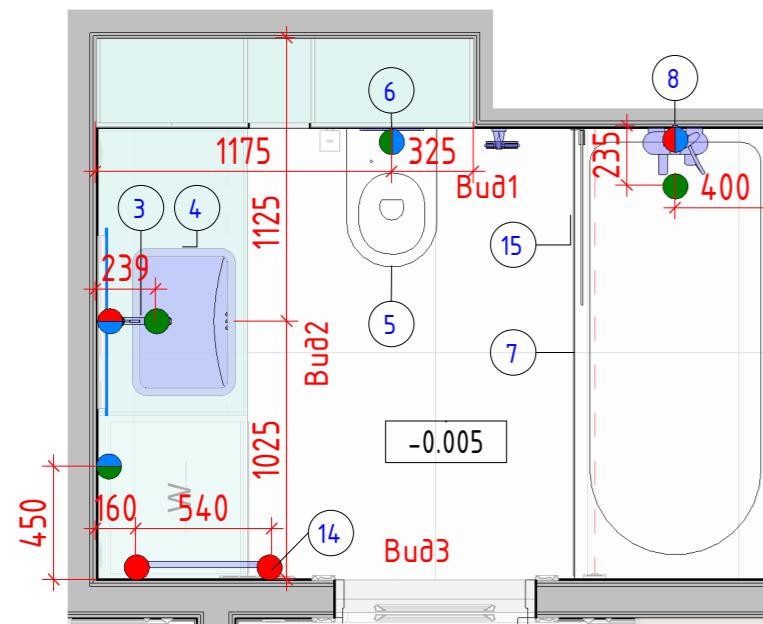


Вид 1

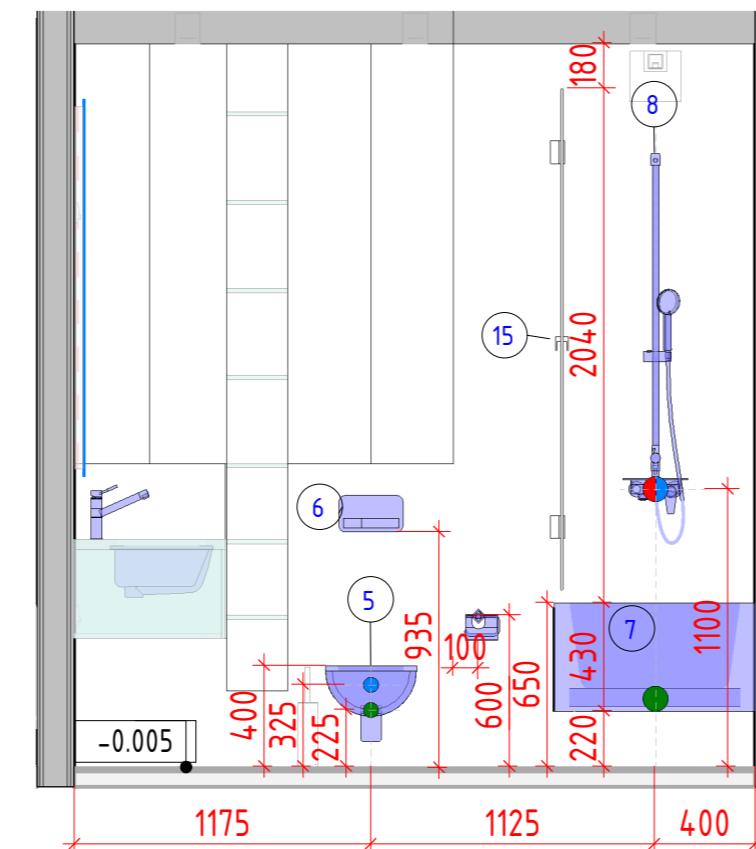



Вид 2

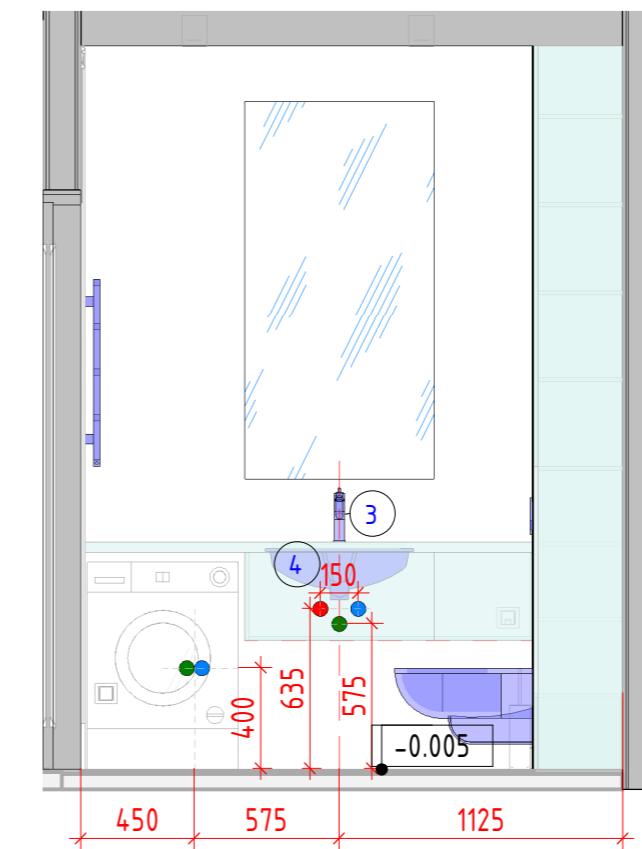

Вид 3

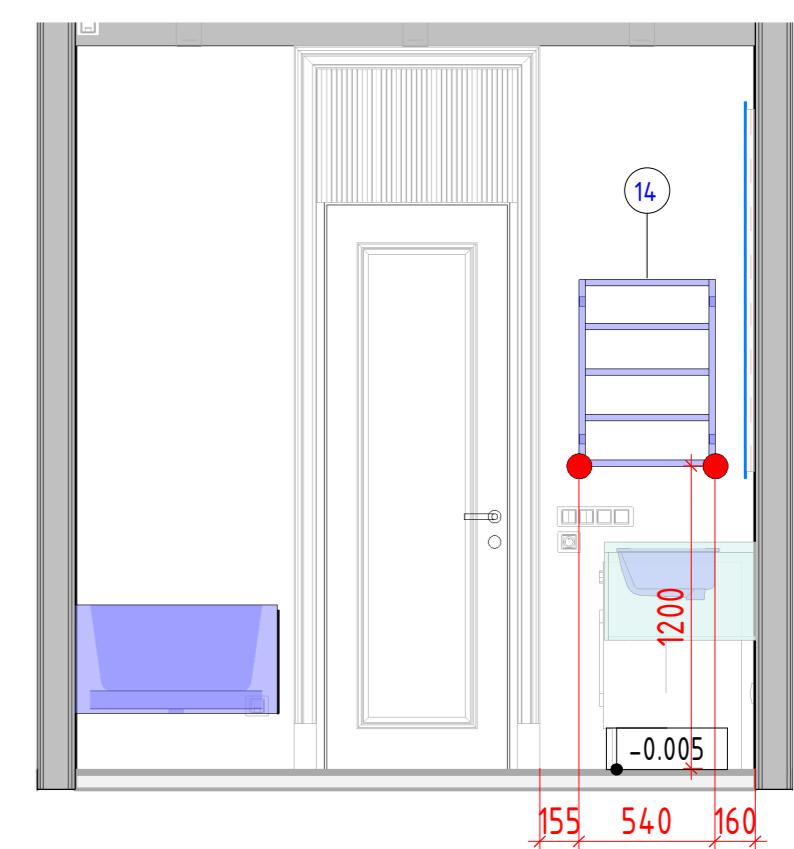

Расположение ВК_Кухня

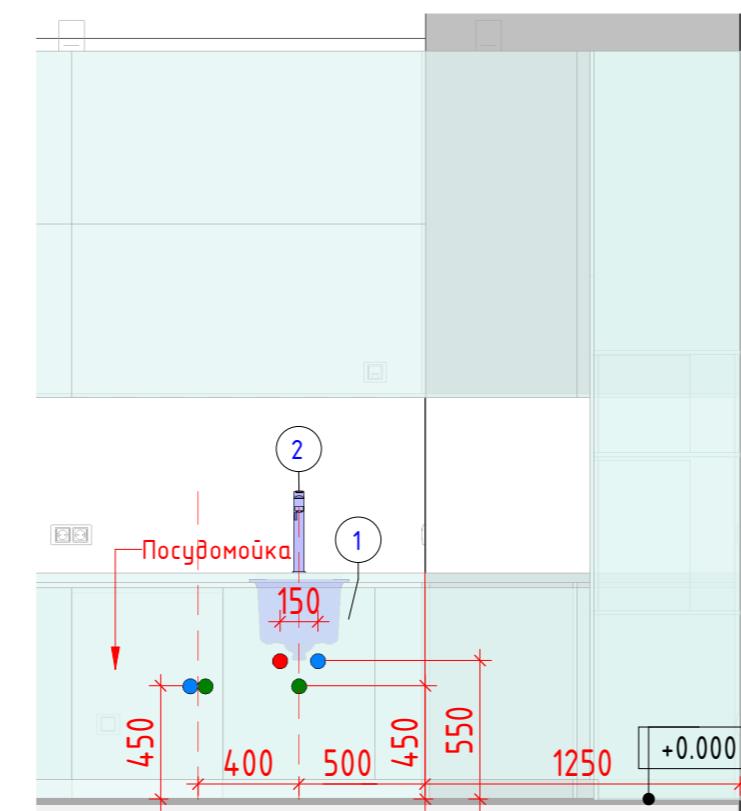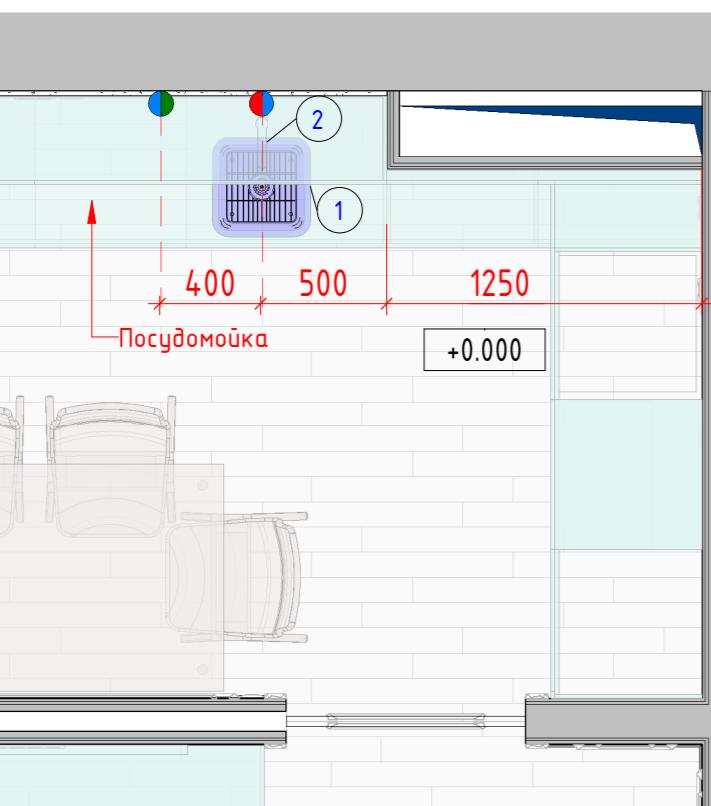

Числовые обозначения:

- ±0.000 — Высотная отметка
- № 150 м2 — Марка помещений
- (1) — Марка сантехнического оборудования
- — Марка сантехнических принадлежностей
- — Холодная вода
- — Горячая вода
- — Канализация


Примечание:

Расстояние между точками крепления полотенцесушителя зависит от выбранной модели


Дизайнер			
Заказчик			

РАСПОЛОЖЕНИЕ ВК КУХНЯ
И САНУЗЕЛ


Расположение ВК_Санузел №9

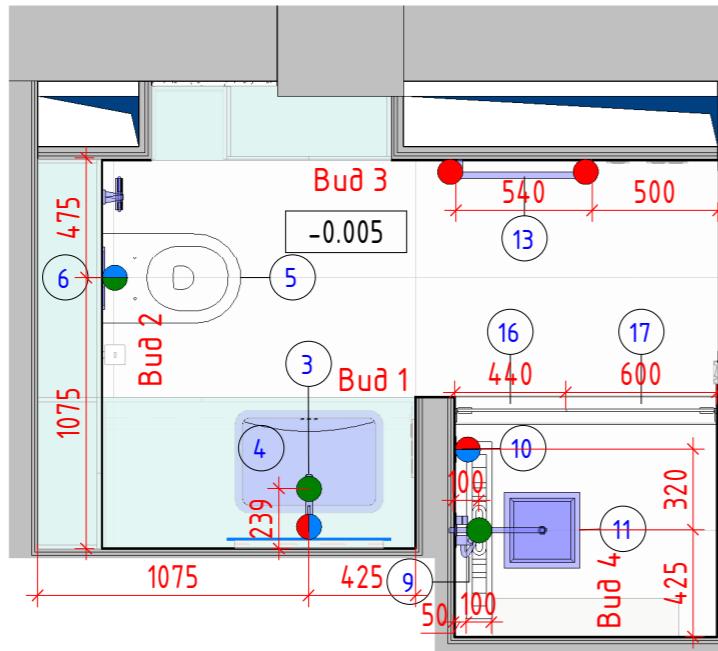



Вид 2

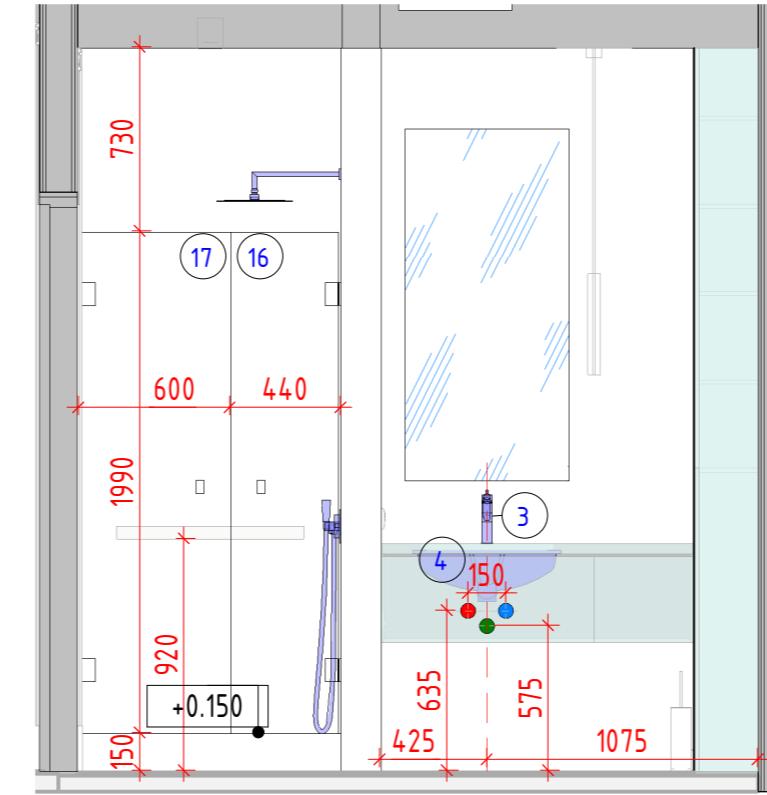

Вид 1

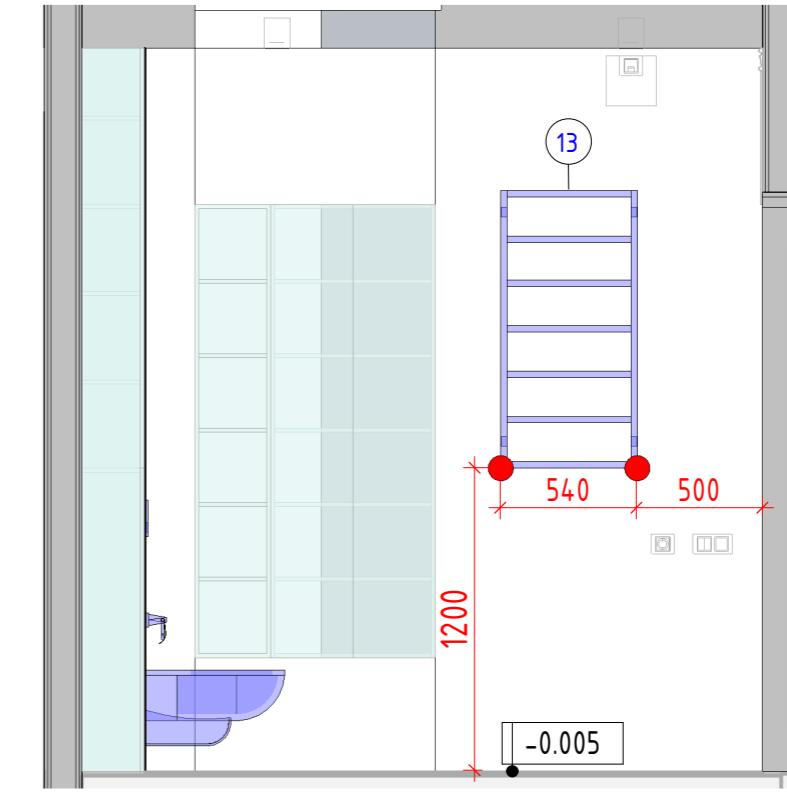

Вид 3

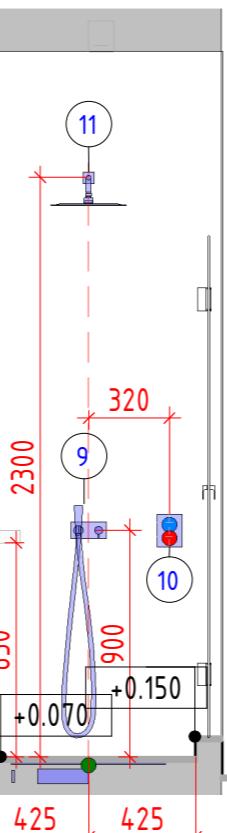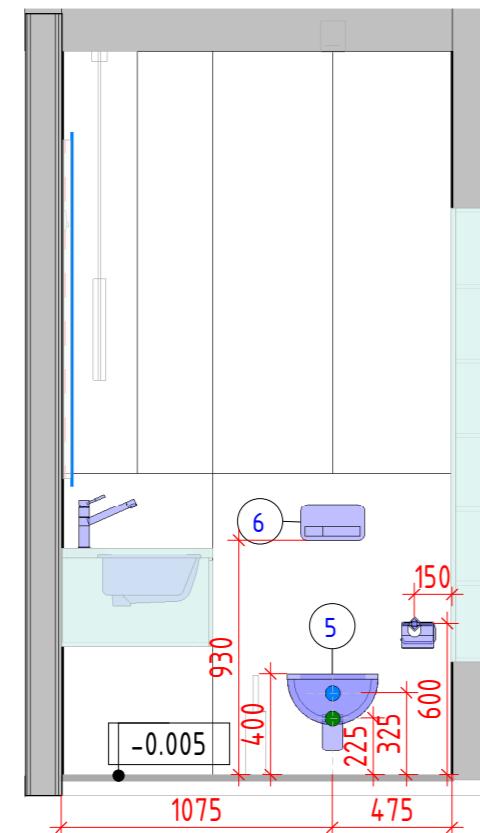

Вид 4

Черновые обозначения:

- ± 0.000 — Высотная отметка
- № 150 м² — Марка помещений
- (1) — Марка сантехнического оборудования
- т1 — Марка сантехнических принадлежностей
- — Холодная вода
- — Горячая вода
- — Канализация

Примечание:


Расстояние между точками крепления полотенцесушителя зависит от выбранной модели

Дизайнер			
Заказчик			

Стадия	Лист	Листов
АИ		

РАСПОЛОЖЕНИЕ ВК КУХНЯ
И САНУЗЕЛ

Luxhouse_studio

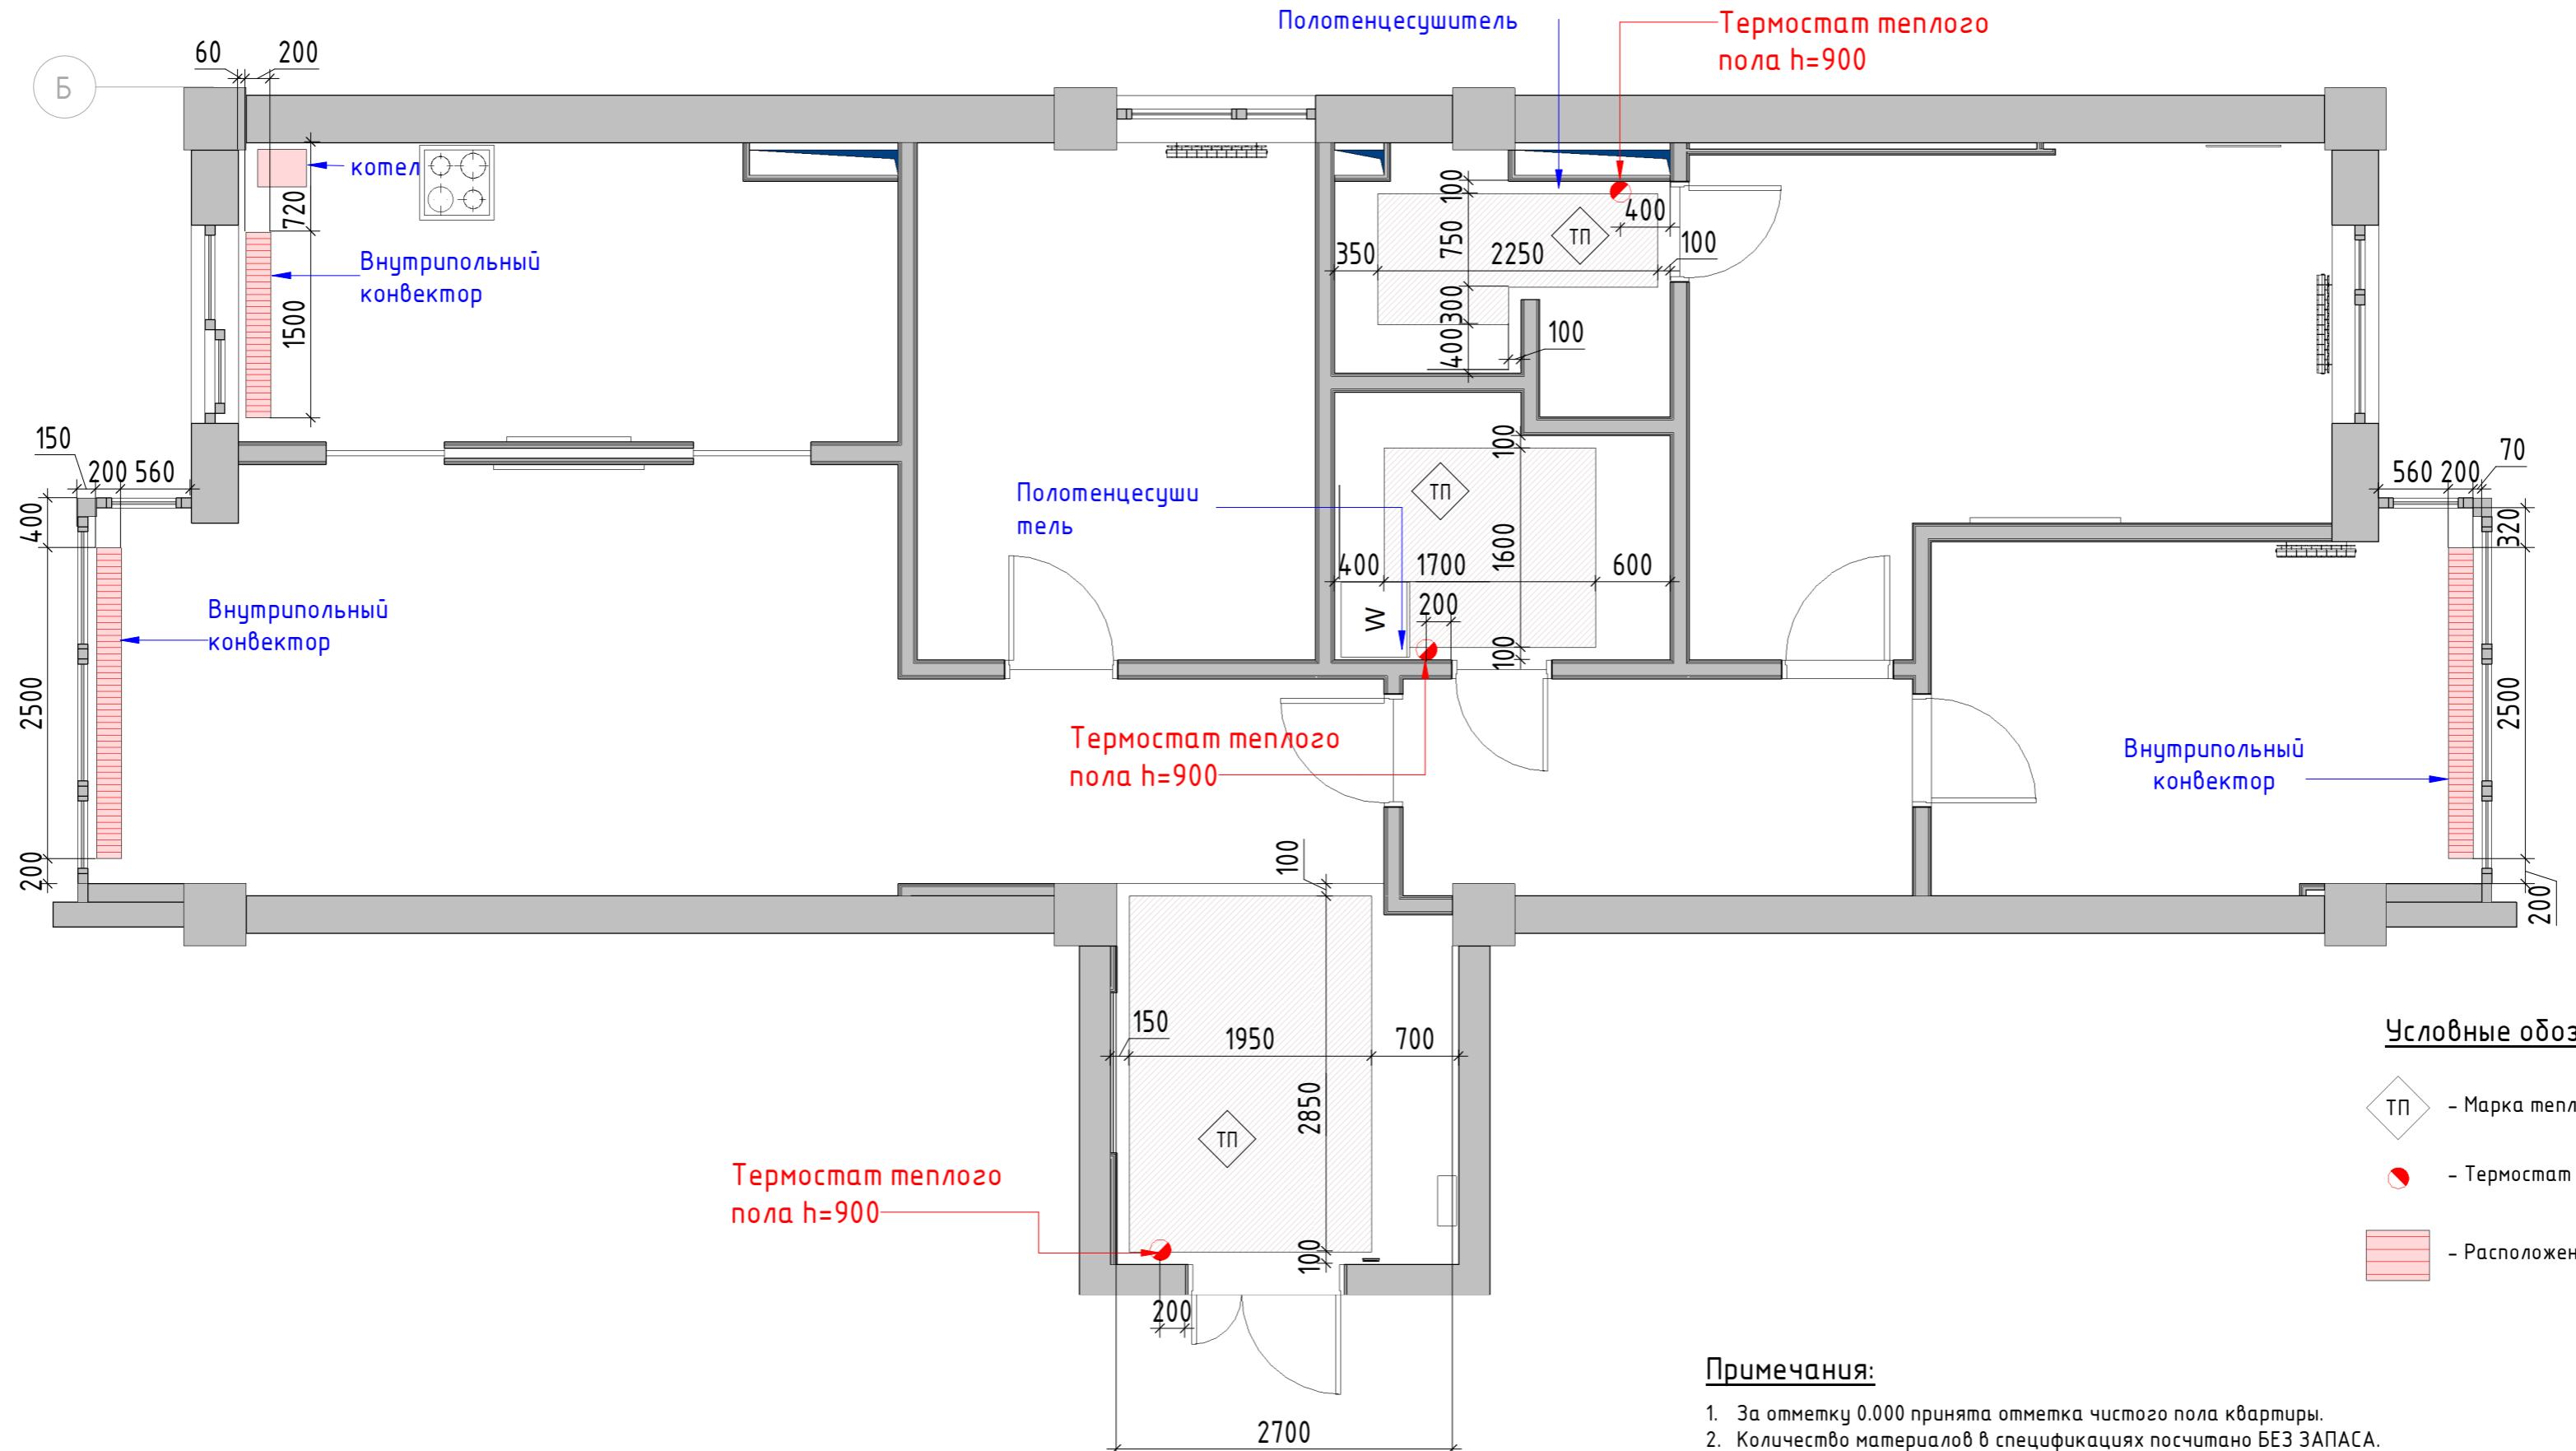


Условные обозначения:

- △ ТП - Марка теплого пола
- Термостат
- Расположение конвекторов

Примечания:

- За отметку 0.000 принята отметка чистого пола квартиры.
- Количество материалов в спецификациях посчитано БЕЗ ЗАПАСА.
- Все размеры уточняются по месту.
- Модель отопительных оборудований и разводки смотреть раздел ОВ



Стадия	Лист	Листов
Дизайнер		
Заказчик	ПЛАН ОТОПЛЕНИЯ	
	Luxhouse_studio	

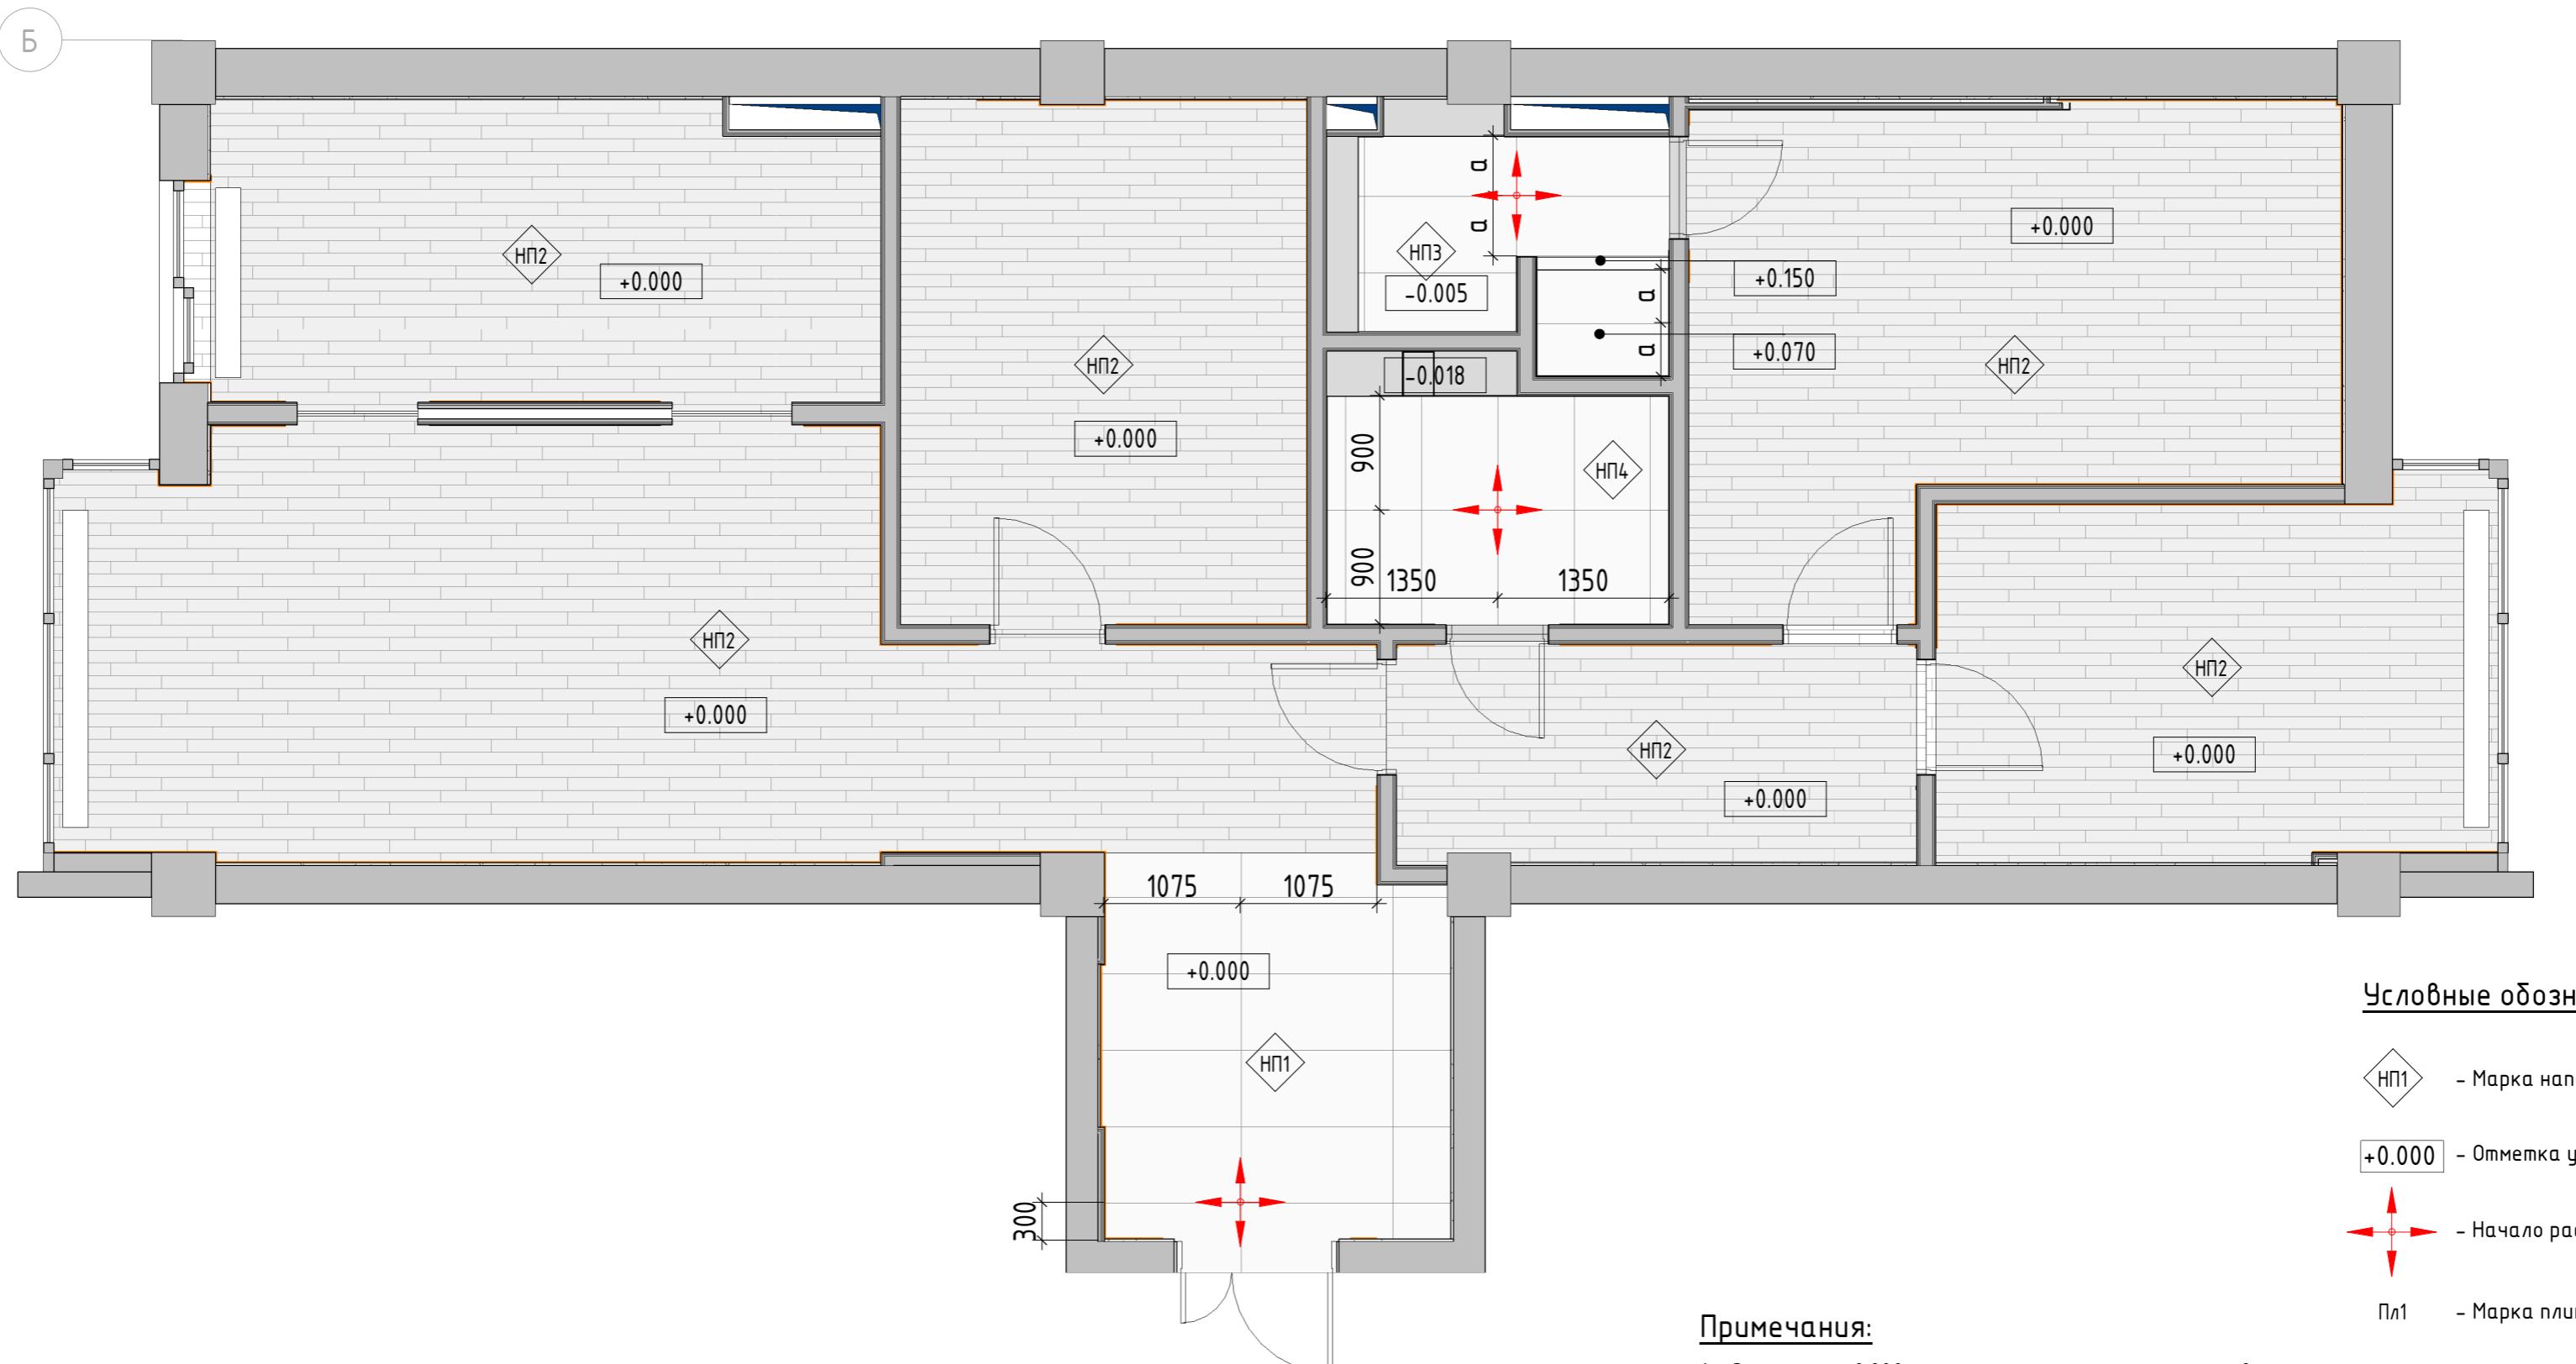

Примечания:

- За отметку 0.000 принята отметка чистого пола квартиры.
- Количество материалов в спецификациях посчитано БЕЗ ЗАПАСА.
- Все размеры уточняются по месту.
- Стыки разных типов покрытий должны производиться под полотном двери (по оси дверного полотна).

Стадия	Лист	Листов
Дизайнер		
Заказчик	ПЛАН НАПОЛЬНЫЙ ПОКРЫТИЙ	
	Luxhouse_studio	

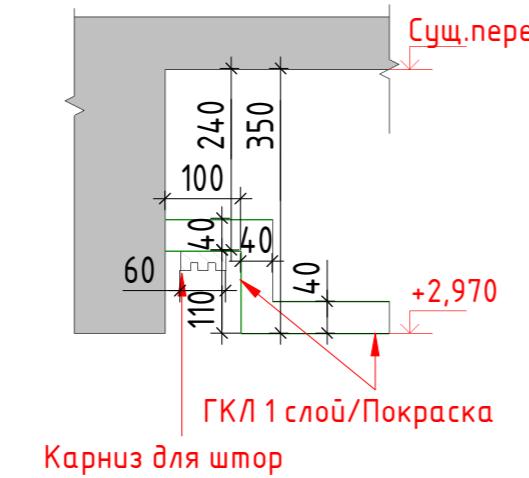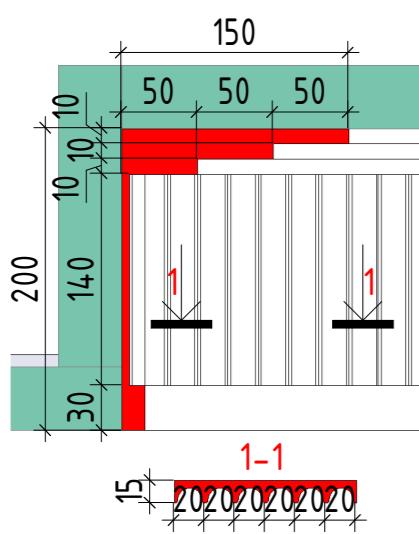

Карниз для штор

Условные обозначения:

- (ПТ1) – Марка потолка
- +2.600 – Отметка уровня потолка
- Предусмотреть усиление в местах монтажа стеклянных перегородок

Примечания:

1. За отметку 0.000 принята отметка чистого пола квартиры.
2. Количество материалов в спецификациях посчитано БЕЗ ЗАПАСА.
3. Все размеры уточняются по месту.

Дизайнер			
Заказчик			

ПЛАН ПОТОЛКА



Luxhouse_studio


Формат: А3

Стадия


Лист

Листов

АИ

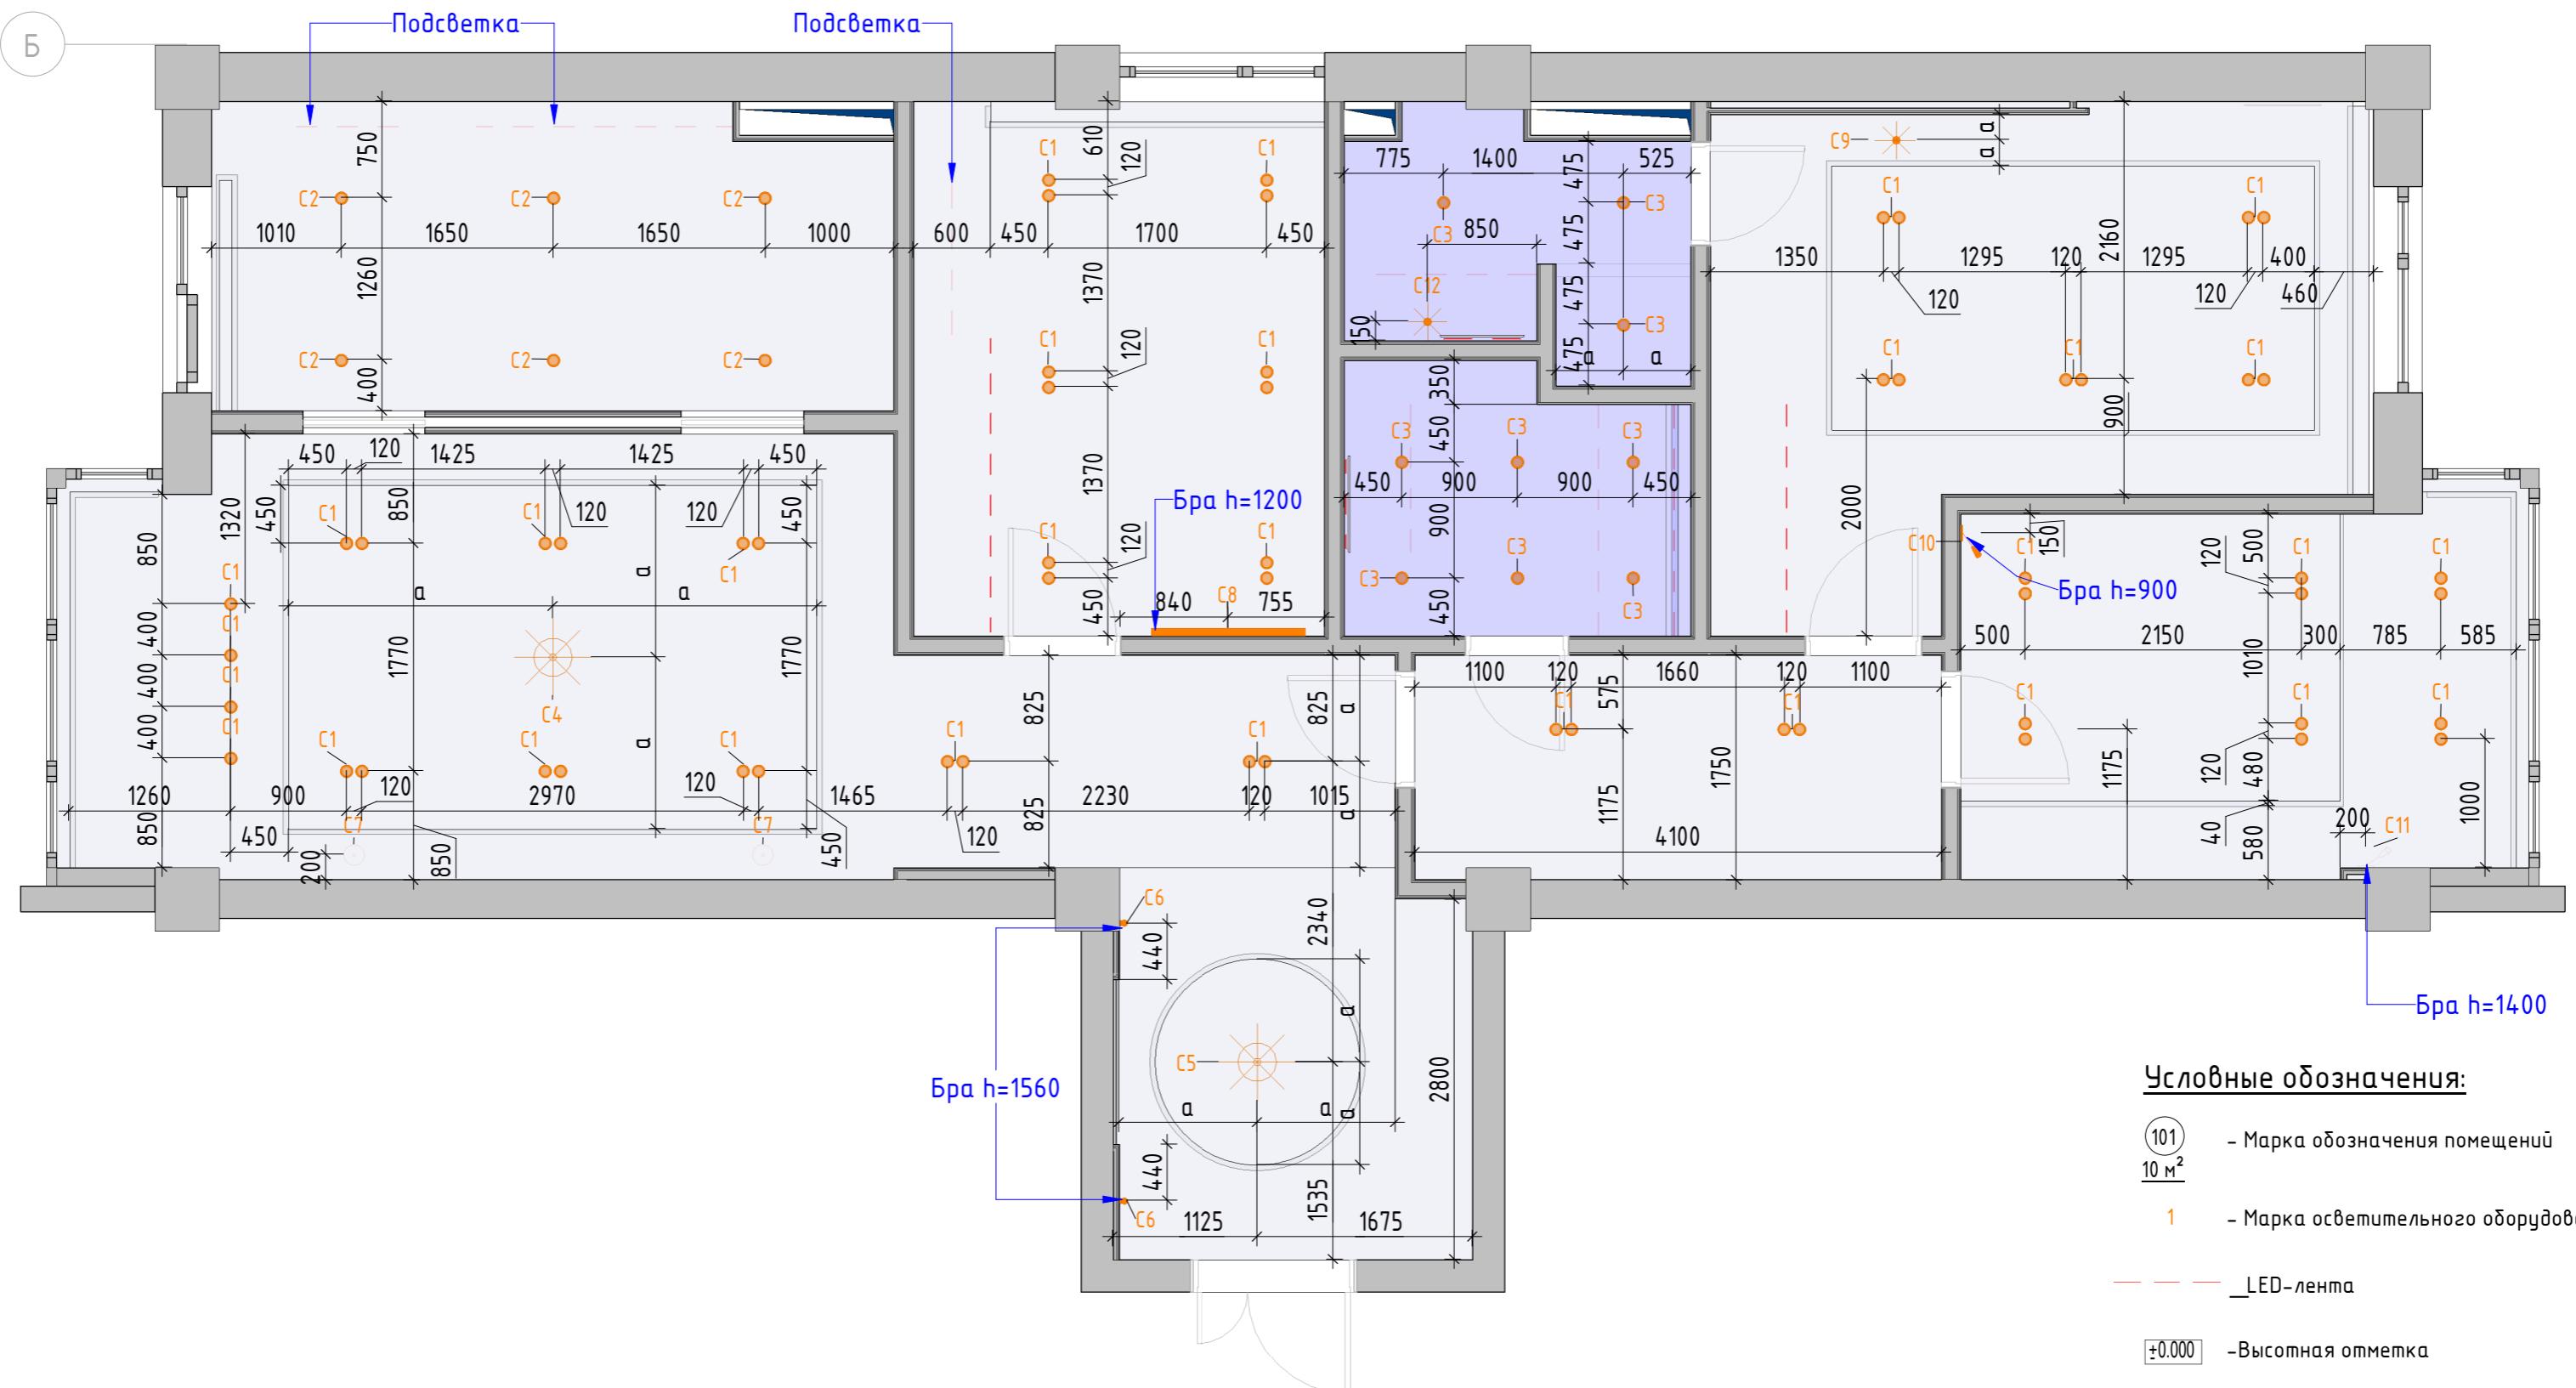


Стадия	Лист	Листов
АИ		
ПЛАН РАССТАНОВКИ ОСВЕТИТЕЛЬНОГО ОБОРУДОВАНИЯ		
Luxhouse_studio		

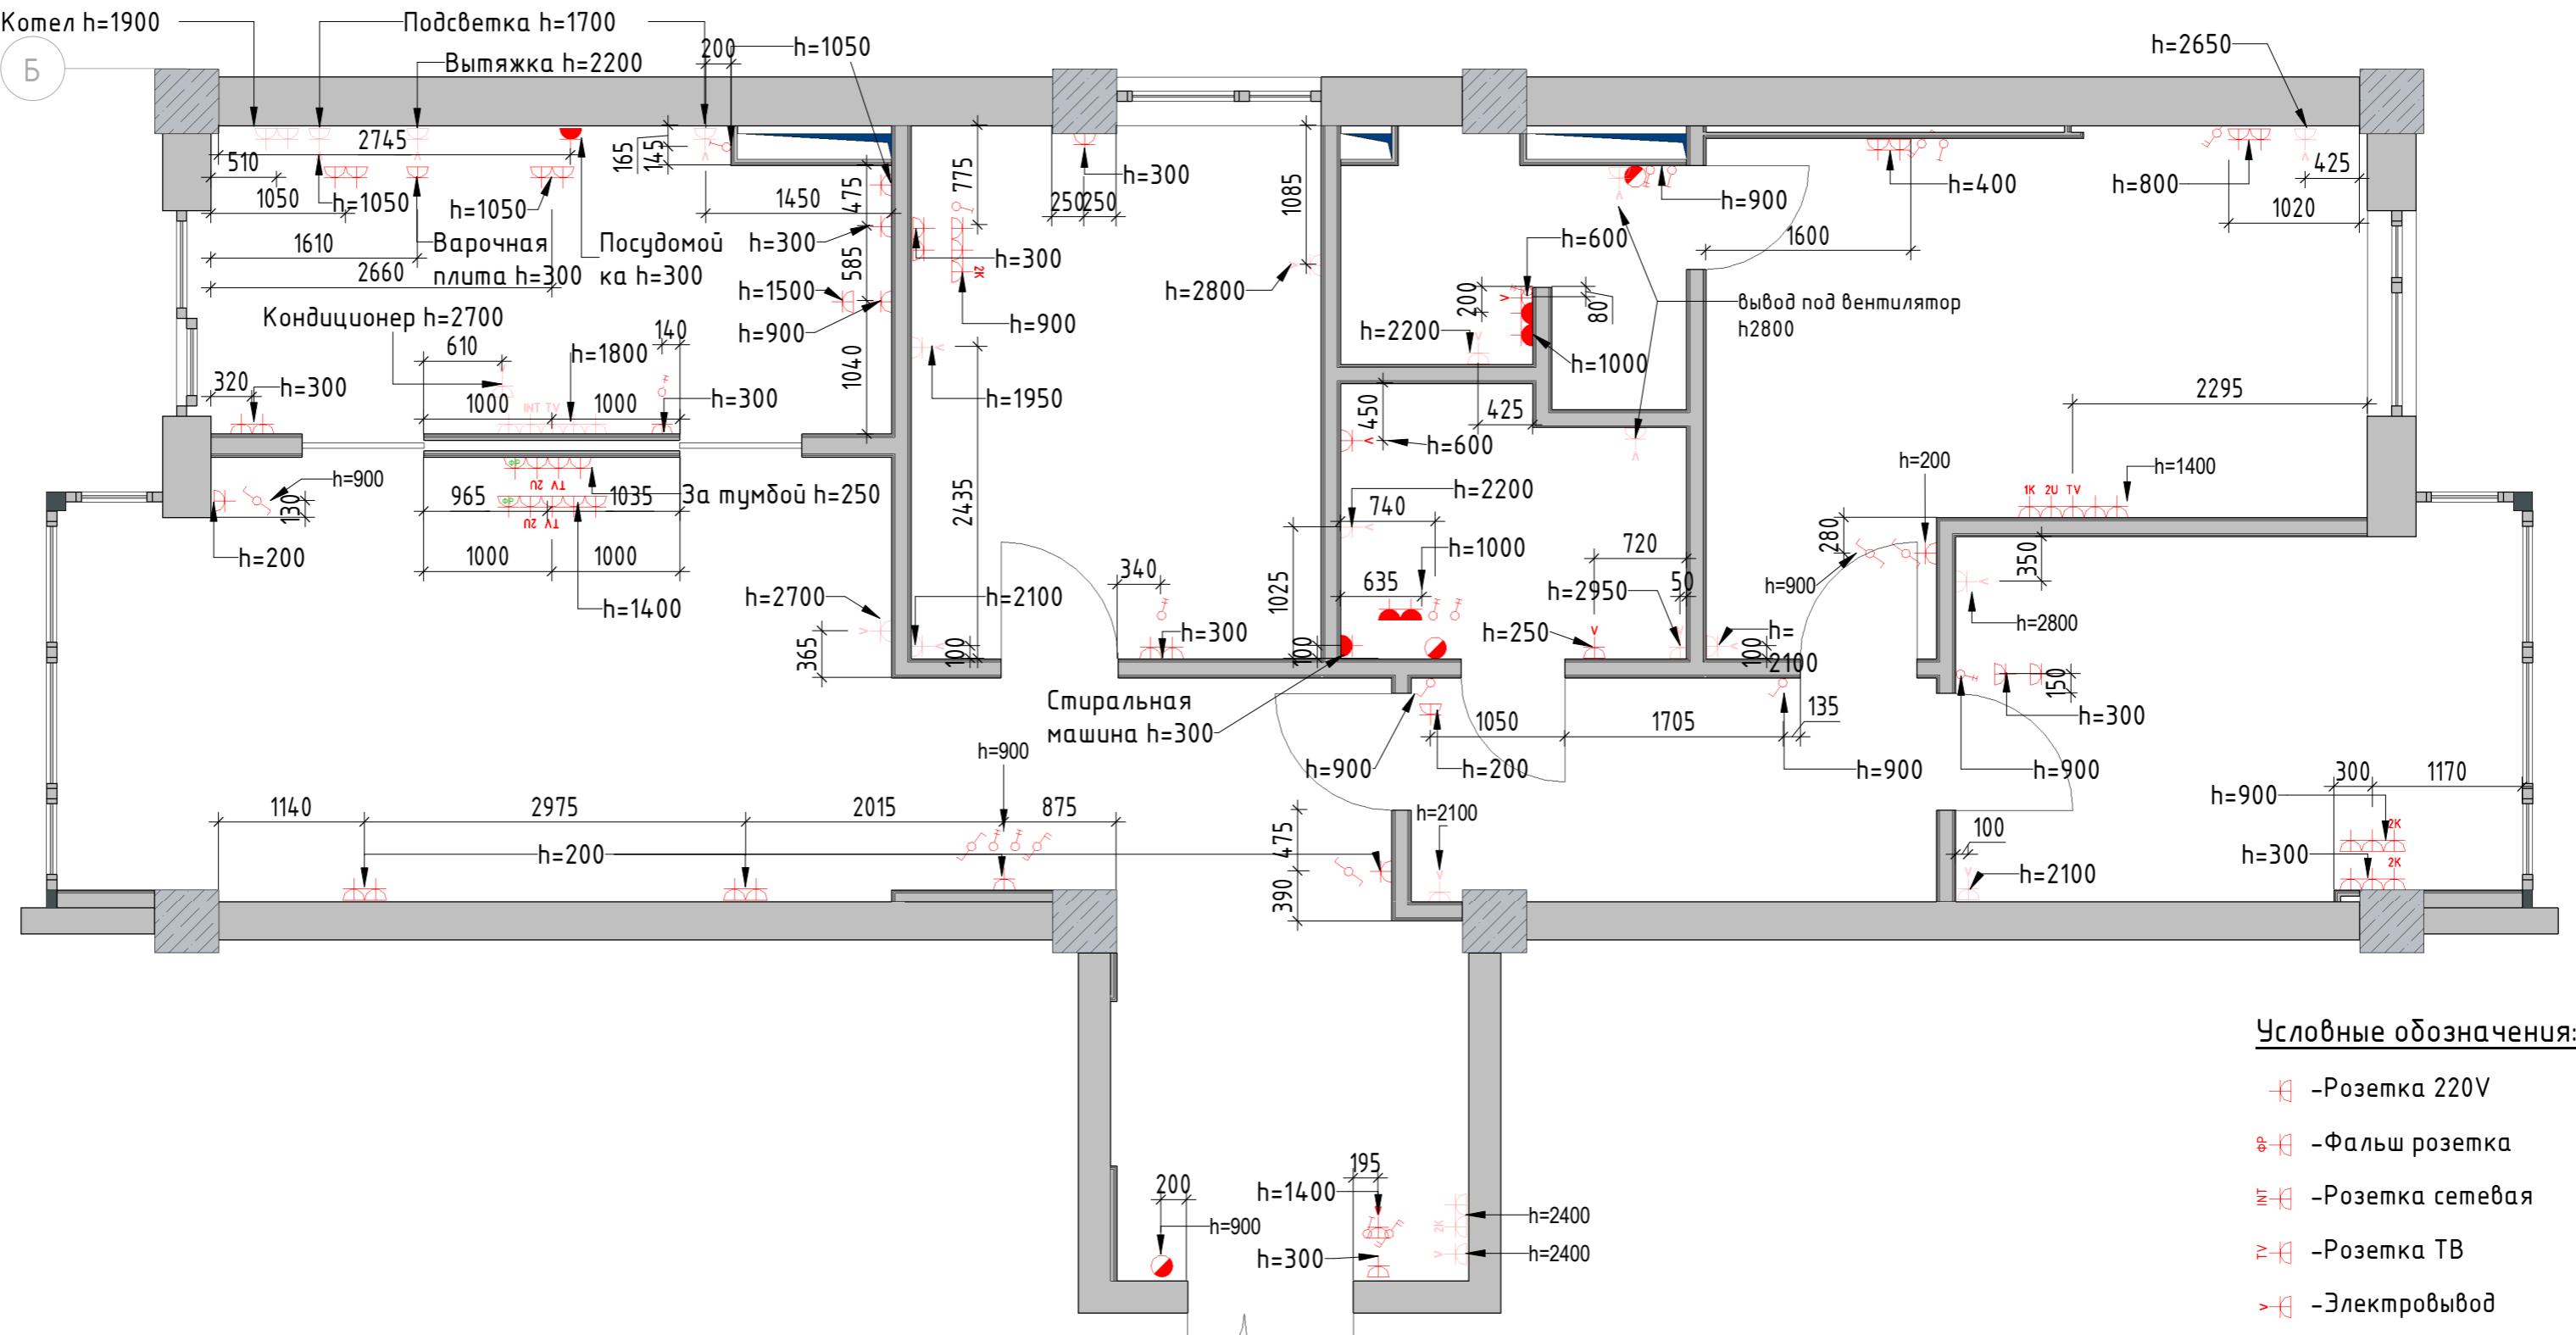

Примечания:

1. За отметку 0.000 принята отметка чистого пола квартиры.
2. Все размеры уточняются по месту.
3. Размеры даны до центра рамки.
4. Смотреть совместно с развертками.

Стадия	Лист	Листов
Дизайнер		
Заказчик	ПЛАН РАССТАНОВКИ РАЗЕТОК	
	Luxhouse_studio	

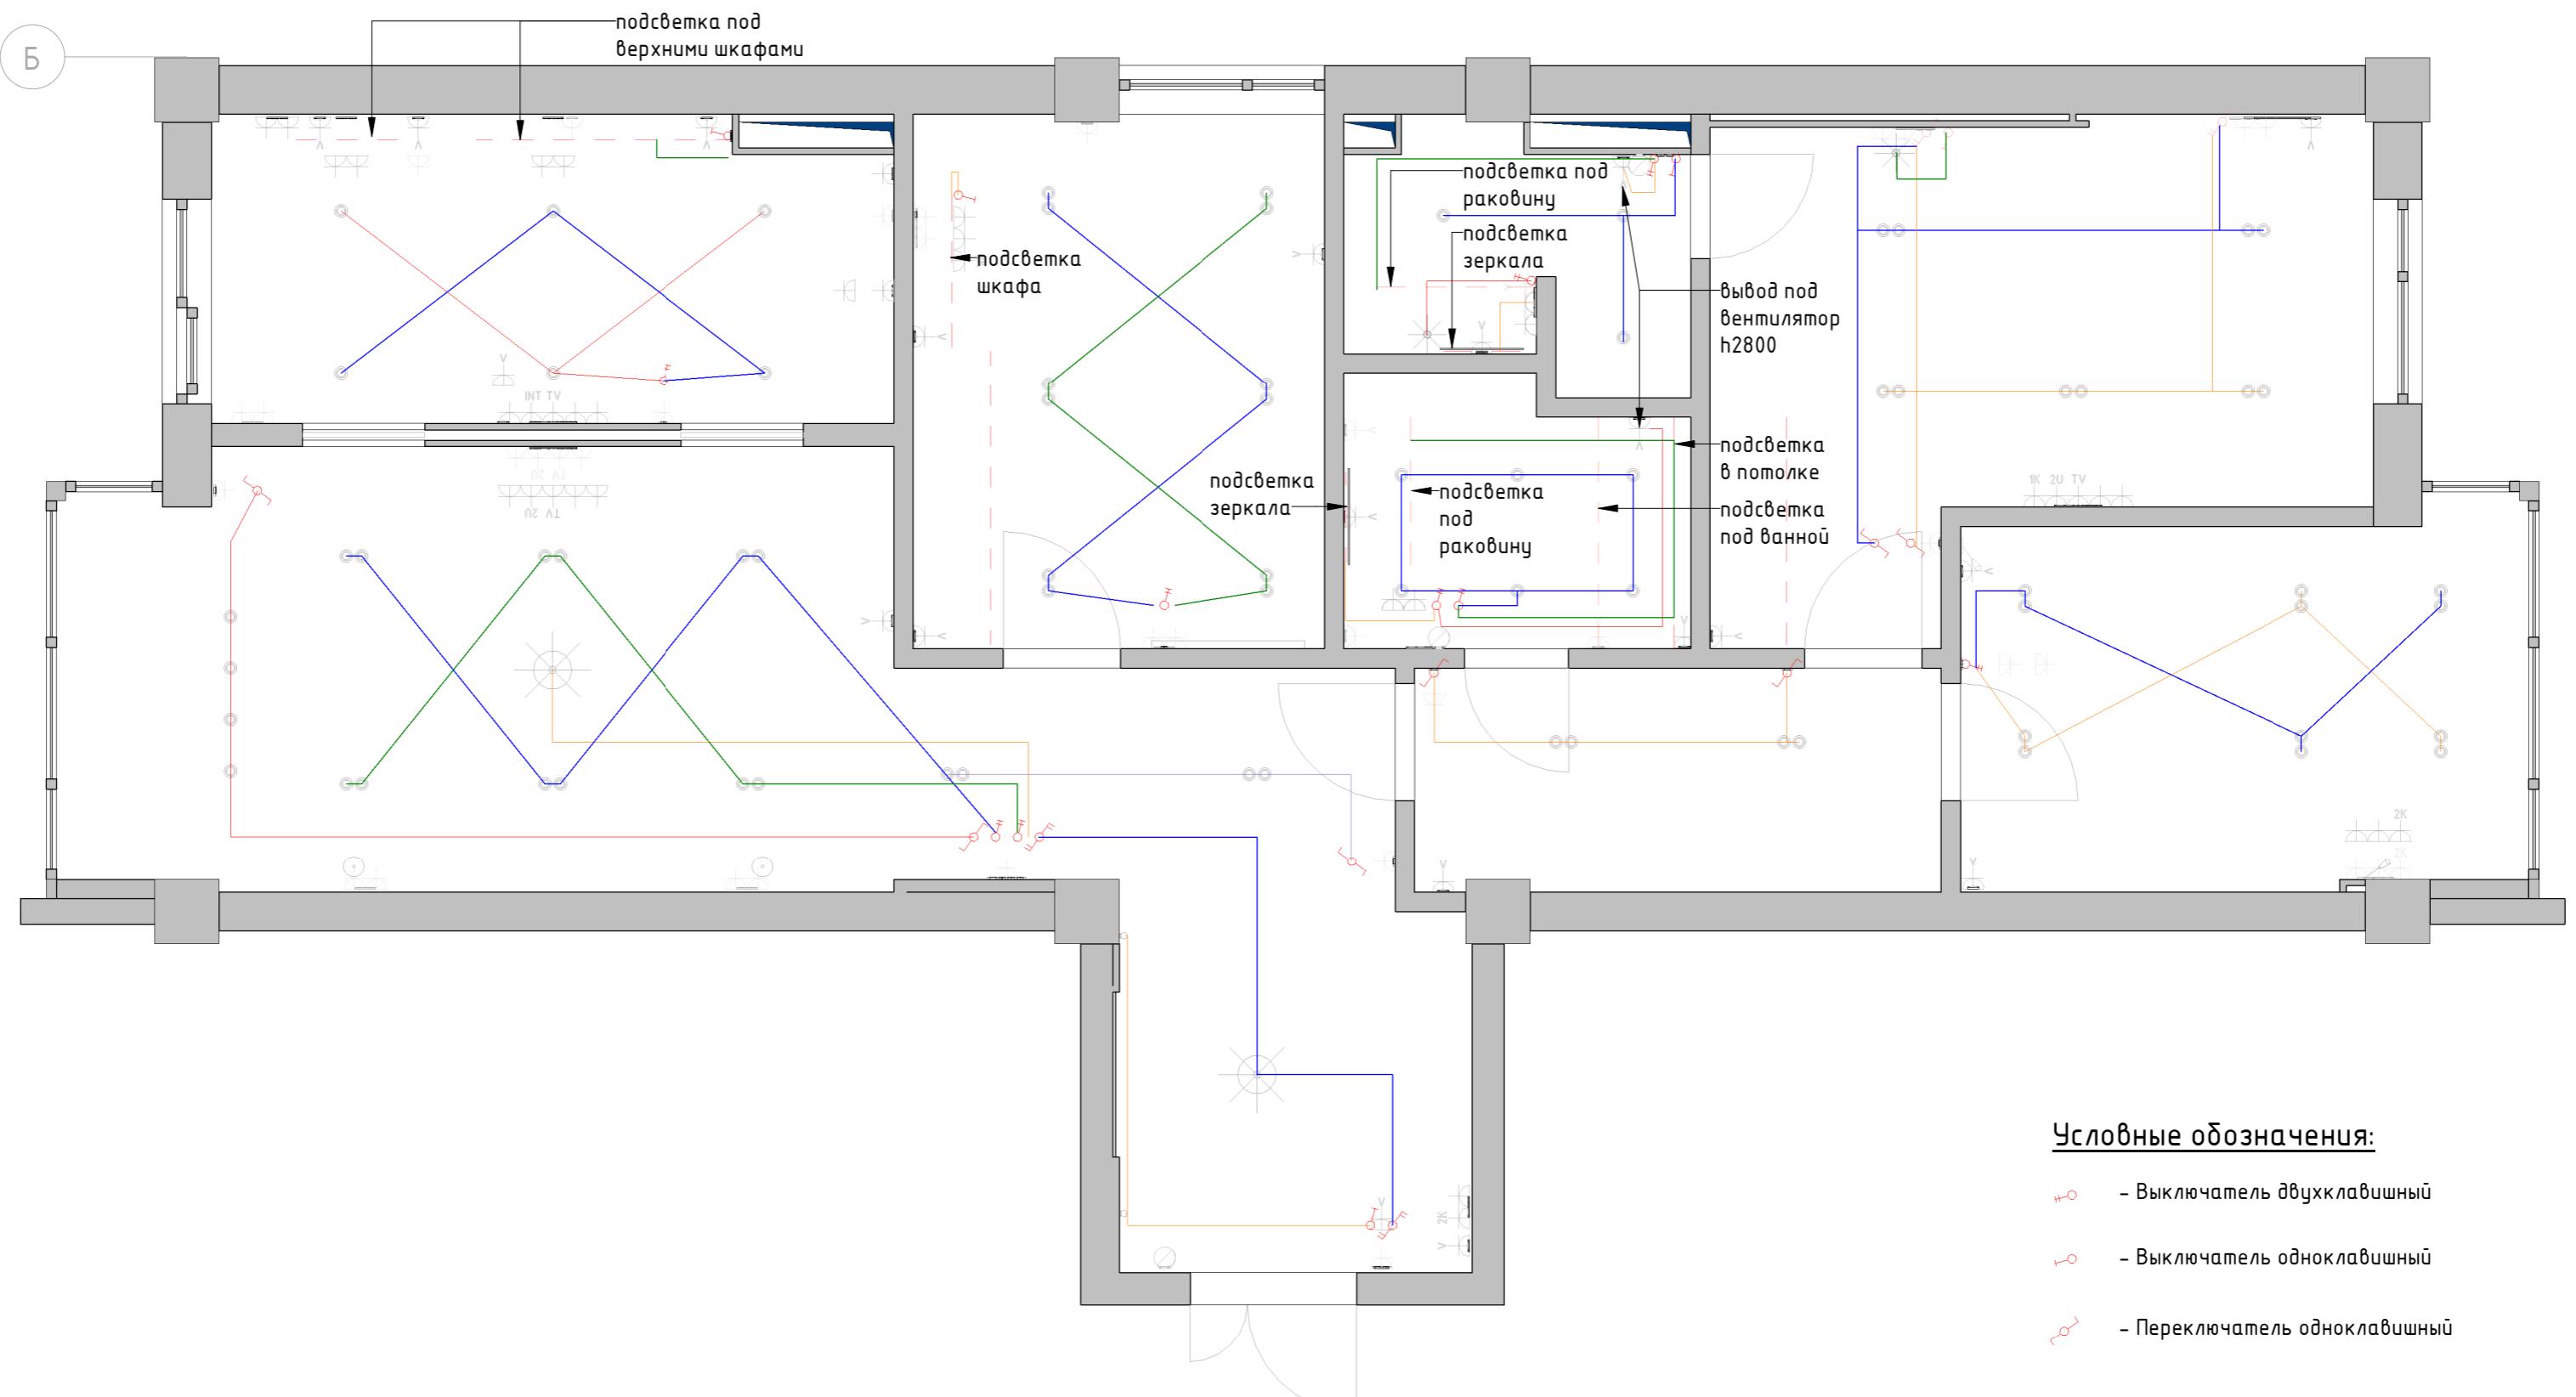

Условные обозначения:

- Выключатель двухклавишный
- Выключатель одноклавишный
- Переключатель одноклавишный

Примечания:

- За отметку 0.000 принята отметка чистого пола квартиры.
- Все размеры уточняются по месту.
- Размеры даны до центра рамки.
- Смотреть совместно с развертками.

Примечание:

Каждая бытовая техника и кондиционеры
должны иметь свой самостоятельный провод
идущий к электрощиту

Стадия	Лист	Листов
АИ		
ПЛАН ПРИВЯЗКИ ПРИБОРОВ ОСВЕЩЕНИЯ К ВЫКЛЮЧАТЕЛЯМ		
Luxhouse_studio		




Стадия	Лист	Листов
АИ		

Дизайнер



Заказчик

ПЛАН ОБОЗНАЧЕНИЯ
РАЗВЕРТОК СТЕН

Вид-1

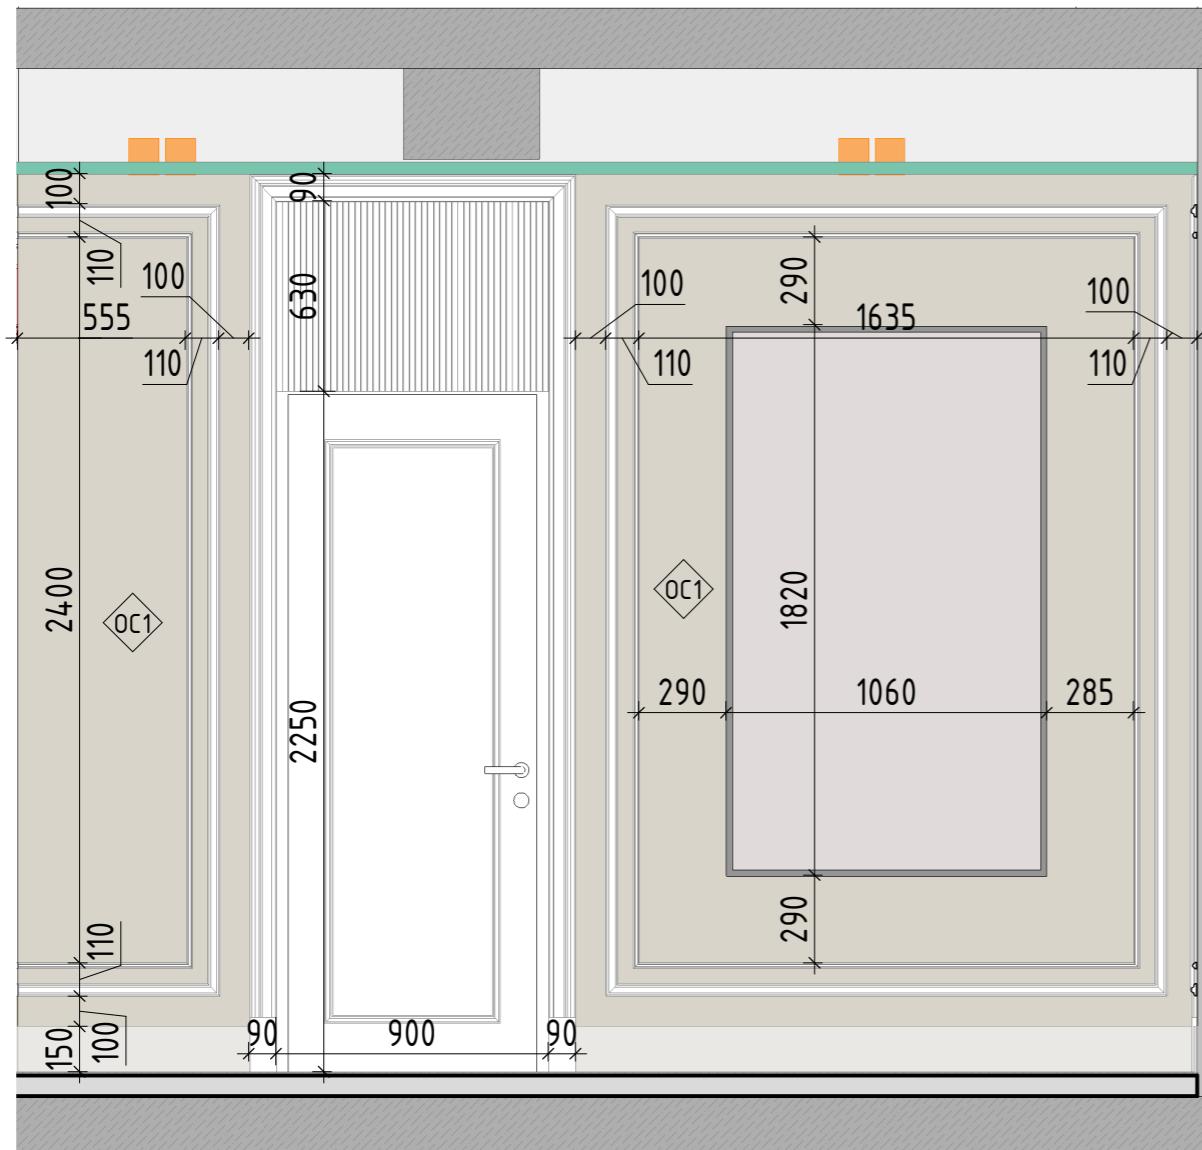

Вид-2

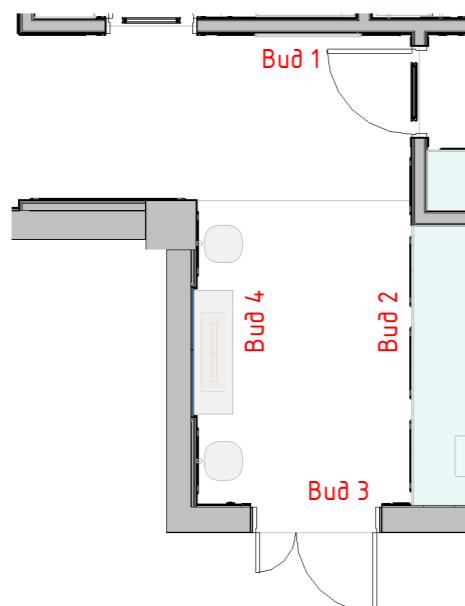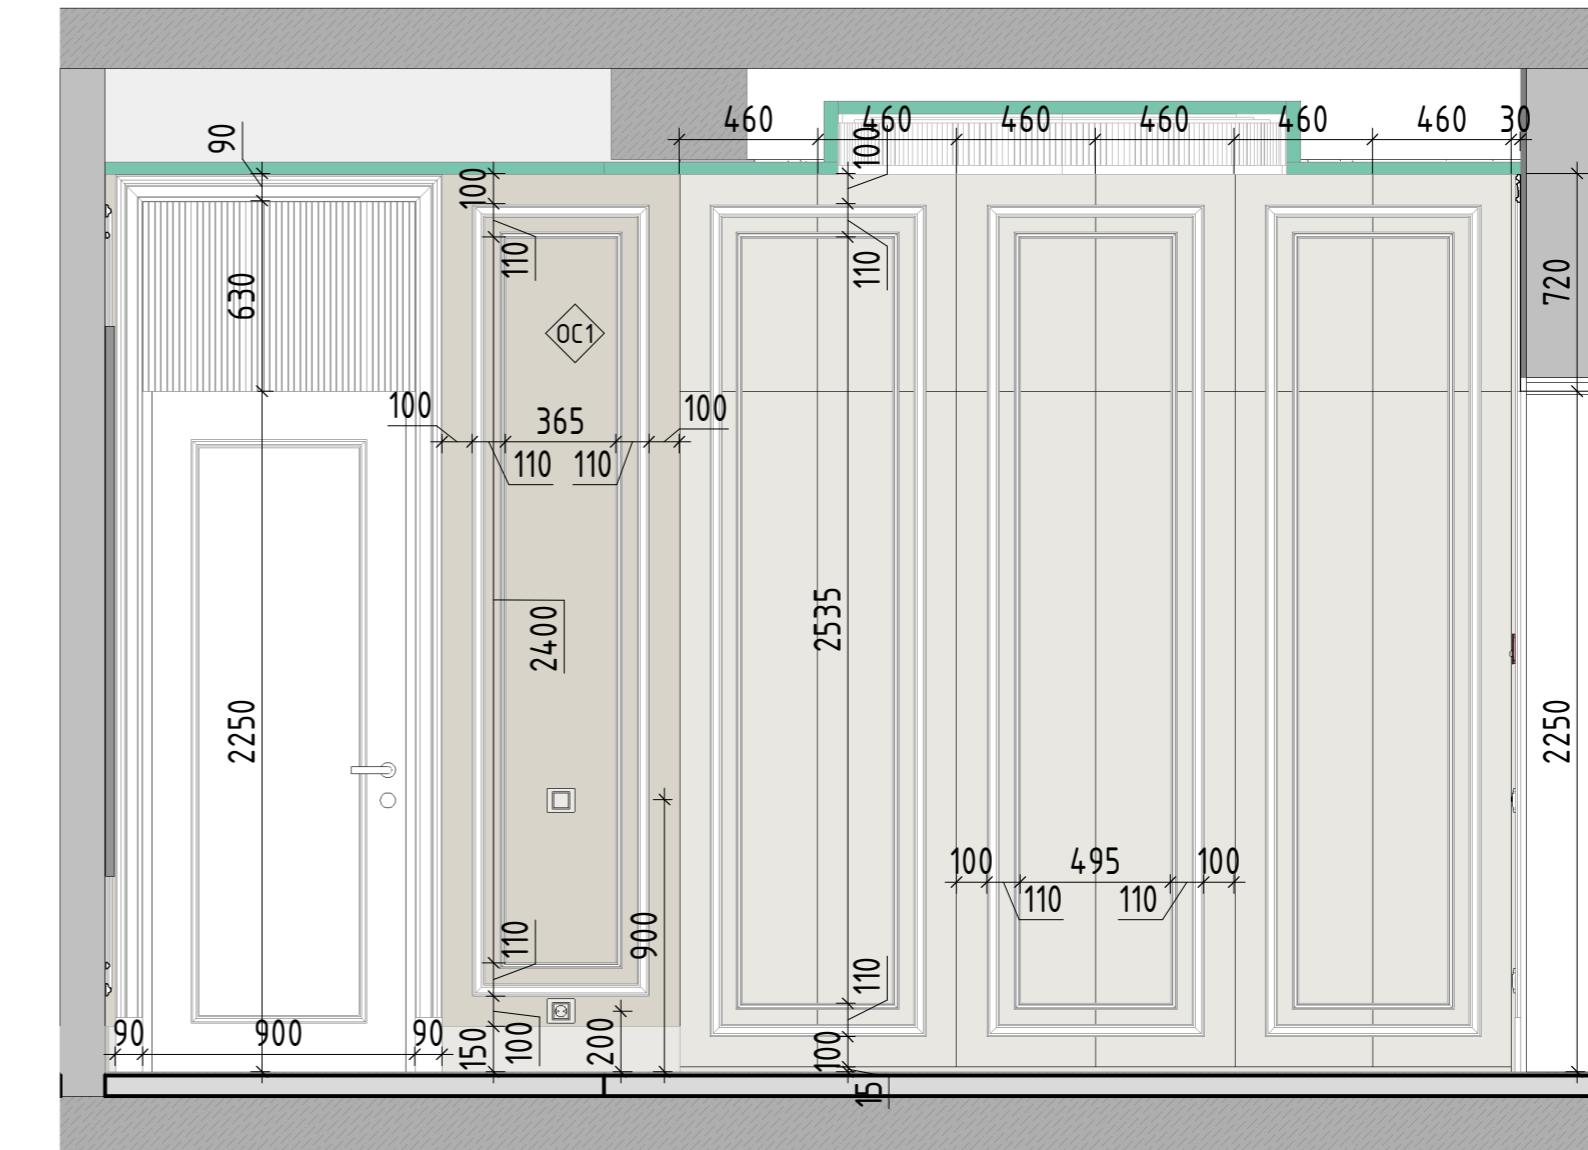

Примечание:

- (OC) -Штукатурка
- (OC1) -Tikkurila_Y487 Пиацца
- (OC2) -Tikkurila_X487 Laasti_Расмвор
- (OC3) -Tikkurila_X445 Lido_Лидо
- (OC4) -Плитка 3000x1000 NOIR DESIR BOCCIARDATO
- (OC5) -Плитка 3000x1000 BIANCO LASA BOCCIARDATO




- (OC6) -Белый керамогранит 1200x600, Vitra
- (OC7) -Плитка 3000x1000 VERDERAME LUX
- (OC8) -ARVEN RECTIFIED PARLAK NANO 60X120 OT KUTAHYA
- (OC9) -55012910RL 60x120 ATLANTIS БЕЛЫЙ ЛАПАТИРОВАННЫЙ
- (OC10) -Фартук на кухне
- Двери/Гардеробные шкафы/Плинтусы Цвет - Tikkurila_G497 Ноуѓу_Пар

Примечания:

1. За отметку 0.000 принята отметка чистого пола квартиры.
2. Все размеры уточняются по месту.
3. Наличник дверей со стороны санузлов на 100 мм ниже чем в остальных помещениях

Дизайнер			
Заказчик			

ПРИХОЖАЯ. РАЗВЕРТКА СТЕН

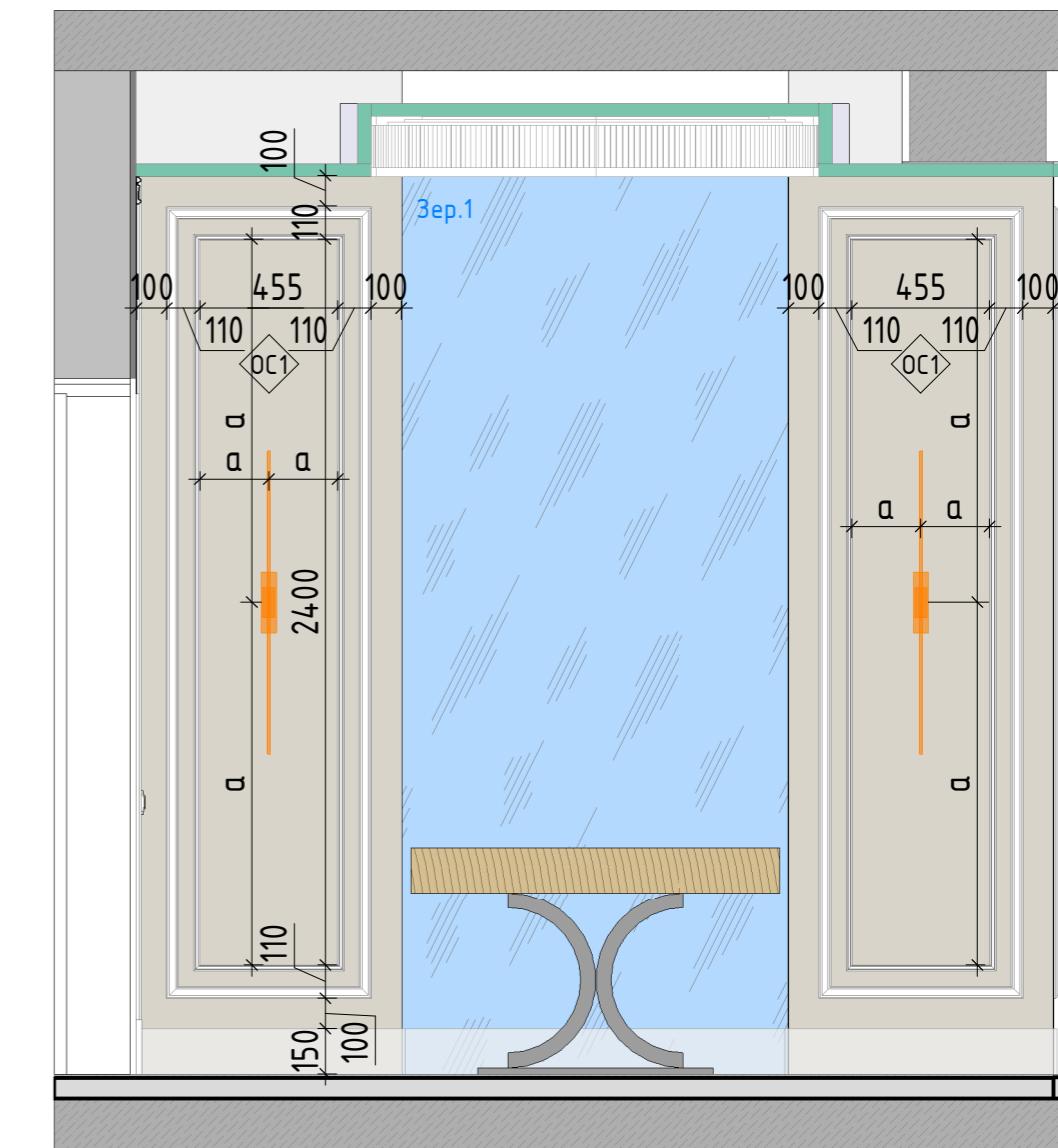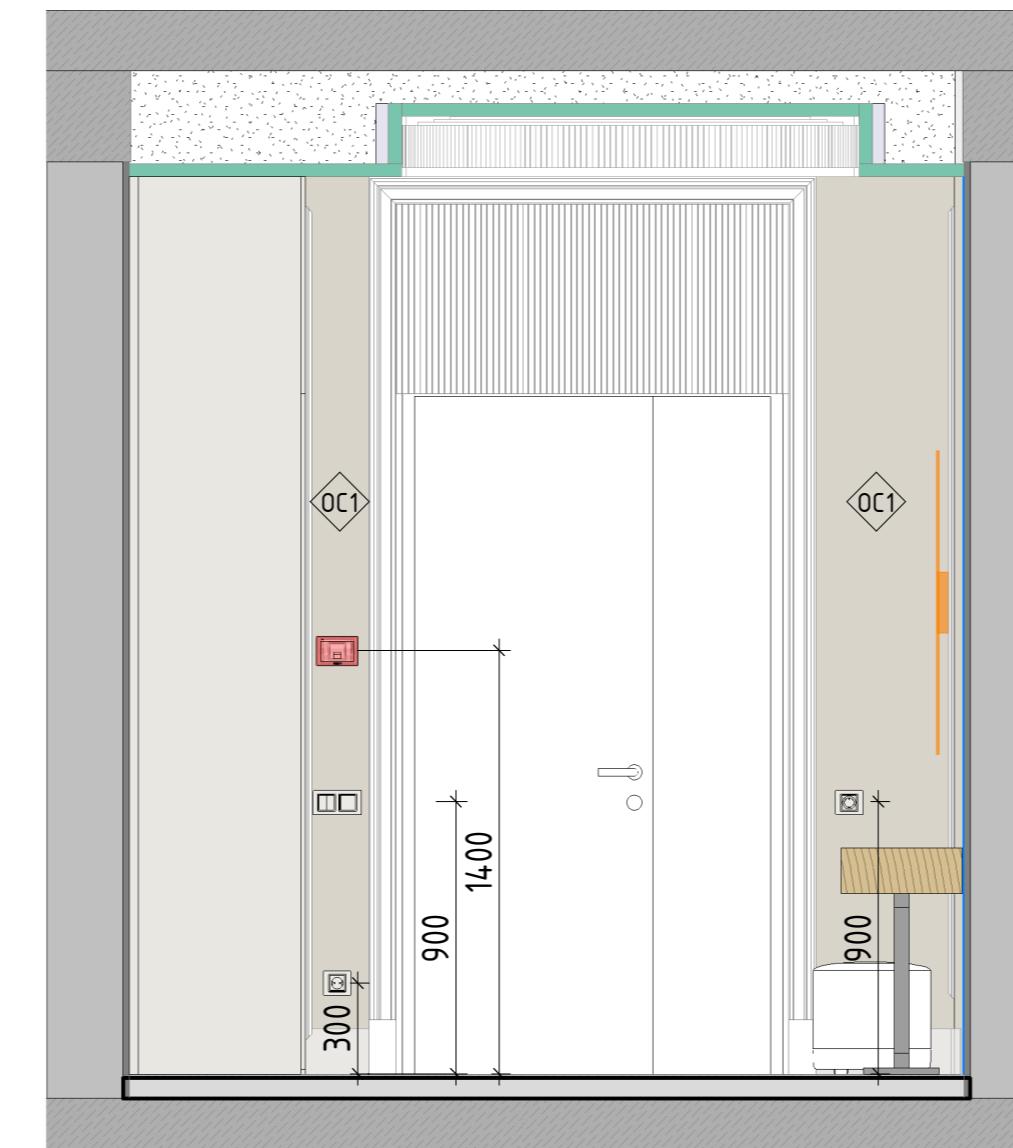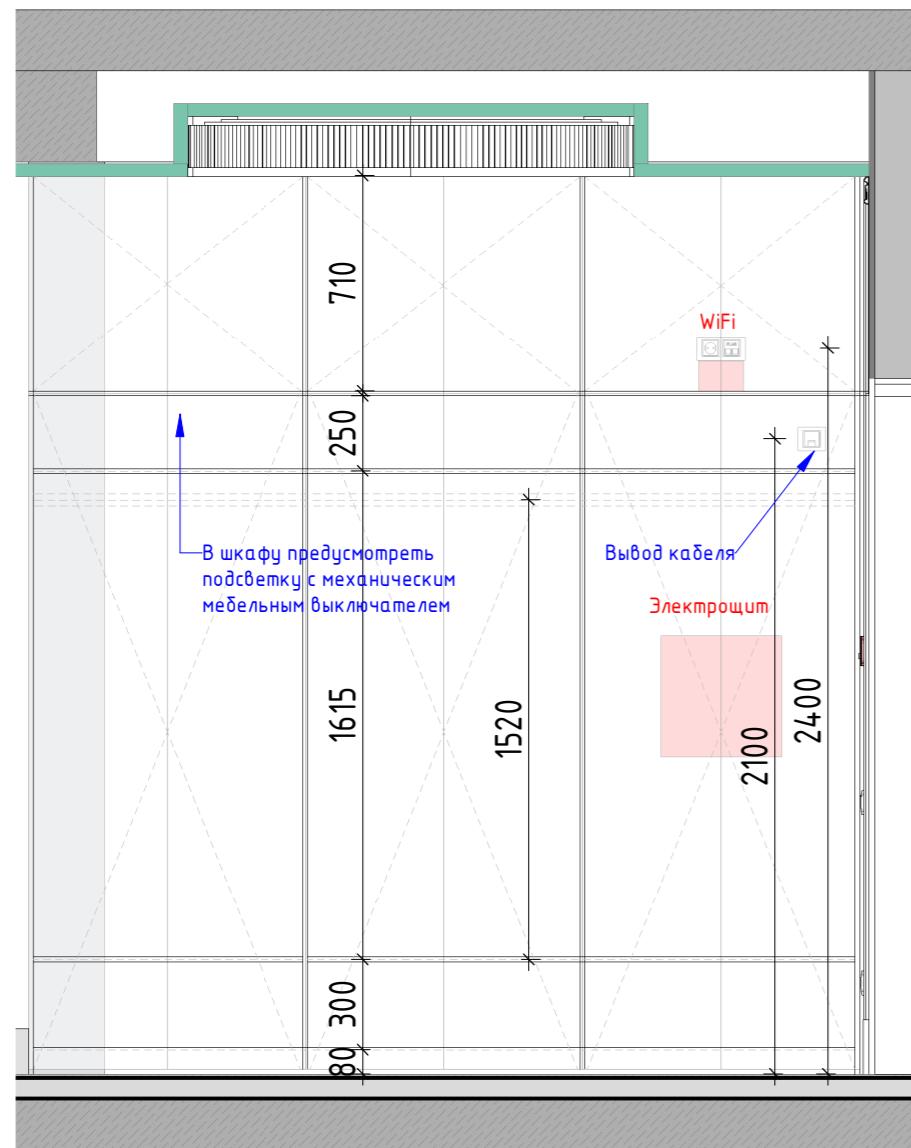



Примечание:

- (ОС) -Штукатурка
- (ОС1) -Tikkurila_Y487 Пиацца
- (ОС2) -Tikkurila_X487 Laasti_Расмвор
- (ОС3) -Tikkurila_X445 Lido_Лудо
- (ОС4) -Плитка 3000x1000 NOIR DESIR BOCCIARDATO
- (ОС5) -Плитка 3000x1000 BIANCO LASA BOCCIARDATO
- (ОС6) -Белый керамогранит 1200x600, Vitra
- (ОС7) -Плитка 3000x1000 VERDERAME LUX
- (ОС8) -ARVEN RECTIFIED PARLAK NANO 60X120 OT KUTAHYA
- (ОС9) -55012910RL 60x120 ATLANTIS БЕЛЫЙ ЛАПАТИРОВАННЫЙ
- (ОС10) -Фартук на кухне
- Двери/Гардеробные шкафы/Плинтусы Цвем - Tikkurila_G497 Ноугу_Пар

Примечания:

1. За отметку 0.000 принята отметка чистого пола квартиры.
2. Все размеры уточняются по месту.
3. Наличник дверей со стороны санузлов на 100 мм ниже чем в остальных помещениях

Дизайнер	Стадия	Лист	Листов
АИ			
ПРИХОЖАЯ. РАЗВЕРТКА СТЕН			Luxhouse_studio
			Формат: А3

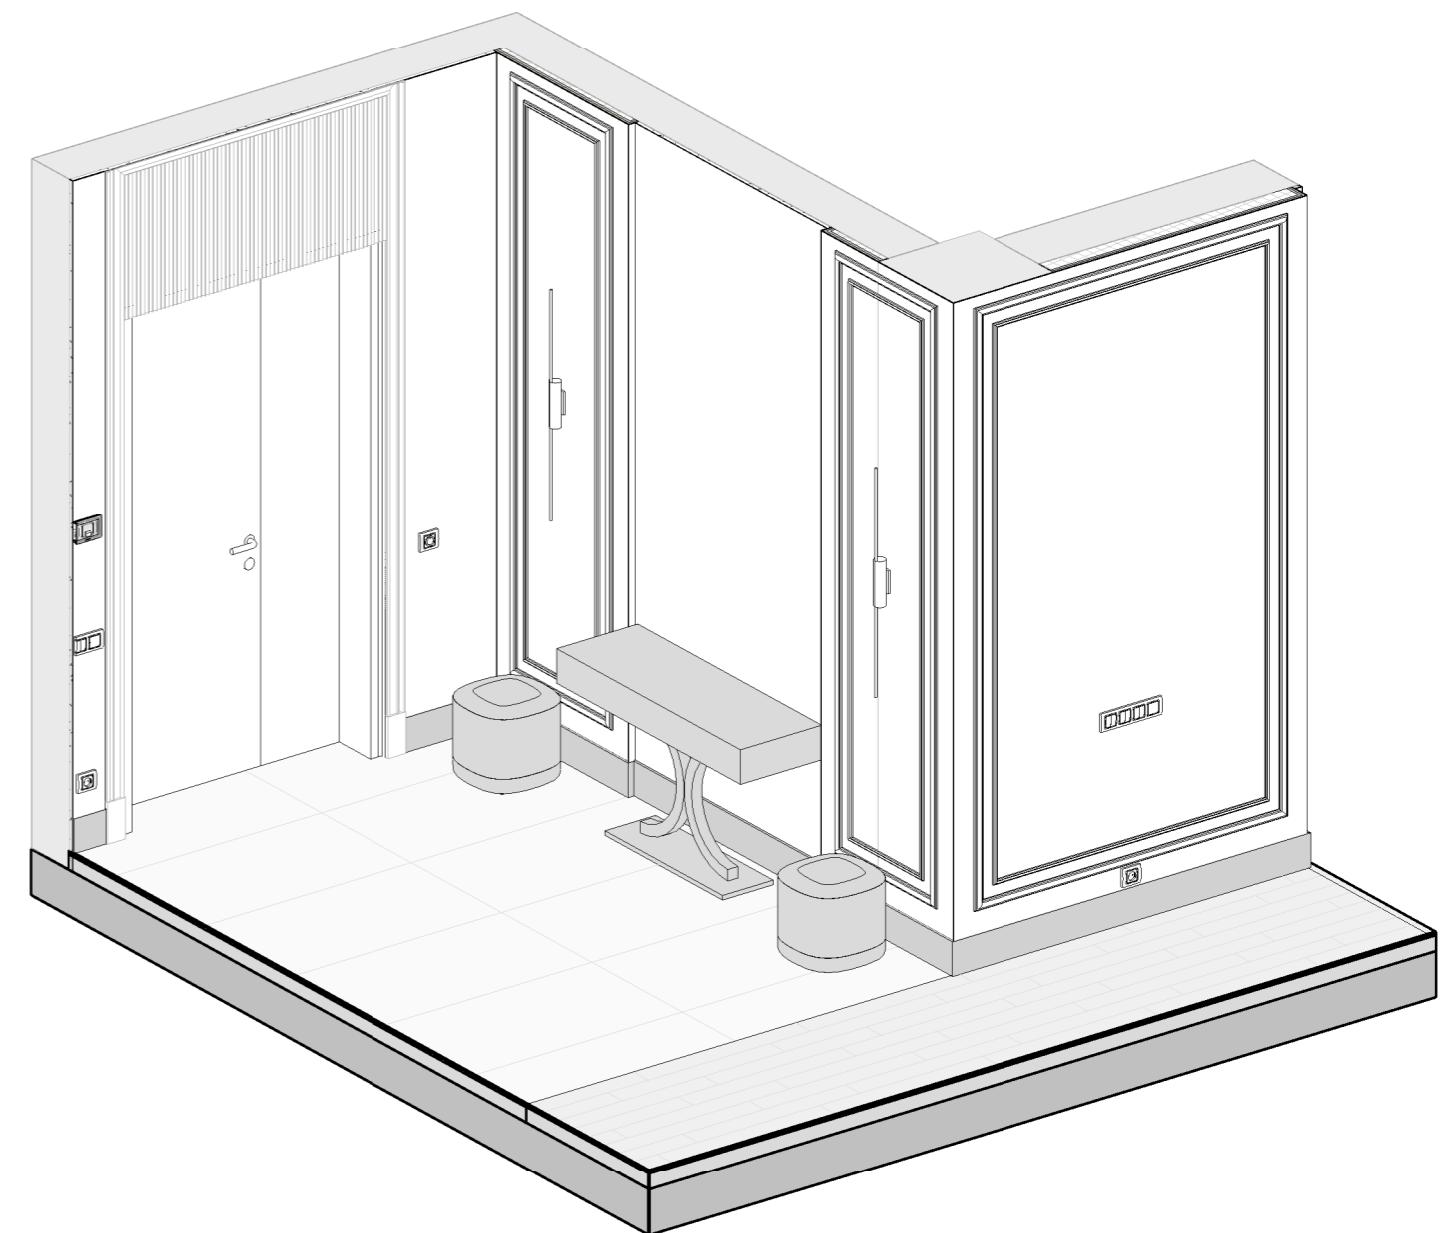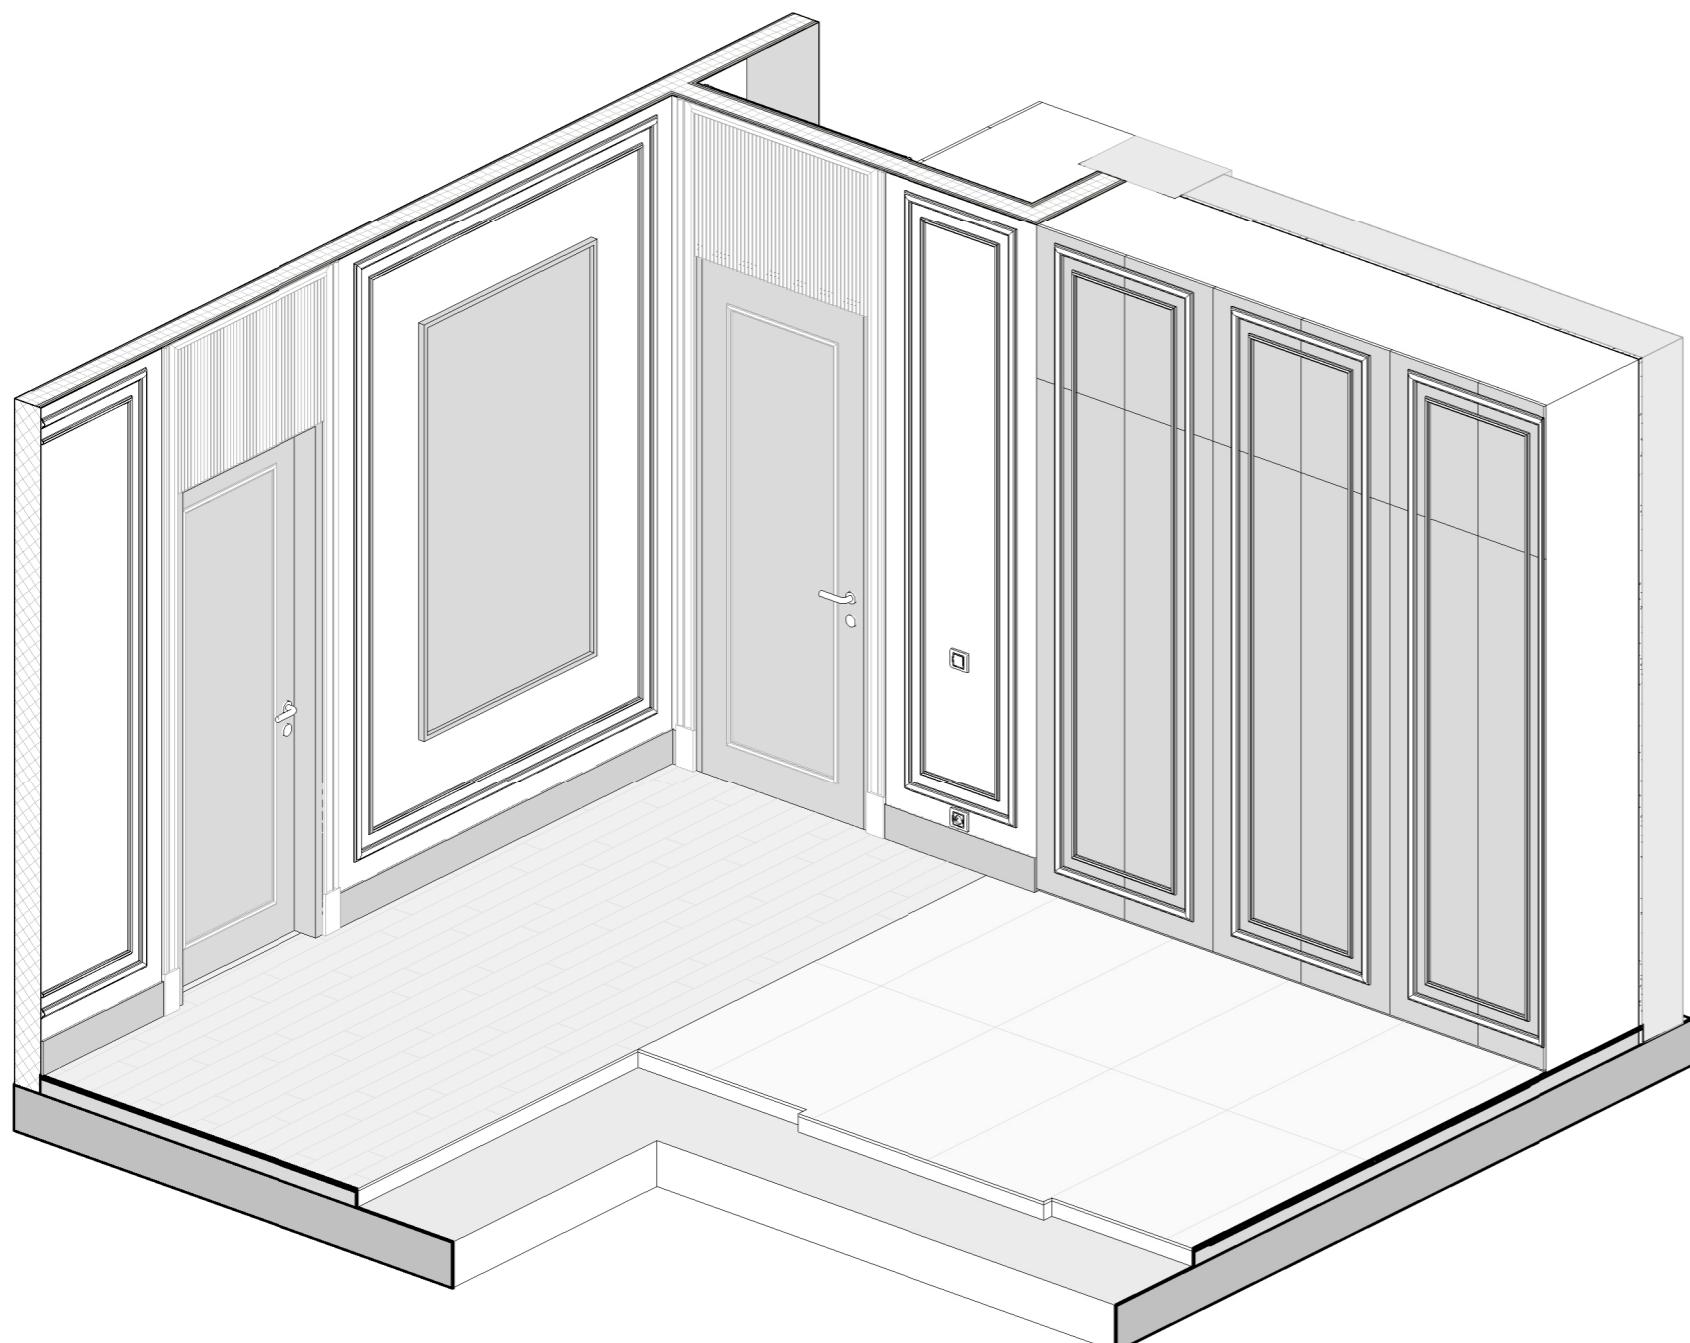


Дизайнер			
Заказчик			


Стадия	Лист	Листов
АИ		
ПРИХОЖАЯ ЗД ВИД		Luxhouse_studio

Формат: А3


Вид-1

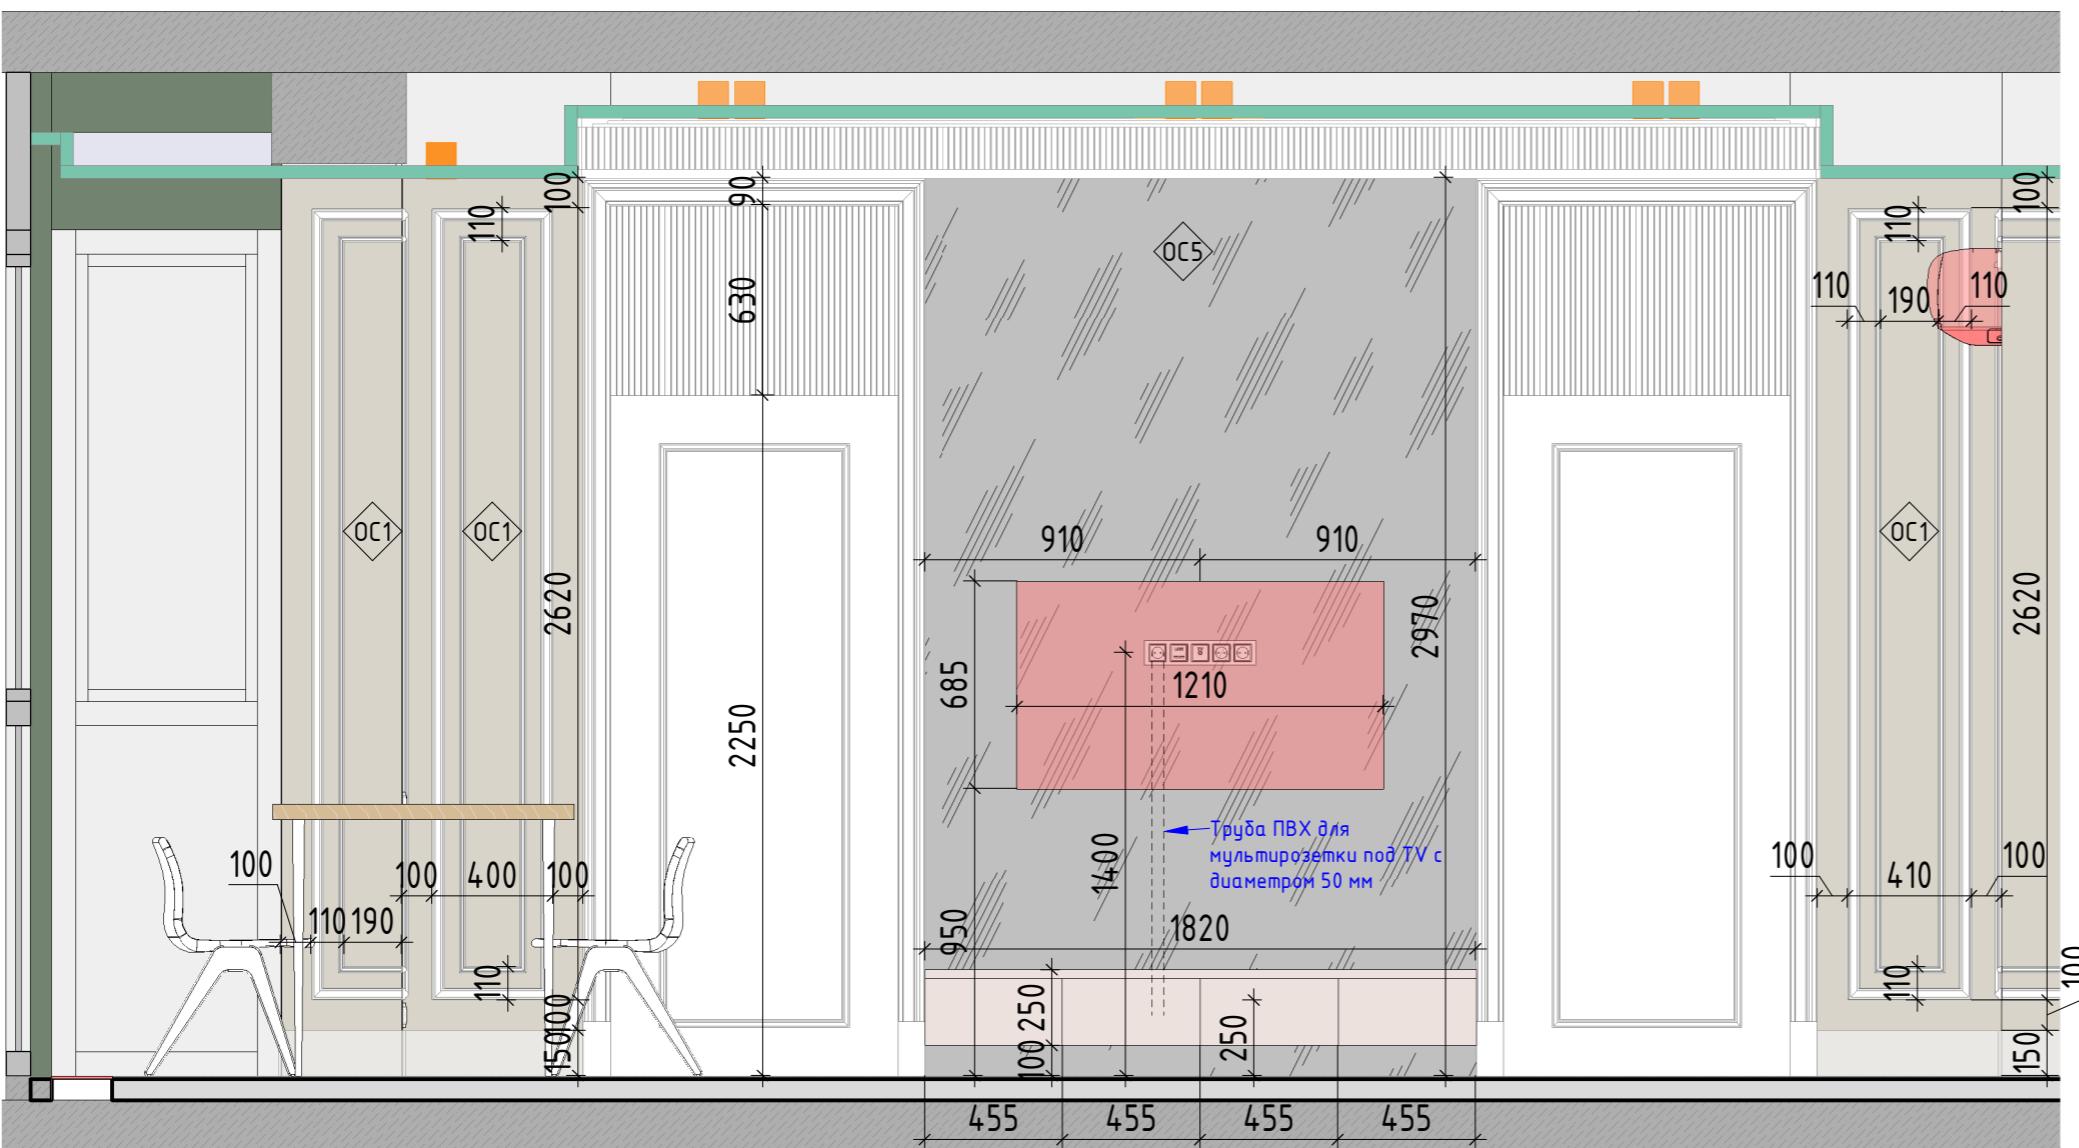

Вид-2

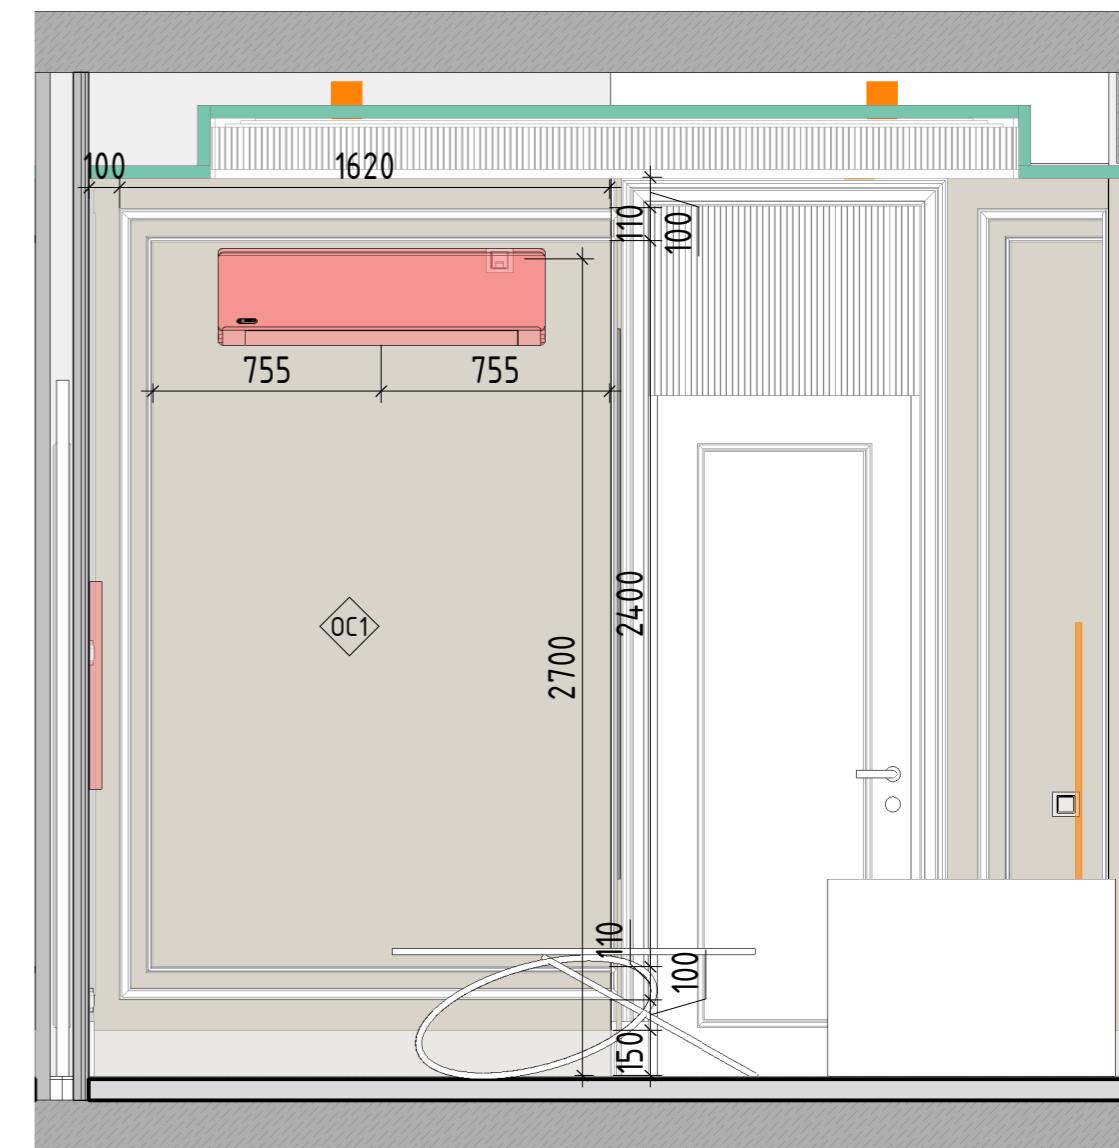

Примечание:

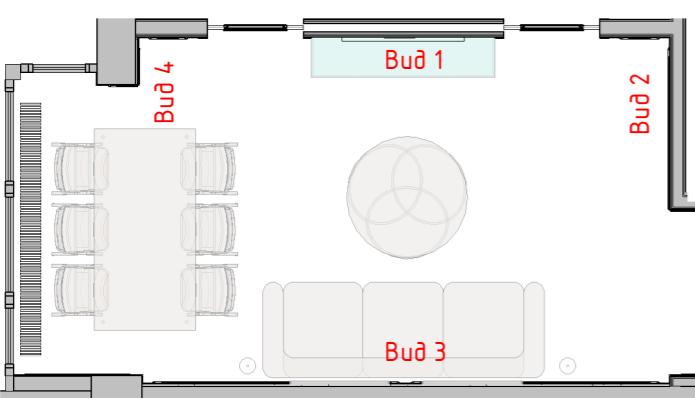

- (OC) -Штукатурка
- (OC1) -Tikkurila_Y487 Пицца
- (OC2) -Tikkurila_X487 Laasti_Раствор
- (OC3) -Tikkurila_X445 Lido_Лидо
- (OC4) -Плитка 3000x1000 NOIR DESIR BOCCARDATO
- (OC5) -Плитка 3000x1000 BIANCO LASA BOCCARDATO
- (OC6) -Белый керамогранит 1200x600, Vitra
- (OC7) -Плитка 3000x1000 VERDERAME LUX
- (OC8) -ARVEN RECTIFIED PARLAK NANO 60X120 OT KUTAHYA
- (OC9) -55012910RL 60x120 ATLANTIS БЕЛЫЙ ЛАПАТИРОВАННЫЙ
- (OC10) -Фартук на кухне
- Двери/Гардеробные шкафы/Плинтусы Цвет - Tikkurila_G497 Ноугу_Пар


Примечания:

1. За отметку 0.00 принята отметка чистого пола квартиры.
2. Все размеры уточняются по месту.
3. Наличник дверей со стороны санузлов на 100 мм ниже чем в остальных помещениях

Стадия	Лист	Листов
АИ		

ГОСТИНАЯ. РАЗВЕРТКА СТЕН

Вид-3

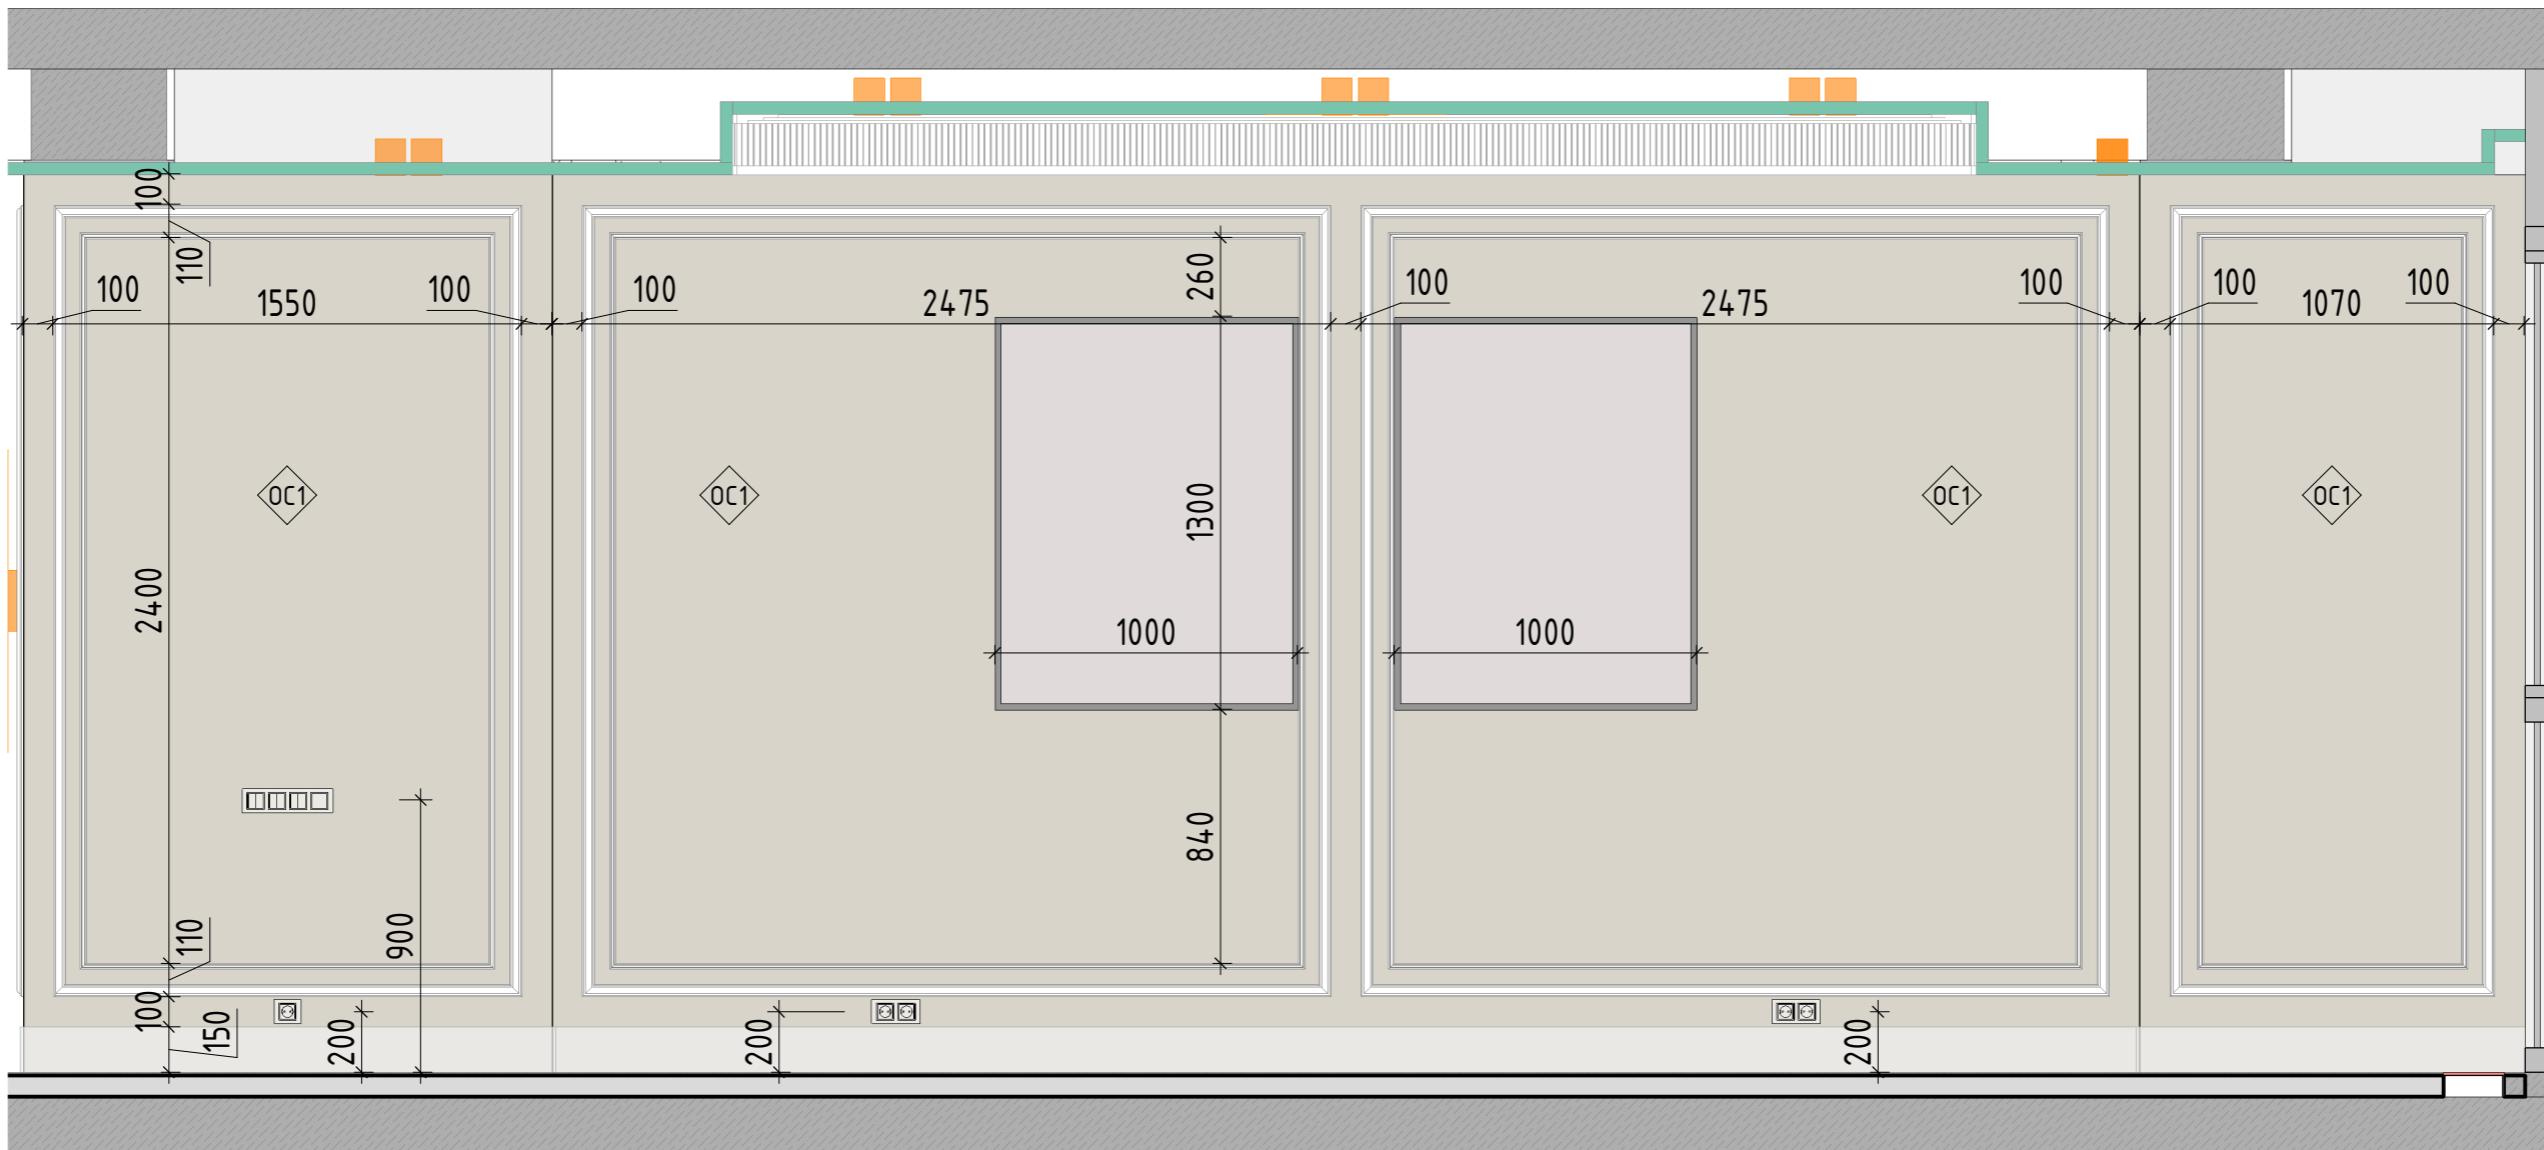

Примечание:



- (OC) -Штукатурка
- (OC1) -Tikkurila_Y487 Пицца
- (OC2) -Tikkurila_X487 Laasti_Расмбор
- (OC3) -Tikkurila_X445 Lido_Лидо
- (OC4) -Плитка 3000x1000 NOIR DESIR BOCCIARDATO
- (OC5) -Плитка 3000x1000 BIANCO LASA BOCCIARDATO
- (OC6) -Белый керамогранит 1200x600, Vitra
- (OC7) -Плитка 3000x1000 VERDERAME LUX
- (OC8) -ARVEN RECTIFIED PARLAK NANO 60X120 OT KUTAHYA
- (OC9) -55012910RL 60x120 ATLANTIS БЕЛЫЙ ЛАПАТИРОВАННЫЙ
- (OC10) -Фартук на кухне
- Двери/Гардеробные шкафы/Плинтусы Цвет - Tikkurila_G497 Ноугу_Пар

Примечания:

1. За отметку 0.000 принята отметка чистого пола квартиры.
2. Все размеры уточняются по месту.
3. Наличник дверей со стороны санузлов на 100 мм ниже чем в остальных помещениях

Стадия	Лист	Листов
AИ		
ГОСТИНАЯ. РАЗВЕРТКА СТЕН		
Luxhouse_studio		

Вид-4

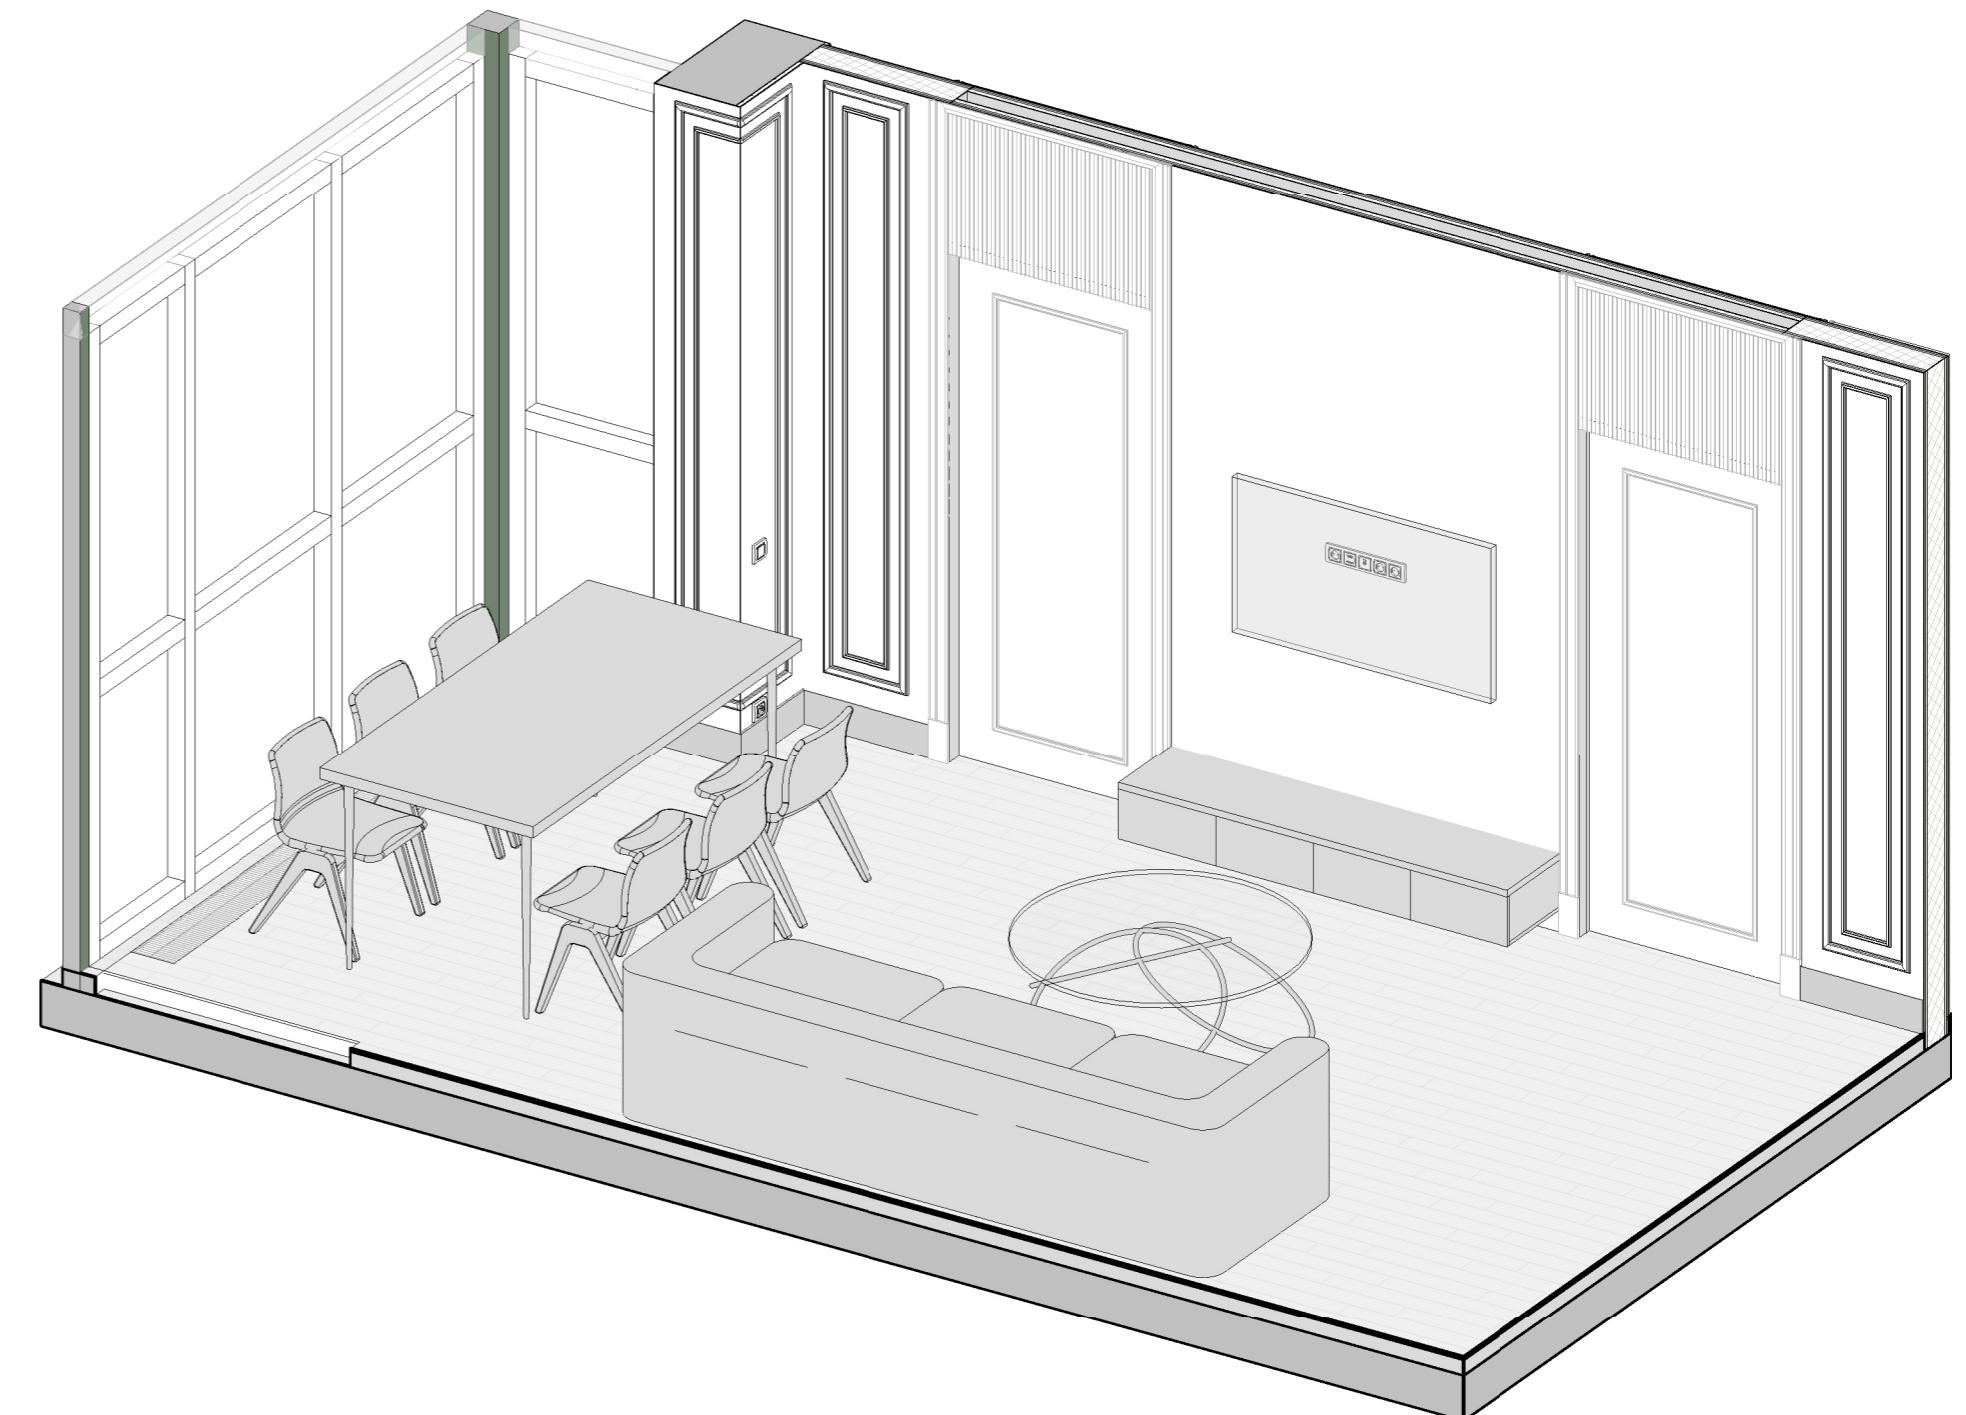
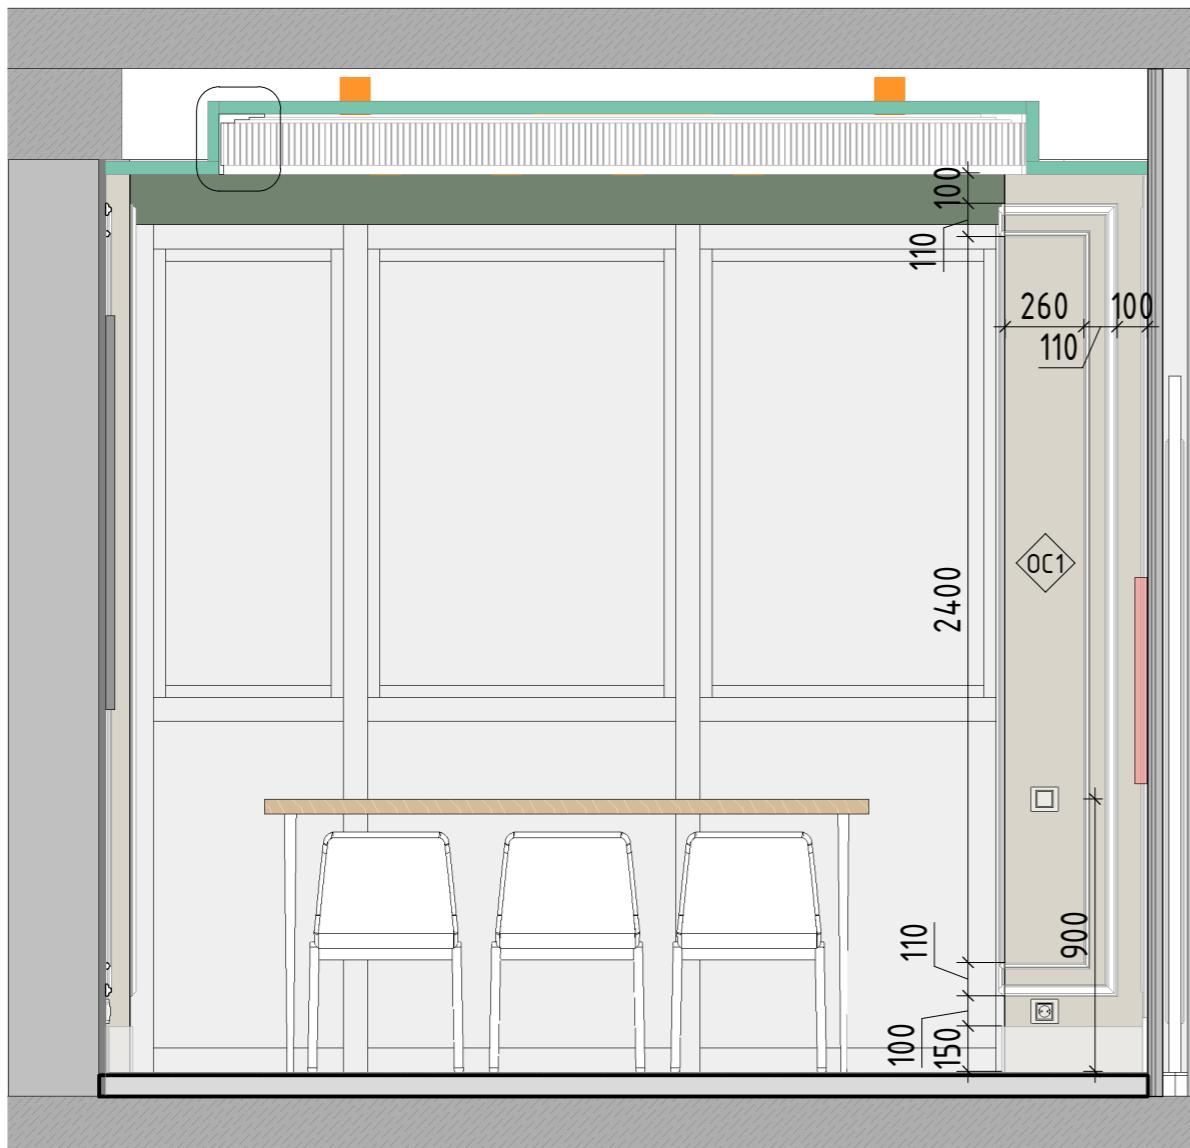


Примечания:

1. За отметку 0.000 принята отметка чистого пола квартиры.
2. Все размеры уточняются по месту.
3. Наличник дверей со стороны санузлов на 100 мм ниже чем в остальных помещениях

Дизайнер	Лист	Листов
АИ		
Заказчик		
ГОСТИНАЯ. РАЗВЕРТКА СТЕН		
Luxhouse_studio		

Вид-1

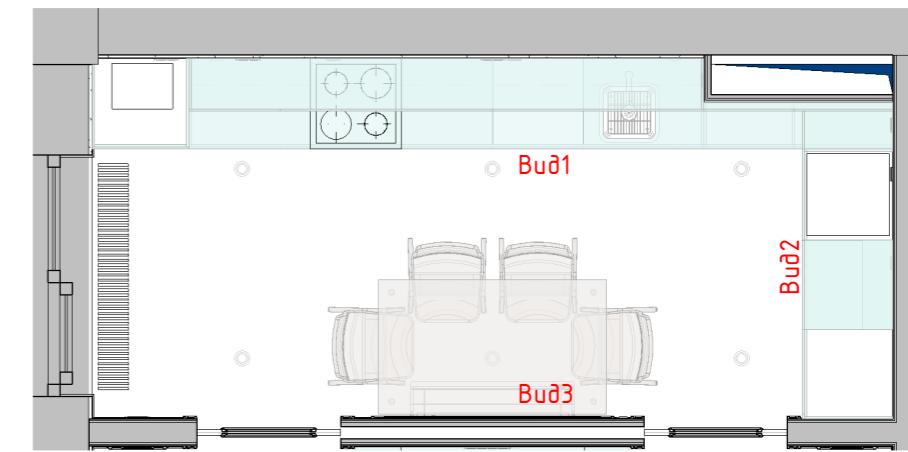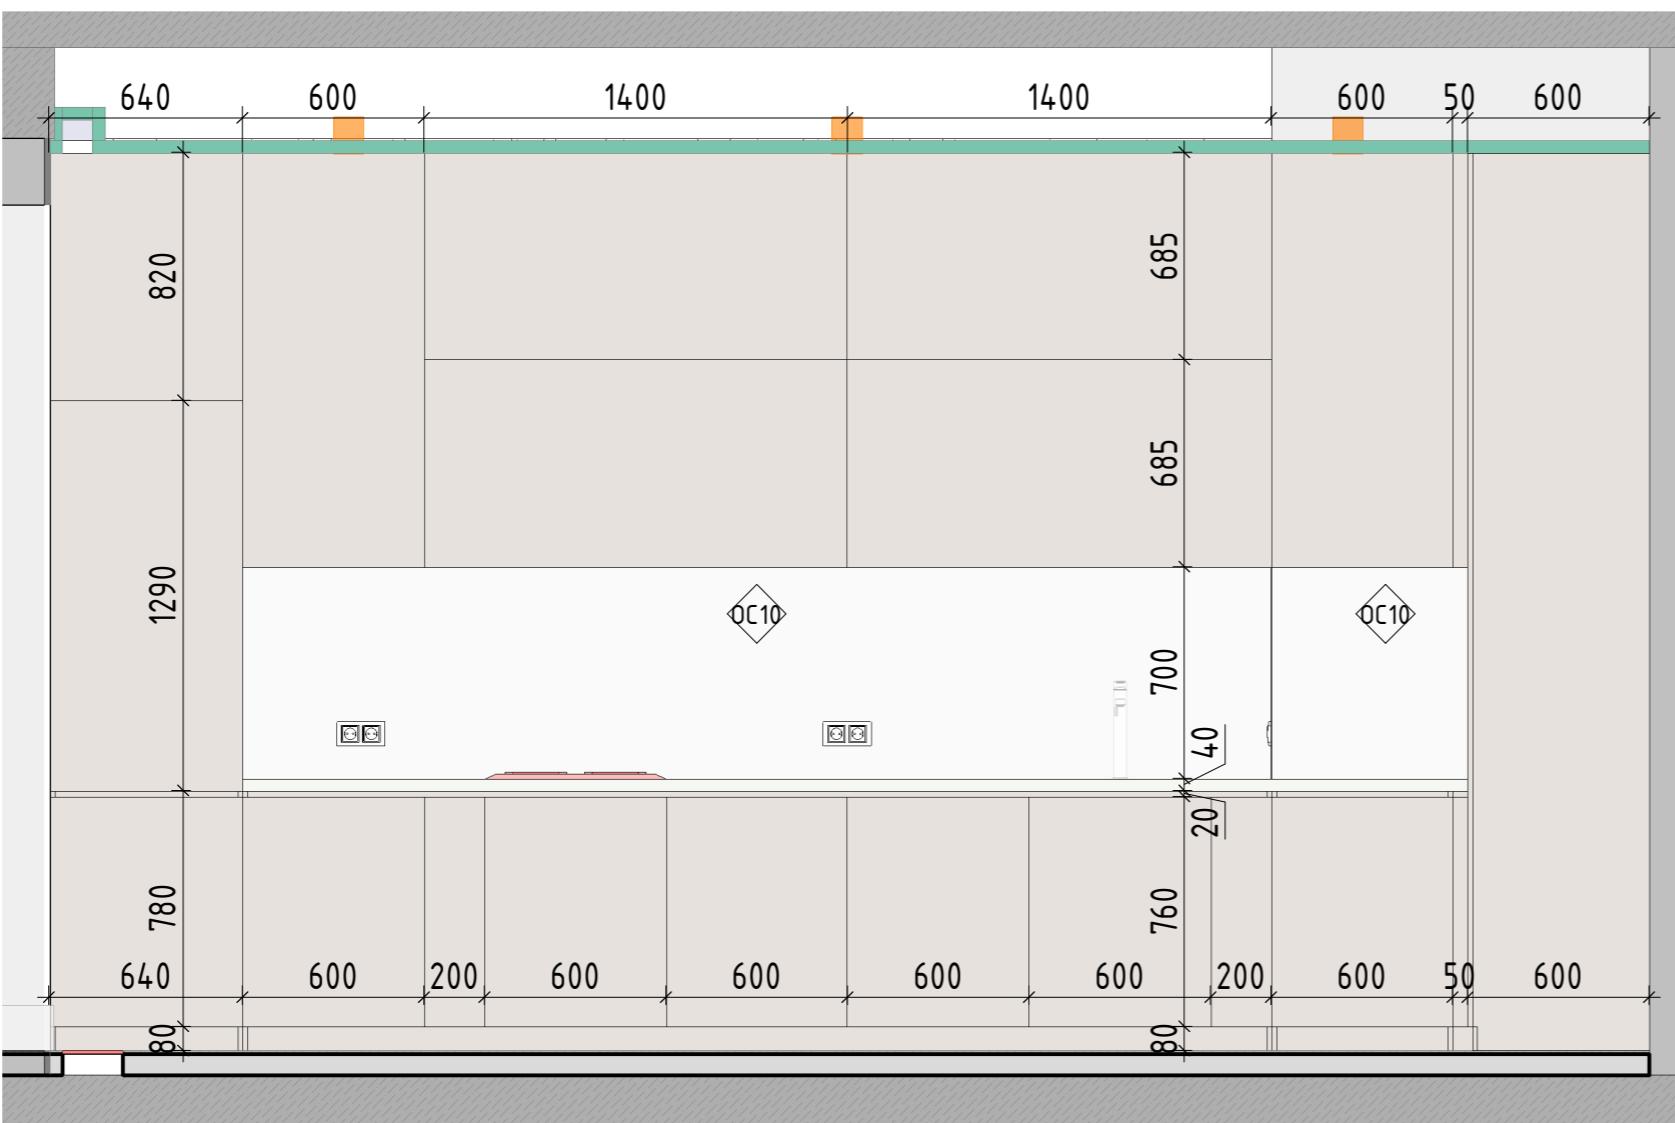

Примечание:

- (OC) - Штукатурка
- (OC1) - Tikkurila_Y487 Пиацца
- (OC2) - Tikkurila_X487 Laasti_Раствор
- (OC3) - Tikkurila_X445 Lido_Лидо
- (OC4) - Плитка 3000x1000 NOIR DESIR BOCCIARDATO
- (OC5) - Плитка 3000x1000 BIANCO LASA BOCCIARDATO
- (OC6) - Белый керамогранит 1200x600, Vitra
- (OC7) - Плитка 3000x1000 VERDERAME LUX
- (OC8) - ARVEN RECTIFIED PARLAK NANO 60X120 OT KUTAHYA
- (OC9) - 55012910RL 60x120 ATLANTIS БЕЛЫЙ ЛАПАТИРОВАННЫЙ
- (OC10) - Фартук на кухне
- Двери/Гардеробные шкафы/Плинтусы Цвет - Tikkurila_G497 Hoygu_Пар


Примечание:

Габариты кухонной мебели могут отличаться по факту от выбранной модели бытовой техники

Примечания:

1. За отмечку 0.000 принята отмечка чистого пола квартиры.
2. Все размеры уточняются по месту.
3. Наличник дверей со стороны санузлов на 100 мм ниже чем в остальных помещениях

Стадия	Лист	Листов
Дизайнер		
АИ		
Заказчик		
КУХНЯ. РАЗВЕРТКА СТЕН		Luxhouse_studio

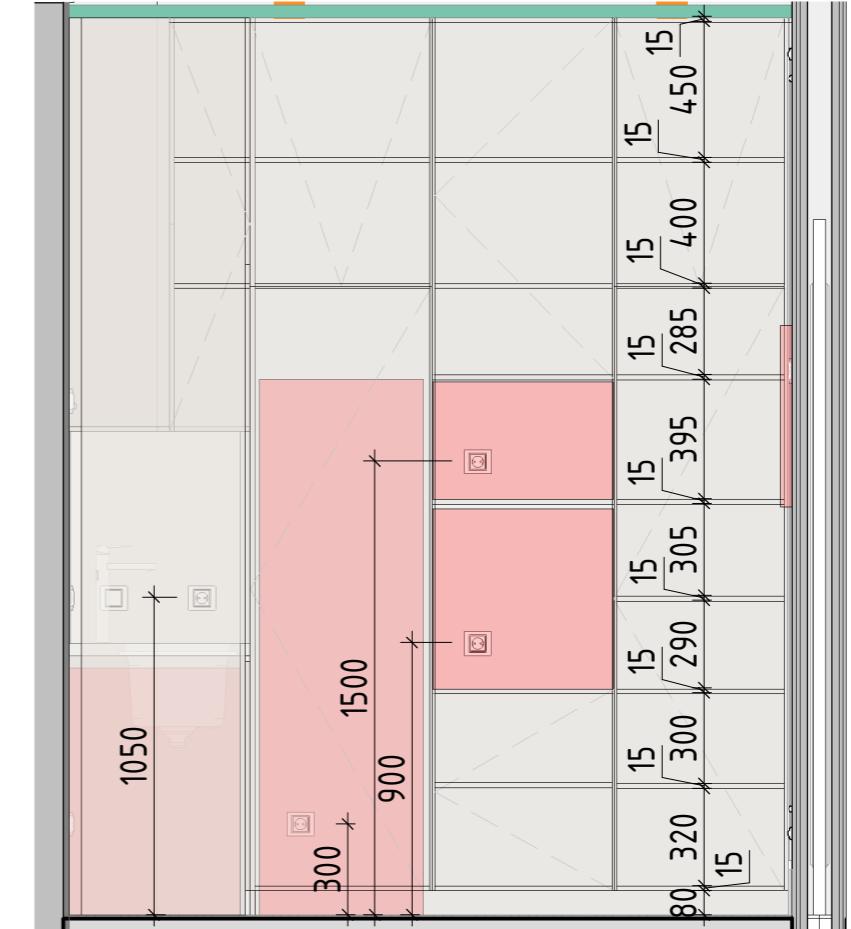

Примечания:

- За отметку 0.000 принята отметка чистого пола квартиры.
- Все размеры уточняются по месту.
- Наличник дверей со стороны санузлов на 100 мм ниже чем в остальных помещениях

Примечание:


Габариты кухонной мебели могут отличаться по факту от выбранной модели бытовой техники

Стадия	Лист	Листов
АИ		
Дизайнер		
Заказчик		


КУХНЯ. РАЗВЕРТКА СТЕН

Luxhouse_studio

Вид 1

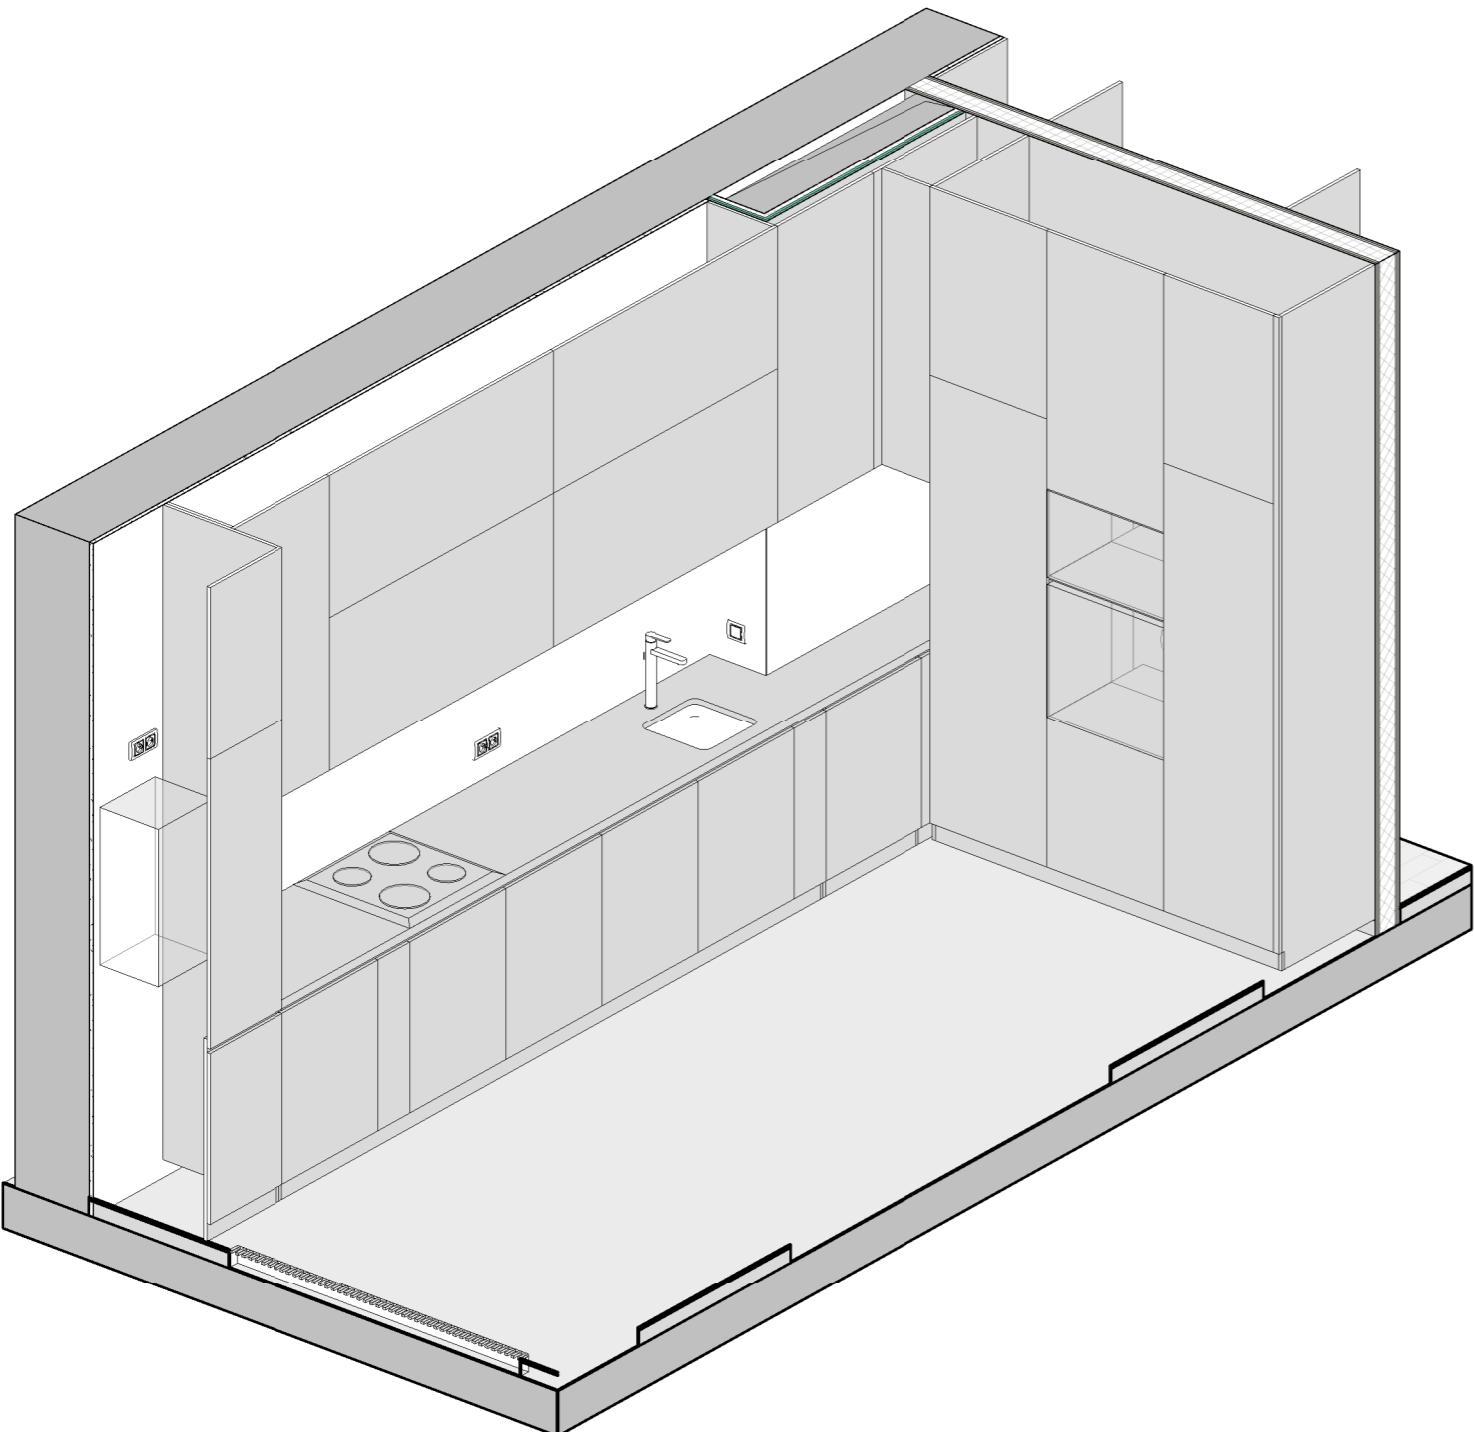

Вид 2

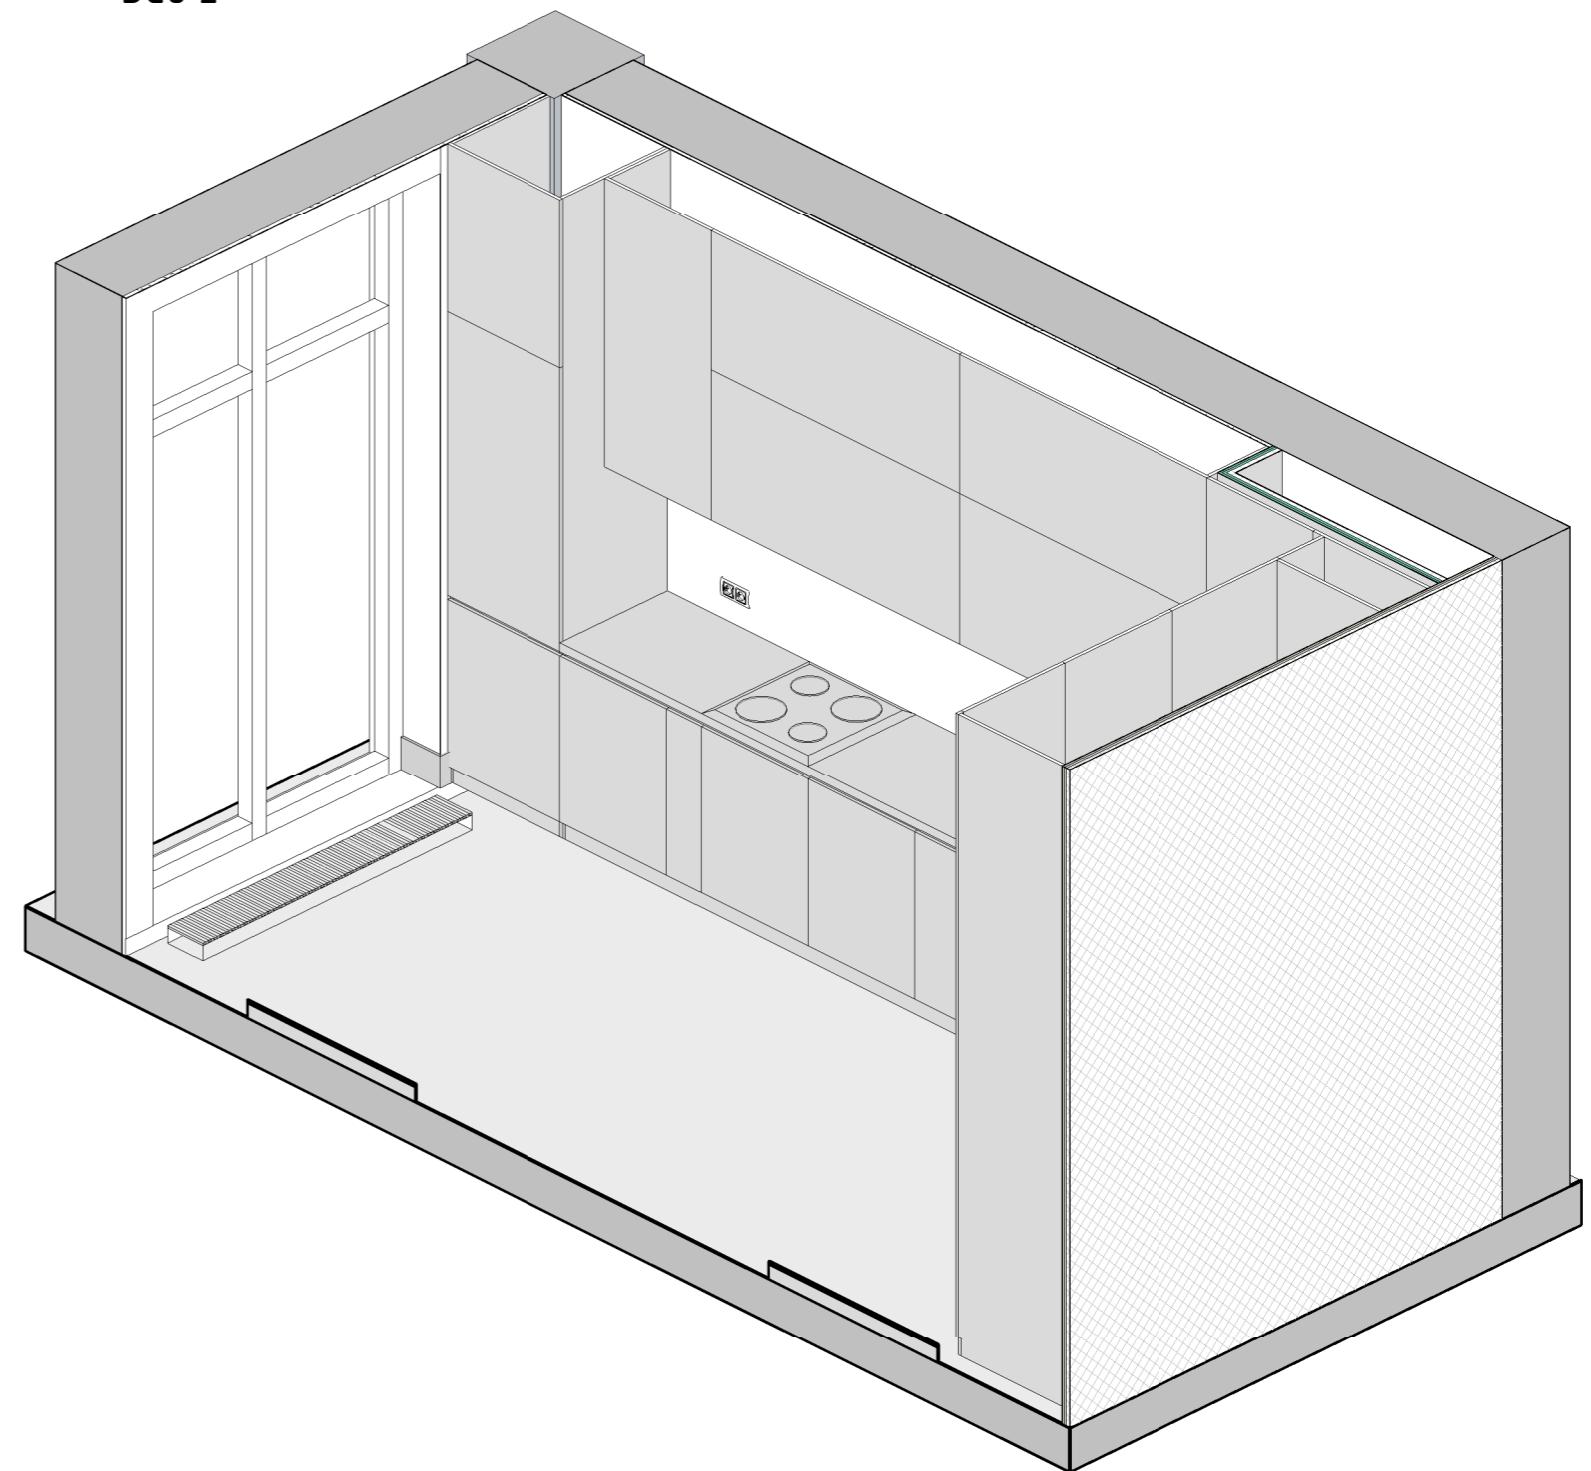

Дизайнер			
Заказчик			

КУХНЯ ЗД ВИД


Luxhouse_studio

Формат: А3




Luxhouse_studio

Вид-1

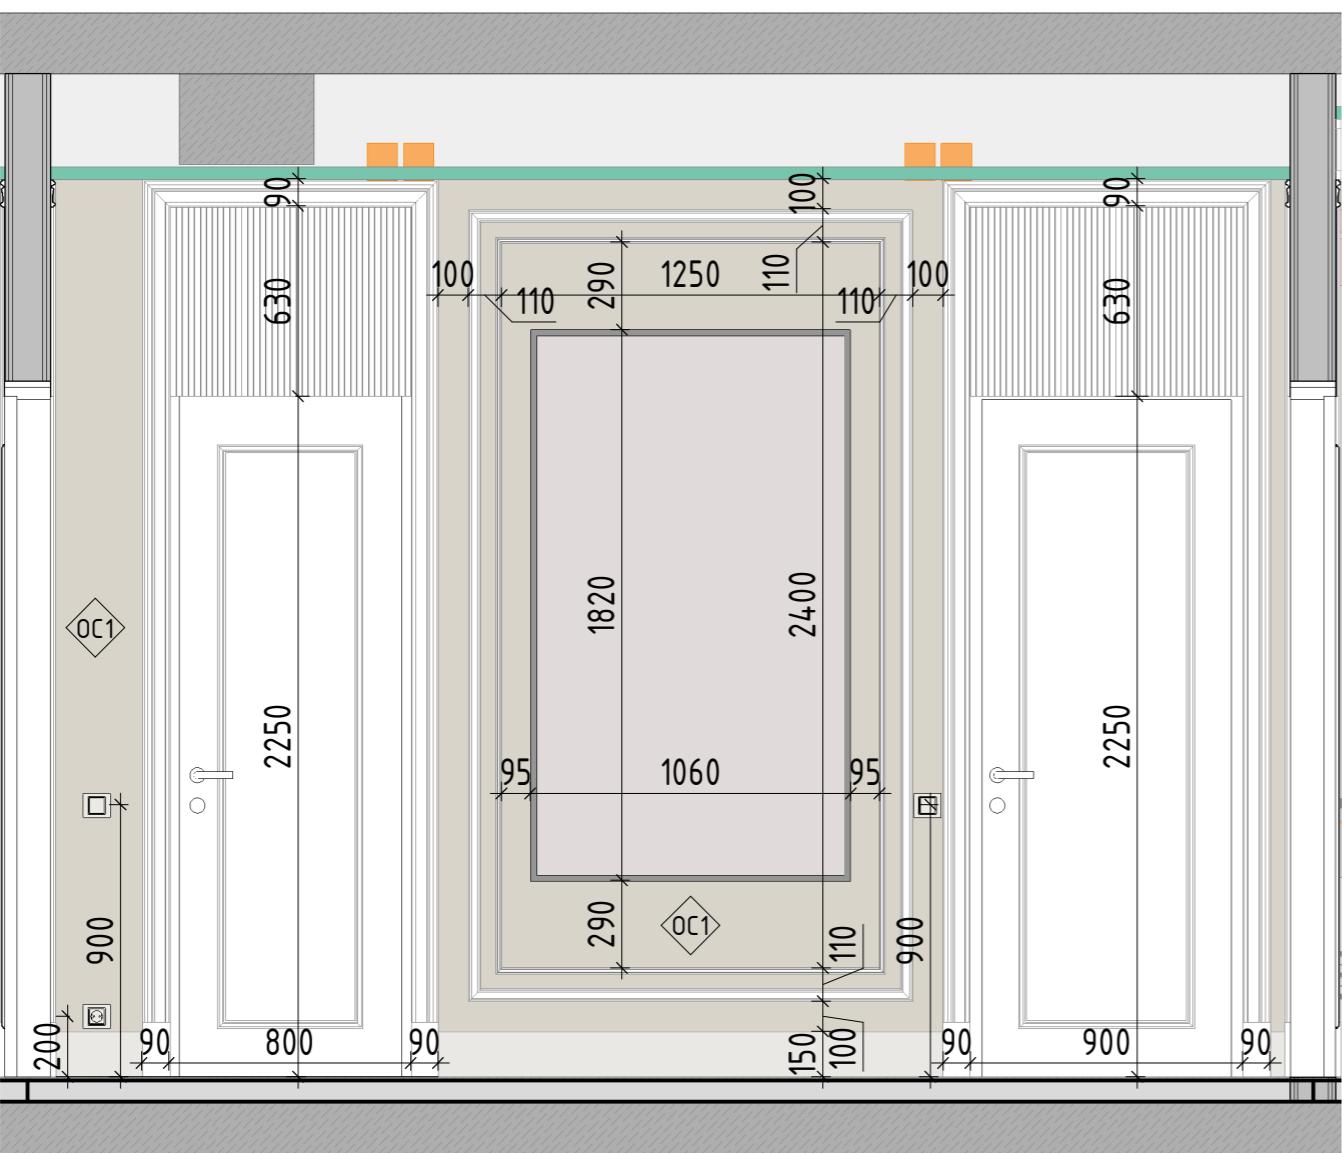

Вид-2

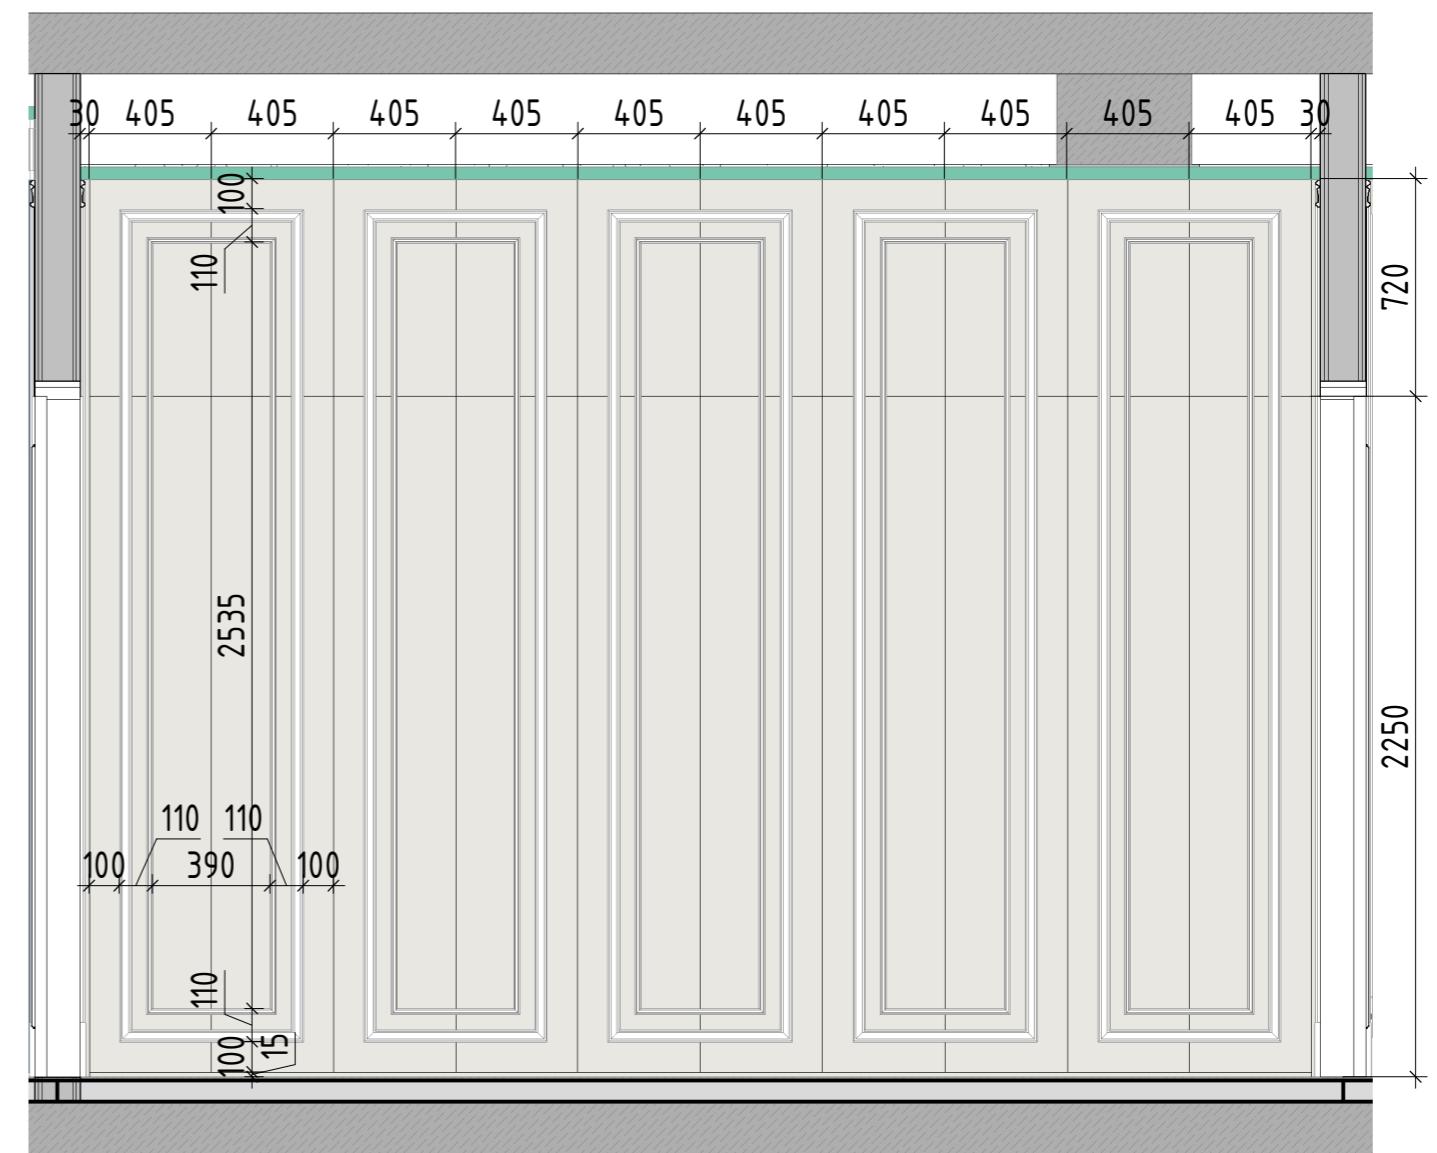


Примечание:


- (OC) -Штукатурка
- (OC1) -Tikkurila_Y487 Пиацца
- (OC2) -Tikkurila_X487 Laasti_Раствор
- (OC3) -Tikkurila_X445 Lido_Либо
- (OC4) -Плитка 3000x1000 NOIR DESIR BOCCIARDATO
- (OC5) -Плитка 3000x1000 BIANCO LASA BOCCIARDATO
- (OC6) -Белый керамогранит 1200x600, Vitra
- (OC7) -Плитка 3000x1000 VERDERAME LUX
- (OC8) -ARVEN RECTIFIED PARLAK NANO 60X120 OT KUTAHYA
- (OC9) -55012910RL 60x120 ATLANTIS БЕЛЫЙ ЛАПАТИРОВАННЫЙ
- (OC10) -Фартук на кухне
- Двери/Гардеробные шкафы/Плинтусы Цвет - Tikkurila_G497 Ноуѓу_Пар

Примечания:


1. За отметку 0.000 принята отметка чистого пола квартиры.
2. Все размеры уточняются по месту.
3. Наличник дверей со стороны санузлов на 100 мм ниже чем в остальных помещениях

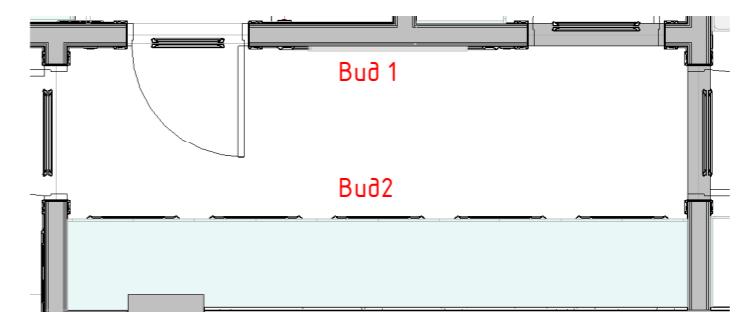

Дизайнер				Стадия	Лист	Листов
				АИ		
Заказчик				КОРИДОР. РАЗВЕРТКА СТЕН		
Luxhouse_studio						Формат: А3

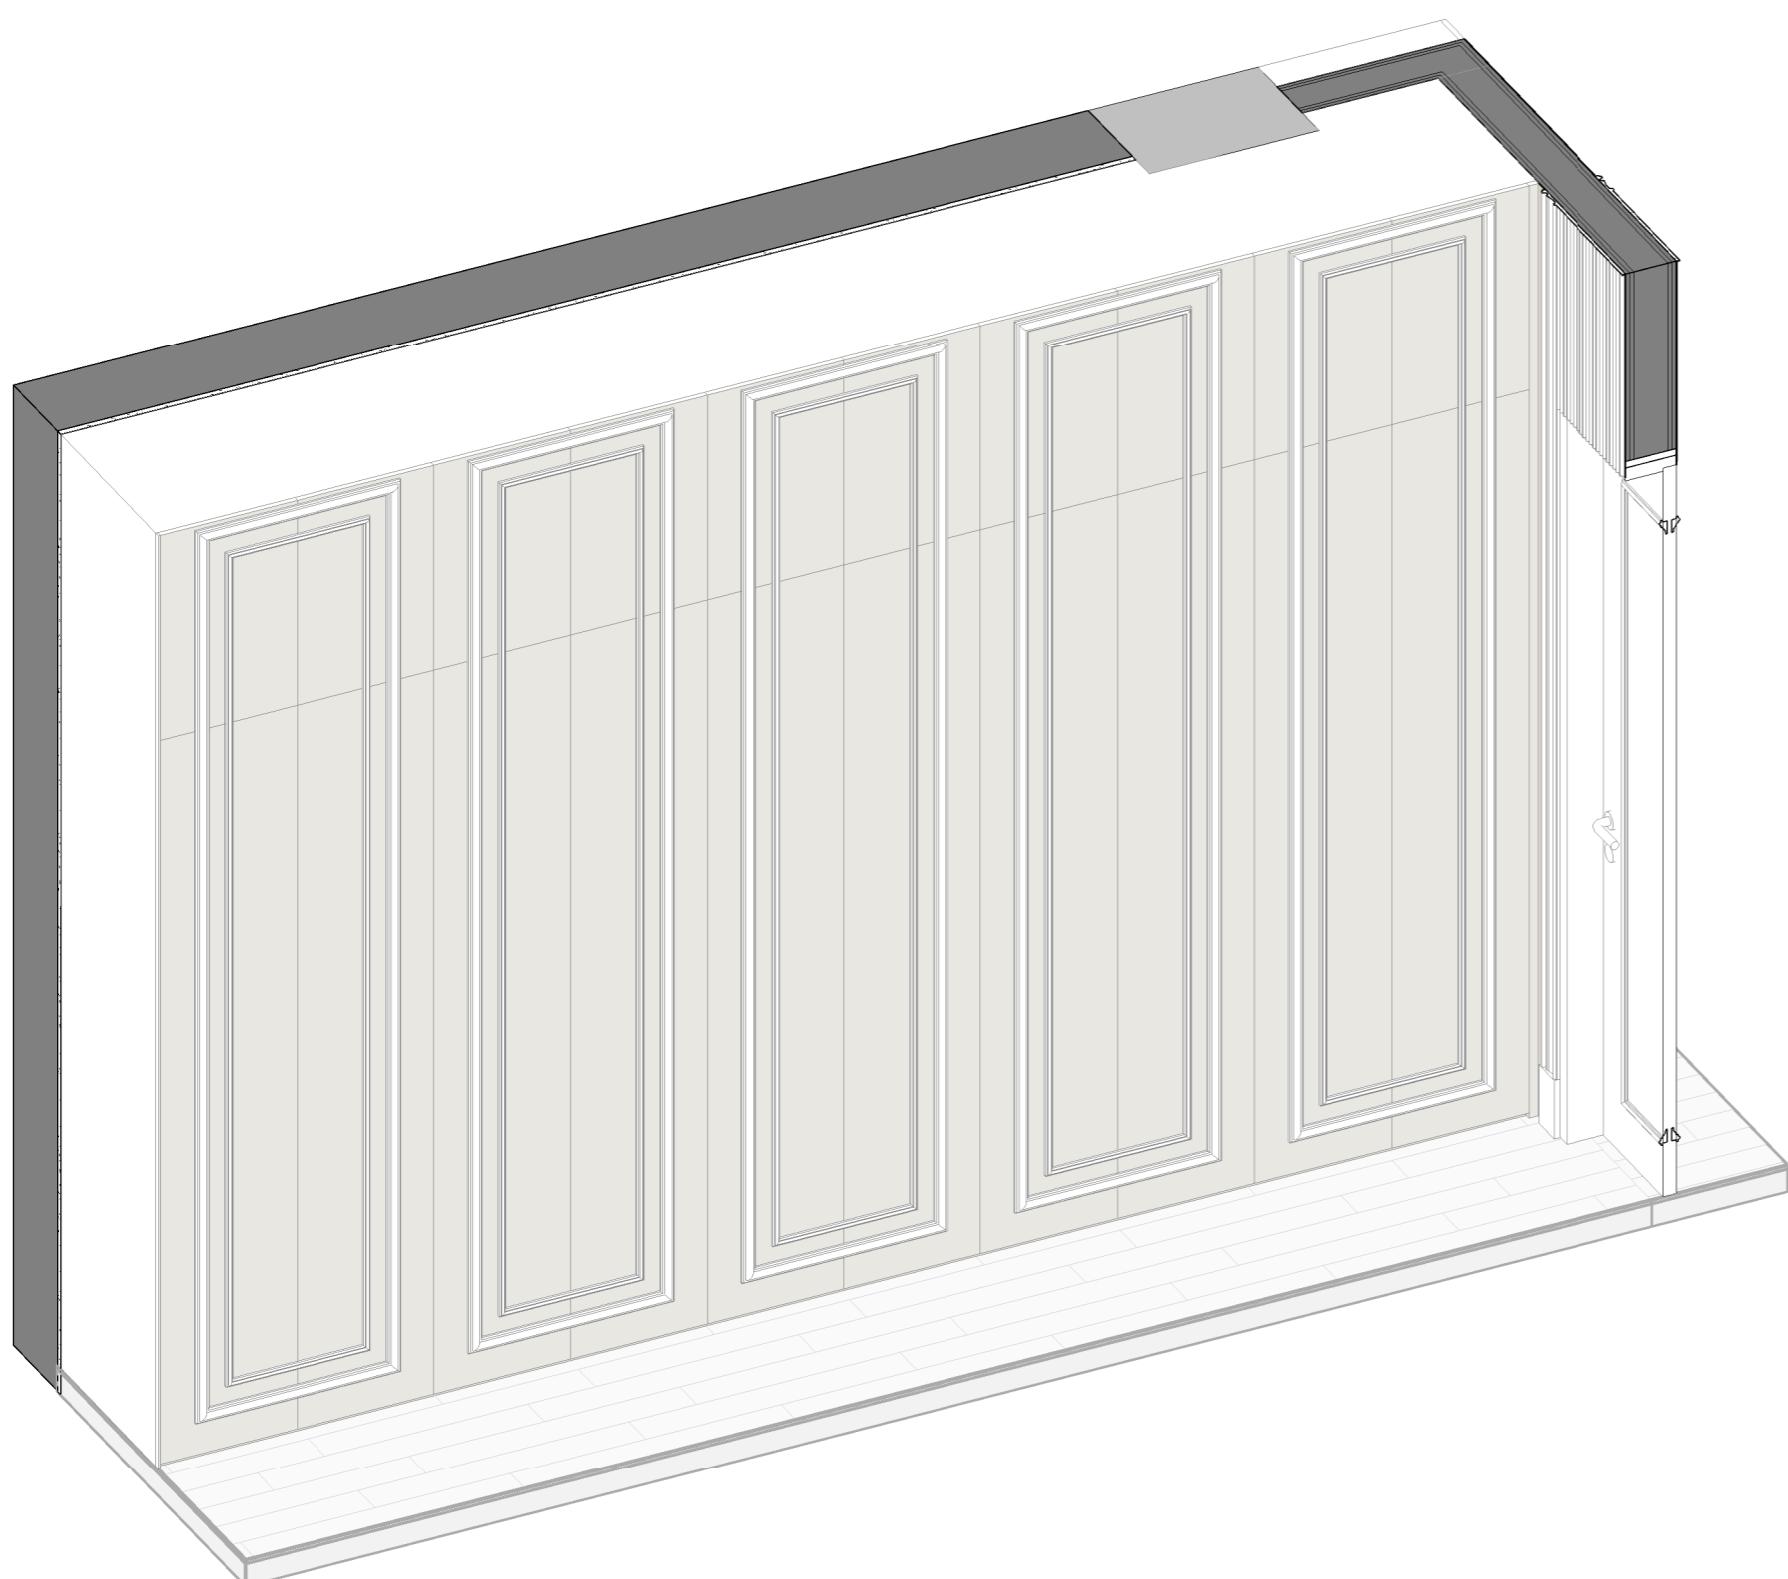

Вид-3 Наполнение

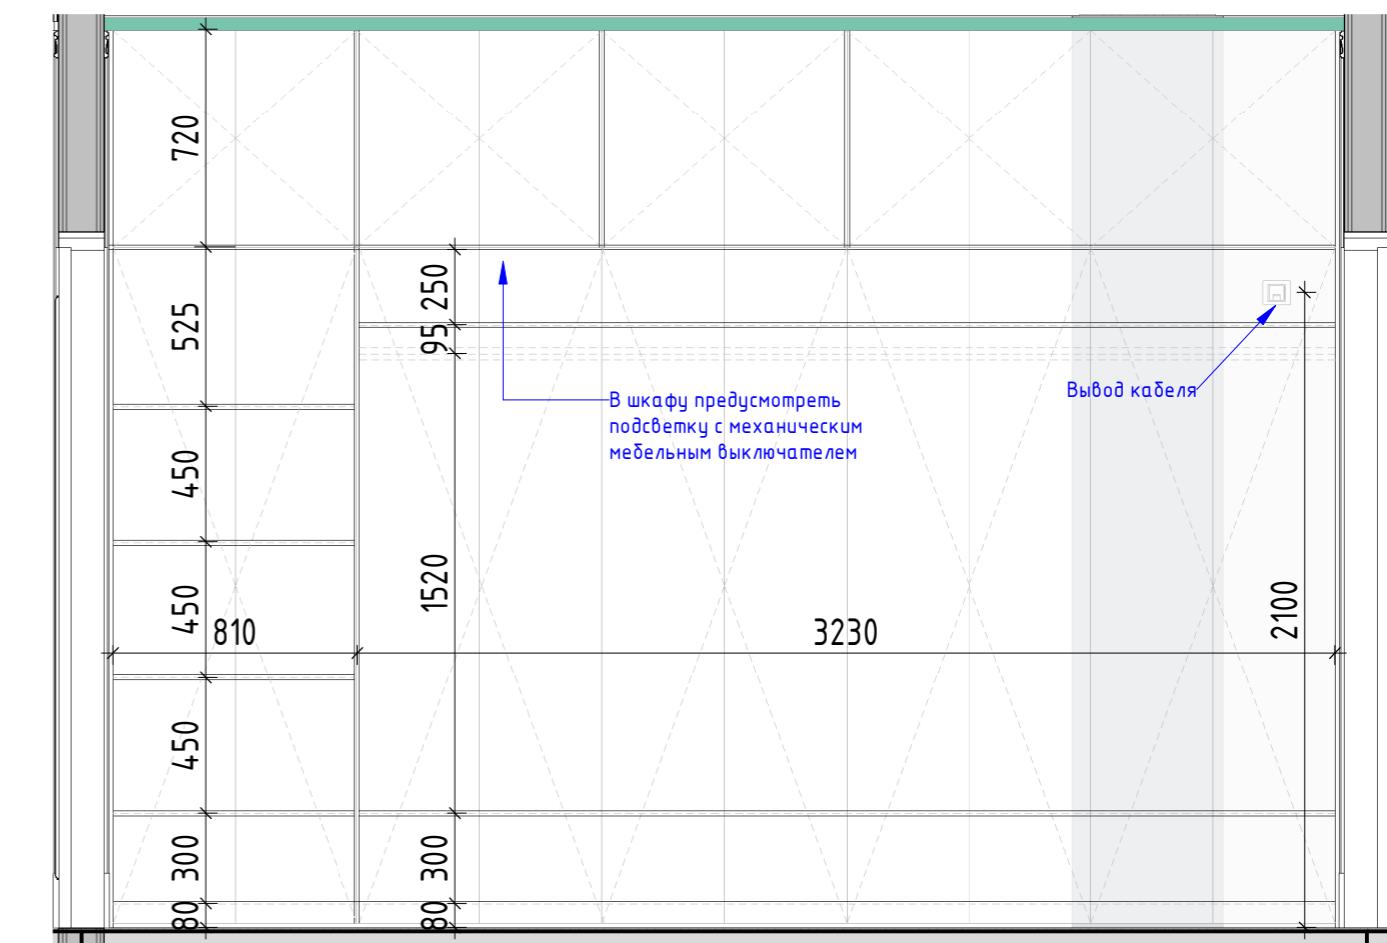

Дизайнер			
Заказчик			


КОРИДОР. РАЗВЕРТКА СТЕН

Luxhouse_studio



Формат: А3

Стадия	Лист	Листов
АИ		

Вид-1

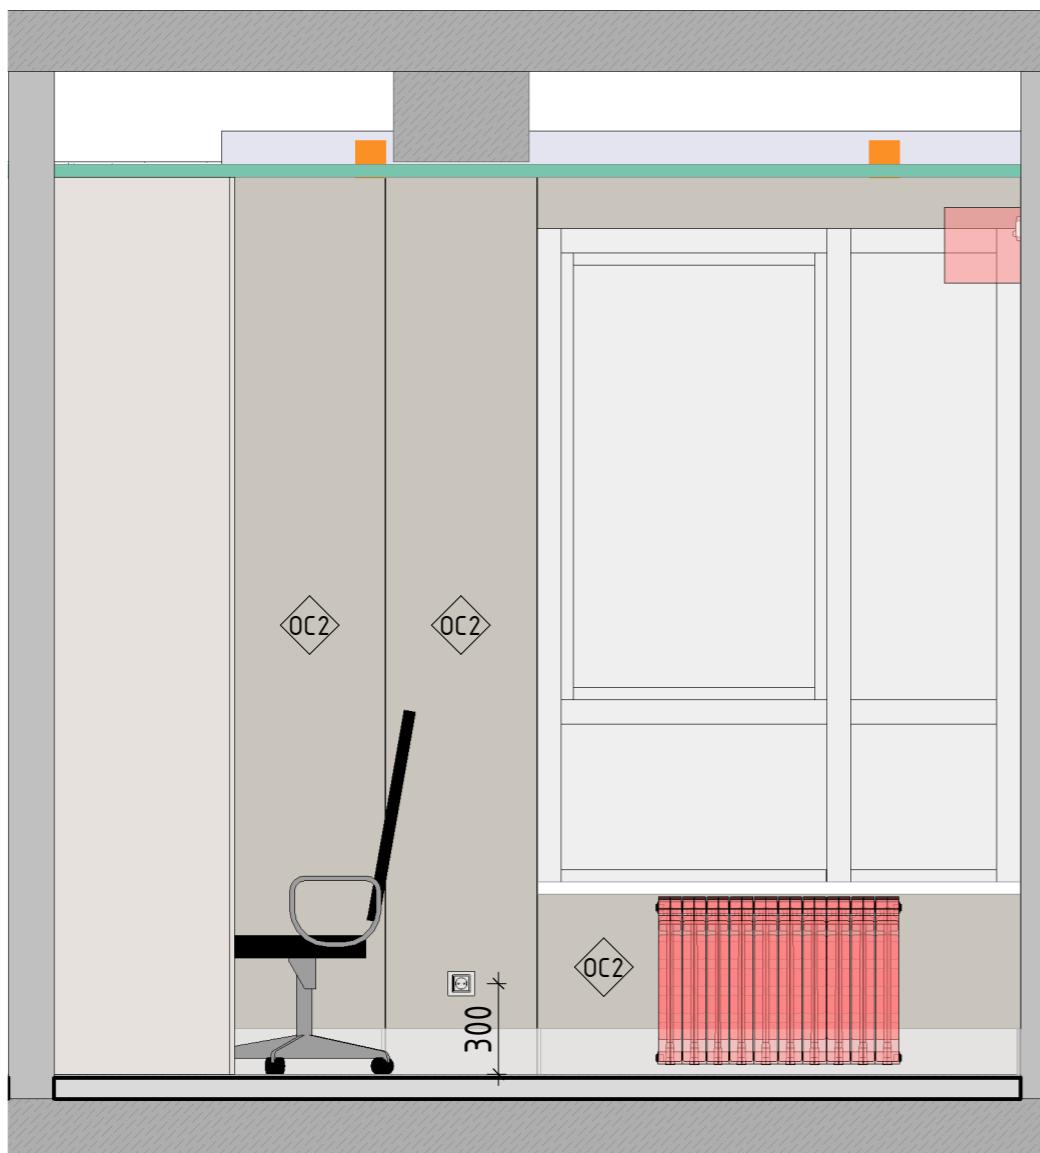

Вид-2

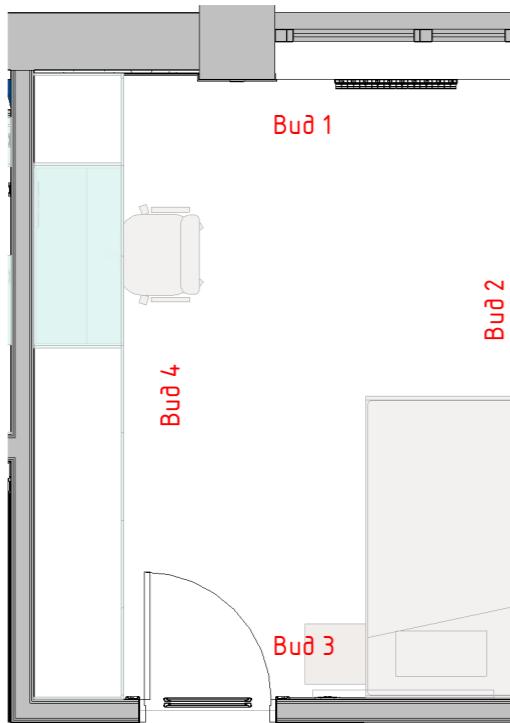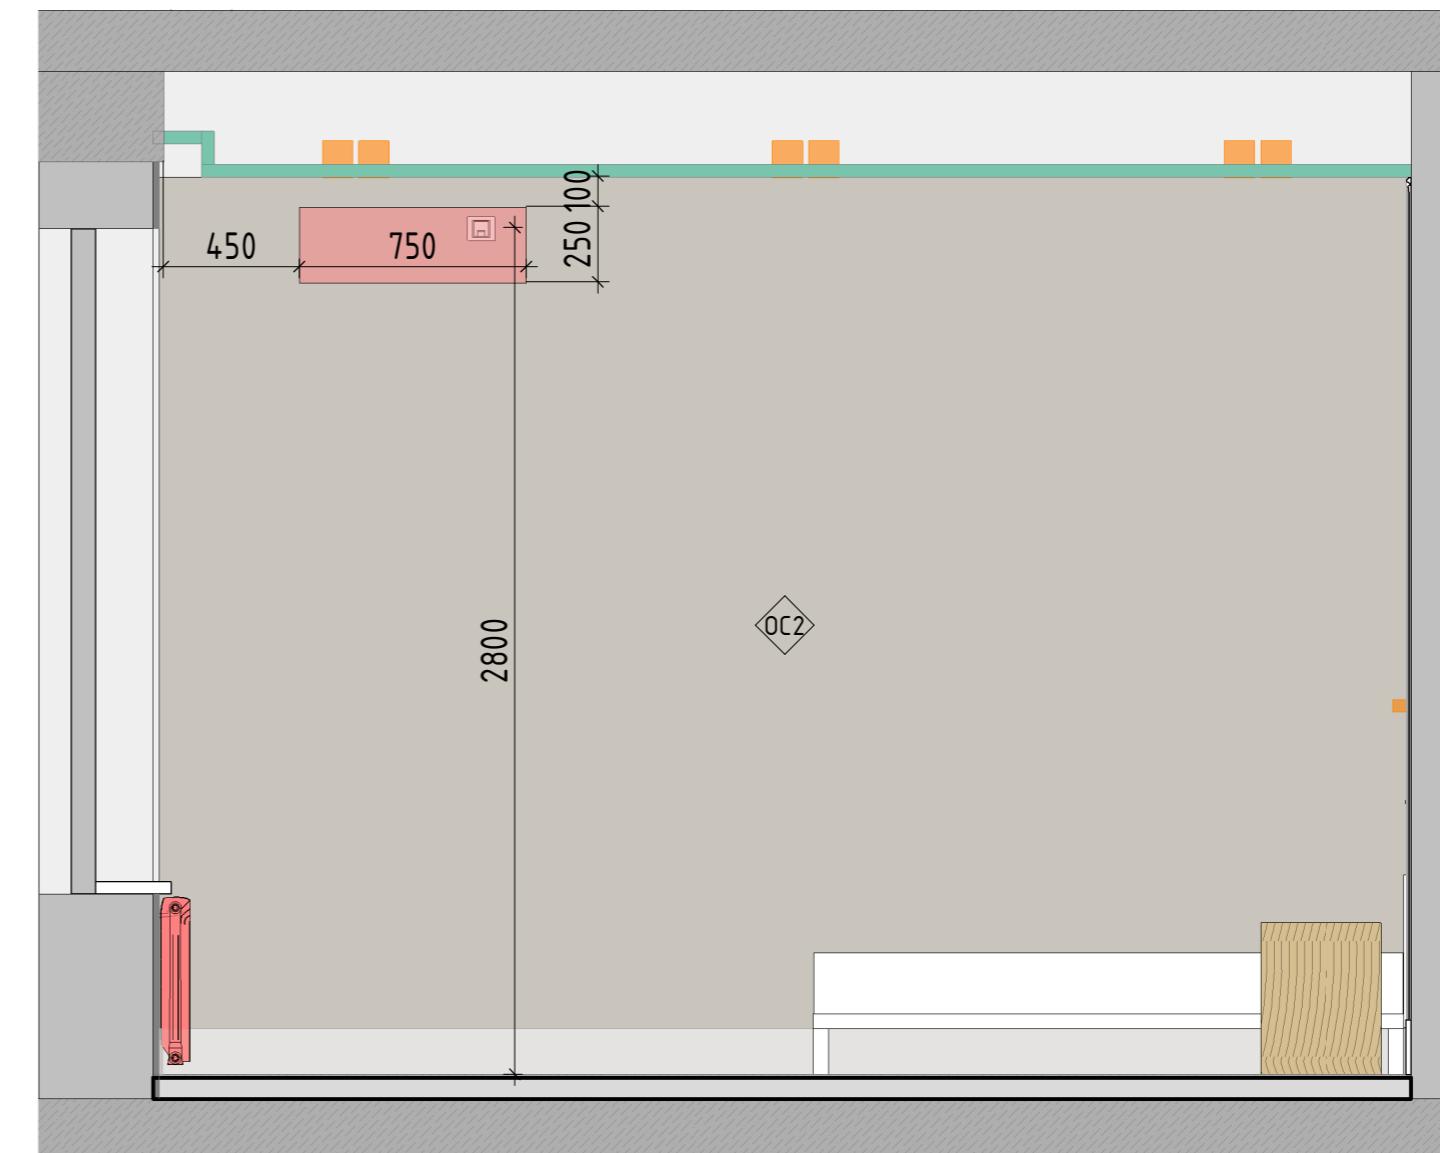

Примечание:

- OC - Штукатурка
- OC1 - Tikkurila_Y487 Пиаца
- OC2 - Tikkurila_X487 Laasti_Раствор
- OC3 - Tikkurila_X445 Lido_Лидо
- OC4 - Плитка 3000x1000 NOIR DESIR BOCCIARDATO
- OC5 - Плитка 3000x1000 BIANCO LASA BOCCIARDATO

- OC6 - Белый керамогранит 1200x600, Vitra
- OC7 - Плитка 3000x1000 VERDERAME LUX
- OC8 - ARVEN RECTIFIED PARLAK NANO 60X120 OT KUTAHYA
- OC9 - 55012910RL 60x120 ATLANTIS БЕЛЫЙ ЛАПАТИРОВАННЫЙ
- OC10 - Фартук на кухне
- Двери/Гардеробные шкафы/Плинтусы Цвет - Tikkurila_G497 Ноугу_Пар

Примечания:

1. За отметку 0.000 принята отметка чистого пола квартир.
2. Все размеры уточняются по месту.
3. Наличник дверей со стороны санузлов на 100 мм ниже чем в остальных помещениях

Дизайнер			
Заказчик			

ДЕТСКАЯ СПАЛЬНЯ.
РАЗВЕРТКА СТЕН

Luxhouse_studio

Формат: А3





Формат: А3

Листов

Стадия	Лист	Листов
AI		

Вид-4

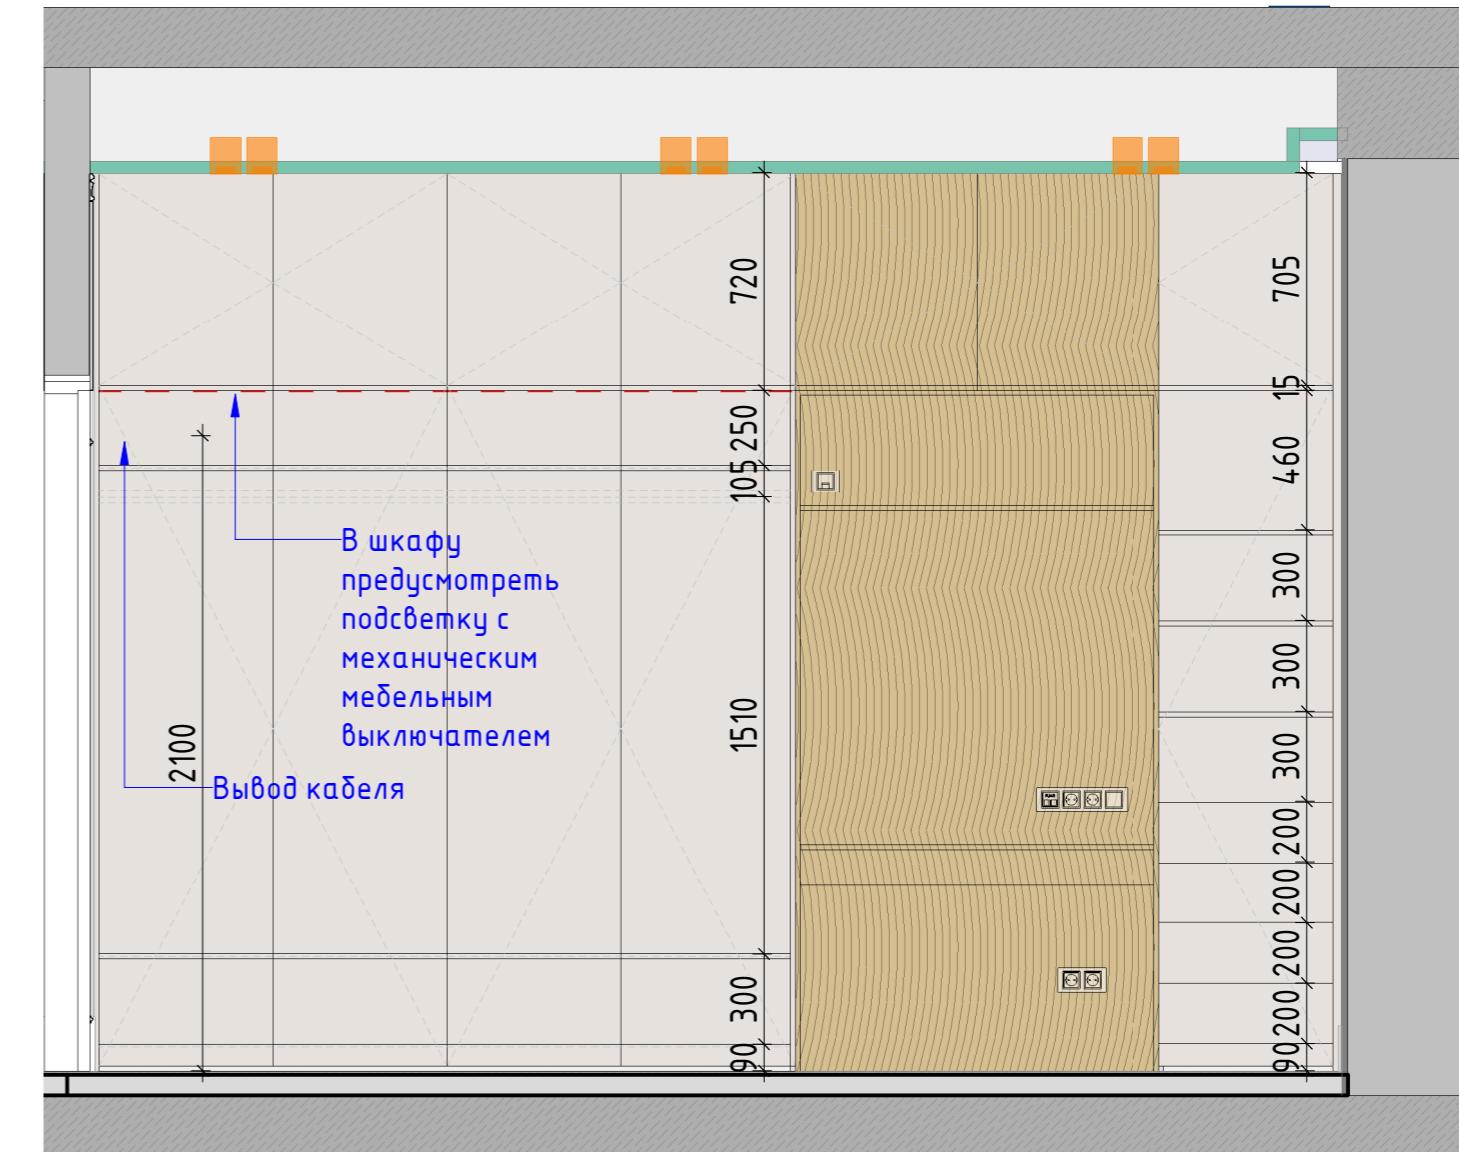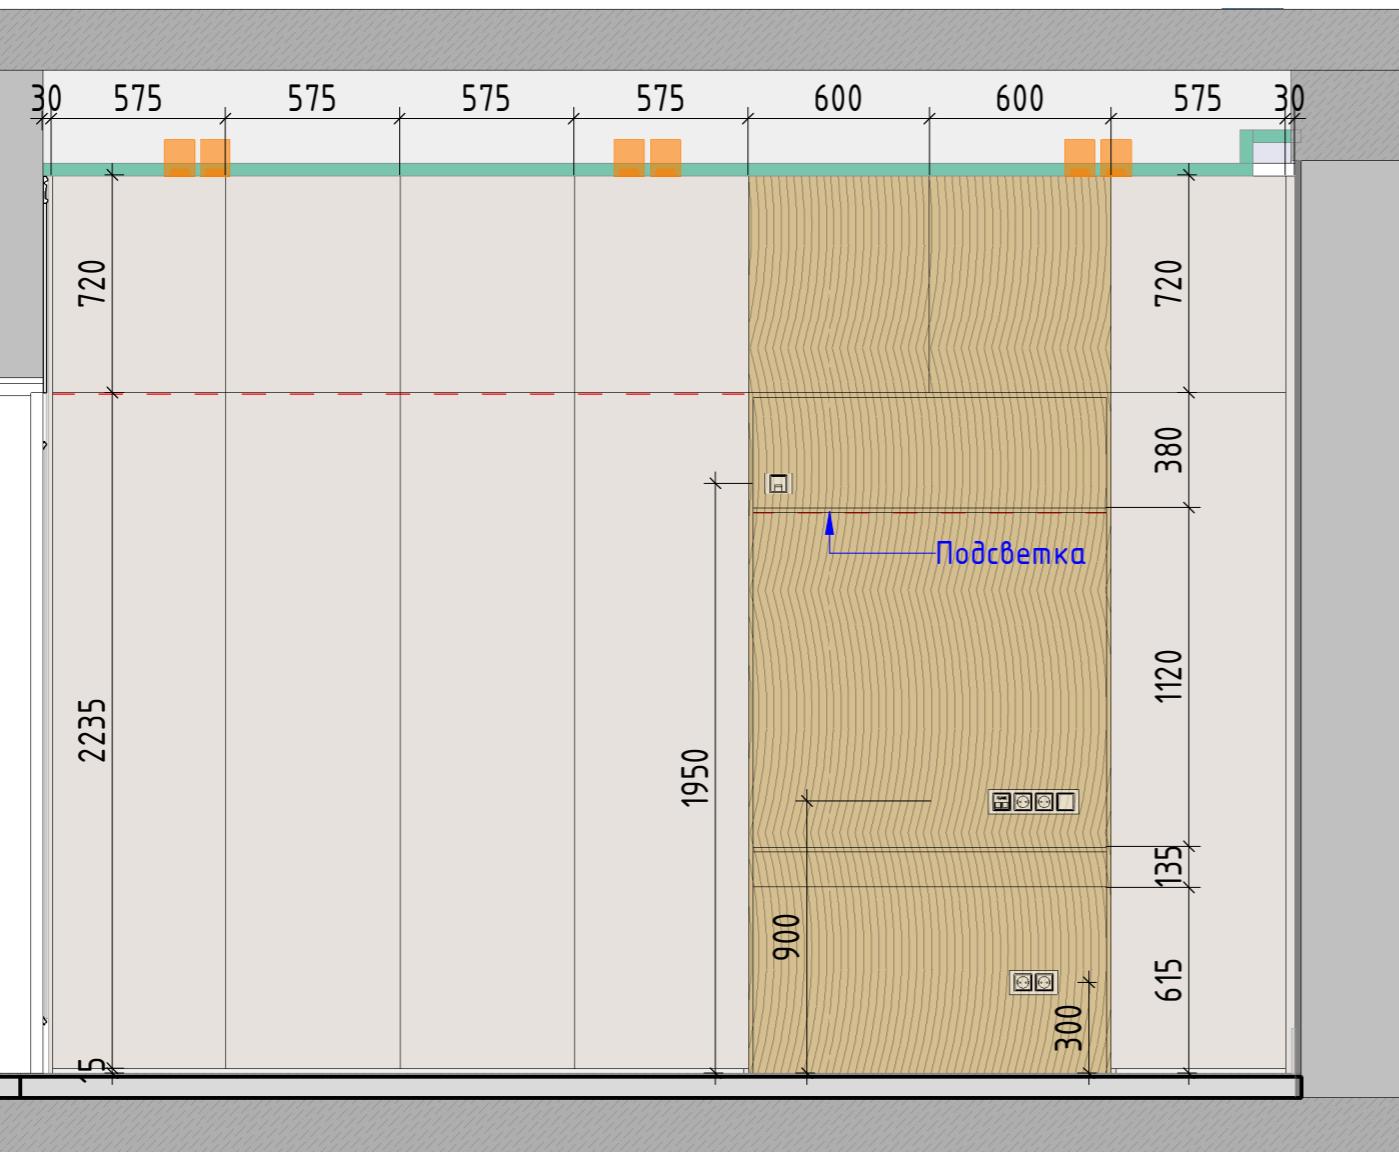

Примечание:


- | | | | |
|-------|---|--------|---|
| (OC) | -Штукатурка | (OC6) | -Белый керамогранит 1200x600, Vitra |
| (OC1) | -Tikkurila_Y487 Пиаца | (OC7) | -Плитка 3000x1000 VERDERAME LUX |
| (OC2) | -Tikkurila_X487 Laasti_Расмбор | (OC8) | -ARVEN RECTIFIED PARLAK NANO 60X120 OT KUTAHYA |
| (OC3) | -Tikkurila_X445 Lido_Лидо | (OC9) | -55012910RL 60x120 ATLANTIS БЕЛЫЙ ЛАПАТИРОВАННЫЙ |
| (OC4) | -Плитка 3000x1000 NOIR DESIR BOCCIARDATO | (OC10) | -Фартук на кухне |
| (OC5) | -Плитка 3000x1000 BIANCO LASA BOCCIARDATO | | -Двери/Гардеробные шкафы/Плинтусы Цвет - Tikkurila_G497 Ноугу_Пар |

Примечания:

- За отметку 0.000 принята отметка чистого пола квартиры.
- Все размеры уточняются по месту.
- Наличник дверей со стороны санузлов на 100 мм ниже чем в остальных помещениях


Стадия	Лист	Листов
АИ		
ДЕТСКАЯ СПАЛЬНЯ. РАЗВЕРТКА СТЕН		Luxhouse_studio
Формат: А3		

Вид-1

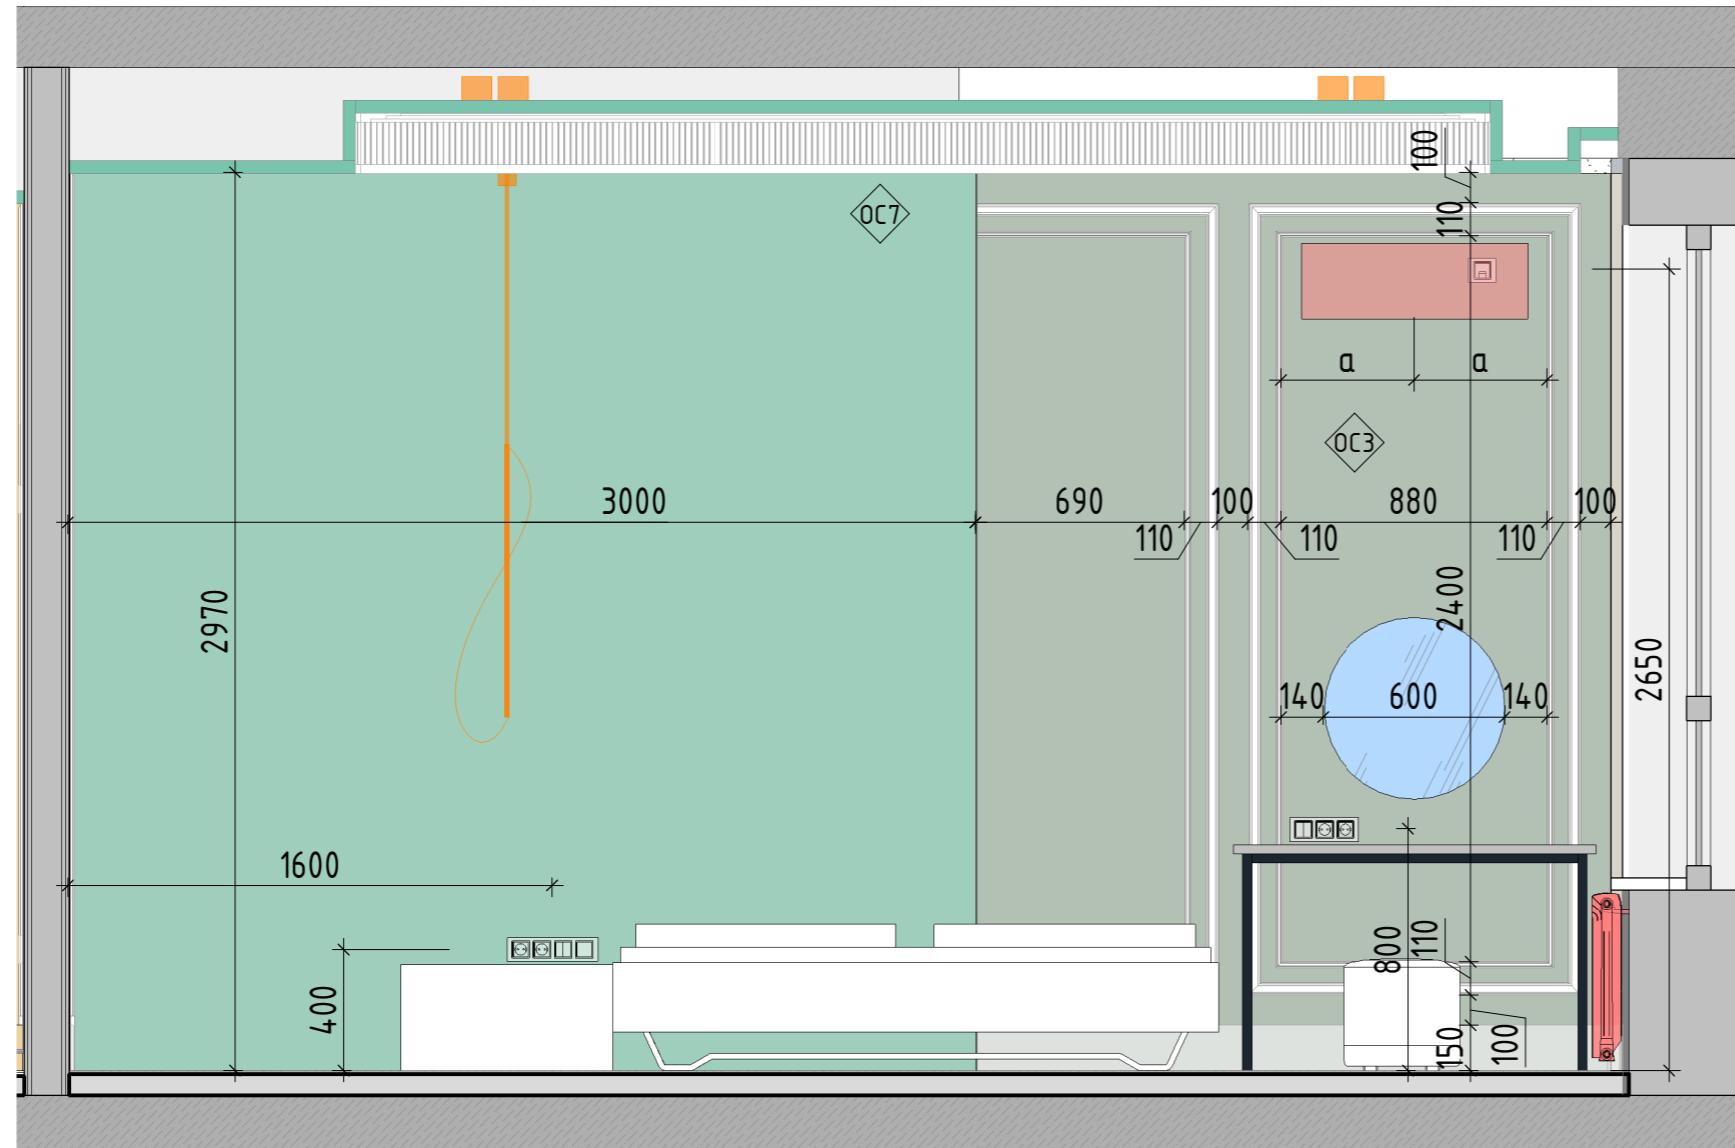

Примечание:

- OC - Штукатурка
- OC1 - Tikkurila_Y487 Пиаца
- OC2 - Tikkurila_X487 Laasti_Раствор
- OC3 - Tikkurila_X445 Lido_Лидо
- OC4 - Плитка 3000x1000 NOIR DESIR BOCCARDATO
- OC5 - Плитка 3000x1000 BIANCO LASA BOCCARDATO
- OC6 - Белый керамогранит 1200x600, Vitra
- OC7 - Плитка 3000x1000 VERDERAME LUX
- OC8 - ARVEN RECTIFIED PARLAK NANO 60X120 ОТ KUTAHYA
- OC9 - 55012910RL 60x120 ATLANTIS БЕЛЫЙ ЛАПАТИРОВАННЫЙ
- OC10 - Фартук на кухне
- Двери/Гардеробные шкафы/Плинтусы Цвет - Tikkurila_G497 Ноугу_Пар

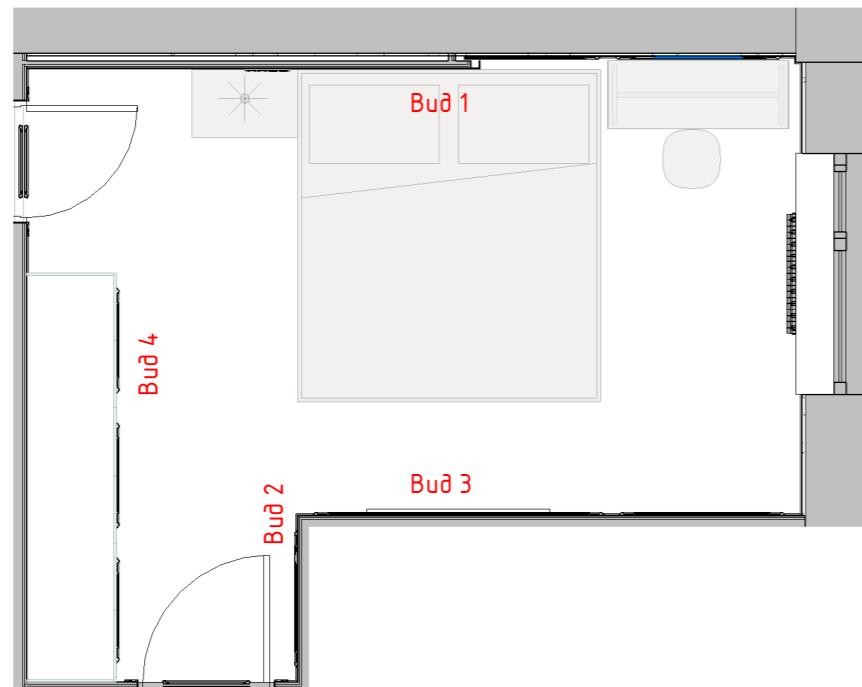


Примечания:


1. За отмечку 0.000 принята отмечка чистого пола квартиры.
2. Все размеры уточняются по месту.
3. Наличник дверей со стороны санузлов на 100 мм ниже чем в остальных помещениях

Стадия	Лист	Листов
Дизайнер		
Заказчик		
РОДИТЕЛЬСКАЯ СПАЛЬНЯ. РАЗВЕРТКА СТЕН	Luxhouse_studio	

Вид-2

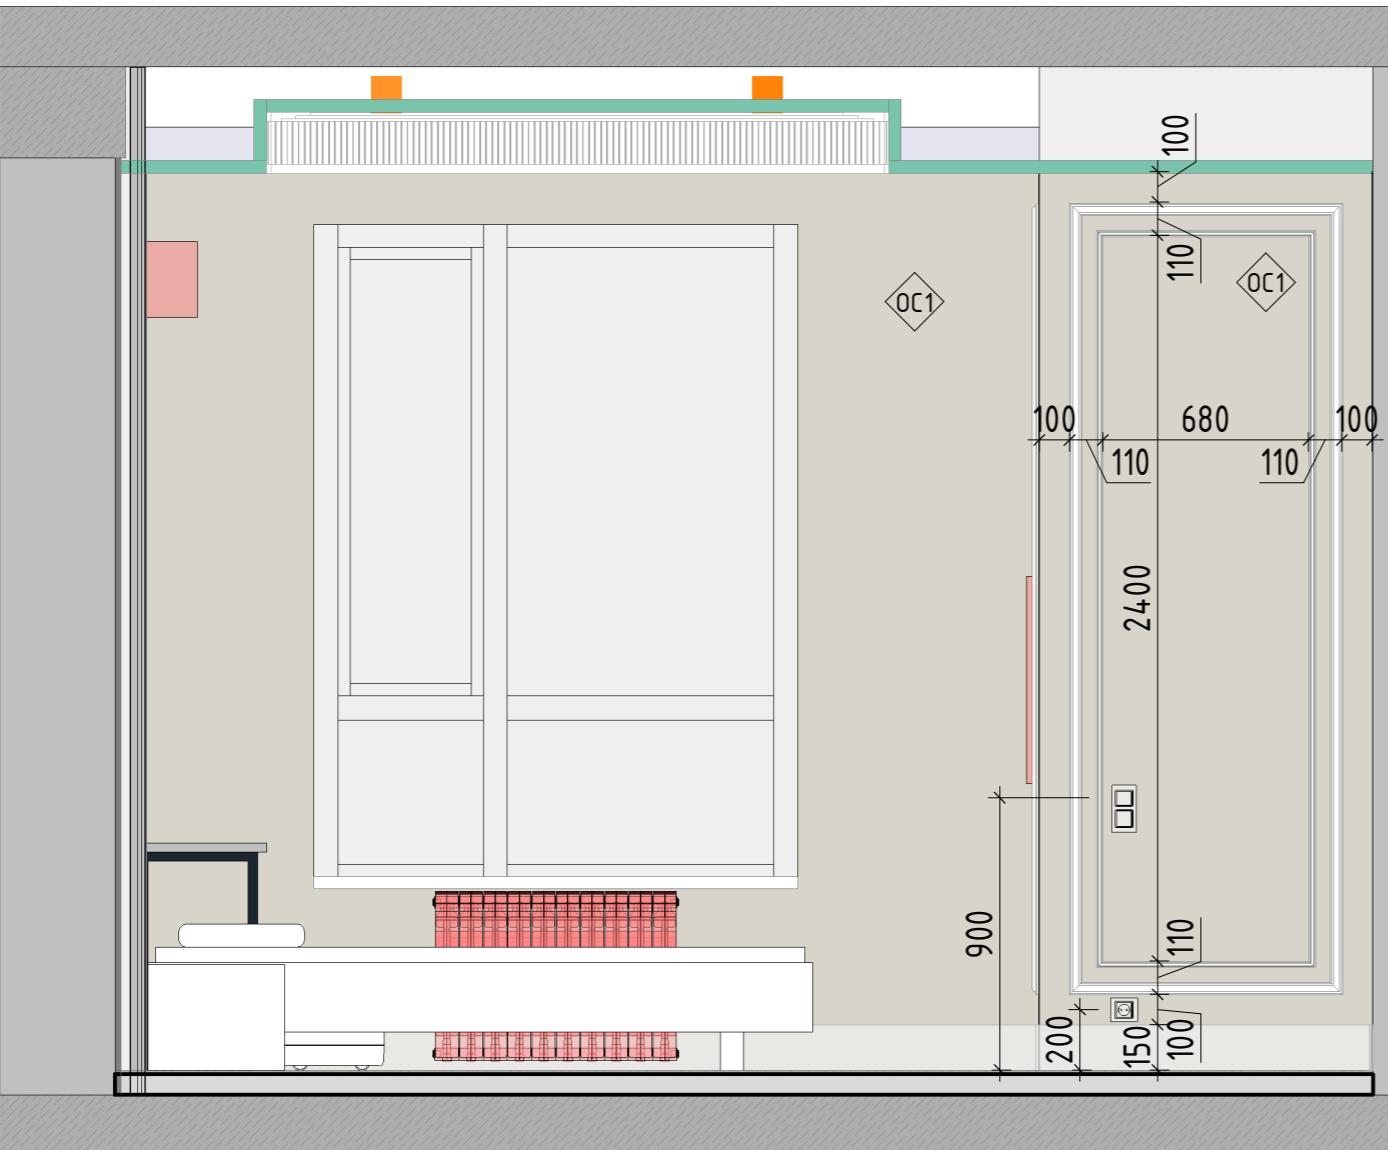

Вид-3

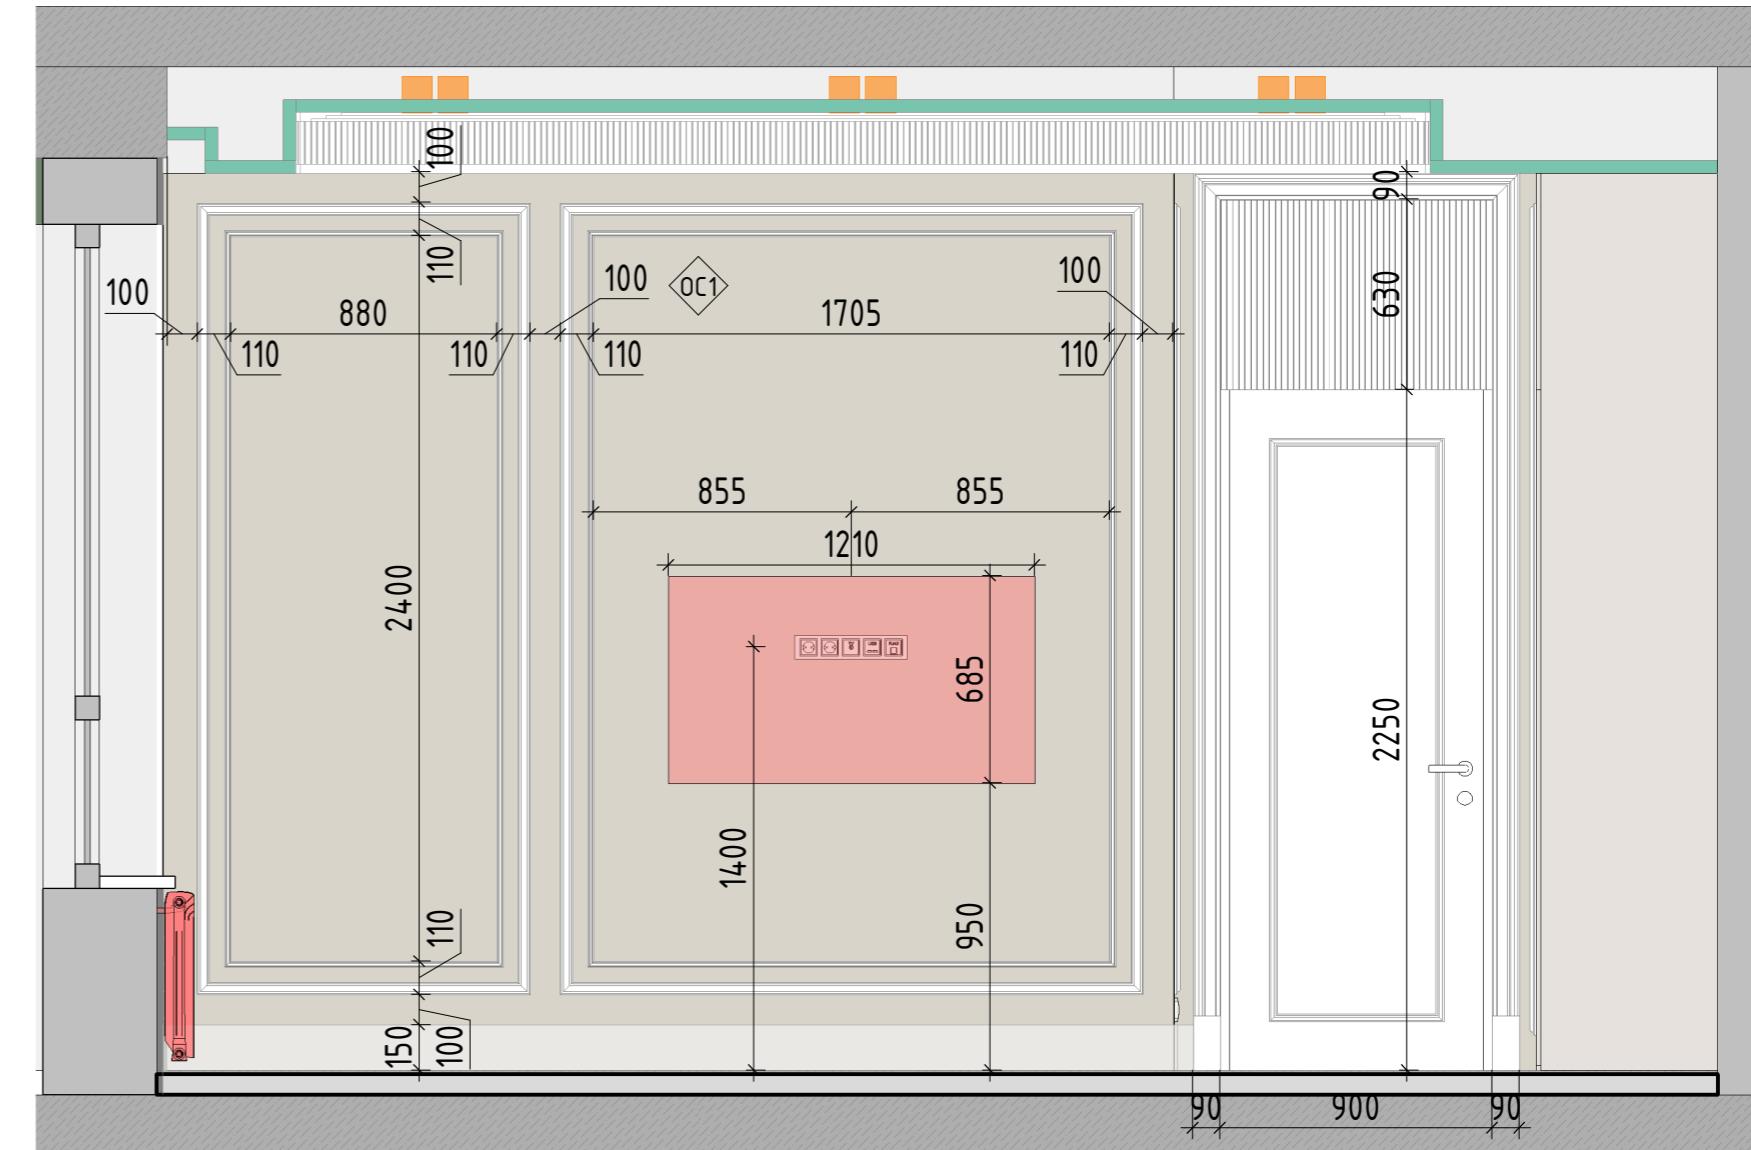

Дизайнер			
Заказчик			


РОДИТЕЛЬСКАЯ СПАЛЬНЯ.
РАЗВЕРТКА СТЕН

Luxhouse_studio


Формат: А3

Стадия	Лист	Листов
АИ		

Вид-4

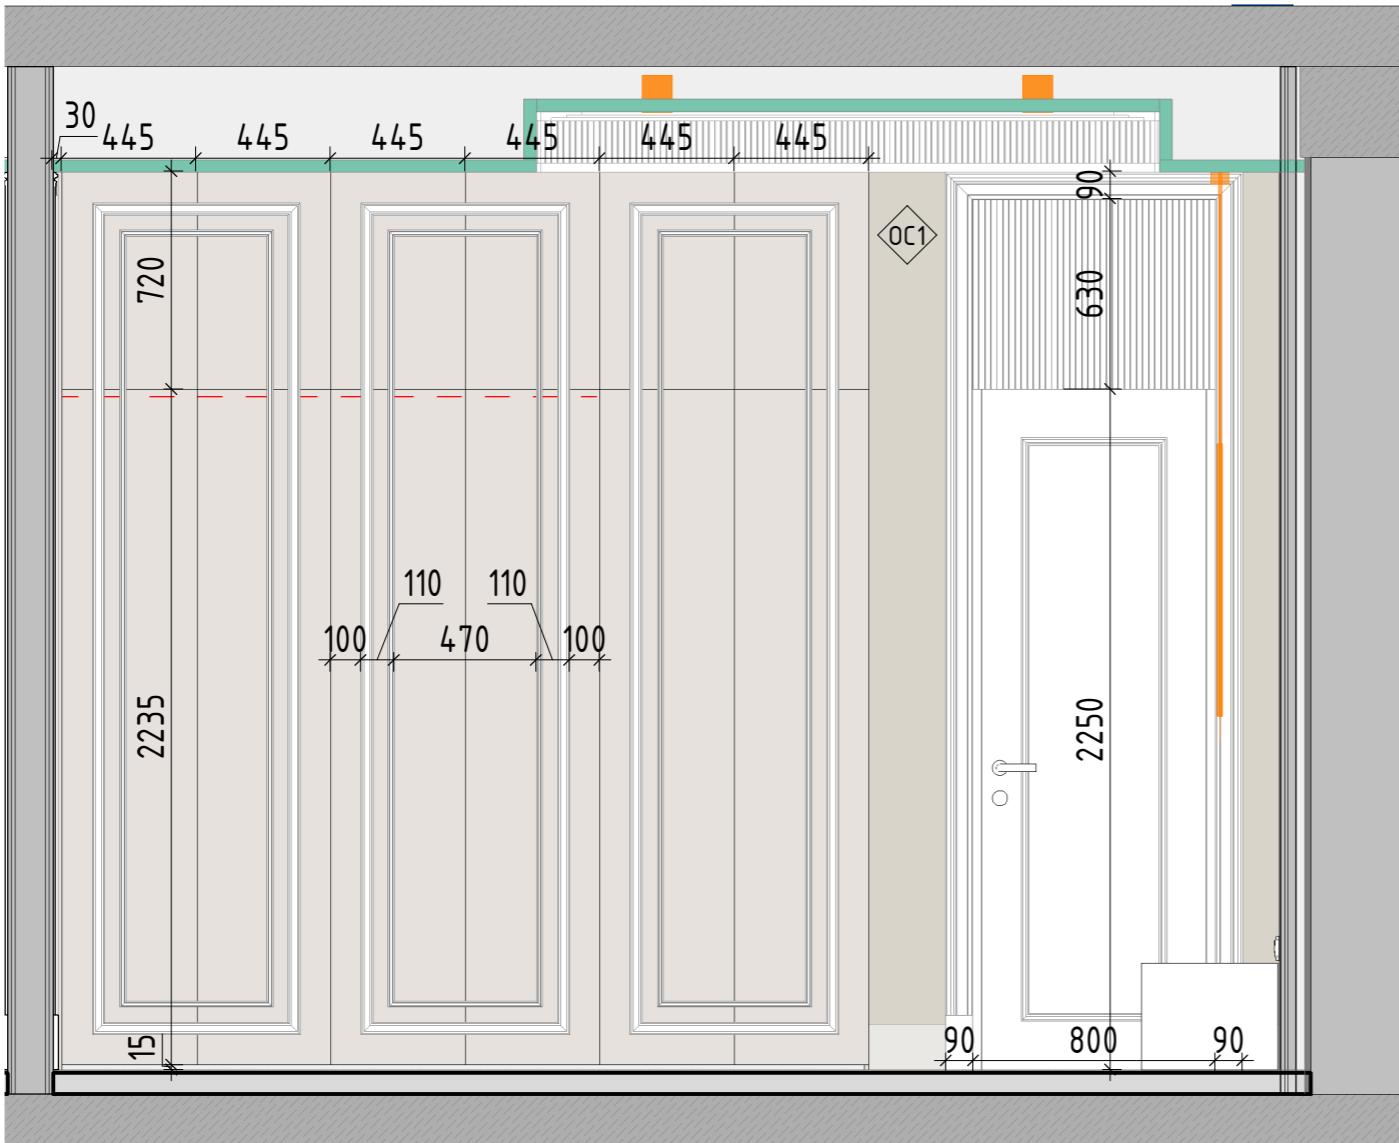

Выход кабеля

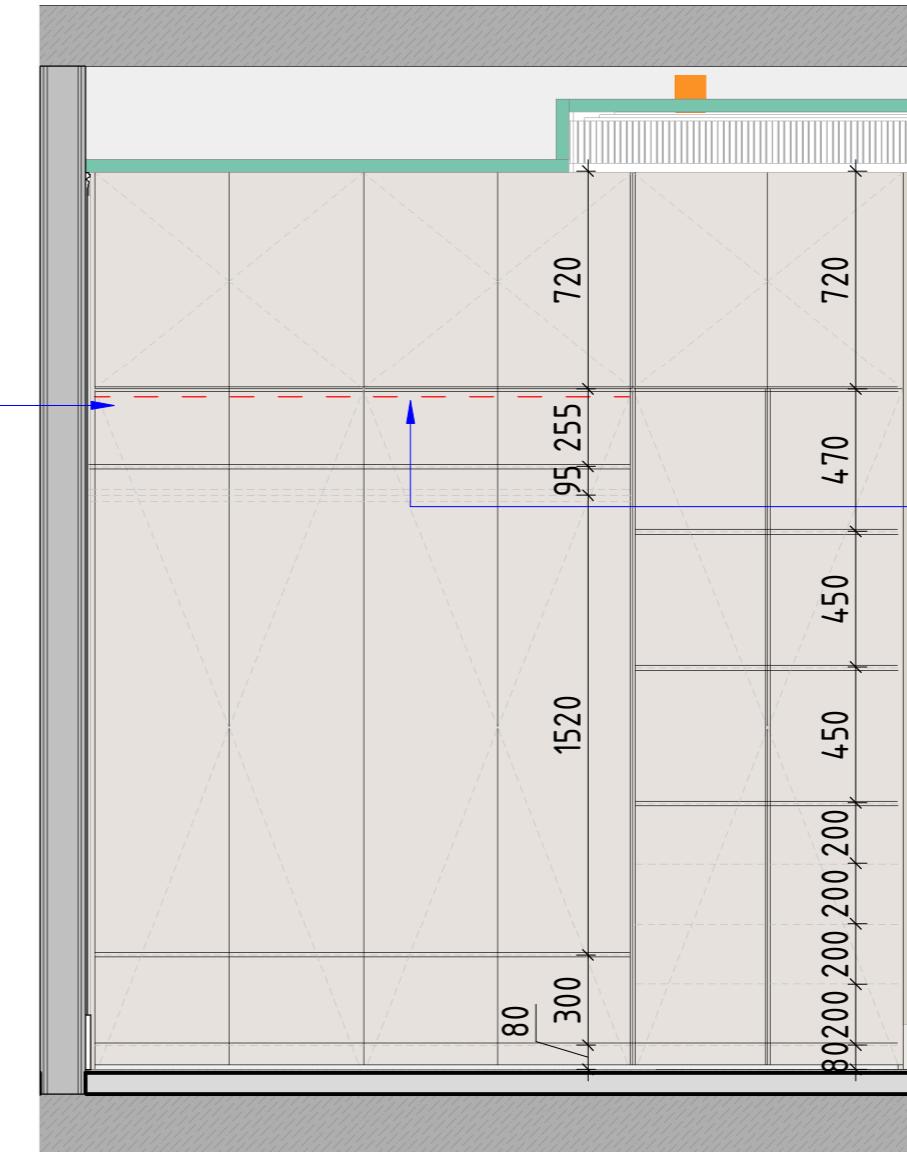

В шкафу
предусмотреть
подсветку с
механическим
мебельным
выключателем

Примечание:

- | | | | |
|-------|---|--------|---|
| (OC) | -Штукатурка | (OC6) | -Белый керамогранит 1200x600, Vitra |
| (OC1) | -Tikkurila_Y487 Пицца | (OC7) | -Плитка 3000x1000 VERDERAME LUX |
| (OC2) | -Tikkurila_X487 Laasti_Раствор | (OC8) | -ARVEN RECTIFIED PARLAK NANO 60X120 OT KUTAHYA |
| (OC3) | -Tikkurila_X445 Lido_Лидо | (OC9) | -55012910RL 60x120 ATLANTIS БЕЛЫЙ ЛАПАТИРОВАННЫЙ |
| (OC4) | -Плитка 3000x1000 NOIR DESIR BOCCIARDATO | (OC10) | -Фартук на кухне |
| (OC5) | -Плитка 3000x1000 BIANCO LASA BOCCIARDATO | | -Двери/Гардеробные шкафы/Плинтусы Цвет - Tikkurila_G497 Ноугу_Пар |


Примечания:

- За отметку 0.000 принята отметка чистого пола квартиры.
- Все размеры уточняются по месту.
- Наличник дверей со стороны санузлов на 100 мм ниже чем в остальных помещениях


Стадия	Лист	Листов
AI		

РОДИТЕЛЬСКАЯ СПАЛЬНЯ.
РАЗВЕРТКА СТЕН

Вид-1

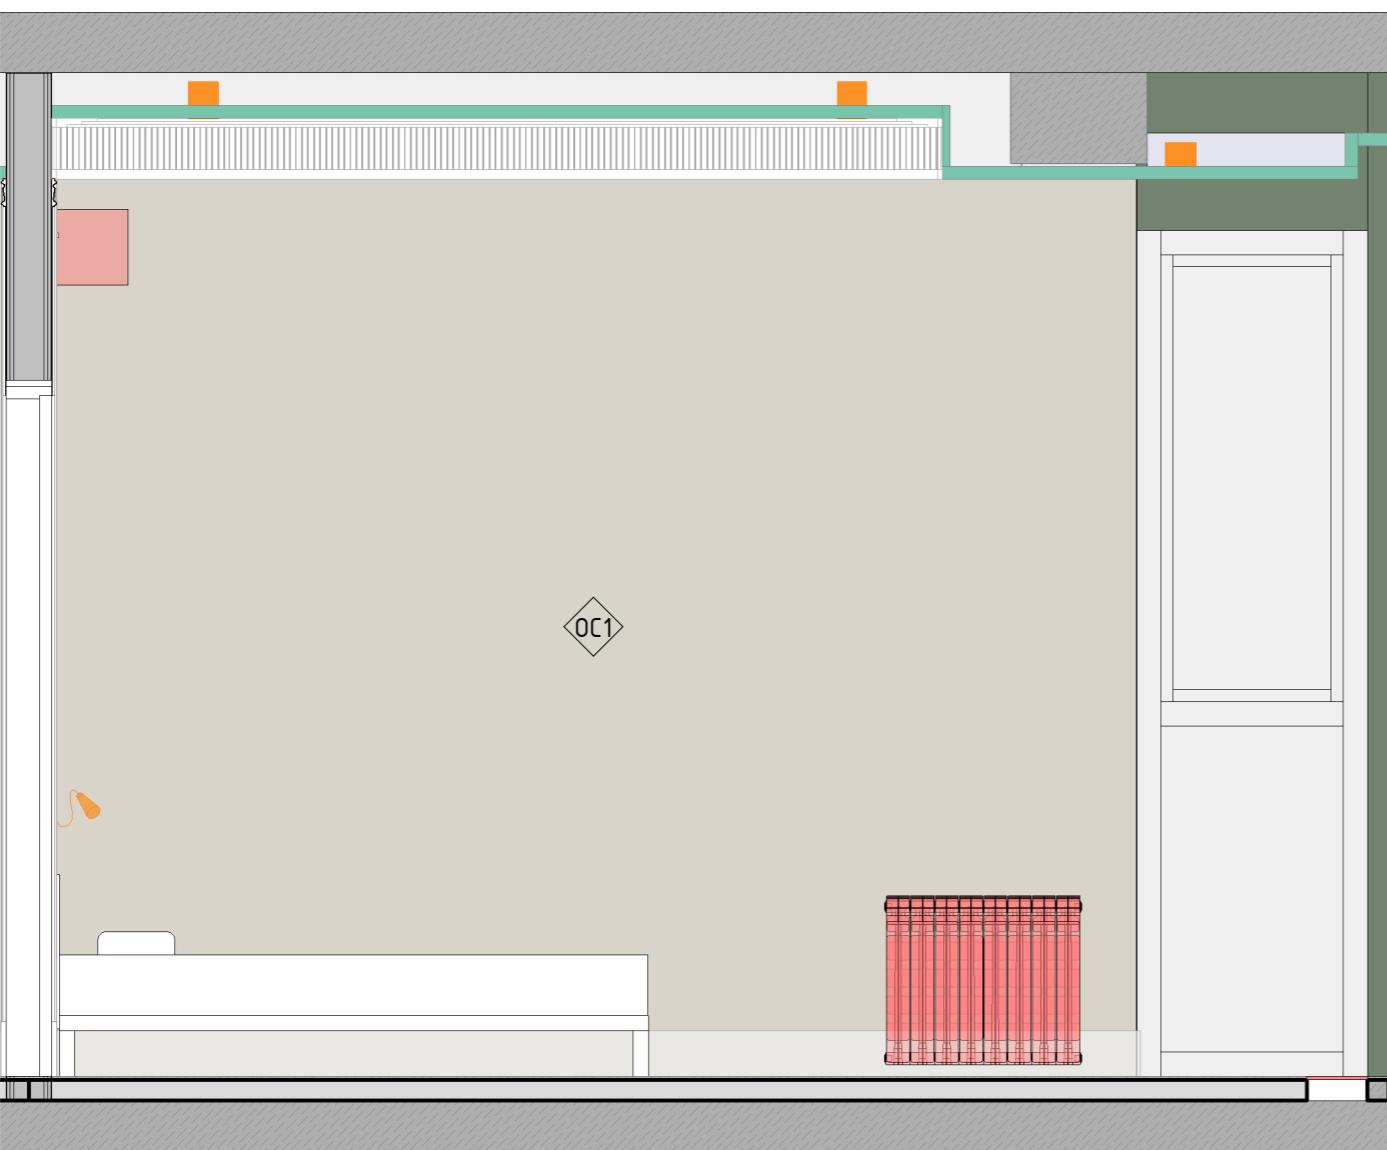


Вид-2

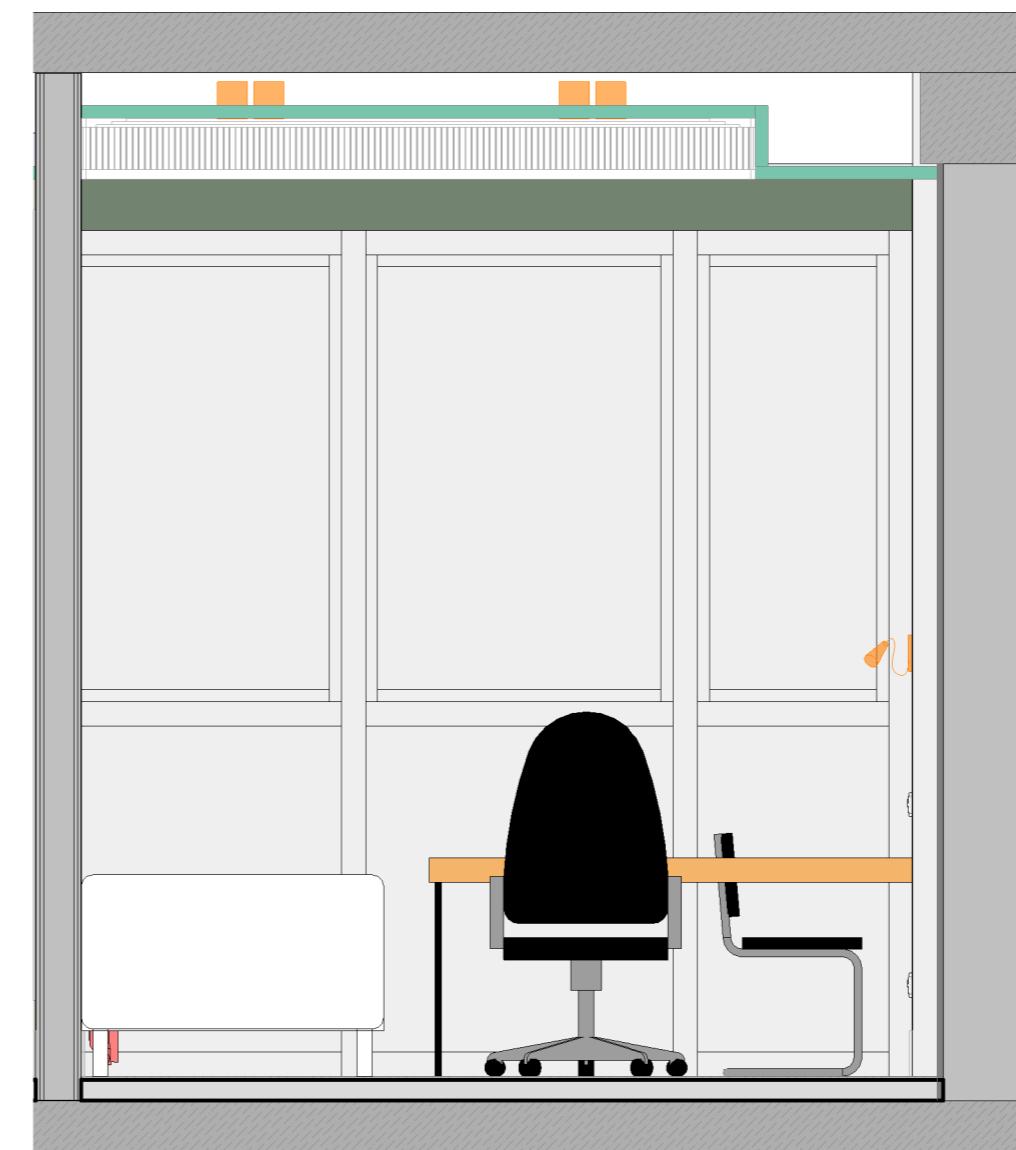

Примечание:

- (OC) -Штукатурка
- (OC1) -Tikkurila_Y487 Пицца
- (OC2) -Tikkurila_X487 Laasti_Раствор
- (OC3) -Tikkurila_X445 Lido_Лидо
- (OC4) -Плитка 3000x1000 NOIR DESIR BOCCIARDATO
- (OC5) -Плитка 3000x1000 BIANCO LASA BOCCIARDATO
- (OC6) -Белый керамогранит 1200x600, Vitra
- (OC7) -Плитка 3000x1000 VERDERAME LUX
- (OC8) -ARVEN RECTIFIED PARLAK NANO 60X120 ОТ КУТАНЬЯ
- (OC9) -55012910RL 60x120 ATLANTIS БЕЛЫЙ ЛАПАТИРОВАННЫЙ
- (OC10) -Фартук на кухне
- Двери/Гардеробные шкафы/Плинтусы Цвет - Tikkurila_G497 Ноугу_Пар

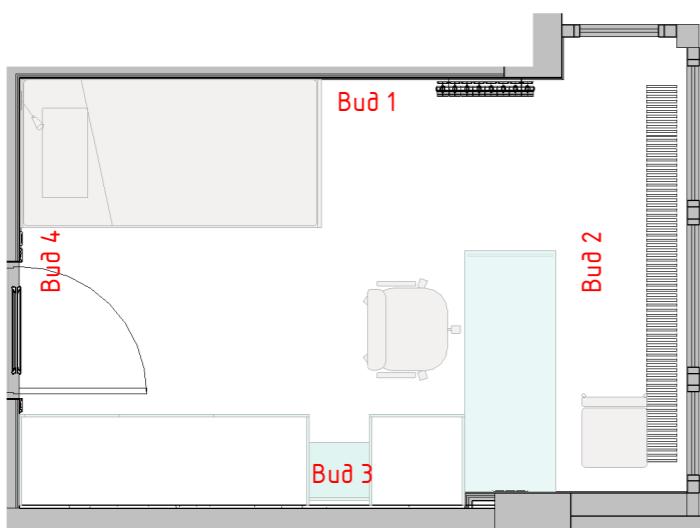

Примечания:



1. За отметку 0.000 принята отметка чистого пола квартиры.
2. Все размеры уточняются по месту.
3. Наличник дверей со стороны санузлов на 100 мм ниже чем в остальных помещениях

Дизайнер			
Заказчик			

ДЕТСКАЯ СПАЛЬНЯ.
РАЗВЕРТКА СТЕН

Luxhouse_studio

Вид-3

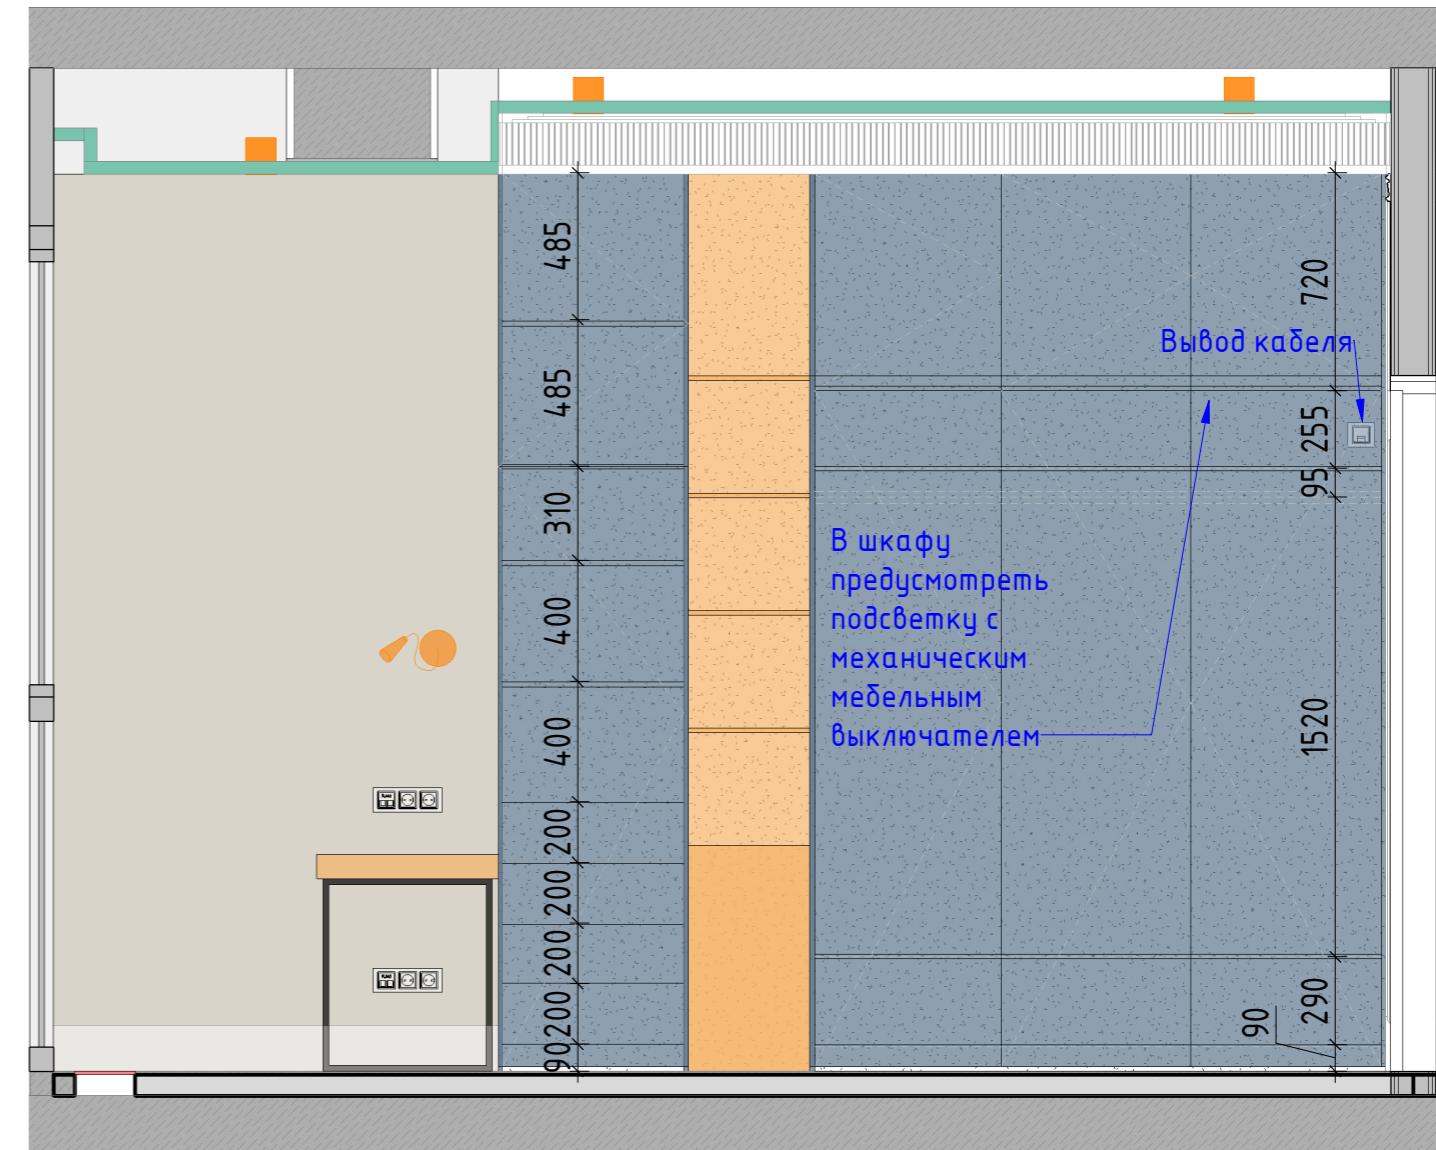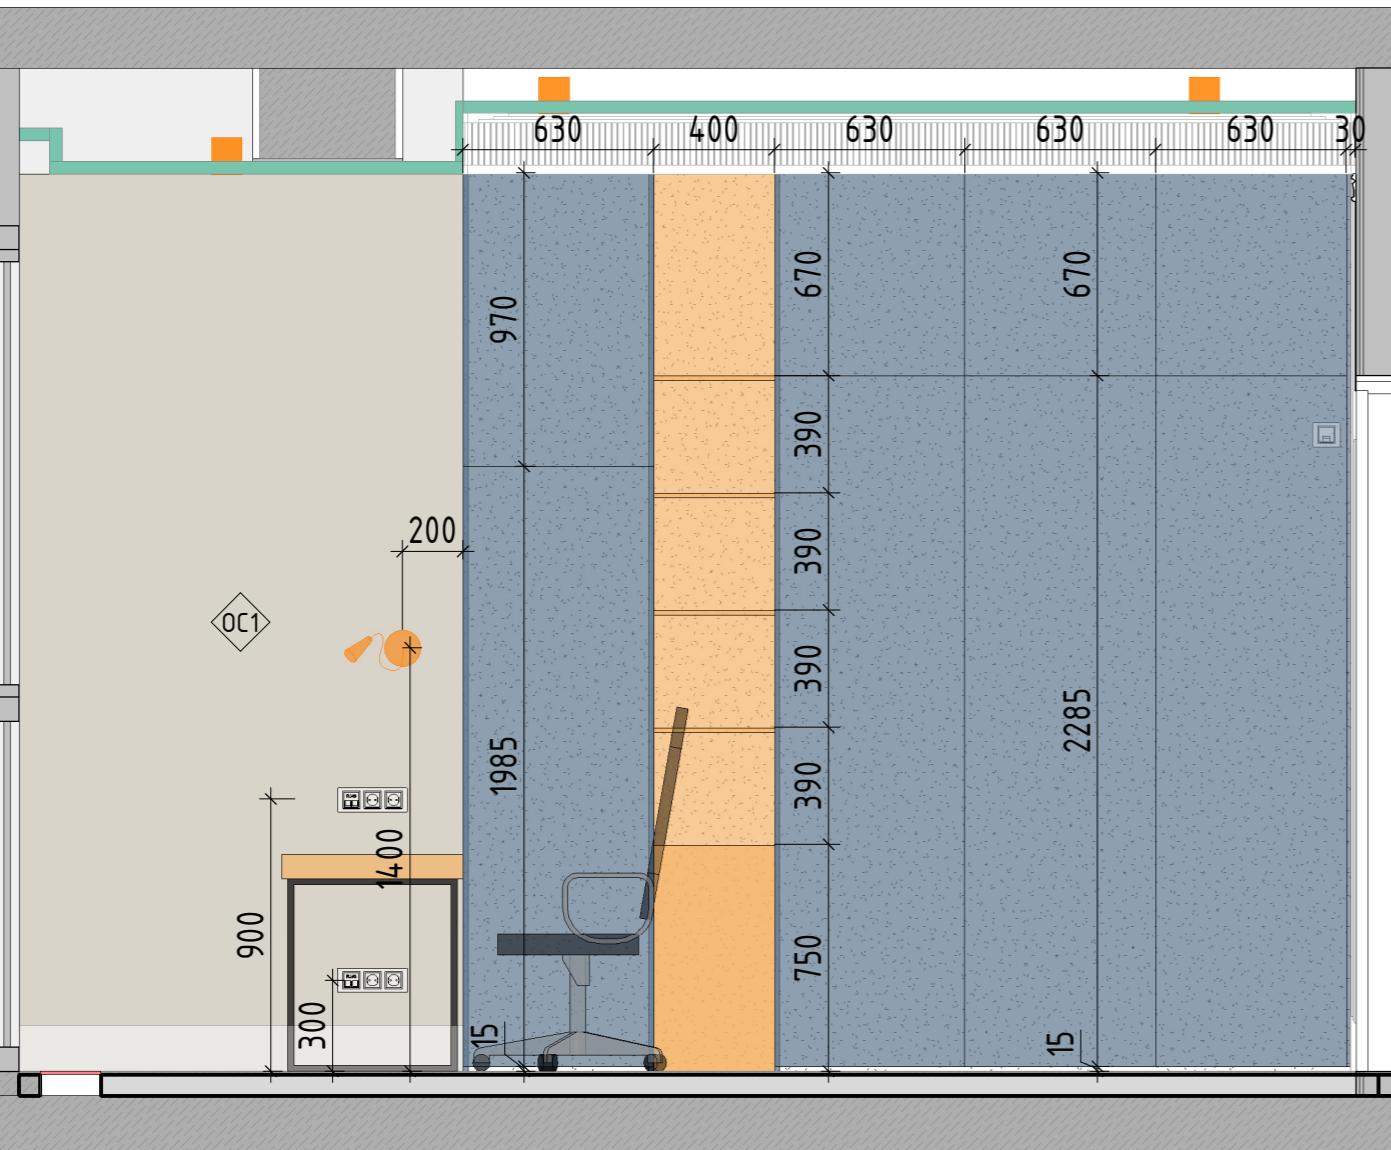



Примечание:

- | | | | |
|-------|---|--------|---|
| (OC) | -Штукатурка | (OC6) | -Белый керамогранит 1200x600, Vitra |
| (OC1) | -Tikkurila_Y487 Пиацца | (OC7) | -Плитка 3000x1000 VERDERAME LUX |
| (OC2) | -Tikkurila_X487 Laasti_Расмбор | (OC8) | -ARVEN RECTIFIED PARLAK NANO 60X120 OT KUTAHYA |
| (OC3) | -Tikkurila_X445 Lido_Лидо | (OC9) | -55012910RL 60x120 ATLANTIS БЕЛЫЙ ЛАПАТИРОВАННЫЙ |
| (OC4) | -Плитка 3000x1000 NOIR DESIR BOCCIARDATO | (OC10) | -Фартук на кухне |
| (OC5) | -Плитка 3000x1000 BIANCO LASA BOCCIARDATO | | -Двери/Гардеробные шкафы/Плинтусы Цвет - Tikkurila_G497 Нуруг_Пар |

Примечания:

- За отметку 0.000 принята отметка чистого пола квартиры.
- Все размеры уточняются по месту.
- Наличник дверей со стороны санузлов на 100 мм ниже чем в остальных помещениях

Дизайнер				Стадия	Лист	Листов	
				АИ			
Заказчик				ДЕТСКАЯ СПАЛЬНЯ. РАЗВЕРТКА СТЕН			
						Luxhouse_studio	

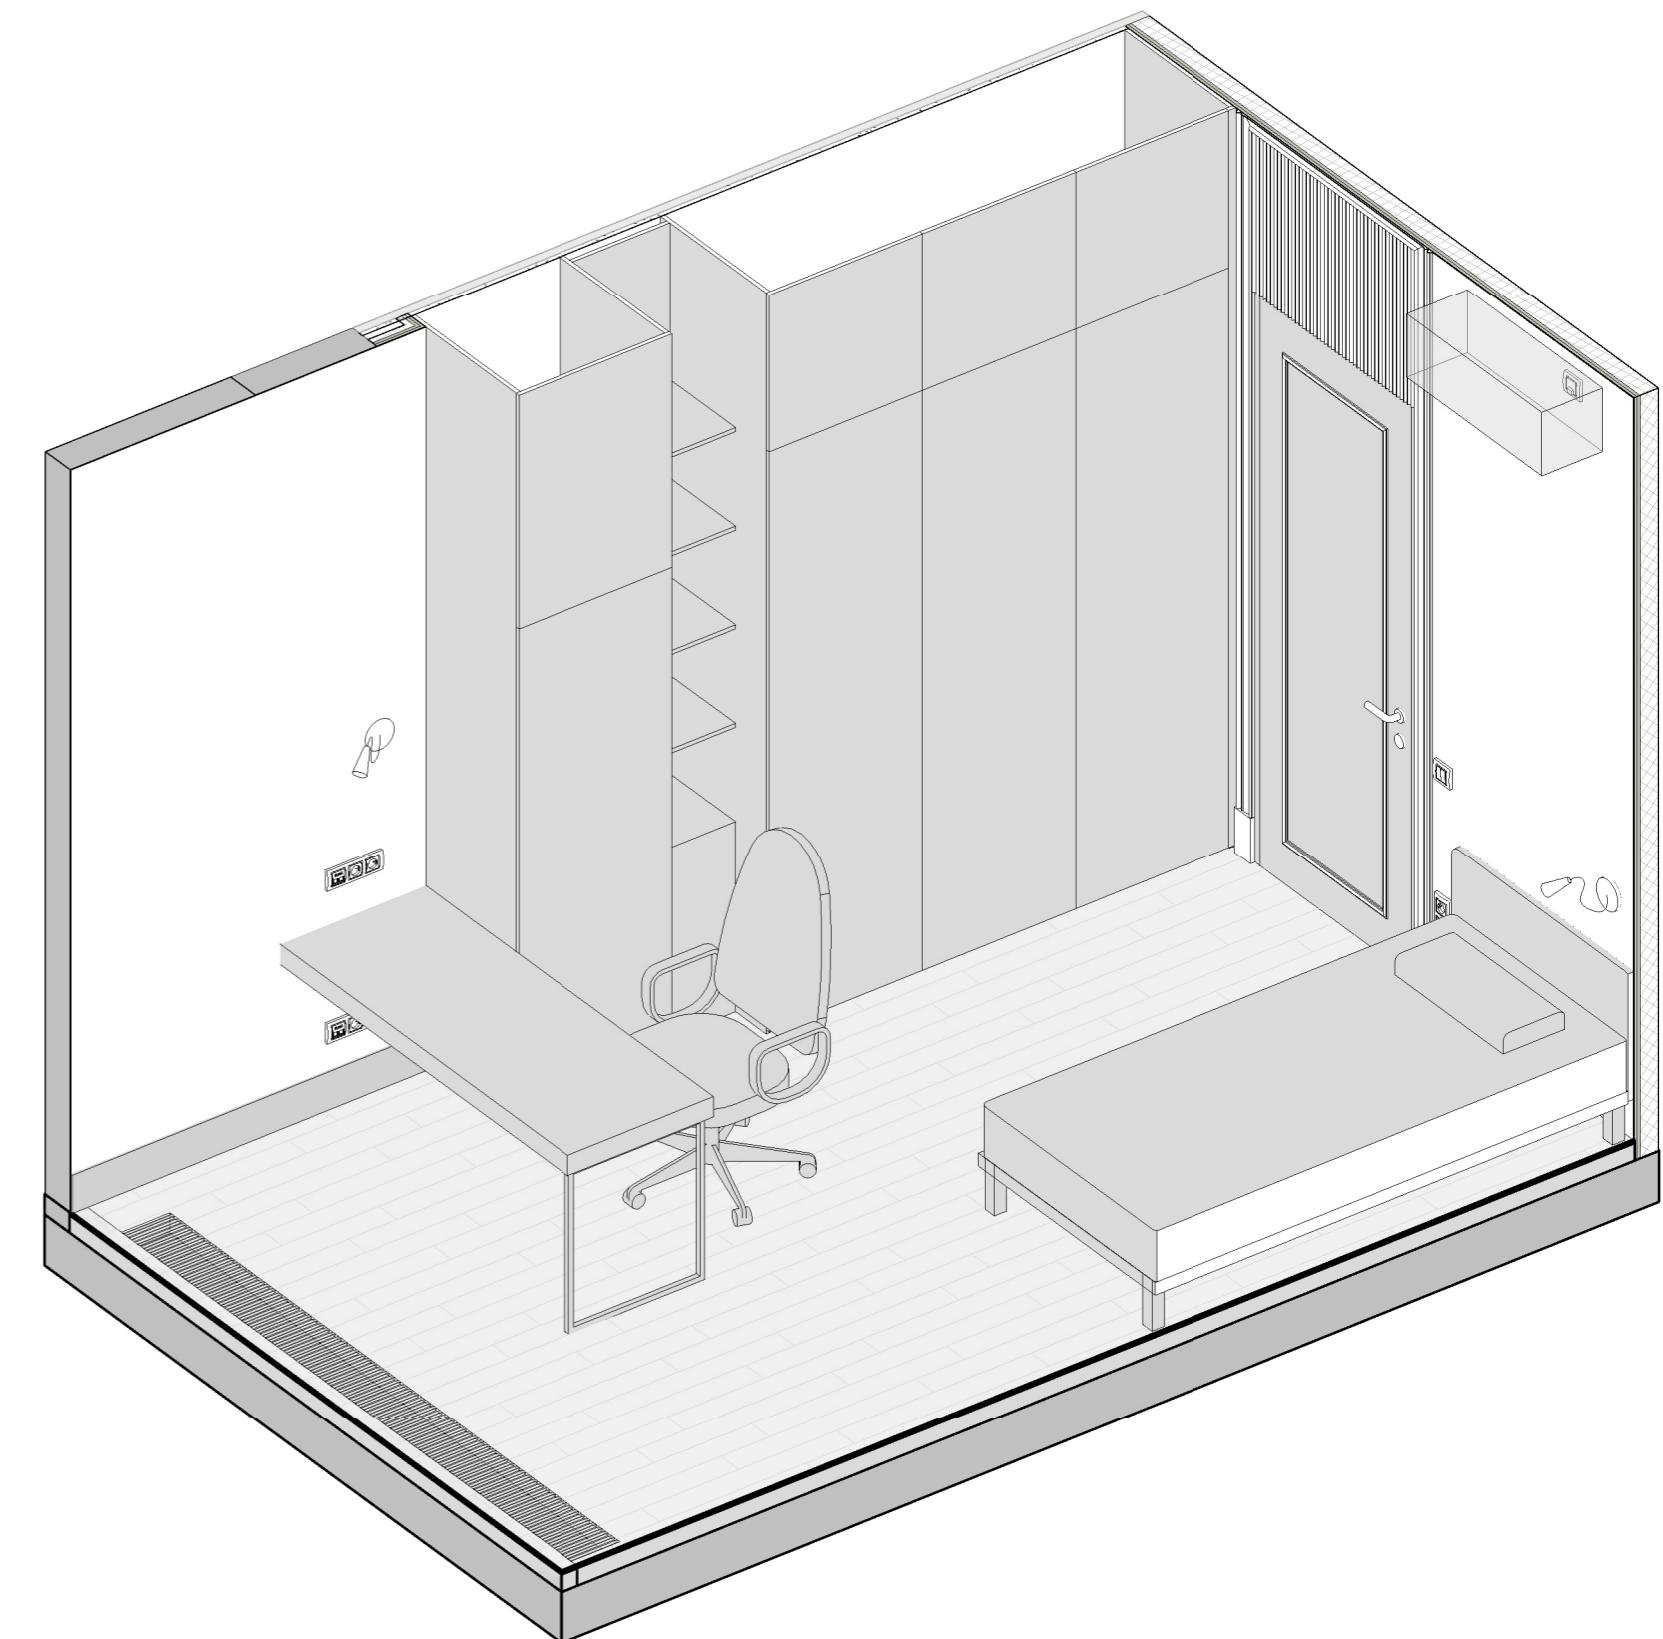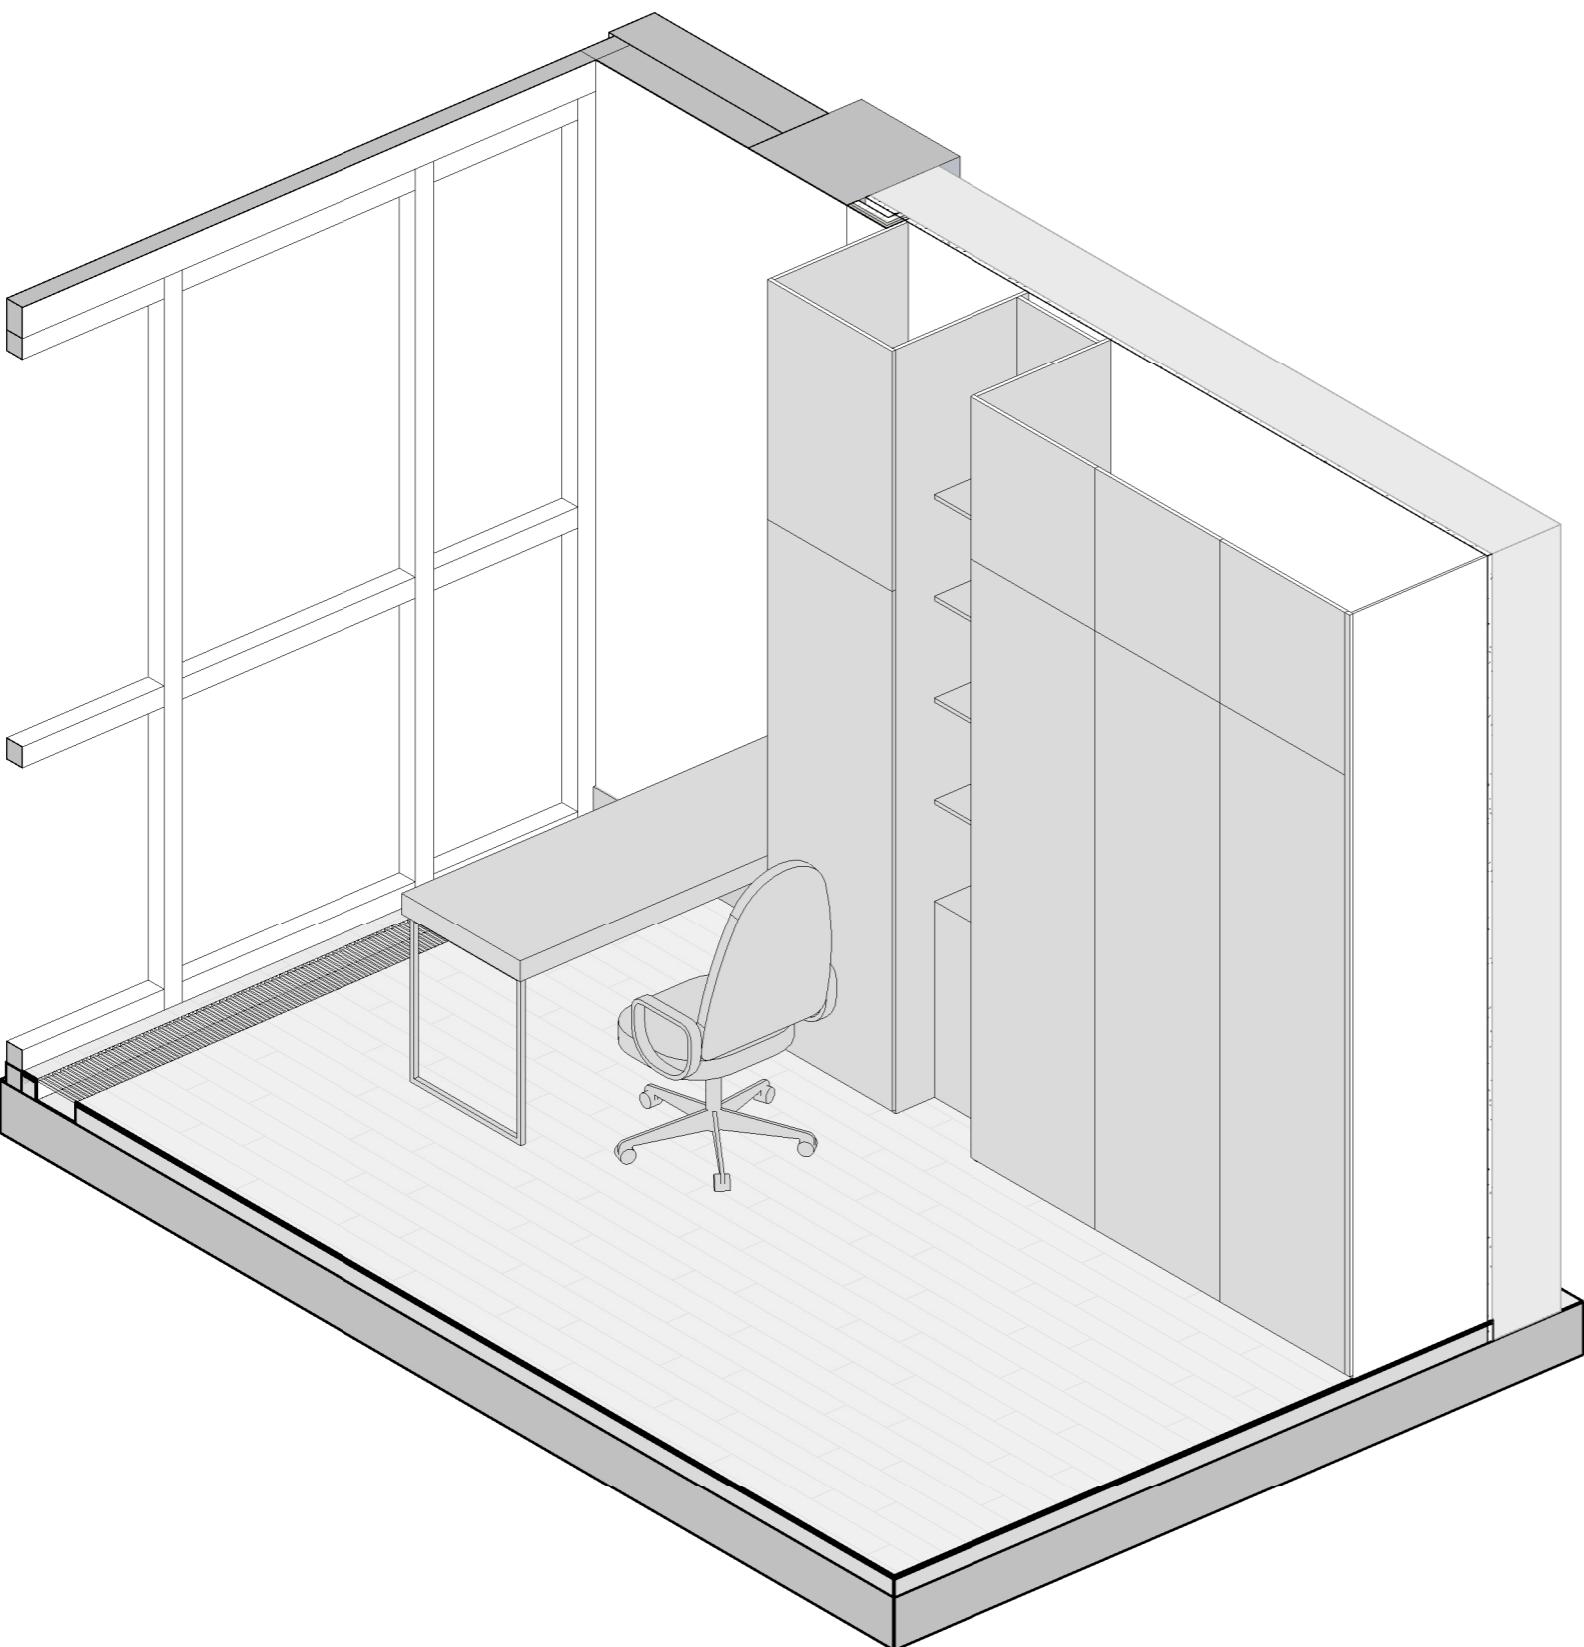

Дизайнер			
Заказчик			

СПАЛЬНЯ ЗД ВИД

Luxhouse_studio


Формат: А3




Формат: А3

Стадия	Лист	Листов
АИ		

Вид-1

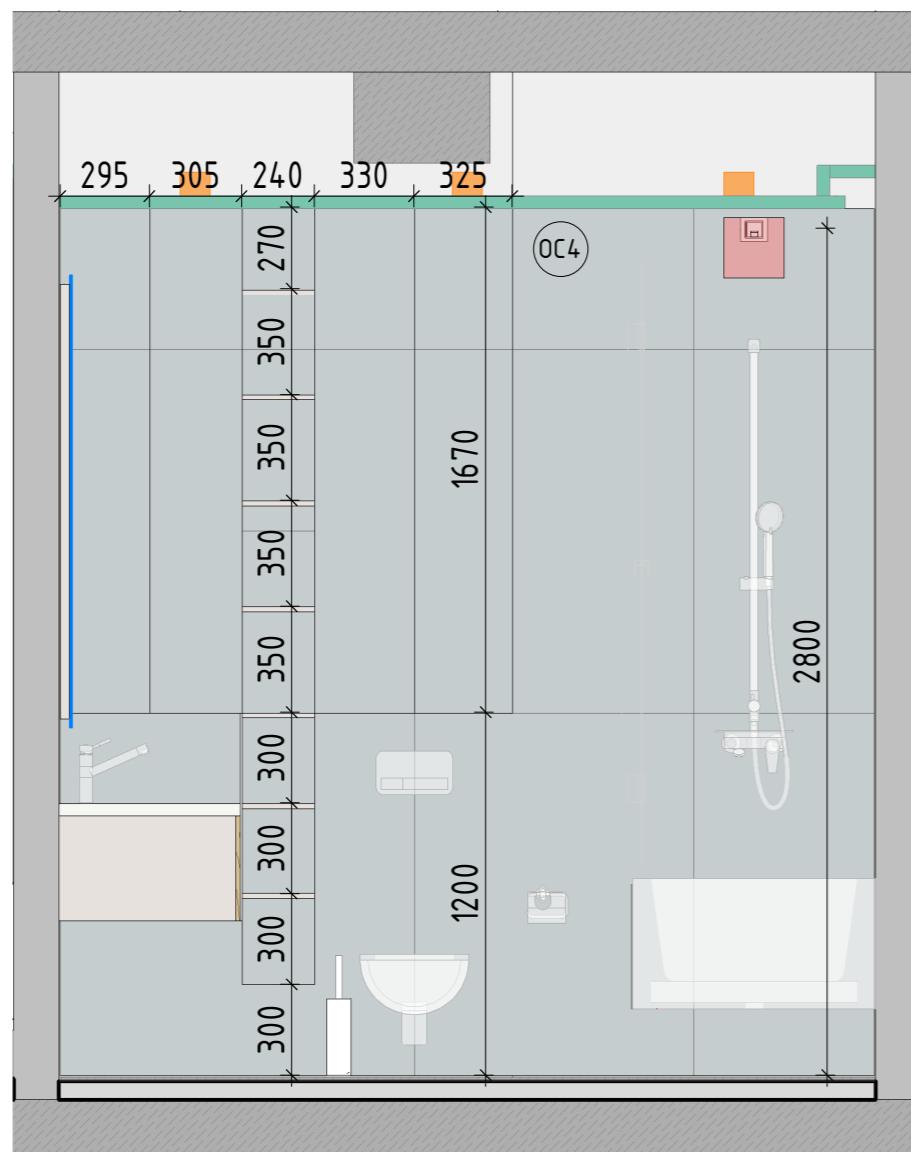


Вид-2

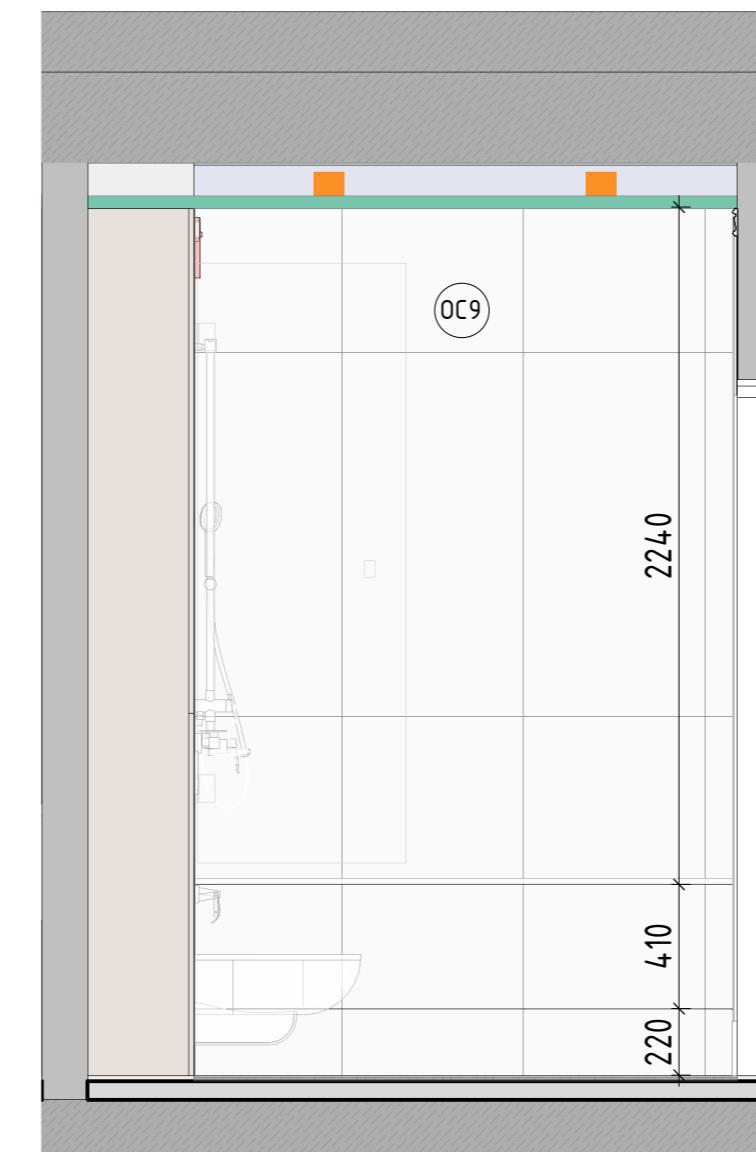

Примечание:

- OC -Штукатурка
- OC1 -Tikkurila_Y487 Пицца
- OC2 -Tikkurila_X487 Laasti_Расмбор
- OC3 -Tikkurila_X445 Lido_Лидо
- OC4 -Плитка 3000x1000 NOIR DESIR BOCCARDATO
- OC5 -Плитка 3000x1000 BIANCO LASA BOCCARDATO
- OC6 -Белый керамогранит 1200x600, Vitra
- OC7 -Плитка 3000x1000 VERDERAME LUX
- OC8 -ARVEN RECTIFIED PARLAK NANO 60x120 OT KUTAHYA
- OC9 -55012910RL 60x120 ATLANTIS БЕЛЫЙ ЛАПАТИРОВАННЫЙ
- OC10 -Фартук на кухне
- Двери/Гардеробные шкафы/Плинтусы Цвет - Tikkurila_G497 Ноугу_Пар

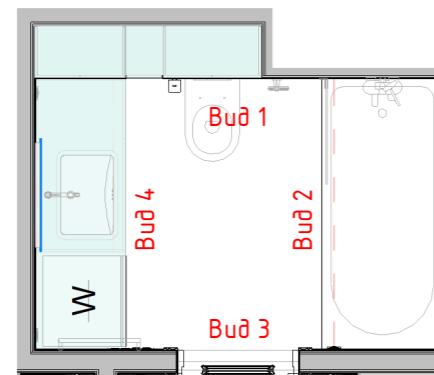


Примечания:

1. За отметку 0.000 принята отметка чистого пола квартиры.
2. Все размеры уточняются по месту.
3. Наличник дверей со стороны санузлов на 100 мм ниже чем в остальных помещениях



Дизайнер			
Заказчик			

ВАННАЯ КОМНАТА.
РАЗВЕРТКА СТЕН

Вид-3

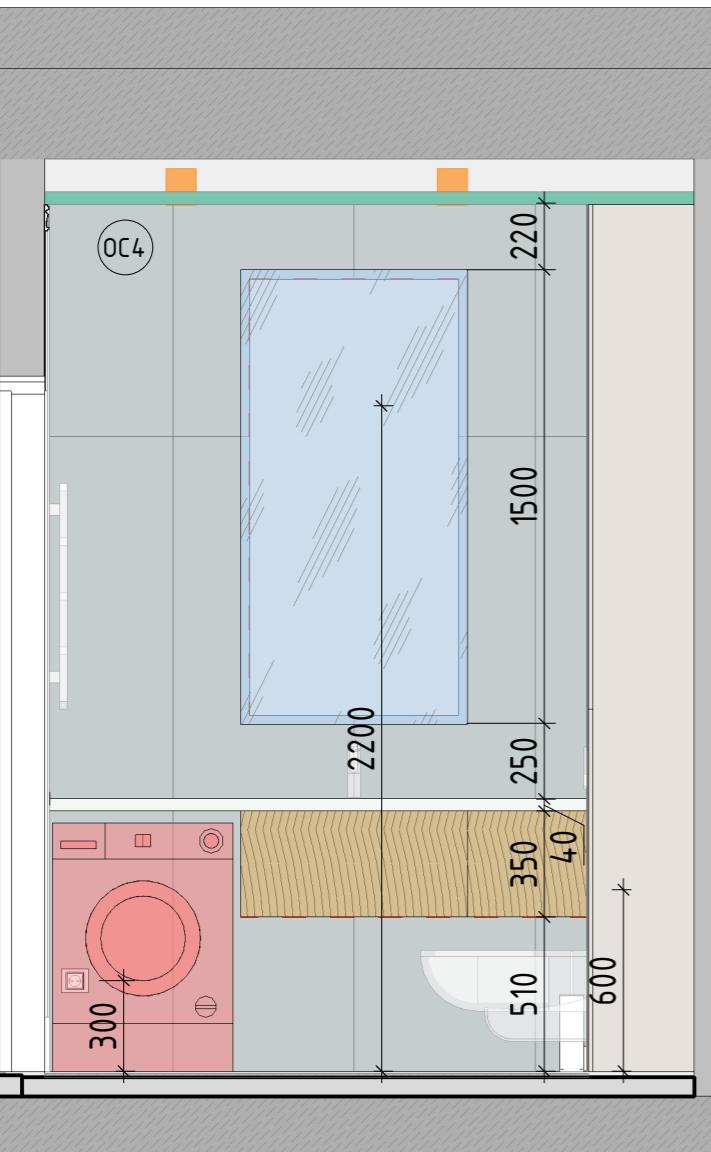

Вид-4

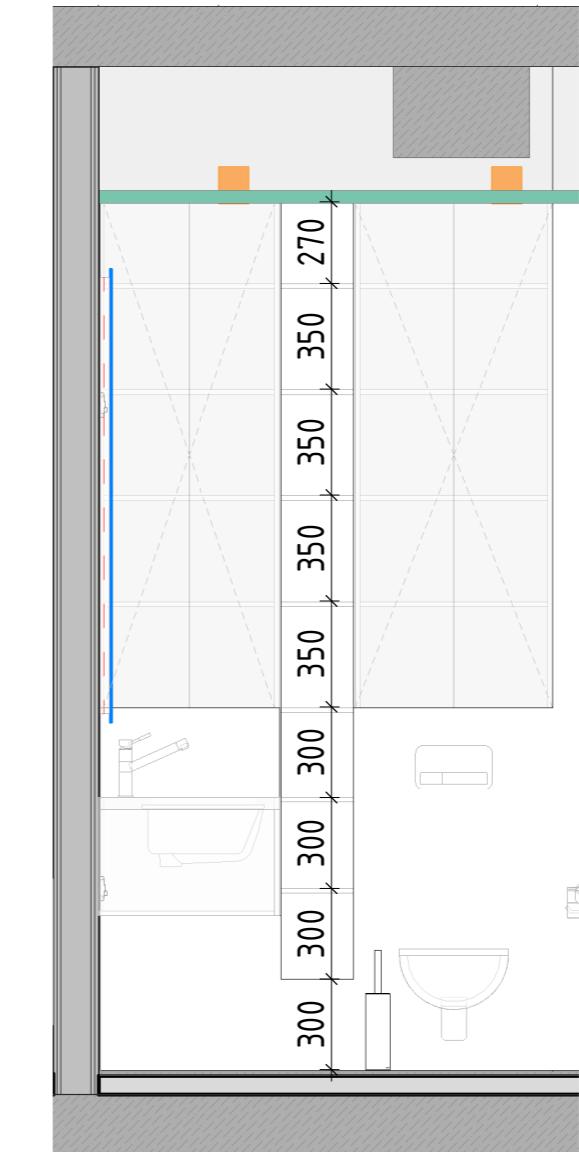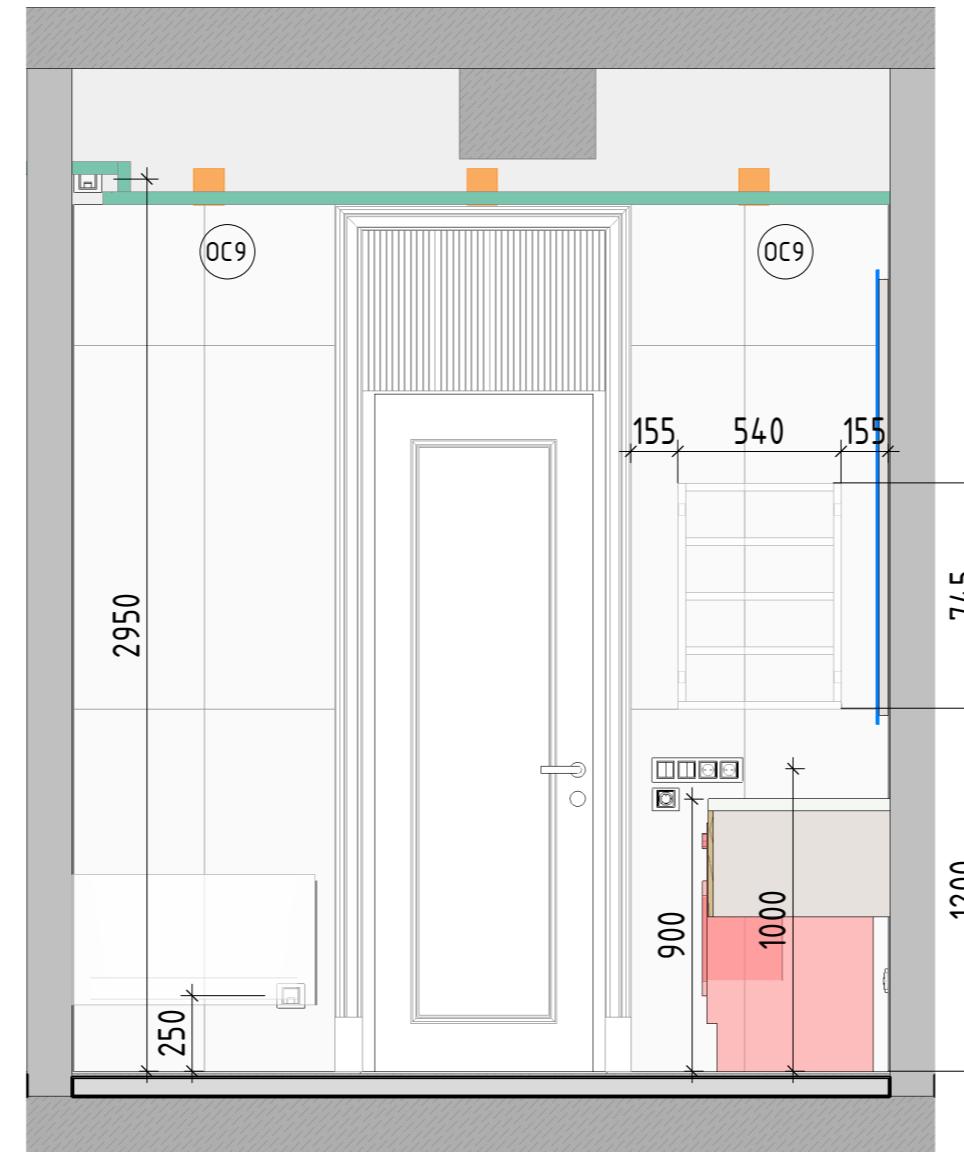

Примечание:

- (OC) - Штукатурка
- (OC1) - Tikkurila_Y487 Пиаца
- (OC2) - Tikkurila_X487 Laasti_Раствор
- (OC3) - Tikkurila_X445 Lido_Лидо
- (OC4) - Плитка 3000x1000 NOIR DESIR BOCCIARDATO
- (OC5) - Плитка 3000x1000 BIANCO LASA BOCCIARDATO
- (OC6) - Белый керамогранит 1200x600, Vitra
- (OC7) - Плитка 3000x1000 VERDERAME LUX
- (OC8) - ARVEN RECTIFIED PARLAK NANO 60X120 OT KUTAHYA
- (OC9) - 55012910RL 60x120 ATLANTIS БЕЛЫЙ ЛАПАТИРОВАННЫЙ
- (OC10) - Фартук на кухне
- Двери/Гардеробные шкафы/Плинтусы Цвет - Tikkurila_G497 Ноугу_Пар


Дизайнер			
Заказчик			

ВАННАЯ КОМНАТА.
РАЗВЕРТКА СТЕН


Стадия	Лист	Листов
АИ		

Luxhouse_studio

Вид-1

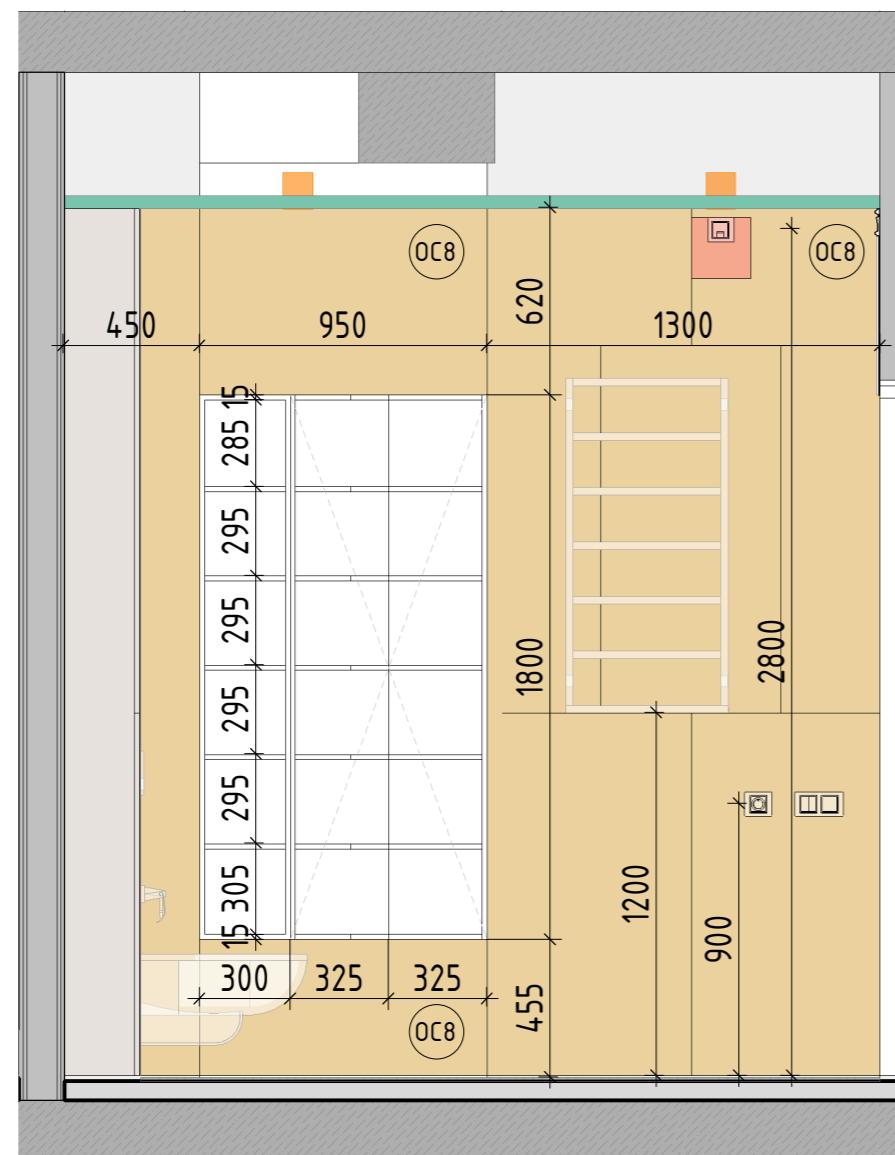


Вид-2

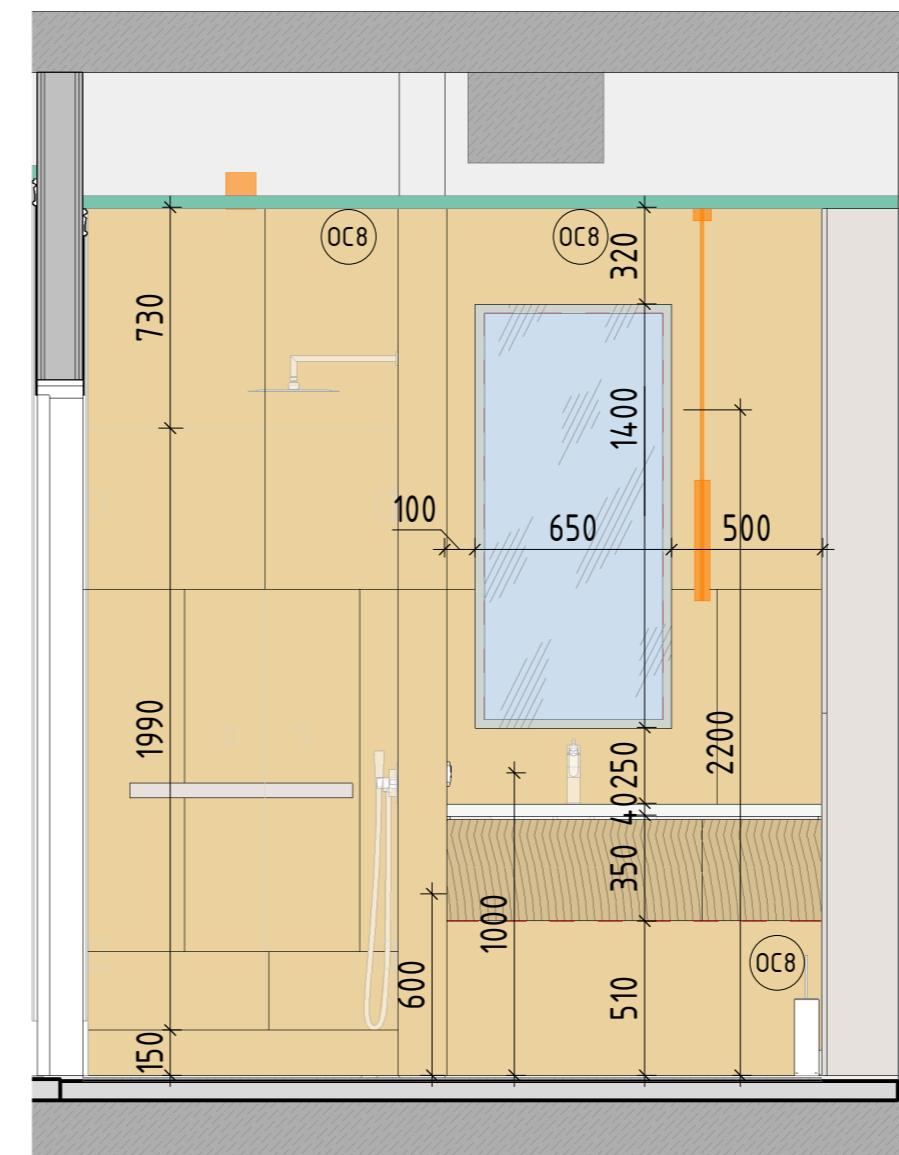

Примечание:

- (OC) -Штукатурка
- (OC1) -Tikkurila_Y487 Пиацца
- (OC2) -Tikkurila_X487 Laasti_Раствор
- (OC3) -Tikkurila_X445 Lido_Лидо
- (OC4) -Плитка 3000x1000 NOIR DESIR BOCCARDATO
- (OC5) -Плитка 3000x1000 BIANCO LASA BOCCARDATO
- (OC6) -Белый керамогранит 1200x600, Vitra
- (OC7) -Плитка 3000x1000 VERDERAME LUX
- (OC8) -ARVEN RECTIFIED PARLAK NANO 60x120 OT KUTAHYA
- (OC9) -55012910RL 60x120 ATLANTIS БЕЛЫЙ ЛАПАТИРОВАННЫЙ
- (OC10) -Фармук на кухне
- Двери/Гардеробные шкафы/Плинтусы Цвет - Tikkurila_G497 Ноуру_Пар

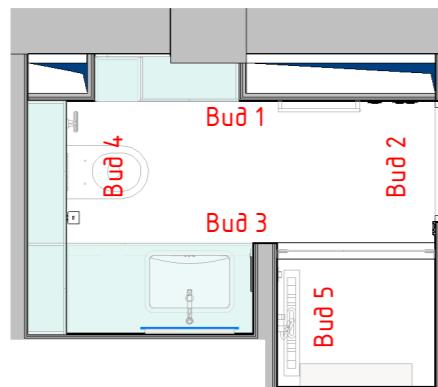


Примечания:

1. За отмечку 0.000 принята отмечка чистого пола квартир.
2. Все размеры уточняются по месту.
3. Наличник дверей со стороны санузлов на 100 мм ниже чем в остальных помещениях



Дизайнер			
Заказчик			

ВАННАЯ КОМНАТА.
РАЗВЕРТКА СТЕН

Вид-3

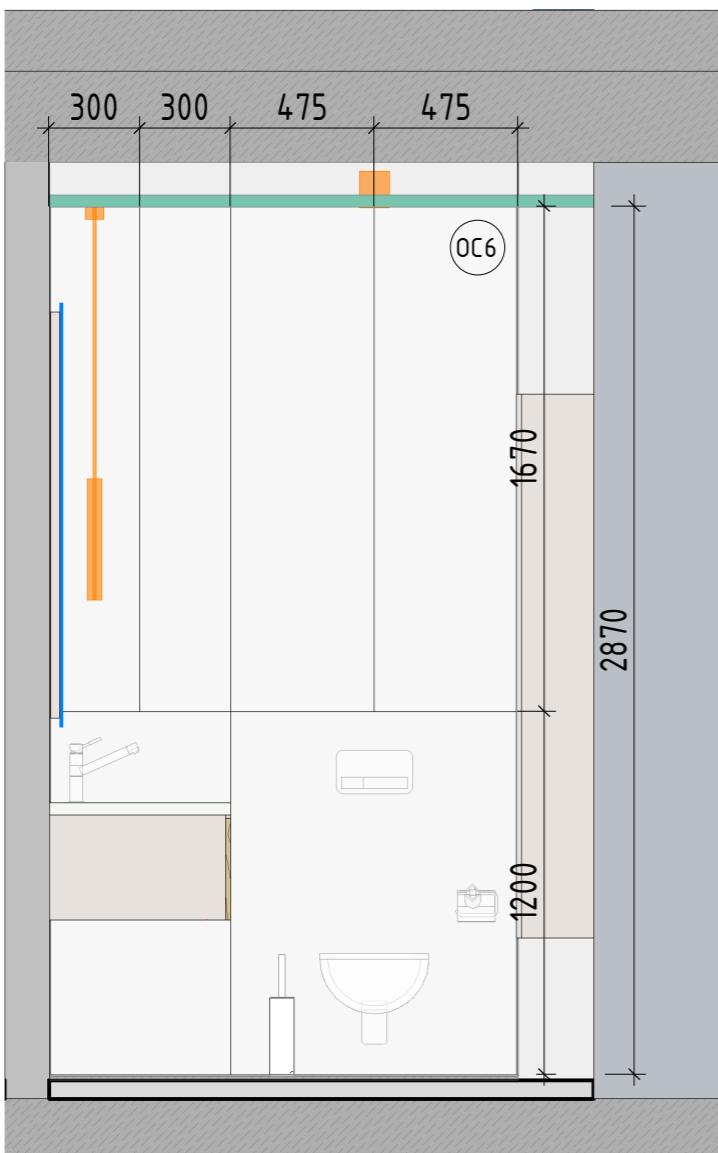

Вид-4

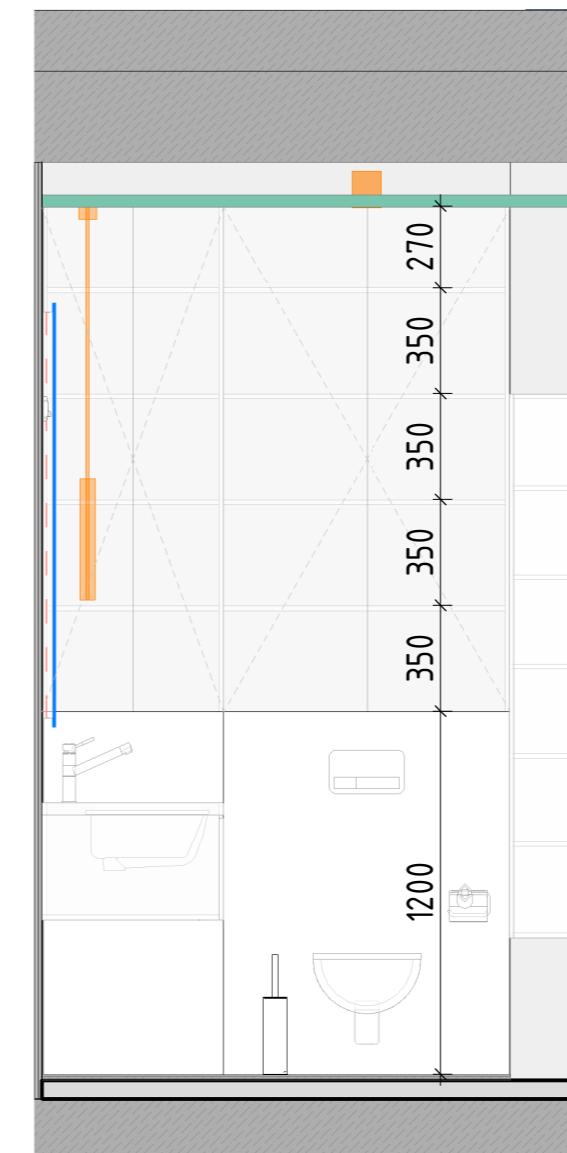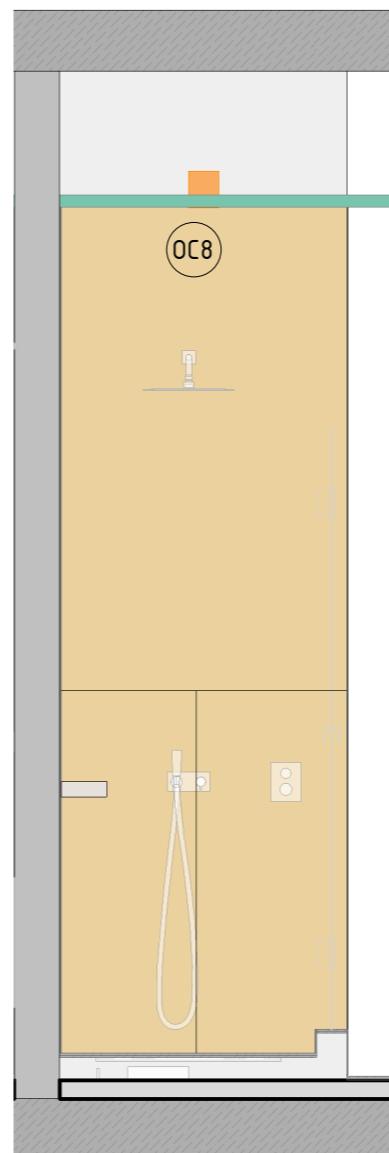


Примечание:


- OC -Штукатурка
- OC1 -Tikkurila_Y487 Пицца
- OC2 -Tikkurila_X487 Laasti_Расмбор
- OC3 -Tikkurila_X445 Lido_Лидо
- OC4 -Плитка 3000x1000 NOIR DESIR BOCCARDATO
- OC5 -Плитка 3000x1000 BIANCO LASA BOCCARDATO
- OC6 -Белый керамогранит 1200x600, Vitra
- OC7 -Плитка 3000x1000 VERDERAME LUX
- OC8 -ARVEN RECTIFIED PARLAK NANO 60X120 OT KUTAHYA
- OC9 -55012910RL 60x120 ATLANTIS БЕЛЫЙ ЛАПАТИРОВАННЫЙ
- OC10 -Фартук на кухне
- Двери/Гардеробные шкафы/Плинтусы Цвет - Tikkurila_G497 Ноугу_Пар

Стадия	Лист	Листов
АИ		
ВАННАЯ КОМНАТА. РАЗВЕРТКА СТЕН		Luxhouse_studio
		Формат: А3

Санузел 1

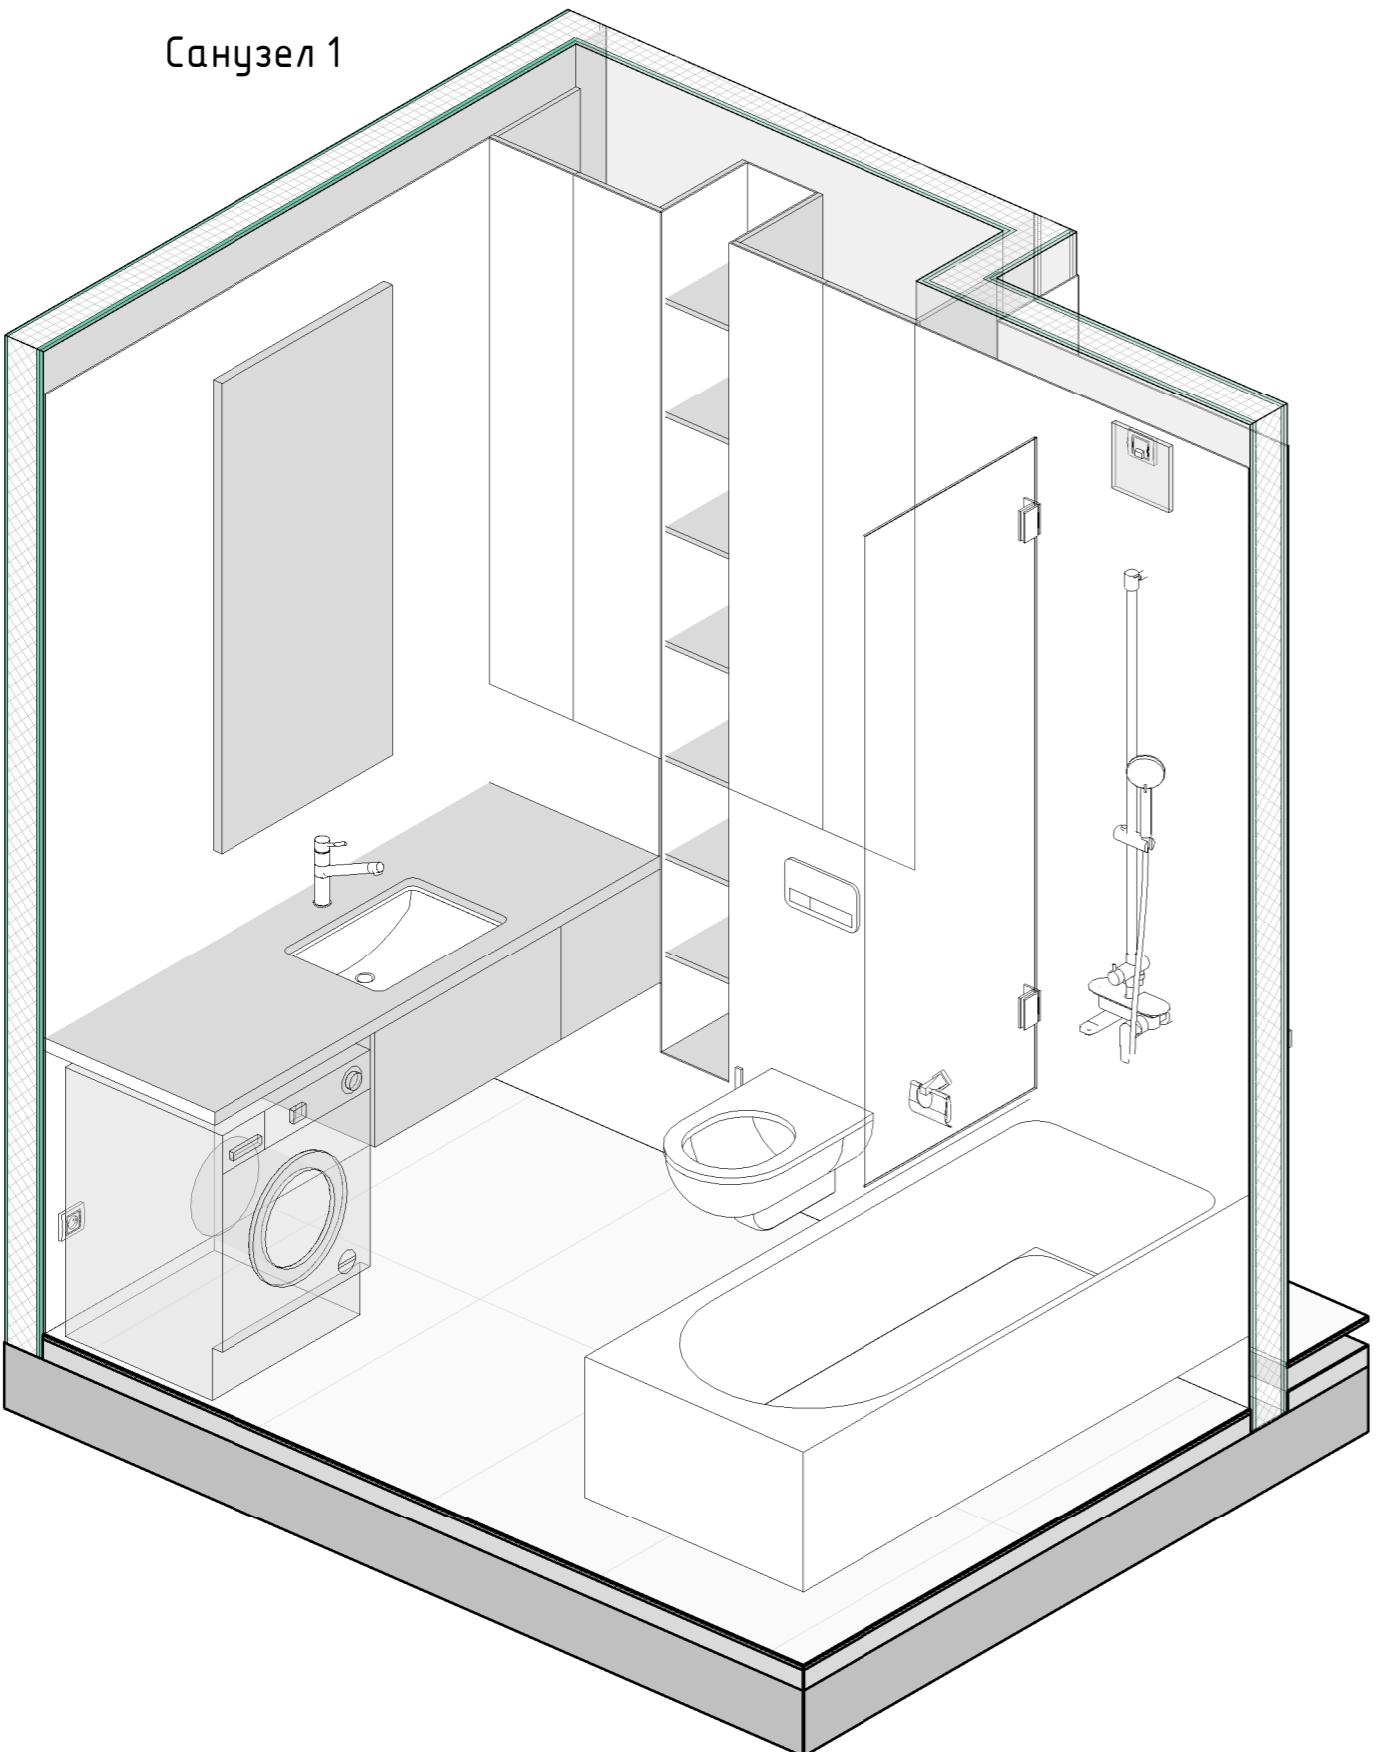

Санузел 2

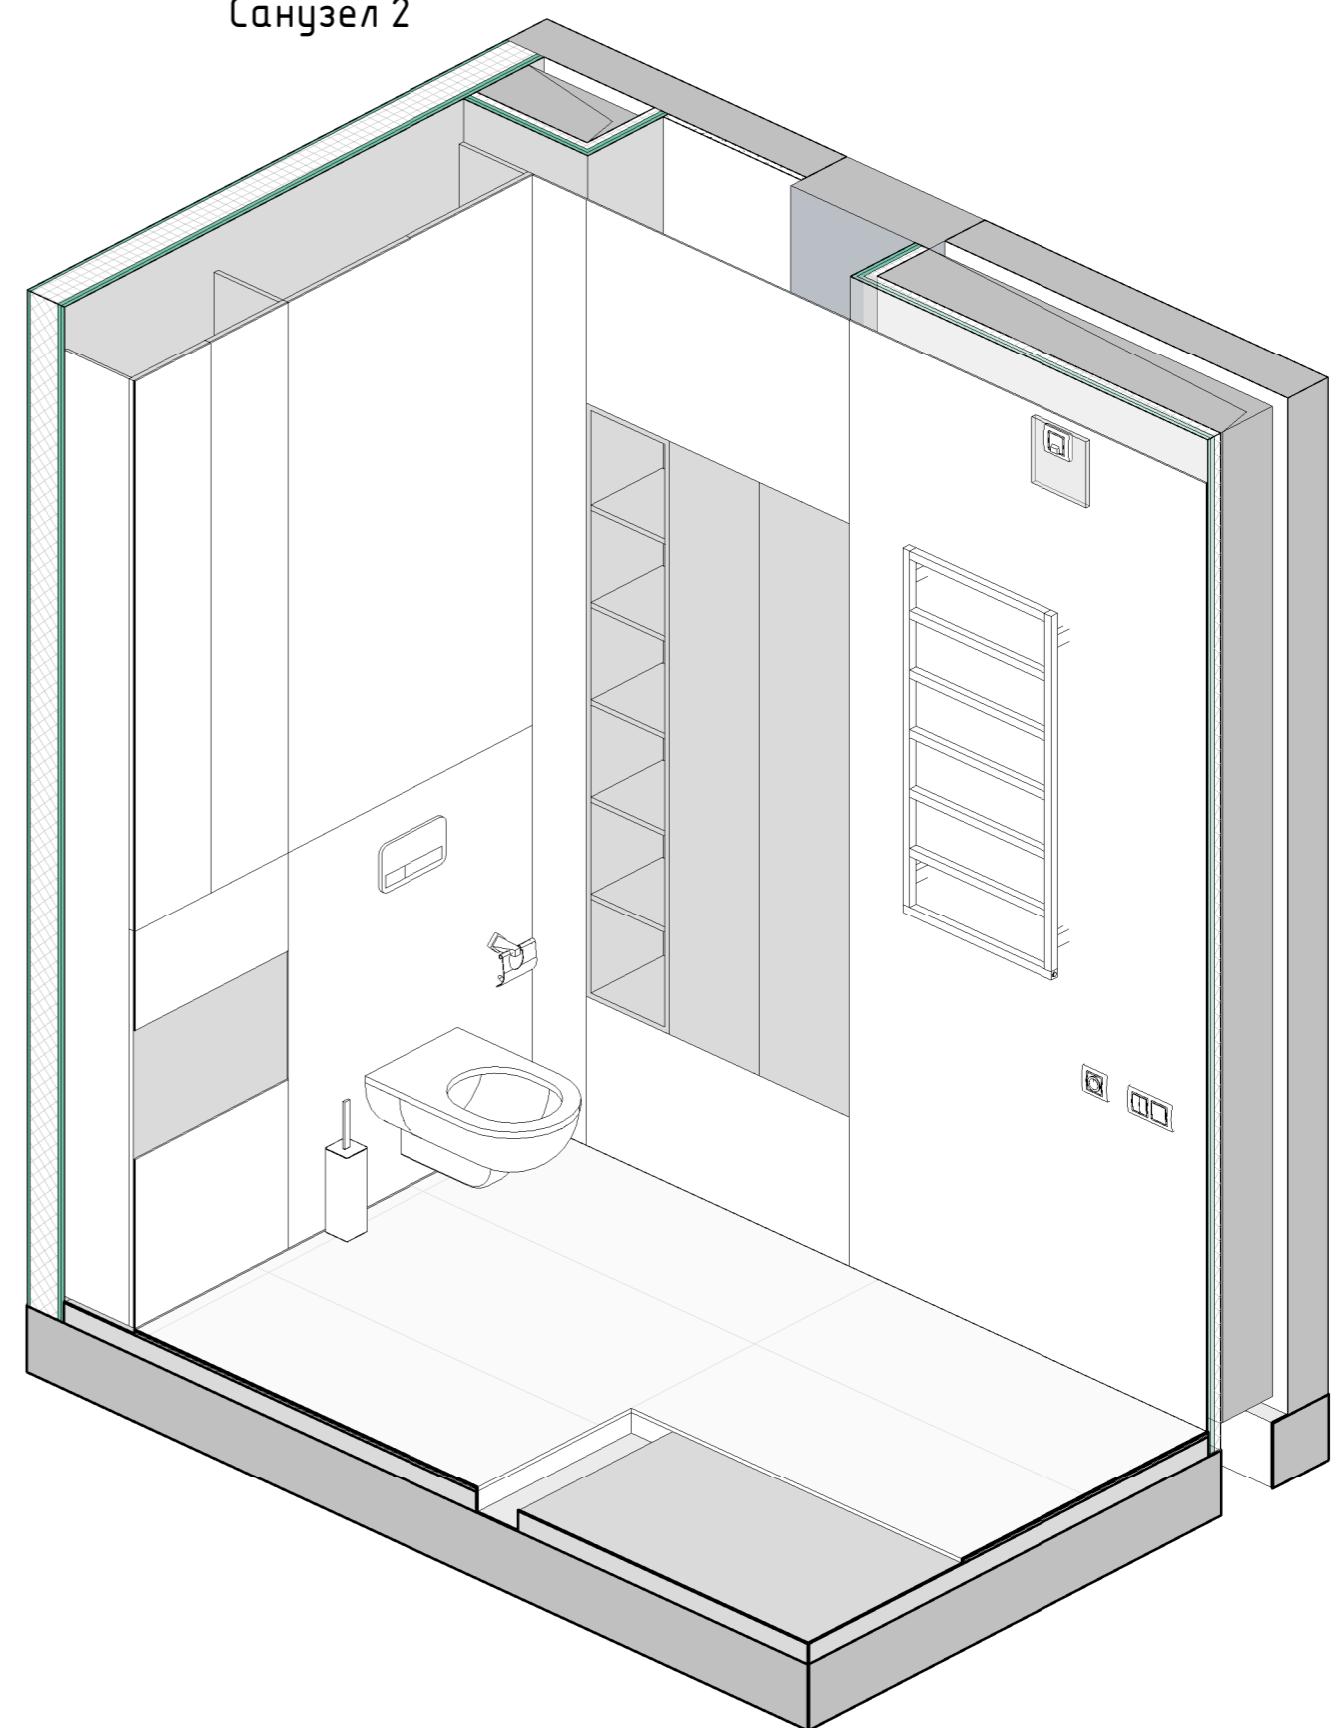


Дизайнер			
Заказчик			

САНУЗЕЛ 1-2, ЗД ВИДЫ


Стадия	Лист	Листов
АИ		

Luxhouse_studio


Д-1

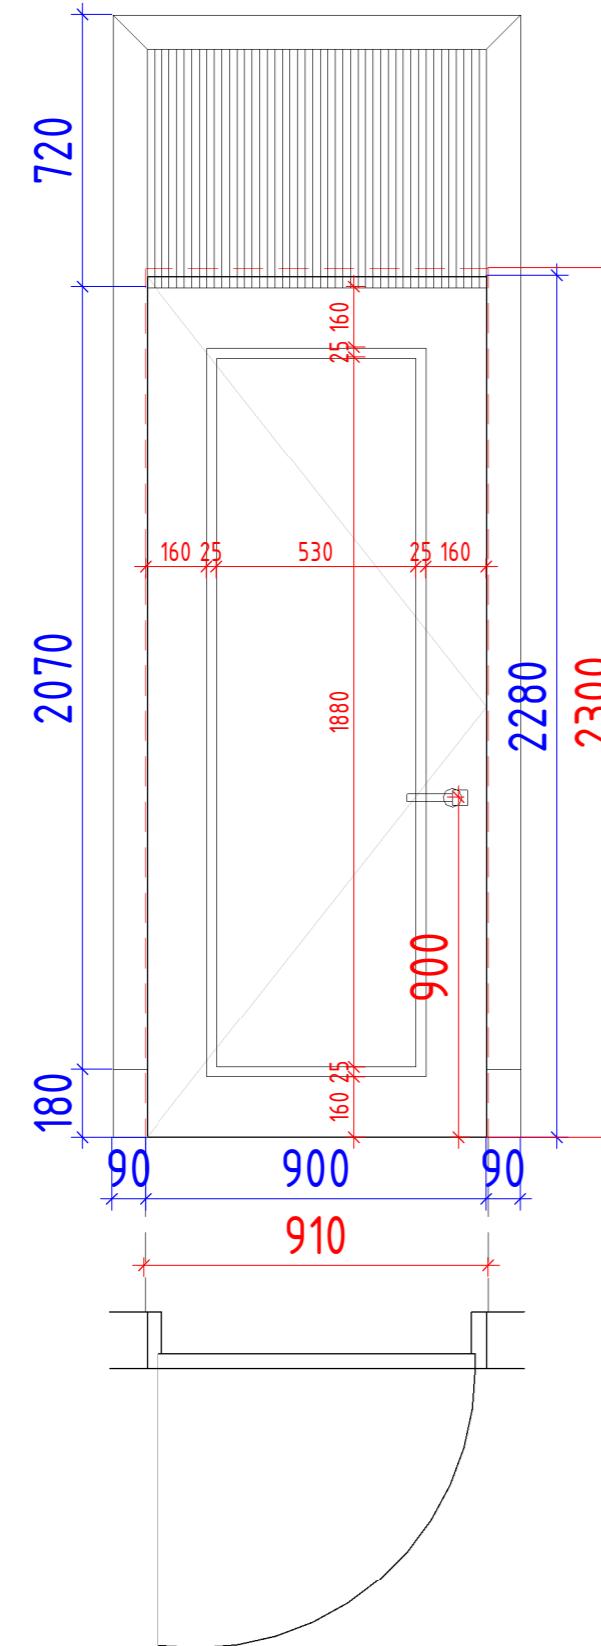

Д-2

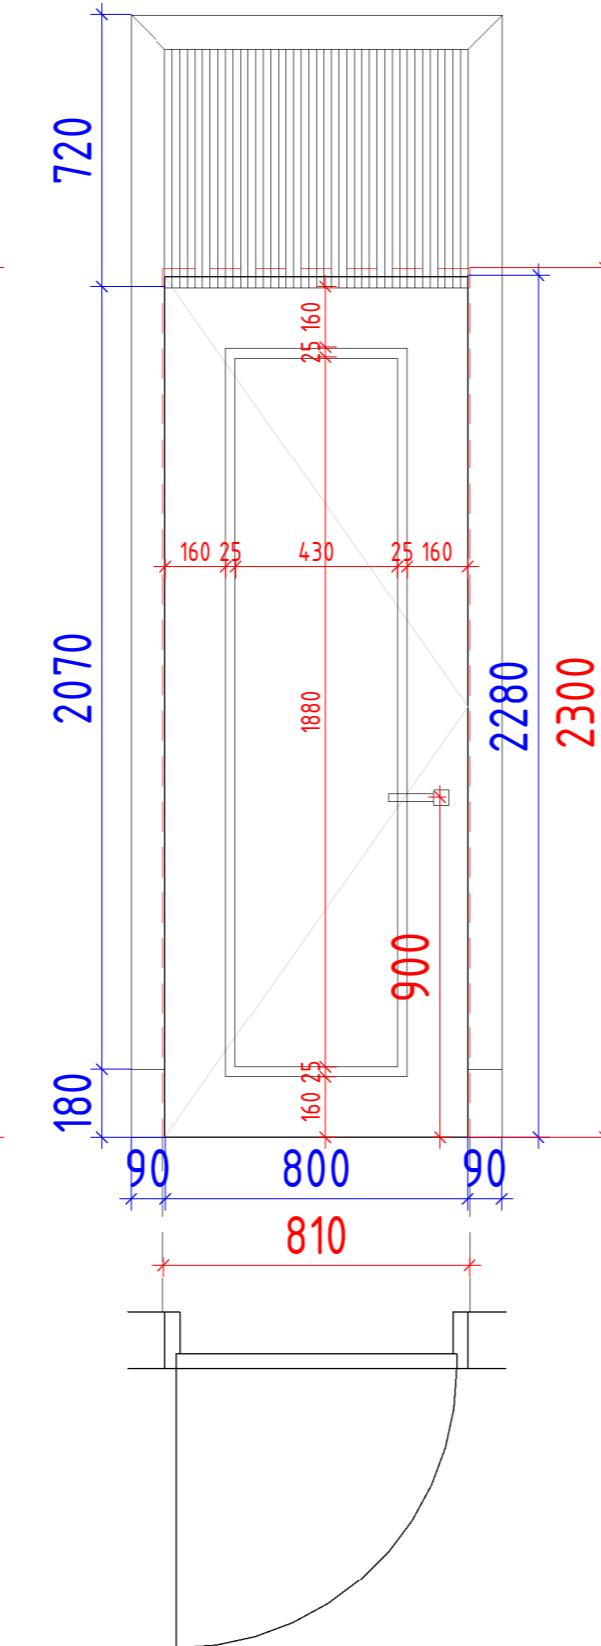

Д-3

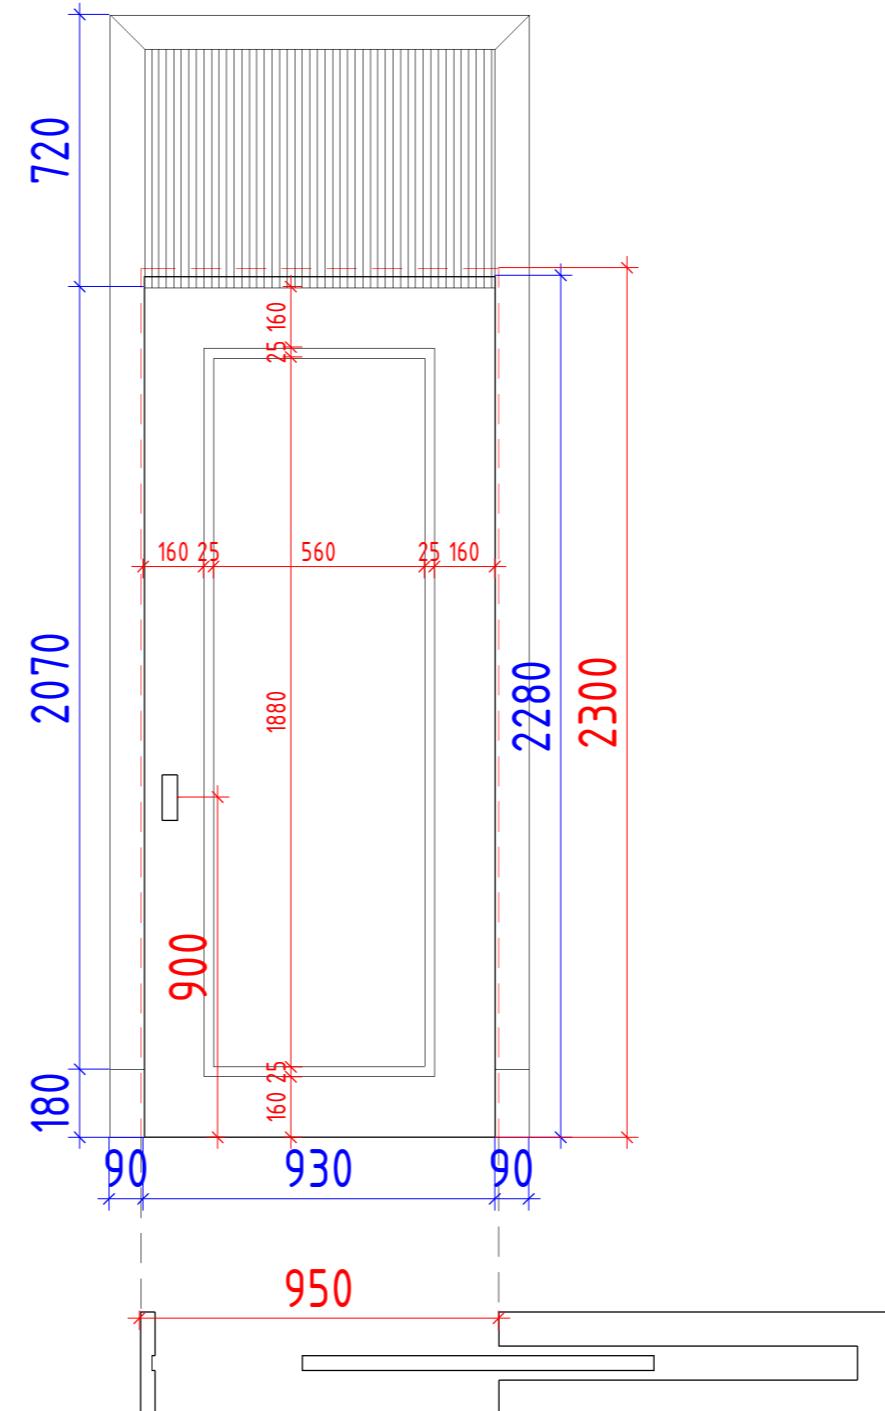

Ведомость заполнения дверных проемов

Тип	Ширина проема	Высота проема	Ширина	Высота	Описание	Кол-во
Д-1л	910	2300	900	2280	Левая	3
Д-1п	910	2300	900	2280	Правая	1
Д-2п	810	2300	800	2280	Дверь с порогом. Правая	2
Д-3л	950	2300	930	2280	Раздвижная левая	1
Д-3п	950	2300	930	2280	Раздвижная правая	1

8

Примечания:

- За отметку 0.000 принята отметка чистого пола квартиры.
- Все размеры уточняются по месту.
- Наличник дверей со стороны санузлов на 100 мм ниже чем в остальных помещениях

Условные обозначения:

-Размер проема

-Размер двери


Отделочные материалы двери

Изображение	Отделка	Цвет	Цвет фурнитуры
	Шпонированный МДФ	Tikkurila_G497 Ноугу_Пар	Графитовый (матовый)


Стадия	Лист	Листов
Дизайнер		

Заказчик	СПЕЦИФИКАЦИЯ ДВЕРИ		
Luxhouse_studio			

Облицовка из ГКЛ марка С 623
в соответствии с рекомендациями KNAUF
серия 1.073.9-2.00.1-7

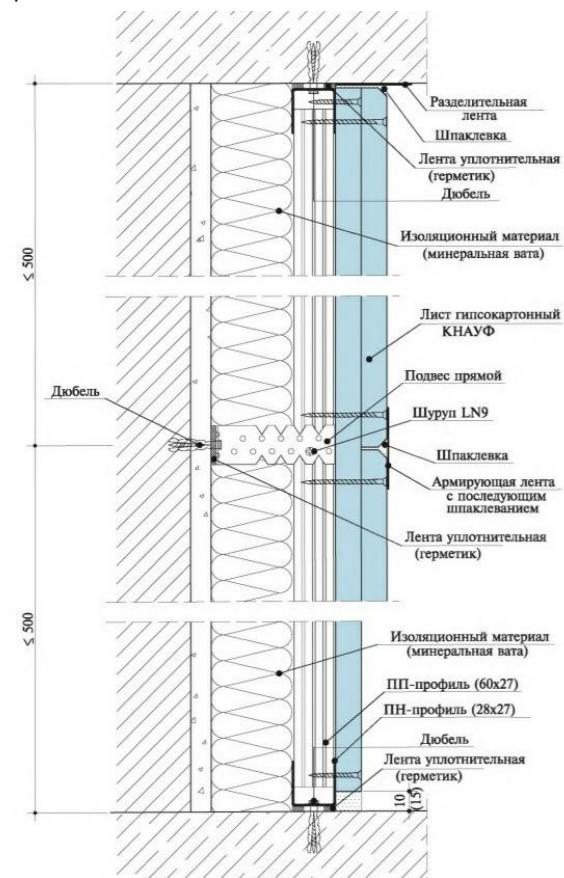

Перегородка из ГКЛ марка С 112
в соответствии с рекомендациями KNAUF
серия 1.031.9-2.07.2-3

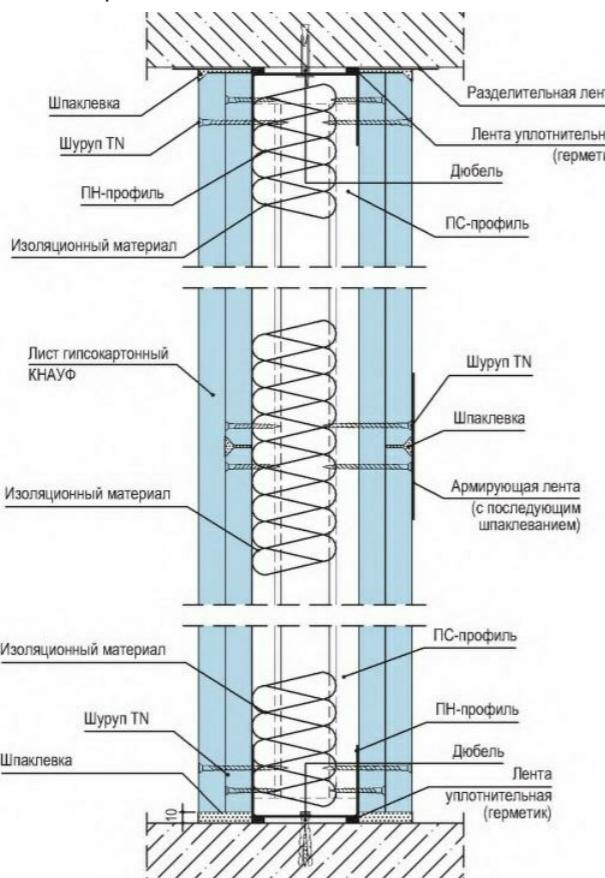

Ведомость перегородок и облицовок из ГКЛ

Изображение	Марка	Описание	Площадь
	0-1	Облицовка из ГКЛ марка С 623 в соответствии с рекомендациями KNAUF серия 1.073.9-2.00.1-7 . Двухслойная облицовка из ГКЛ-листов на металлическом каркасе, со звукоизоляцией, толщина (50мм)	32.81 м ²
	0-2	Облицовка из ГКЛ марка С 623 в соответствии с рекомендациями KNAUF серия 1.073.9-2.00.1-7 . Двухслойная облицовка из ГКЛ-листов на металлическом каркасе, со звукоизоляцией, толщина (100мм)	4.23 м ²
	П-1	Перегородка из ГКЛ марка С 112 в соответствии с рекомендациями KNAUF серия 1.031.9-2.07.2-3 . Двухслойная облицовка из ГКЛ-листов на металлическом каркасе с двух сторон, со звукозащитой, толщина (150мм)	59.85 м ²
	П-2	Перегородка из ГКЛ марка С 112 в соответствии с рекомендациями KNAUF серия 1.031.9-2.07.2-3 . Двухслойная облицовка из ГКЛ-листов на металлическом каркасе с двух сторон, со звукозащитой, толщина (180мм)	4.78 м ²

101.68
м²

Ведомость перегородок и облицовок из ГКЛВ

Изображение	Марка	Описание	Площадь
	0-3	Облицовка из ГКЛ марка С 623 в соответствии с рекомендациями KNAUF серия 1.073.9-2.00.1-7 . Двухслойная облицовка из ГКЛВ-листов на металлическом каркасе, со звукоизоляцией, толщина (50мм)	12.62 м ²
	П-3	Перегородка из ГКЛ марка С 112 в соответствии с рекомендациями KNAUF серия 1.031.9-2.07.2-3 . Двухслойная облицовка из ГКЛВ-листов на металлическом каркасе с двух сторон, со звукоизоляцией, толщина (150мм)	38.62 м ²

51.24 м²

Стадия	Лист	Листов
Дизайнер		
Заказчик		

СПЕЦИФИКАЦИЯ ПЛАН
МОНТАЖА ПЕРЕГОРОДОК

Luxhouse_studio


Формат: А3

Сантехнические оборудование и аксессуары				
Тип	Изображение	Описание	Изготовитель	Кол-во, шт
1		Встраиваемая в столешницу раковина на кухню Maris MRX 110-50, артикул 122.0543.996	Franke	1
2		Смеситель для кухонной мойки артикул 115.0569.461	Franke	1
3		Смеситель для раковины		2
4		Встраиваемая раковина для санузла		2
5		Унитаз, артикул 7082-0075	Vitra	2
6		Кнопка смыва, артикул 740-0586	Vitra	2
7		Акриловая ванна Riho Miami, габариты (дшв): 180x80x43 см	Нидерланды	1
8		Nest code 42242 Shine code 45628		1
9		Ручной душ, артикул 45683	Vitra	1
10		Термостат для душа, артикул 47025	Vitra	1

Сантехнические оборудование и аксессуары				
Тип	Изображение	Описание	Изготовитель	Кол-во, шт
11		Верхний душ, артикул 45646	Vitra	1
12		Душевой лоток Pestan, Confluo Frameless Line		1
13		Полотенцесушитель 600x100 h		1
14		Полотенцесушитель 550x750 h		1
15		Стеклянная перегородка для душа. 700 x 2000 h		1
16		Стеклянная перегородка для душа. 440 x 2000 h		1
17		Стеклянная перегородка для душа - Дверца. 600 x 2000 h		1

Ведомость акрила для столешницы		
Изображение	Описание	Площадь
	AS642 Aspen Seashell	8.51 м ²

Стадия	Лист	Листов
Дизайнер		
Заказчик		
СПЕЦИФИКАЦИЯ САНТЕХНИЧЕСКОГО ОБОРУДОВАНИЯ		
Luxhouse_studio		

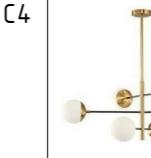Осветительные приборы						
Тип	Изображение	Описание	Кол-во, шт	Кельвин	Вт	Ссылка
C1		Артикул: DL18413/11WW-R White	58	3500	10	
C2		Артикул: DL18413/11WW-R White	6	3500	15	
C3		Артикул: DL18413/11WW-R White	9	3500	7	
C4		Milky Gold Trees Chandelier Главная/Люстры Артикул L1314	1			https://lampsshop.ru/?store-page=Milky-Gold-Trees-Chandelier-p229342405
C5		Люстра Bond Современные люстры Артикул L1323	1	3500		https://lampsshop.ru/?store-page=%D0%9B%D1%8E%D1%81%D1%82%D1%80%D0%BF-Bond-p234774662
C6		Настенный светильник ForkWal. Артикул: 13027-7l	2	3000-60 00	25	https://glode.ru/catalog/product/331976600-485436027791-nastennii-svetilnik-for-kwall
C7		Торшер SimpLumen. Артикул: 00001-2	2			https://glode.ru/catalog/product/334660034-836381128431-torsher-simplumen
C8		Настенный светильник OmniWall. Артикул: 13034-2	1	3000-60 00	25	https://glode.ru/catalog/product/331976600-555954115711-nastennii-svetilnik-omni-wall
C9		Подвесной светильник из серии Perfection Подвесные светильники Артикул PDL2191	1	3000	25	https://lampsshop.ru

Осветительные приборы						
Тип	Изображение	Описание	Кол-во, шт	Кельвин	Вт	Ссылка
C10		Настенный светильник КАА Артикул W111043/1 white	1	3000	3	https://www.donolux.ru/produktsiya/Nastennye-svetilniki/KAA
C11		Бра Loft A Артикул В4283а	1	3000	5	https://lampsshop.ru/?store-page=%D0%99%D1%80%D0%BD-A-loft-A-p349213495&offset=36
C12		Подвесной светильник Heyday. Артикул PDL2194b	1	3000	5	https://lampsshop.ru

Стадия	Лист	Листов
Дизайнер		
Заказчик		

СПЕЦИФИКАЦИЯ
ОСВЕТИТЕЛЬНОГО ПРИБОРОВ

Luxhouse_studio

Спецификация напольных покрытий в душевой (плитки НП3)					
Тип	Условное изображение	Описание	Площадь, кв.м	Пирог пола	Данные элементов пола
НП3		600x1200, 55012923 Vitra	4.07 м ²		1. Керамогранит - 8 мм 2. Клей - 5 мм 3. Цементно-песчанная стяжка - 62 мм 4. Гидроизоляция 5. Существующее перекрытие - 200 мм

Спецификация напольных покрытий (ламинат)					
Тип	Условное изображение	Описание	Площадь, кв.м	Пирог пола	Данные элементов пола
НП2		Quick Step Castle CA 4160 Дуб капучино Класс 33 AC5 1200x396x8 мм	91.65 м ²		1. Ламинат - 8 мм 2. Подложка - 3 мм 3. Цементно-песчаная стяжка - 69 мм 4. Существующее перекрытие - 200 мм

Спецификация напольных покрытий в душевой (плитки НП4)					
Тип	Условное изображение	Описание	Площадь, кв.м	Пирог пола	Данные элементов пола
НП4		600x1200, 55012923 Vitra	4.86 м ²		1. Керамогранит - 8 мм 2. Клей - 5 мм 3. Цементно-песчаная стяжка - 62 мм 4. Гидроизоляция 5. Существующее перекрытие - 200 мм

Ведомость плинтусов				
Тип	Изображение	Обозначение	Описание	Длина
Пл1			Tikkurila_G497 Hougy_Пар	49.86
				49.86

Спецификация напольных покрытий в прихожей (плитки)					
Тип	Условное изображение	Описание	Площадь, кв.м	Пирог пола	Данные элементов пола
НП1		600x1200, 55012906 Vitra	8.61 м ²		1. Керамогранит - 8 мм 2. Клей - 5 мм 3. Цементно-песчаная стяжка - 67 мм 4. Существующее перекрытие - 200 мм



Стадия	Лист	Листов
Дизайнер		
Заказчик		
СПЕЦИФИКАЦИЯ НАПОЛЬНОГО ПОКРЫТИЯ		
Luxhouse_studio		

Спецификация осветительных приборов						
Тип	Изображение	Описание	Кол-во, шт	Кельвин	Вт	Ссылка
C1		Артикул: DL18413/11WW-R White	58	3500	10	
C2		Артикул: DL18413/11WW-R White	6	3500	15	
C3		Артикул: DL18413/11WW-R White	9	3500	7	
C4		Milky Gold Trees Chandelier Гла8ная/Люстры Артикул L1314	1			https://lampsshop.ru/?store-page=Milky-Gold-Trees-Chandelier-p229342405
C5		Люстра Bond Современные люстры Артикул L1323	1	3500		https://lampsshop.ru/?store-page=%D0%9B%D1%8E%D1%81%D1%82%D1%80%D0%BD-Bond-p234774662
C6		Настенный светильник ForkWal. Артикул: 13027-71	2	3000-6000	25	https://glode.ru/catalog/product/331976600-485436027791-nastennii-svetilnik-forkwall

Спецификация осветительных приборов						
Тип	Изображение	Описание	Кол-во, шт	Кельвин	Вт	Ссылка
C7		Торшер SimpLumen. Артикул: 00001-2	2			https://glode.ru/catalog/product/334660034-836381128431-torsher-simplumen
C8		Настенный светильник OmniWall. Артикул: 13034-2	1	3000-6000	25	https://glode.ru/catalog/product/331976600-555954115711-nastennii-svetilnik-omniwall
C9		Подвесной светильник из серии Perfection Подвесные светильники Артикул PDL2191	1	3000	25	https://lampsshop.ru
C10		Настенный светильник KAA Артикул W111043/1 white	1	3000	3	https://www.donolux.ru/produktsiya/Nastennyie-svetilniki/KA-A
C11		Бра Loft A Артикул B4283а	1	3000	5	https://lampsshop.ru/?store-page=%D0%91%D1%80%D0%B0-Loft-A-p349213495&offset=36
C12		Подвесной светильник Heyday. Артикул PDL2194в	1	3000	5	https://lampsshop.ru

Спецификация LED для мебели			
Тип	Изображение	Усл.обозначение	Длина, мм
C14		—	22.14

Стадия	Лист	Листов
Дизайнер		
Заказчик		
СПЕЦИФИКАЦИЯ ОСВЕТИТЕЛЬНЫХ ПРИБОРОВ		Luxhouse_studio

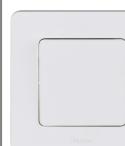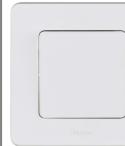Спецификация розеток и выключателей			
Изображение	Описание	Кол-во, шт	Производитель
	Выход кабеля	23	
	Выключатель двойхклавишный	9	Legrand
	Выключатель одноклавишный	5	Legrand
	Переключатель двойхклавишный	4	Legrand
	Переключатель одноклавишный	7	Legrand
	Розетка 2x USB	3	Legrand
	Розетка 220V	52	Legrand


Спецификация розеток и выключателей			
Изображение	Описание	Кол-во, шт	Производитель
	Розетка INT	1	Legrand
	Розетка IP44	6	Legrand
	Розетка TV	4	Legrand
	Розетка компьютерная 1x RJ45	1	Legrand
	Розетка компьютерная 2x RJ45	4	Legrand
	Термостат теплого пола	3	Legrand






Спецификация рамок			
Изображение	Описание	Кол-во, шт	Производитель
	Рамка на 1 пост	49	Legrand
	Рамка на 2 поста	13	Legrand
	Рамка на 3 поста	4	Legrand

Спецификация рамок			
Изображение	Описание	Кол-во, шт	Производитель
	Рамка на 4 поста	5	Legrand
	Рамка на 5 постов	3	Legrand

Стадия	Лист	Листов
Дизайнер		
Заказчик		
СПЕЦИФИКАЦИЯ РОЗЕТОК И ВЫКЛЮЧАТЕЛЕЙ		
Luxhouse_studio		

Спецификация сантехнического оборудования и аксессуаров				
Тип	Изображение	Описание	Изготовитель	Кол-во, шт
1		Встраиваемая в столешницу раковина на кухню. Maris MRX 110-50, артикул 122.0543.996	Franke	1
2		Смеситель для кухонной мойки артикул 115.0569.461	Franke	1
3		Смеситель для раковины		2
4		Встраиваемая раковина для санузла		2
5		Чиназ, артикул 7082-0075	Vitra	2
6		Кнопка смыыва, артикул 740-0586	Vitra	2

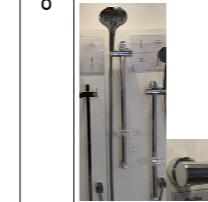Спецификация сантехнического оборудования и аксессуаров				
Тип	Изображение	Описание	Изготовитель	Кол-во, шт
7		Акриловая ванна Rho Miami, габариты (дшг): 180x80x43 см	Нидерланды	1
8		Nest code 42242 Shine code 45628		1
9		Ручной душ, артикул 45683	Vitra	1
10		Термостат для душа, артикул 47025	Vitra	1
11		Верхний душ, артикул 45646	Vitra	1
12		Душевой лоток	Pestan, Confluo Frameless Line	1

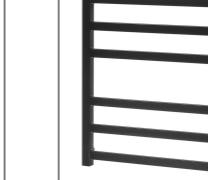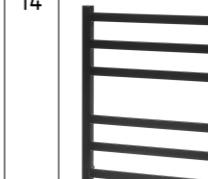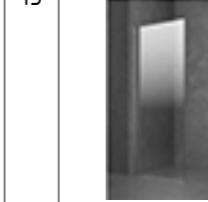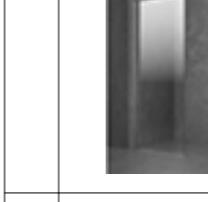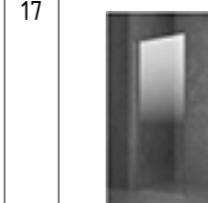Спецификация сантехнического оборудования и аксессуаров				
Тип	Изображение	Описание	Изготовитель	Кол-во, шт
13		Полотенцесушитель 600x1000 h		1
14		Полотенцесушитель 550x750 h		1
15		Стеклянная перегородка для душа. 700 x 2000 h		1
16		Стеклянная перегородка для душа. 440 x 2000 h		1
17		Стеклянная перегородка для душа - Дверца. 600 x 2000 h		1

Дизайнер	Заказчик	СПЕЦИФИКАЦИЯ САНТЕХНИЧЕСКОГО ОБОРУДОВАНИЯ			Стадия	Лист	Листов
					AI		



Стадия	Лист	Листов
Дизайнер		
Заказчик		

КОЛЛАЖ ГОСТИНАЯ



Luxhouse_studio

Формат: А3



Дизайнер			
Заказчик			

КОЛЛАЖ СПАЛЬНИ



Luxhouse_studio

Формат: А3

Стадия	Лист	Листов
АИ		



Дизайнер			
Заказчик			

КОЛЛАЖ ПРИХОЖАЯ



Luxhouse_studio

Формат: А3

Стадия	Лист	Листовъ
АИ		