

### Ведомость рабочих чертежей


Лист	Наименование	Примечание
0	Ведомость рабочих чертежей	
1	Обмерный план	
2	План демонтажа перегородок	
3	План монтажа перегородок	
4	3D Вид монтажа	
5	План расстановки мебели	
6	План расстановки мебели 3D	
7	План расстановки мебели с размерами	
8	Расположение ВК_Кухня и Санузел №8	
9	Расположение ВК_Санузел № 9 и спецификация сантехнических приборов	
10	План отопления	
11	План напольных покрытий	
12	План потолка	
13	План расстановки осветительного оборудования	
14	План расстановки розеток	
15	План привязки приборов освещения к выключателям	


### Ведомость рабочих чертежей

Лист	Наименование	Примечание
16	Спецификация сантехнического оборудования и аксессуаров	
17	Спецификация_План монтажа перегородок	
18	Спецификация План расстановки розеток	
19	Общая спецификация_Стены	
20	Общая спецификация_Полы, Потолки, Отопительные приборы	
21	Общая спецификация_Сантехника	
22	Общая спецификация_Электрика и Бытовая техника	
23	Общая спецификация_Электроника и Бытовая техника	
24	Спецификация План расстановки мебели	
25	Спецификация План напольного покрытия	
26	Спецификация План расстановки осветительного оборудования	
27	Мудборд	
28	Мудборд	
29	Мудборд	

Дизайнер			
Заказчик			

ВЕДОМОСТЬ РАБОЧИХ  
ЧЕРТЕЖЕЙ

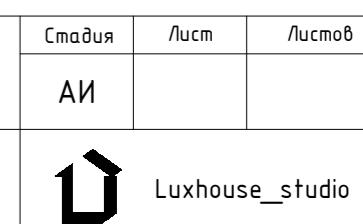

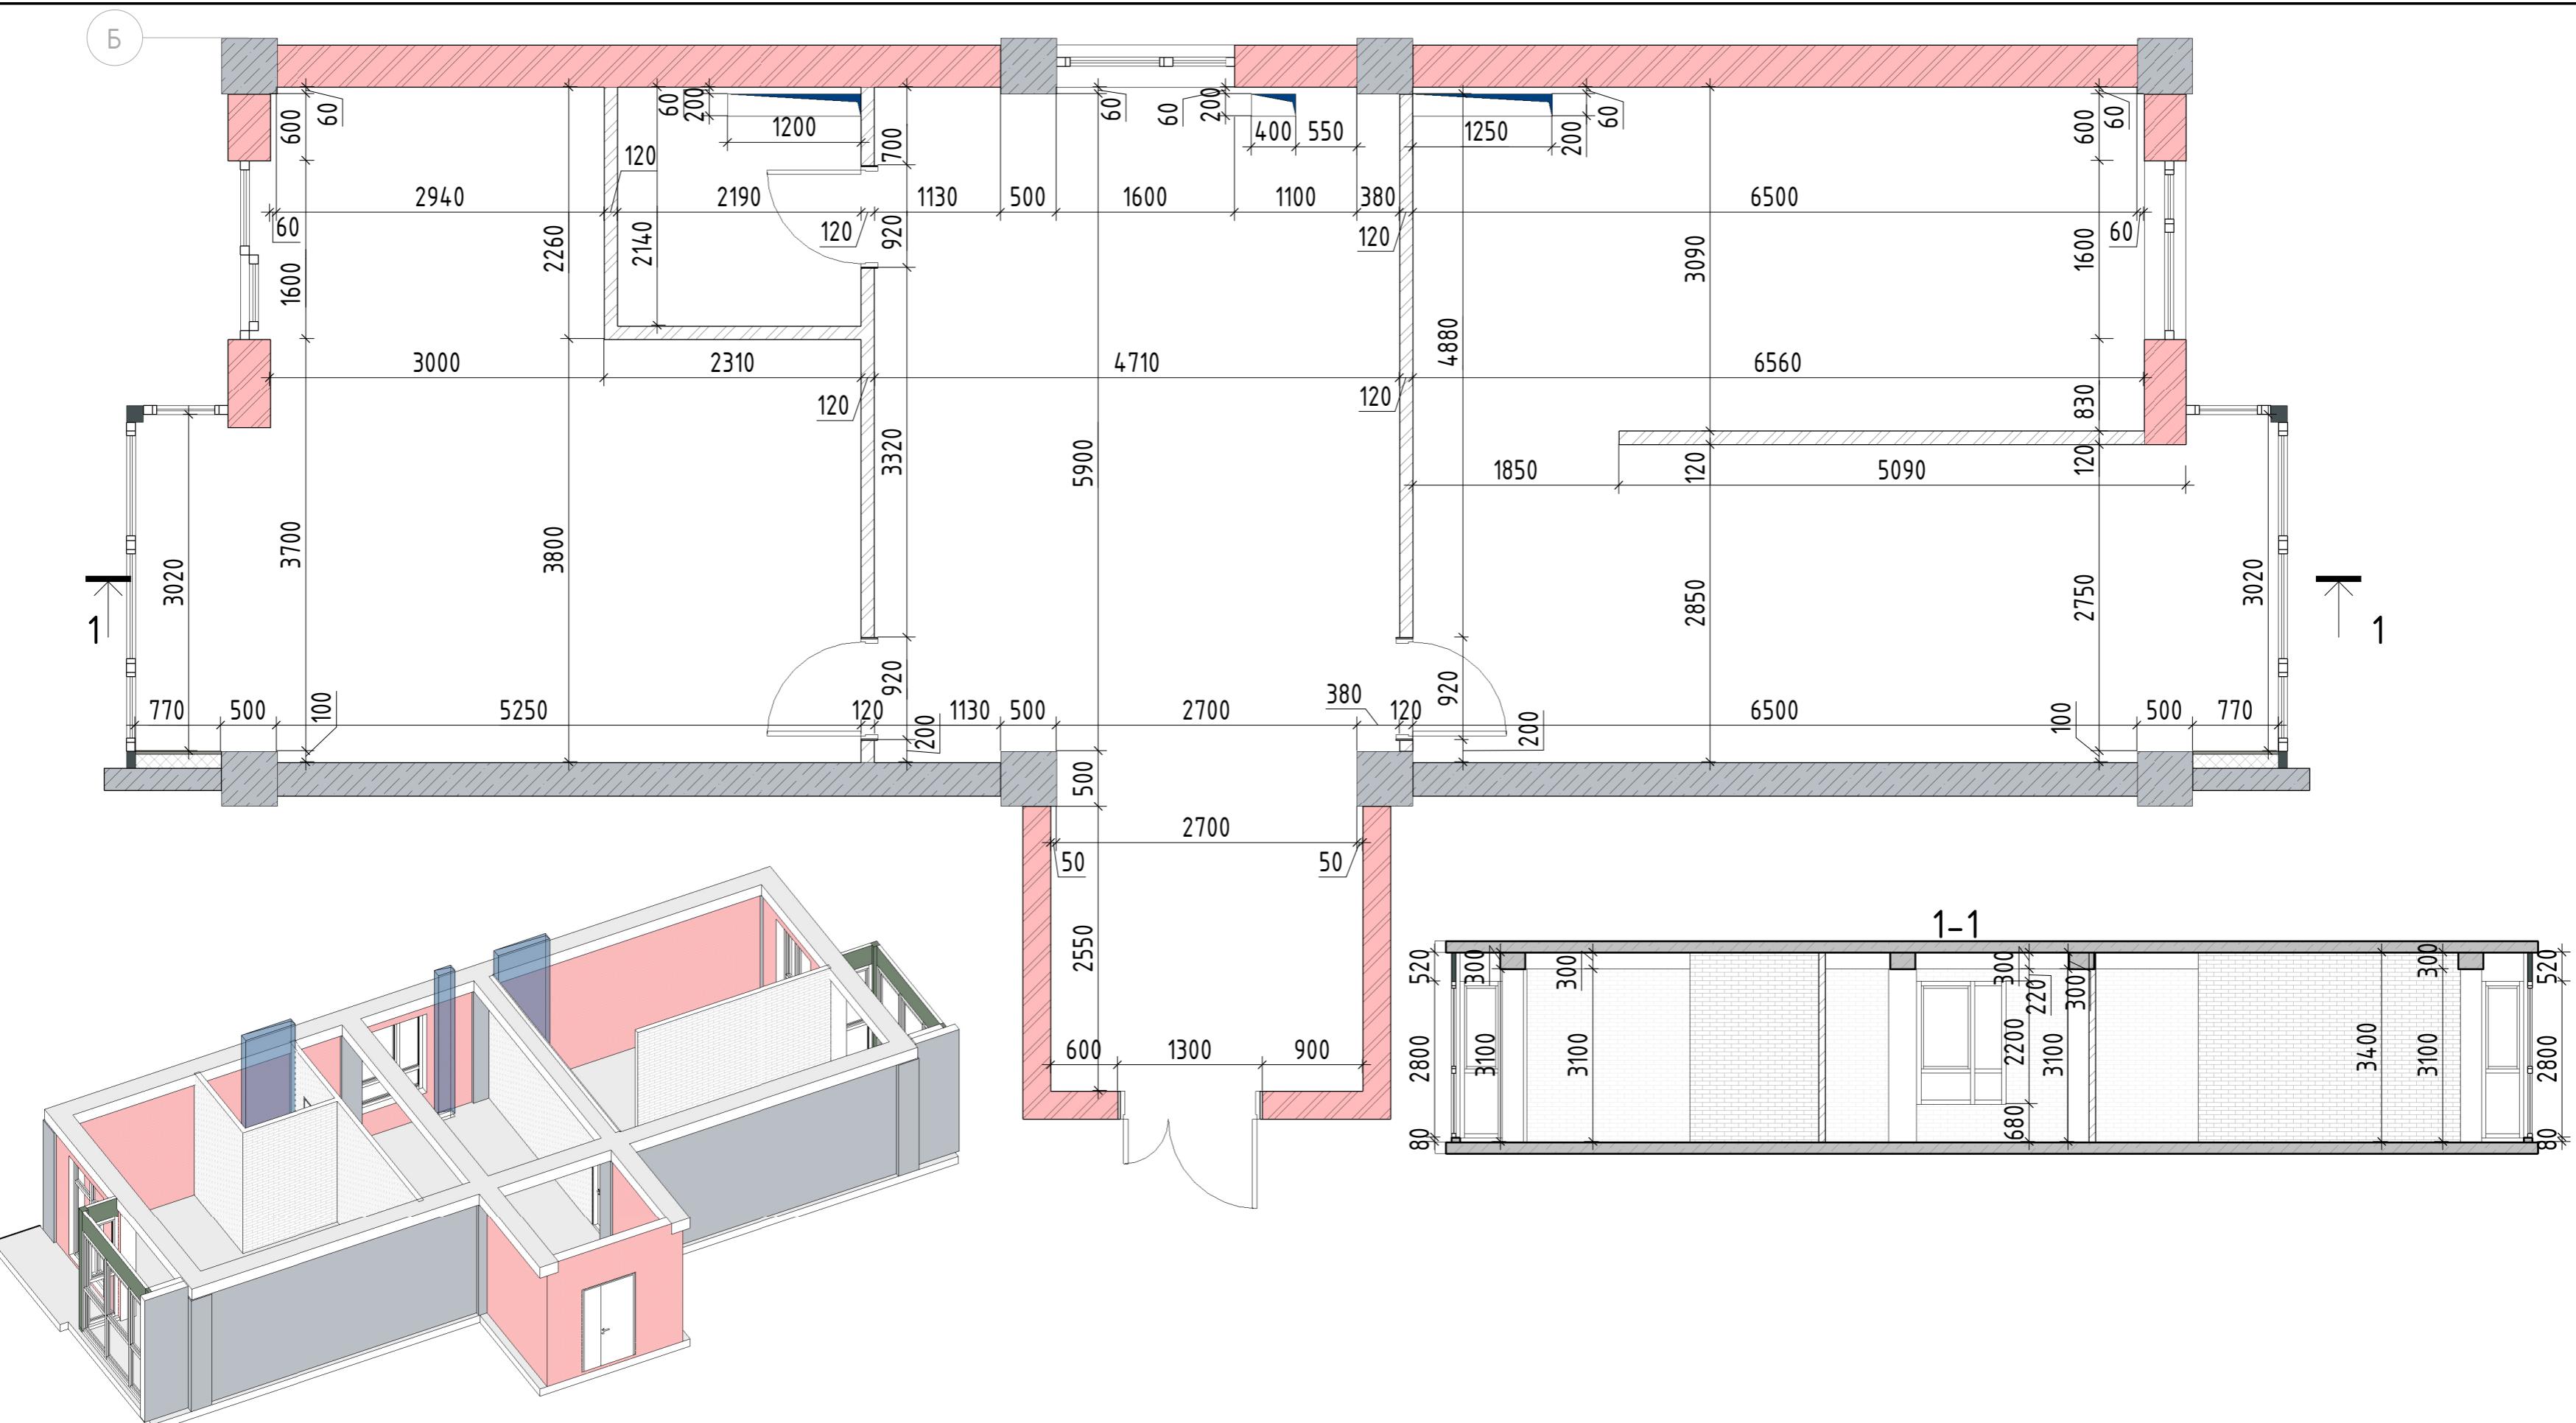



Примечания:

1. За отмечку 0.000 принята отмечка чистого пола проектируемых помещений.
2. Размеры указаны в миллиметрах.
3. Размеры уточнять по месту.

Дизайнер			
Заказчик			

ОБМЕРНЫЙ ПЛАН

Б

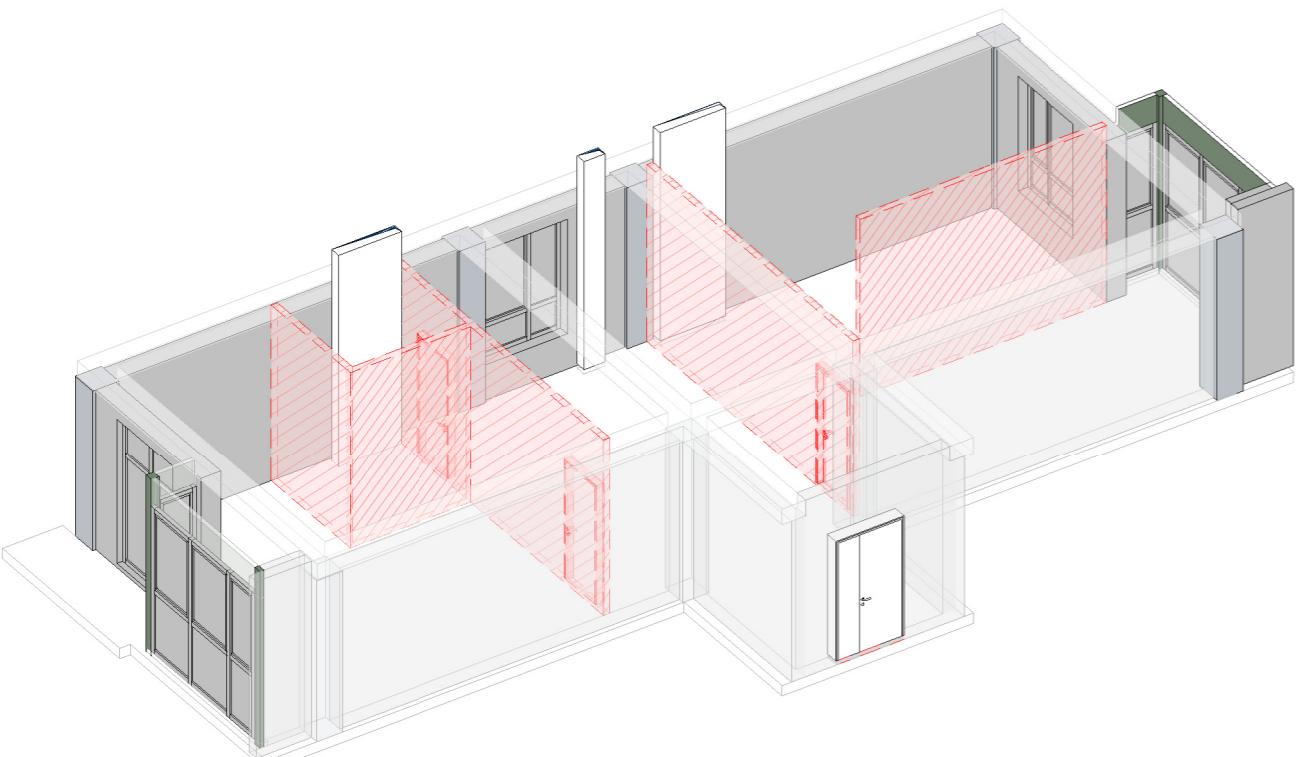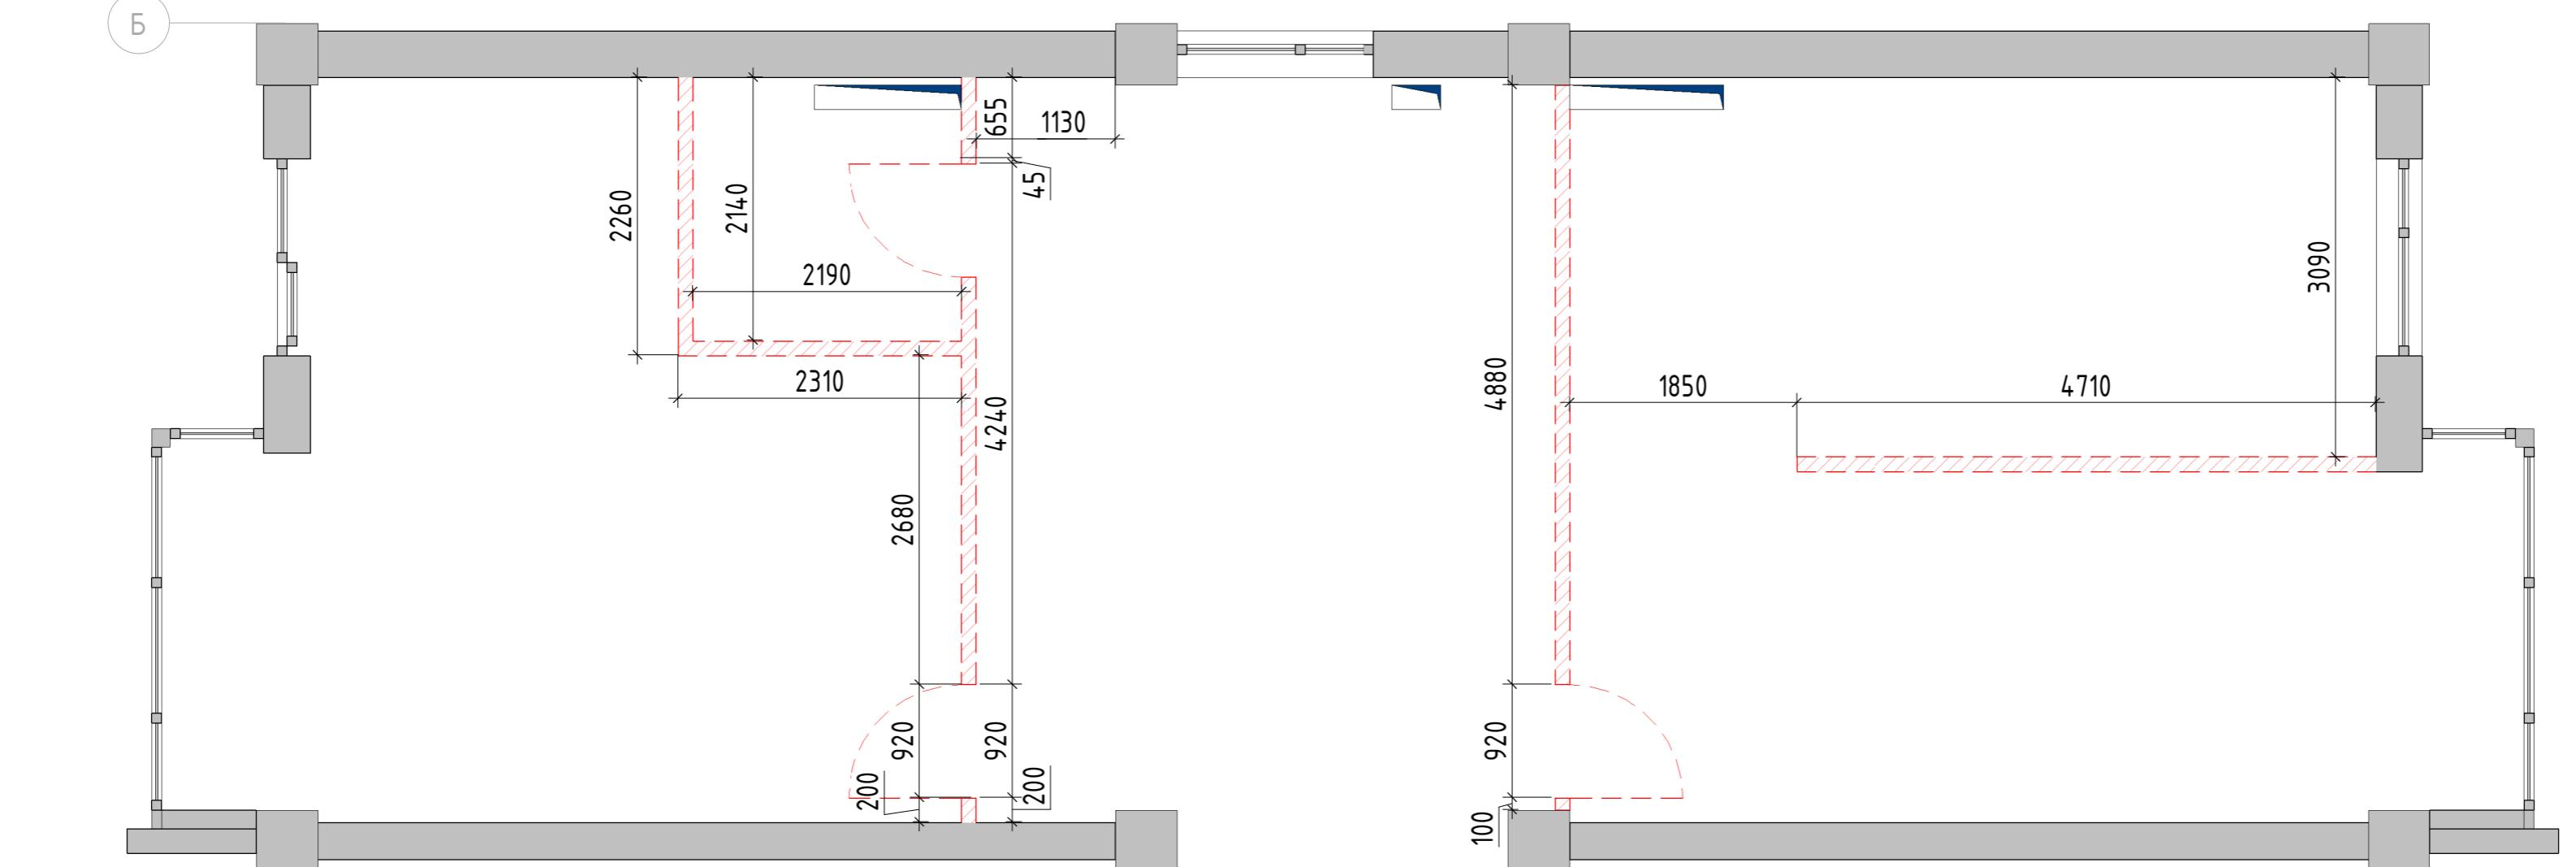

#### Условные обозначения:

- Существующие стены
- Демонтируемые перегородки

#### Примечания:

- За отметку 0.000 принята отметка чистого пола проектируемых помещений.
- Высота потолков \_\_\_\_\_.
- Размеры даны в миллиметрах.
- Фактические размеры могут незначительно отличаться. Проверить по месту.

Дизайнер			
Заказчик			


ПЛАН ДЕМОНТАЖА  
ПЕРЕГОРОДОК

Luxhouse\_studio

Формат: А3

Стадия    Лист    Листов

АИ

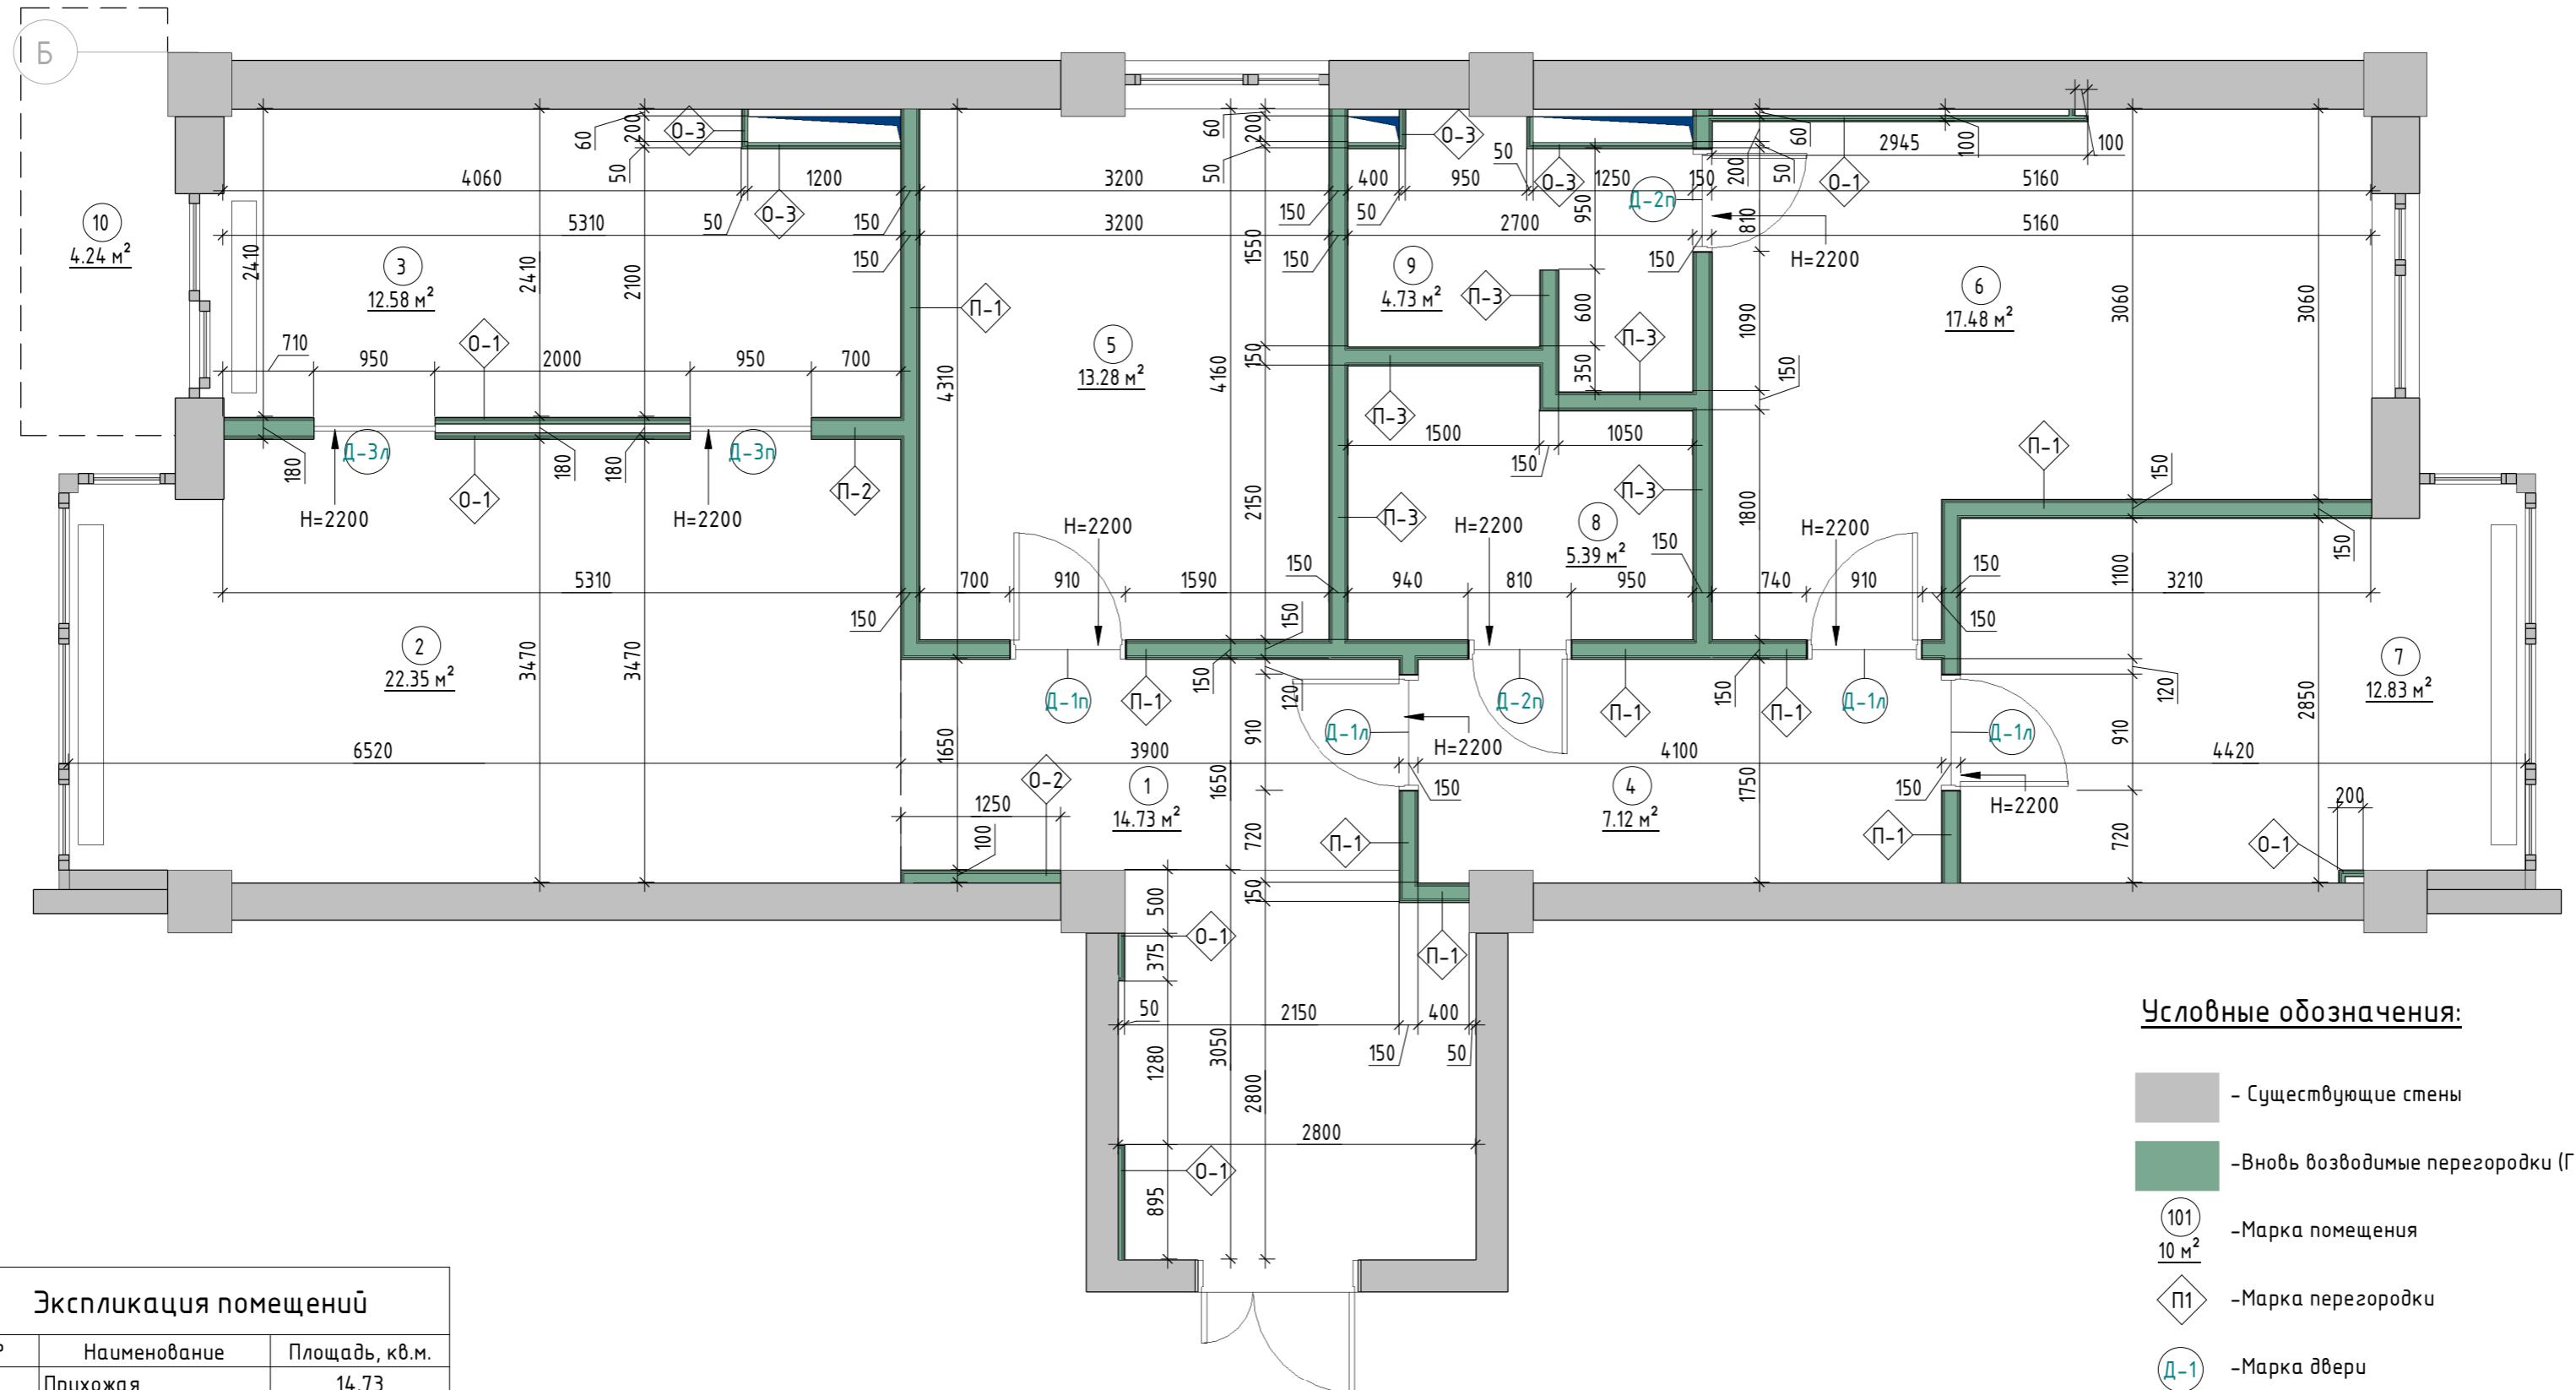

## Експлуатація помешані

Экспликация помещений		
№	Наименование	Площадь, кв.м.
1	Прихожая	14.73
2	Гостиная	22.35
3	Кухня	12.58
4	Коридор	7.12
5	Спальня	13.28
6	Спальня	17.48
7	Спальня	12.83
8	Санузел	5.39
9	Санузел	4.73
10	Балкон	4.24
		114.73

### Условные обозначения:

- Существующие стены
  - Вновь возводимые перегородки (ГКЛ)
    - Марка помещения
    - Марка перегородки
    - Марка двери

## Примечания:



1. За отметку 0.000 принята отметка чистого пола проектируемых помещений.
  2. Размеры указаны в миллиметрах.
  3. Размеры точняться по месту.

Дизайнер			
Заказчик			

## ПЛАН МОНТАЖА ПЕРЕГОРОДОК



Luxhouse studio

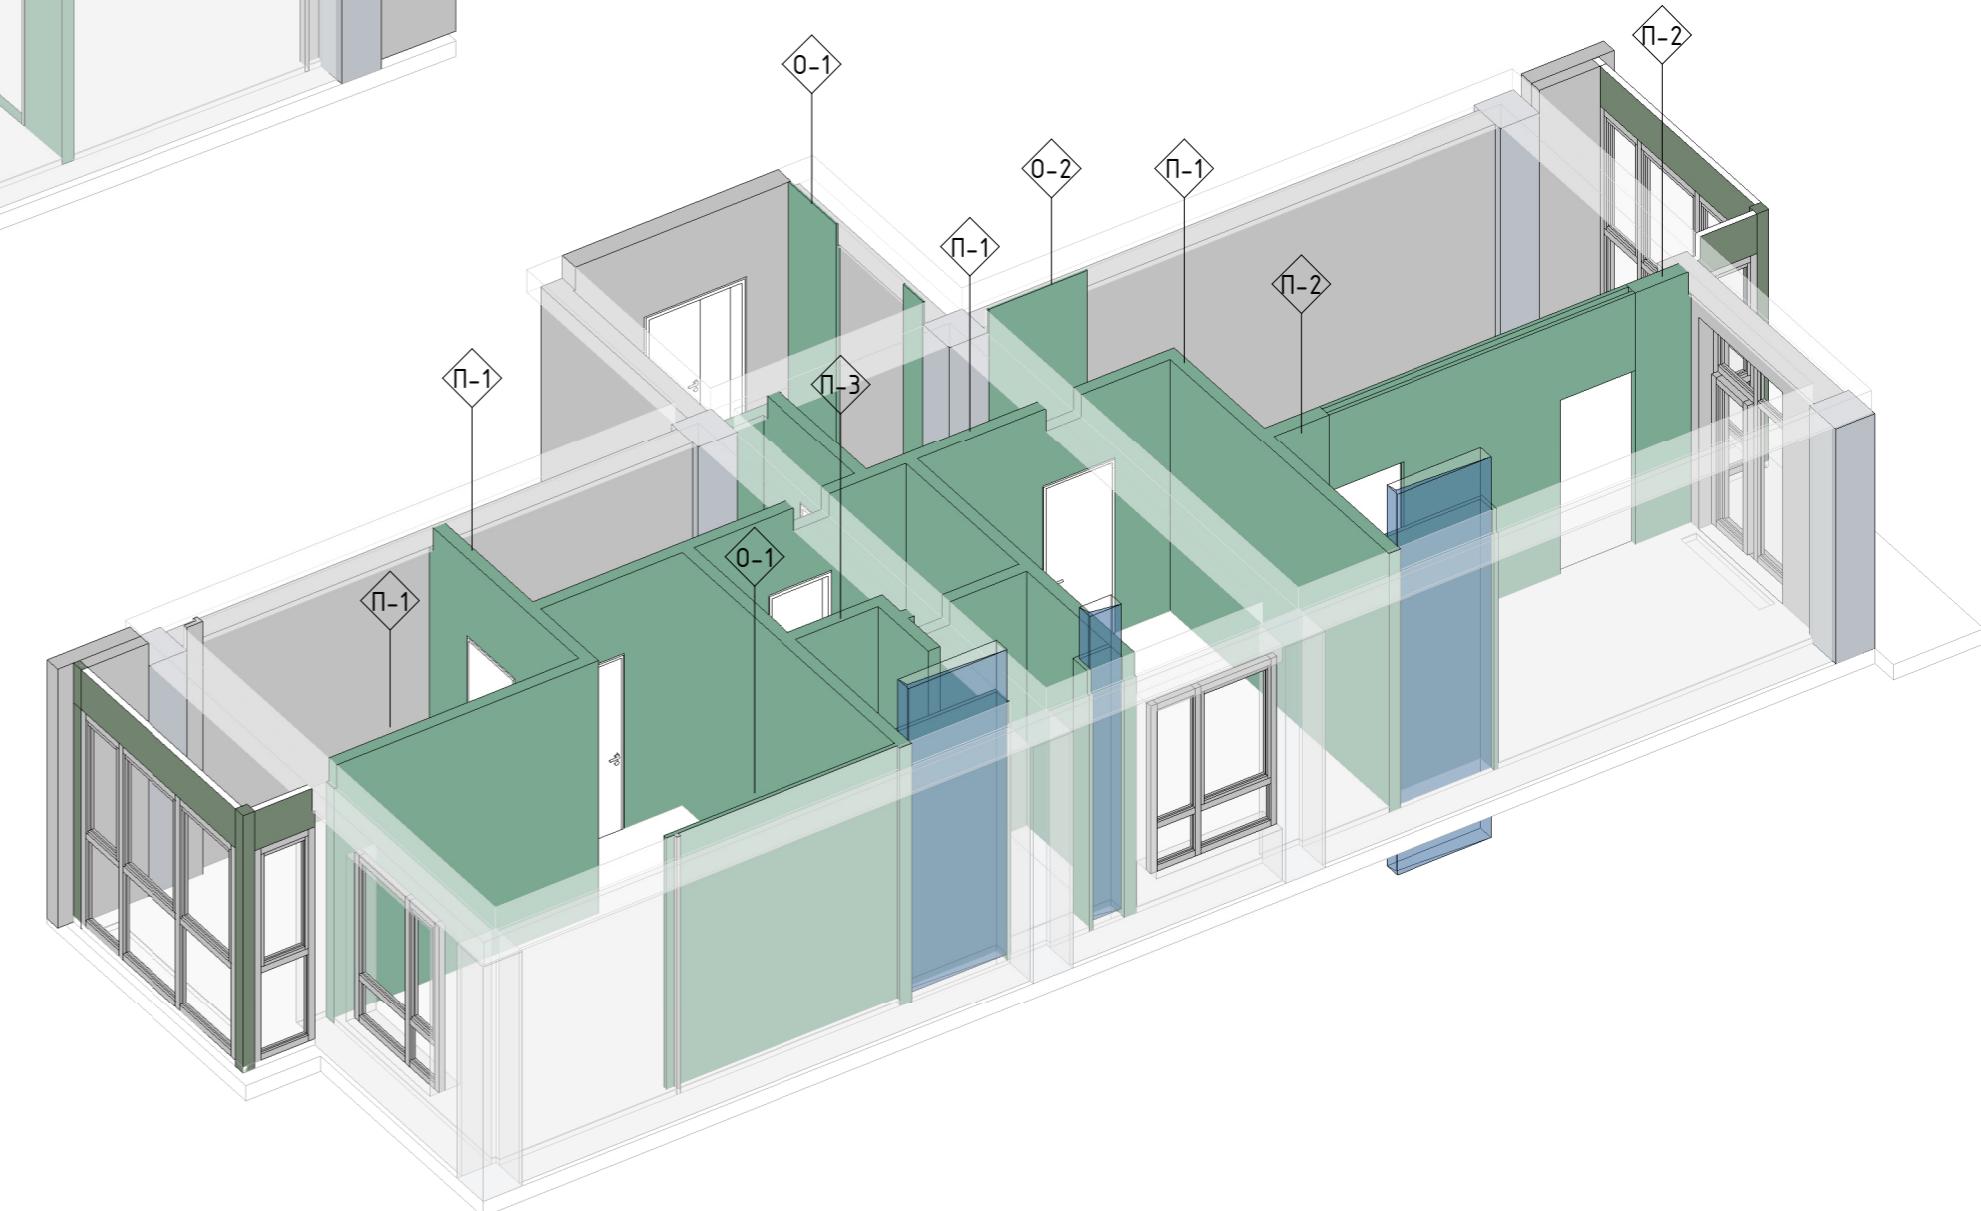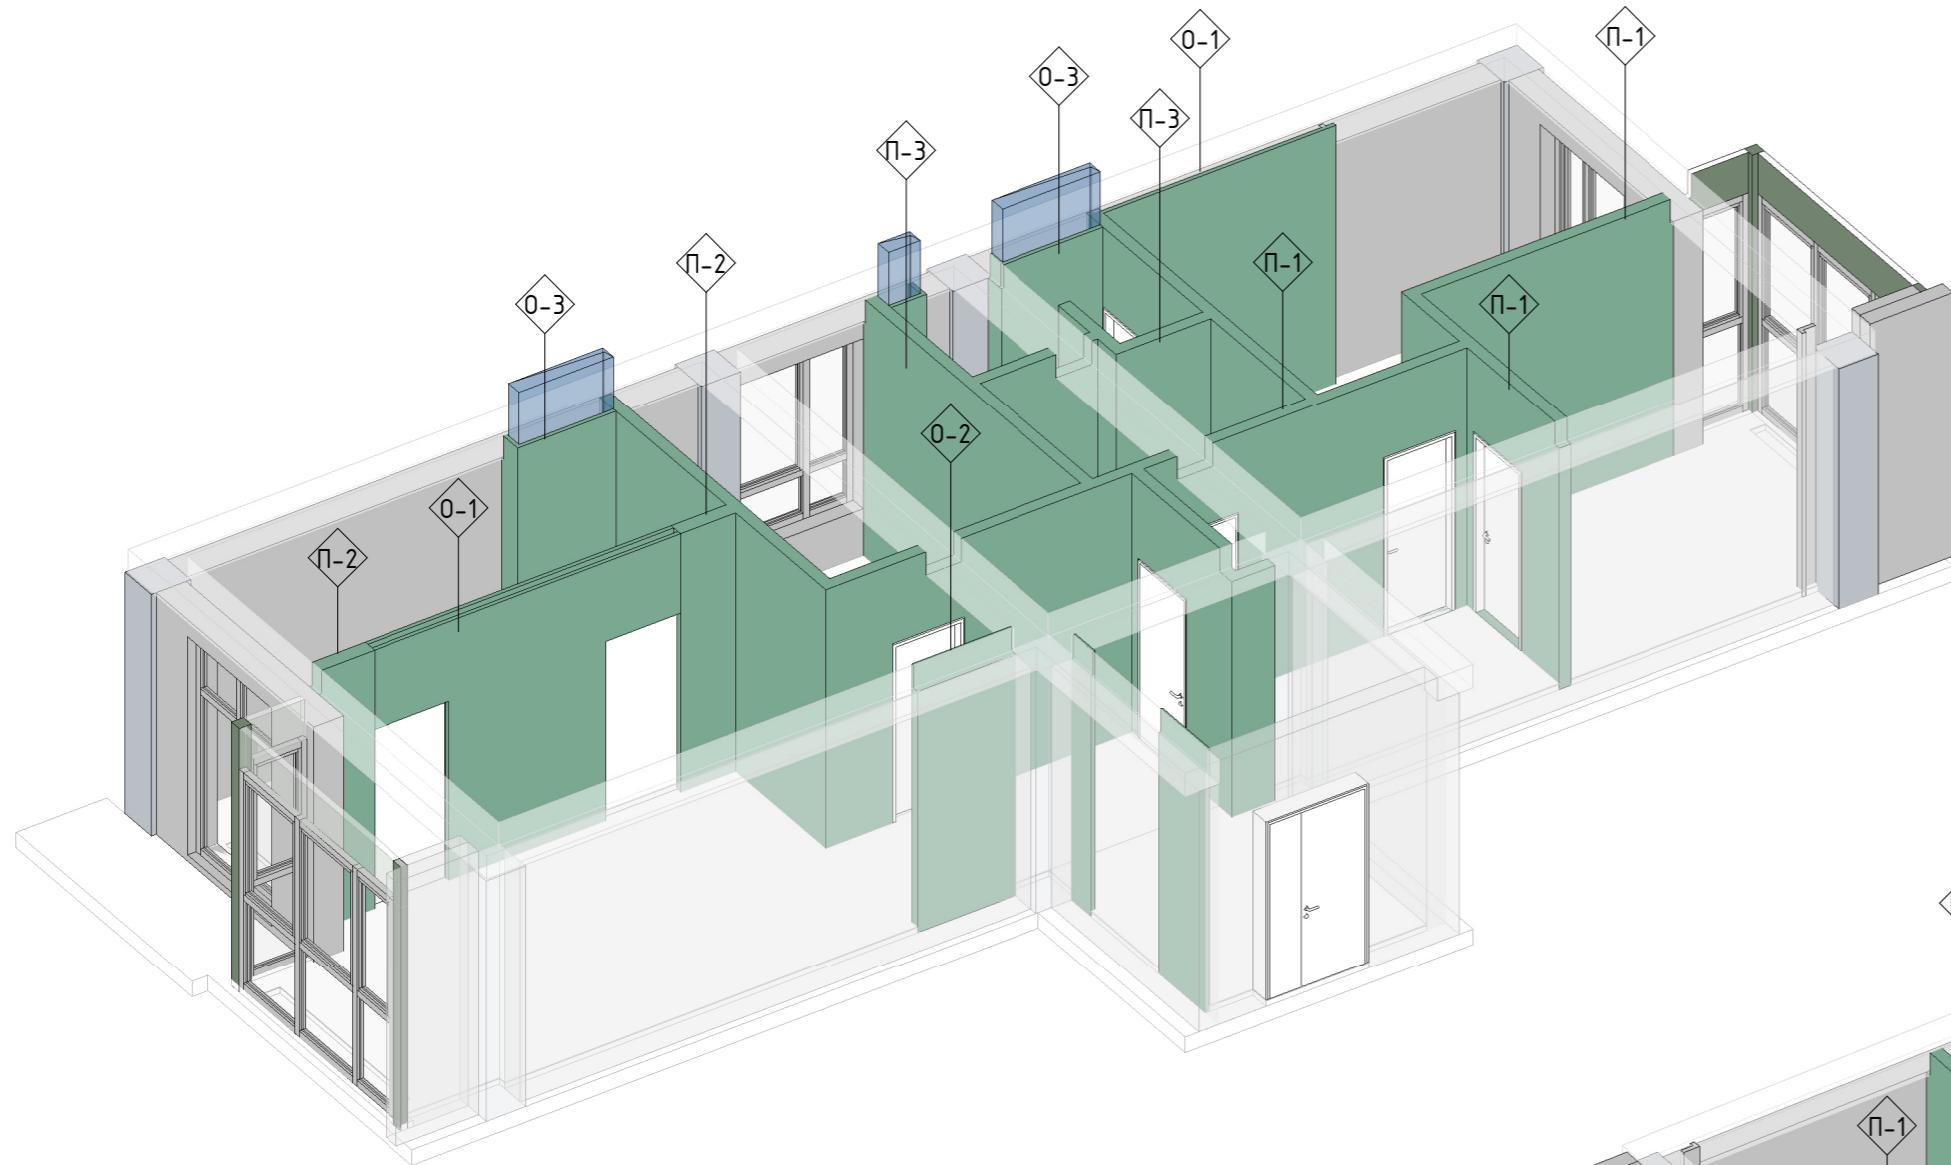

Условные обозначения:

- Существующие стены
- Вновь возводимые перегородки (ГКЛ)
- (101)  
10 м<sup>2</sup> — Марка помещения
- П1 — Марка перегородки
- Д-1 — Марка двери


Дизайнер			
Заказчик			

3D ВИД ПЛАН МОНТАЖА  
ПЕРЕГОРОДОК

Luxhouse\_studio

Формат: А3

Стадия	Лист	Листов
АИ		

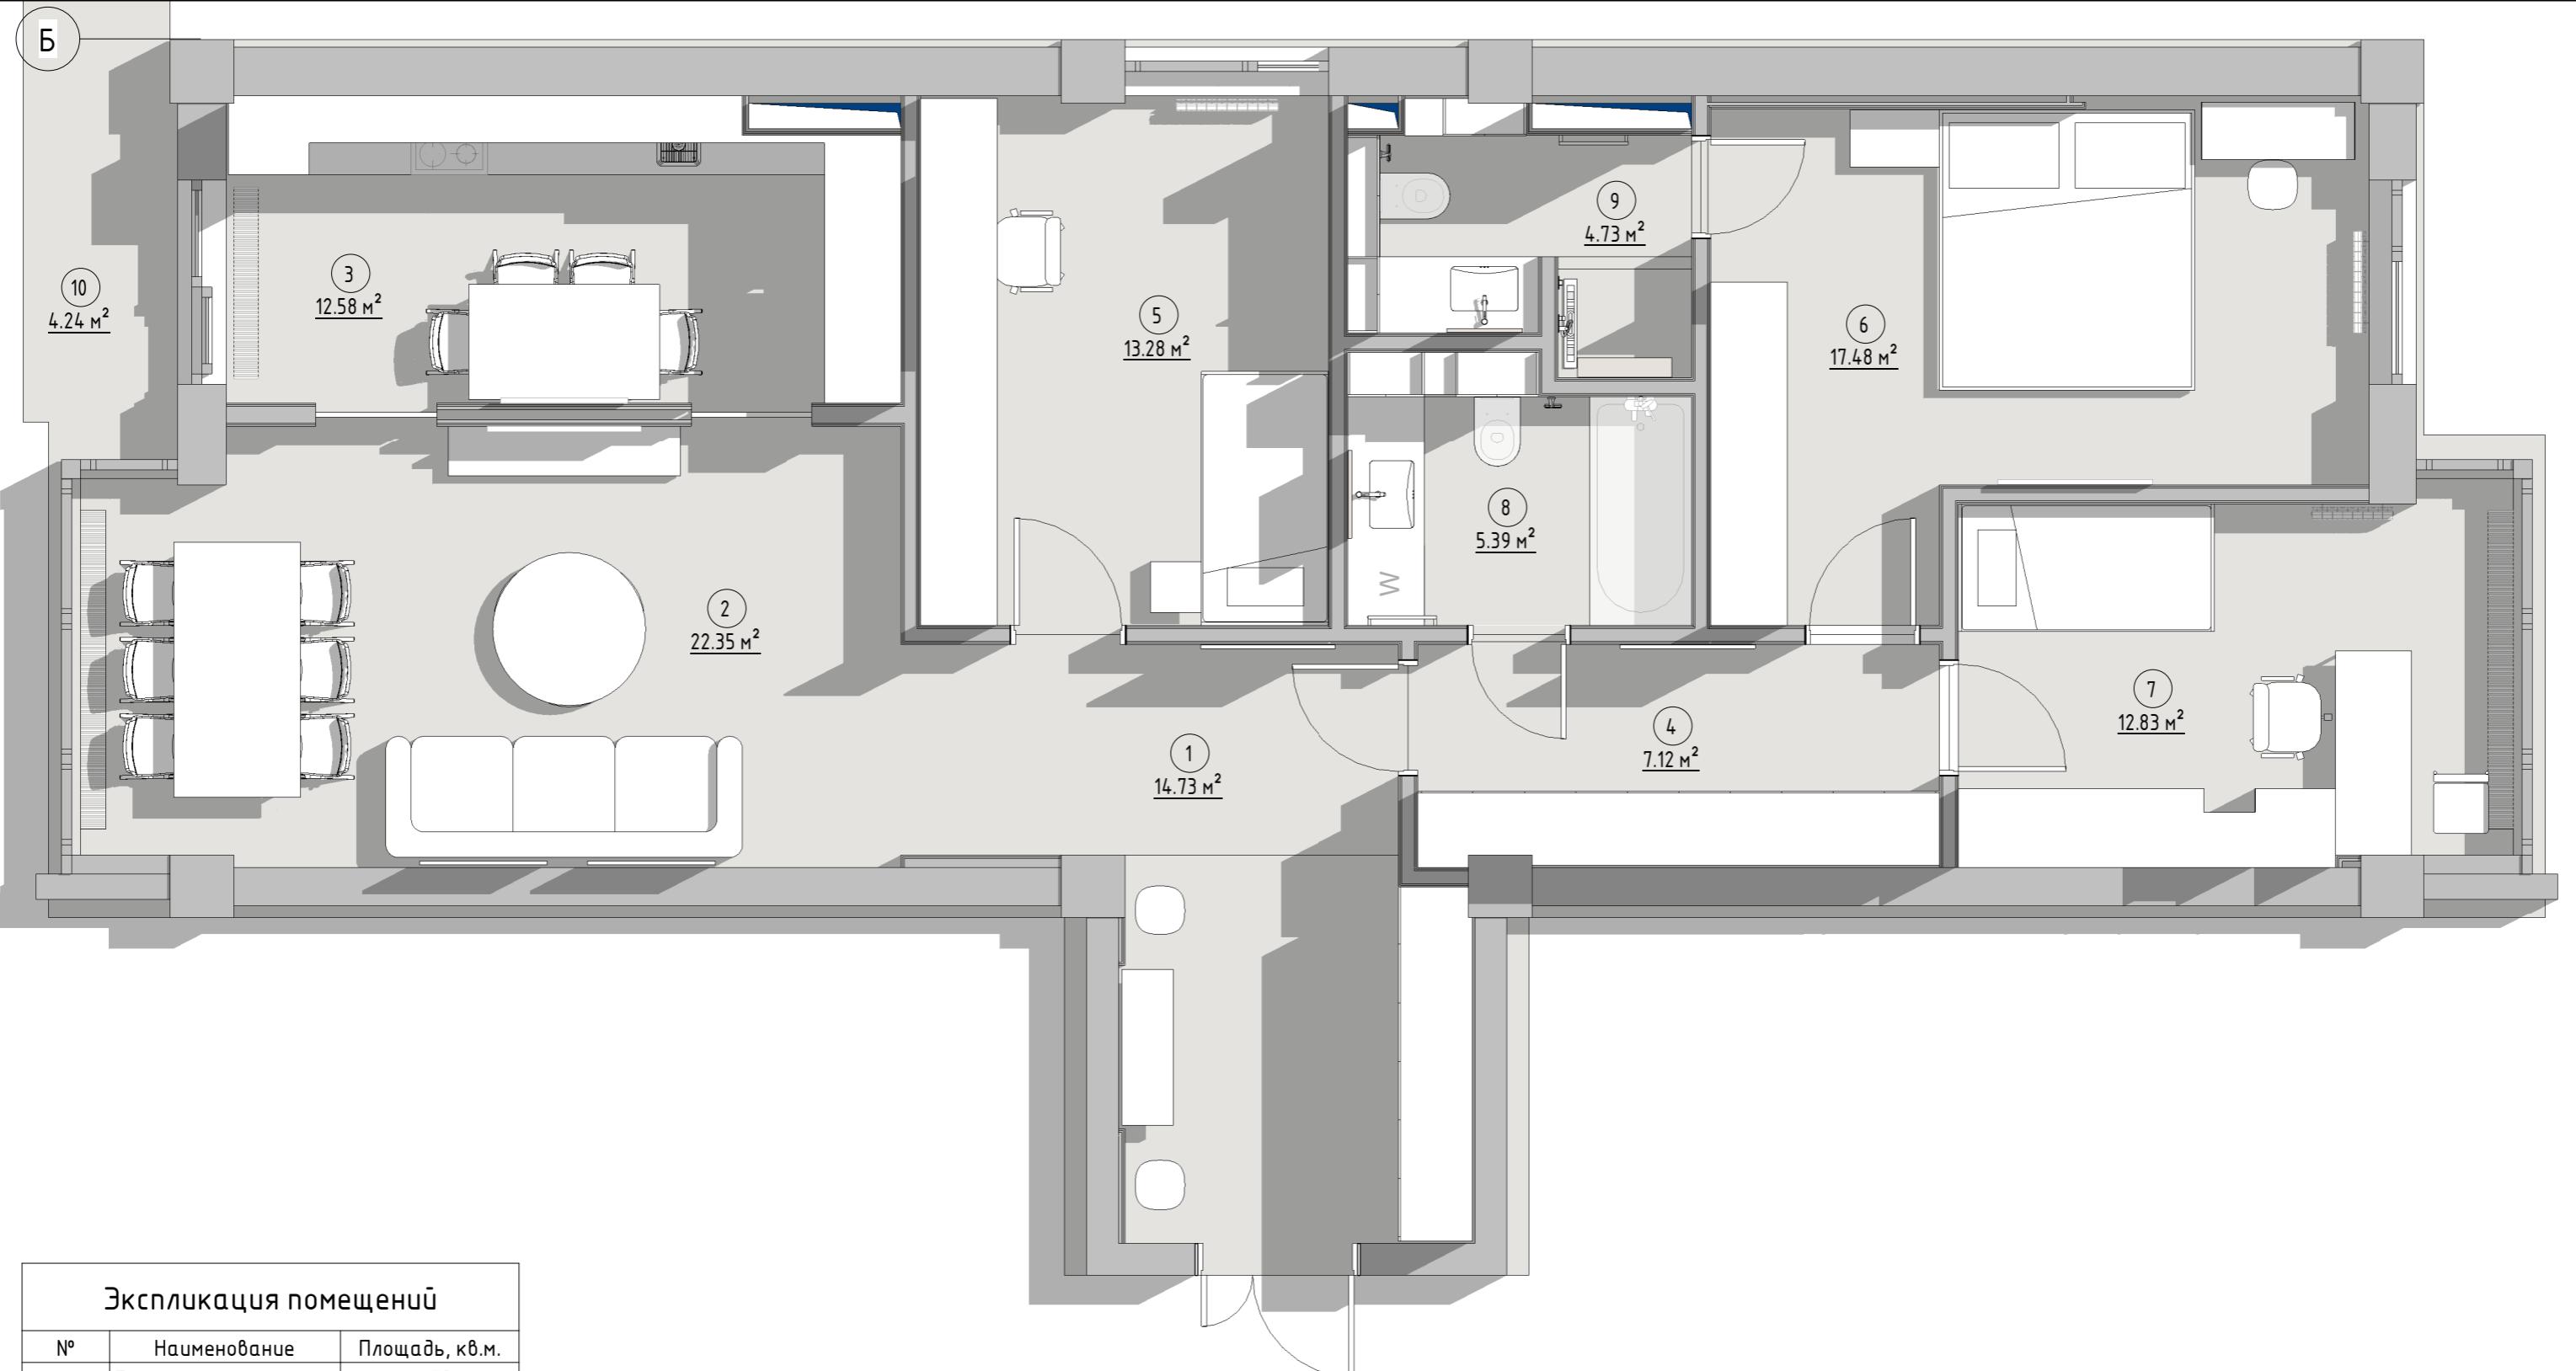


#### Экспликация помещений

№	Наименование	Площадь, кв.м.
1	Прихожая	14.73
2	Гостиная	22.35
3	Кухня	12.58
4	Коридор	7.12
5	Спальня	13.28
6	Спальня	17.48
7	Спальня	12.83
8	Санузел	5.39
9	Санузел	4.73
10	Балкон	4.24
		114.73

Стадия	Лист	Листов
Дизайнер		
Заказчик		
АИ		

ПЛАН РАССТАНОВКИ МЕБЕЛИ

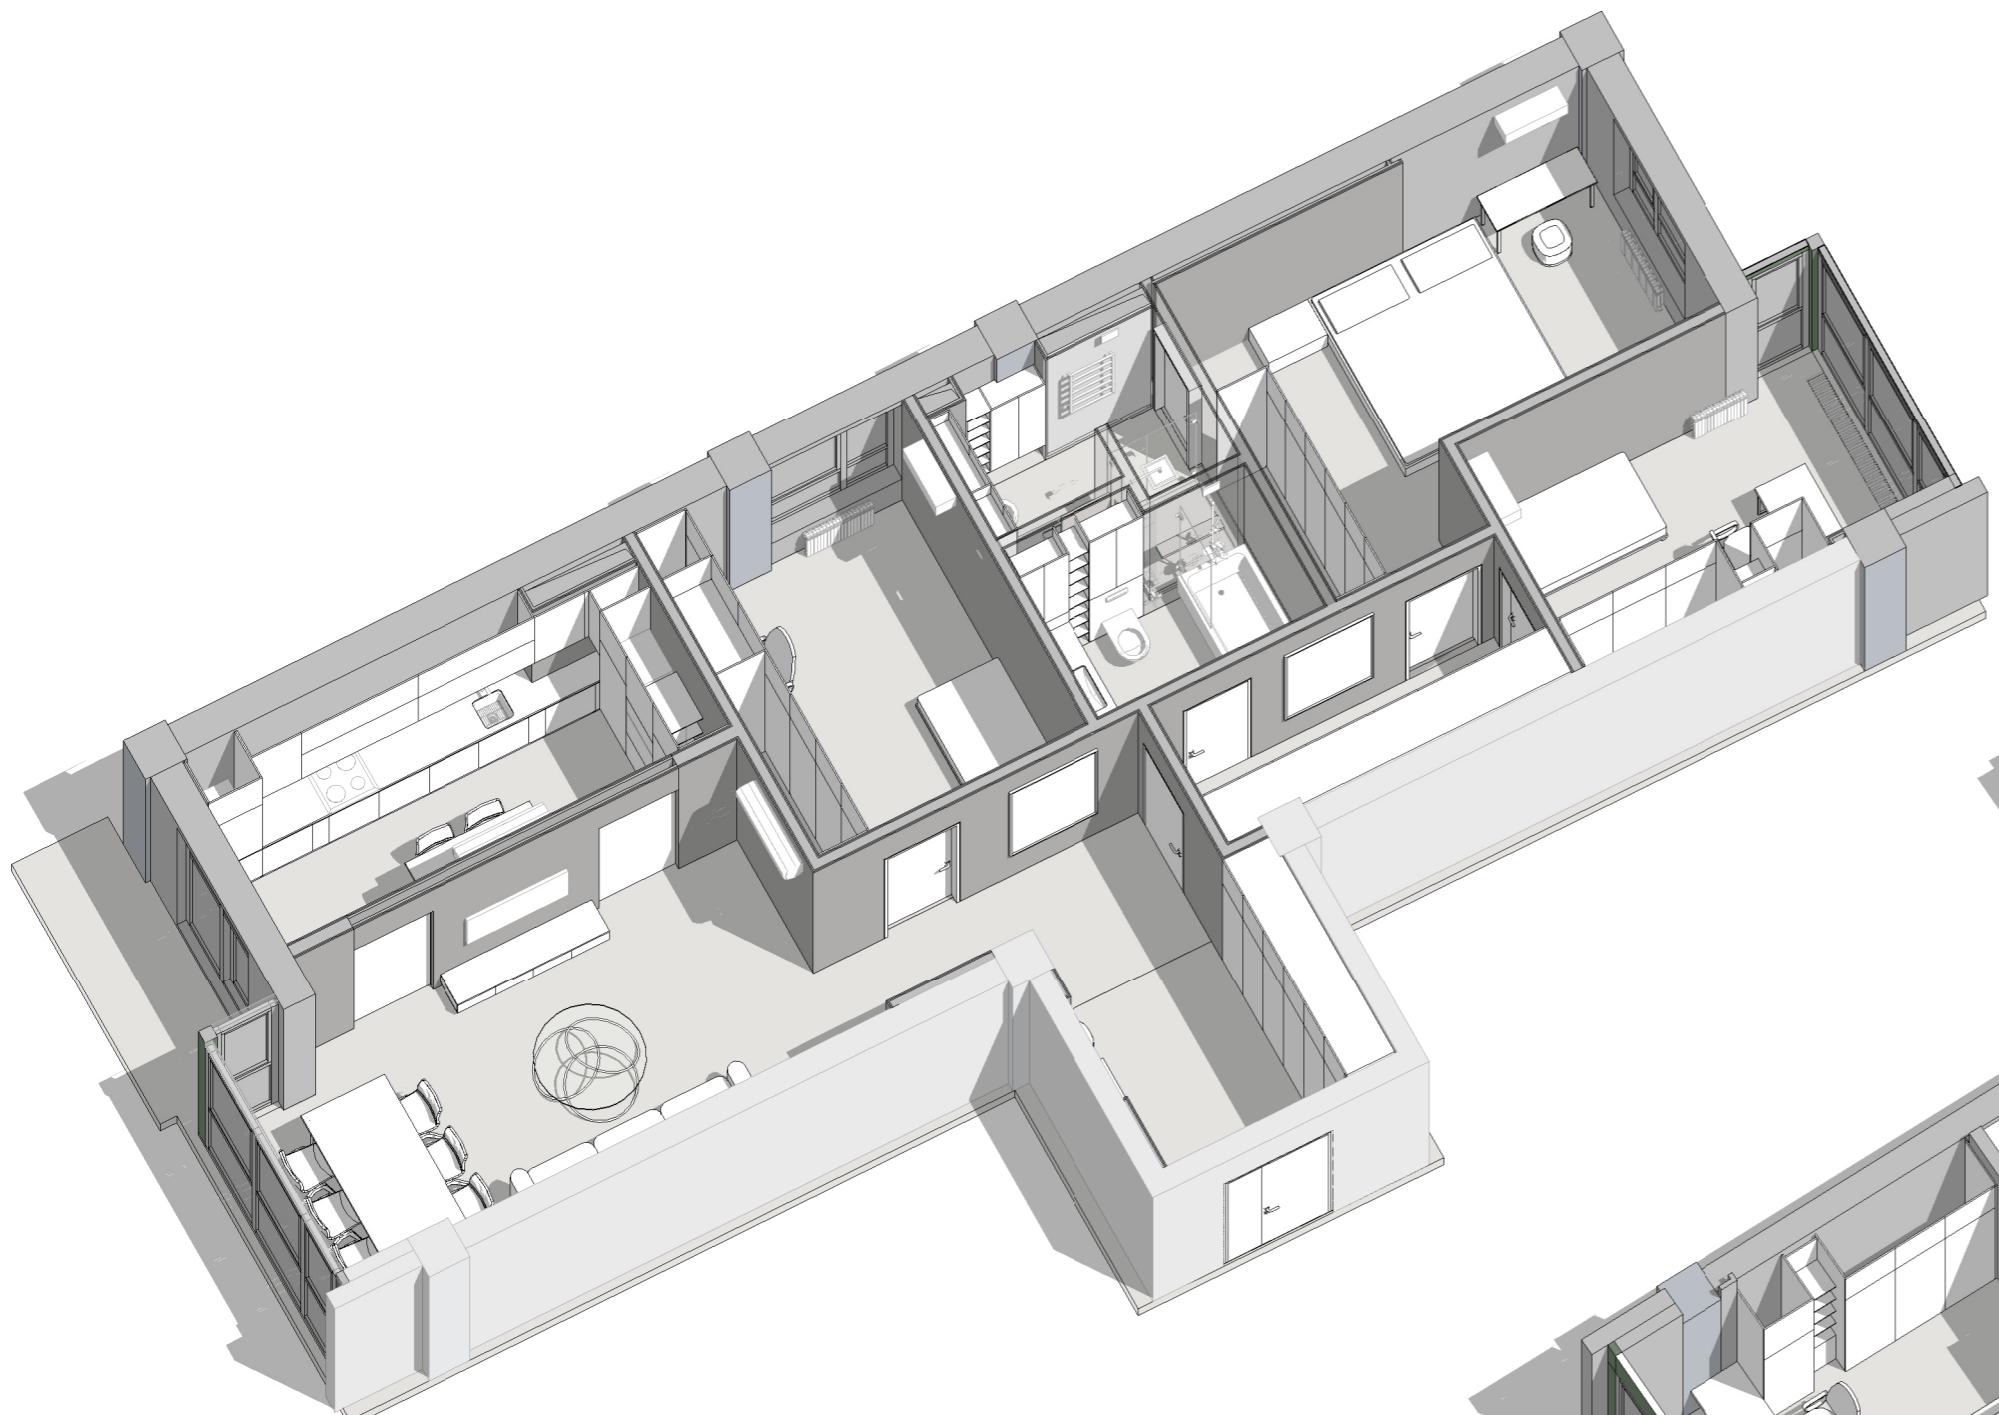

Дизайнер			
Заказчик			


3D ВИД РАССТАНОВКИ  
МЕБЕЛИ

Luxhouse\_studio

Формат: А3

Стадия      Лист      Листов

АИ

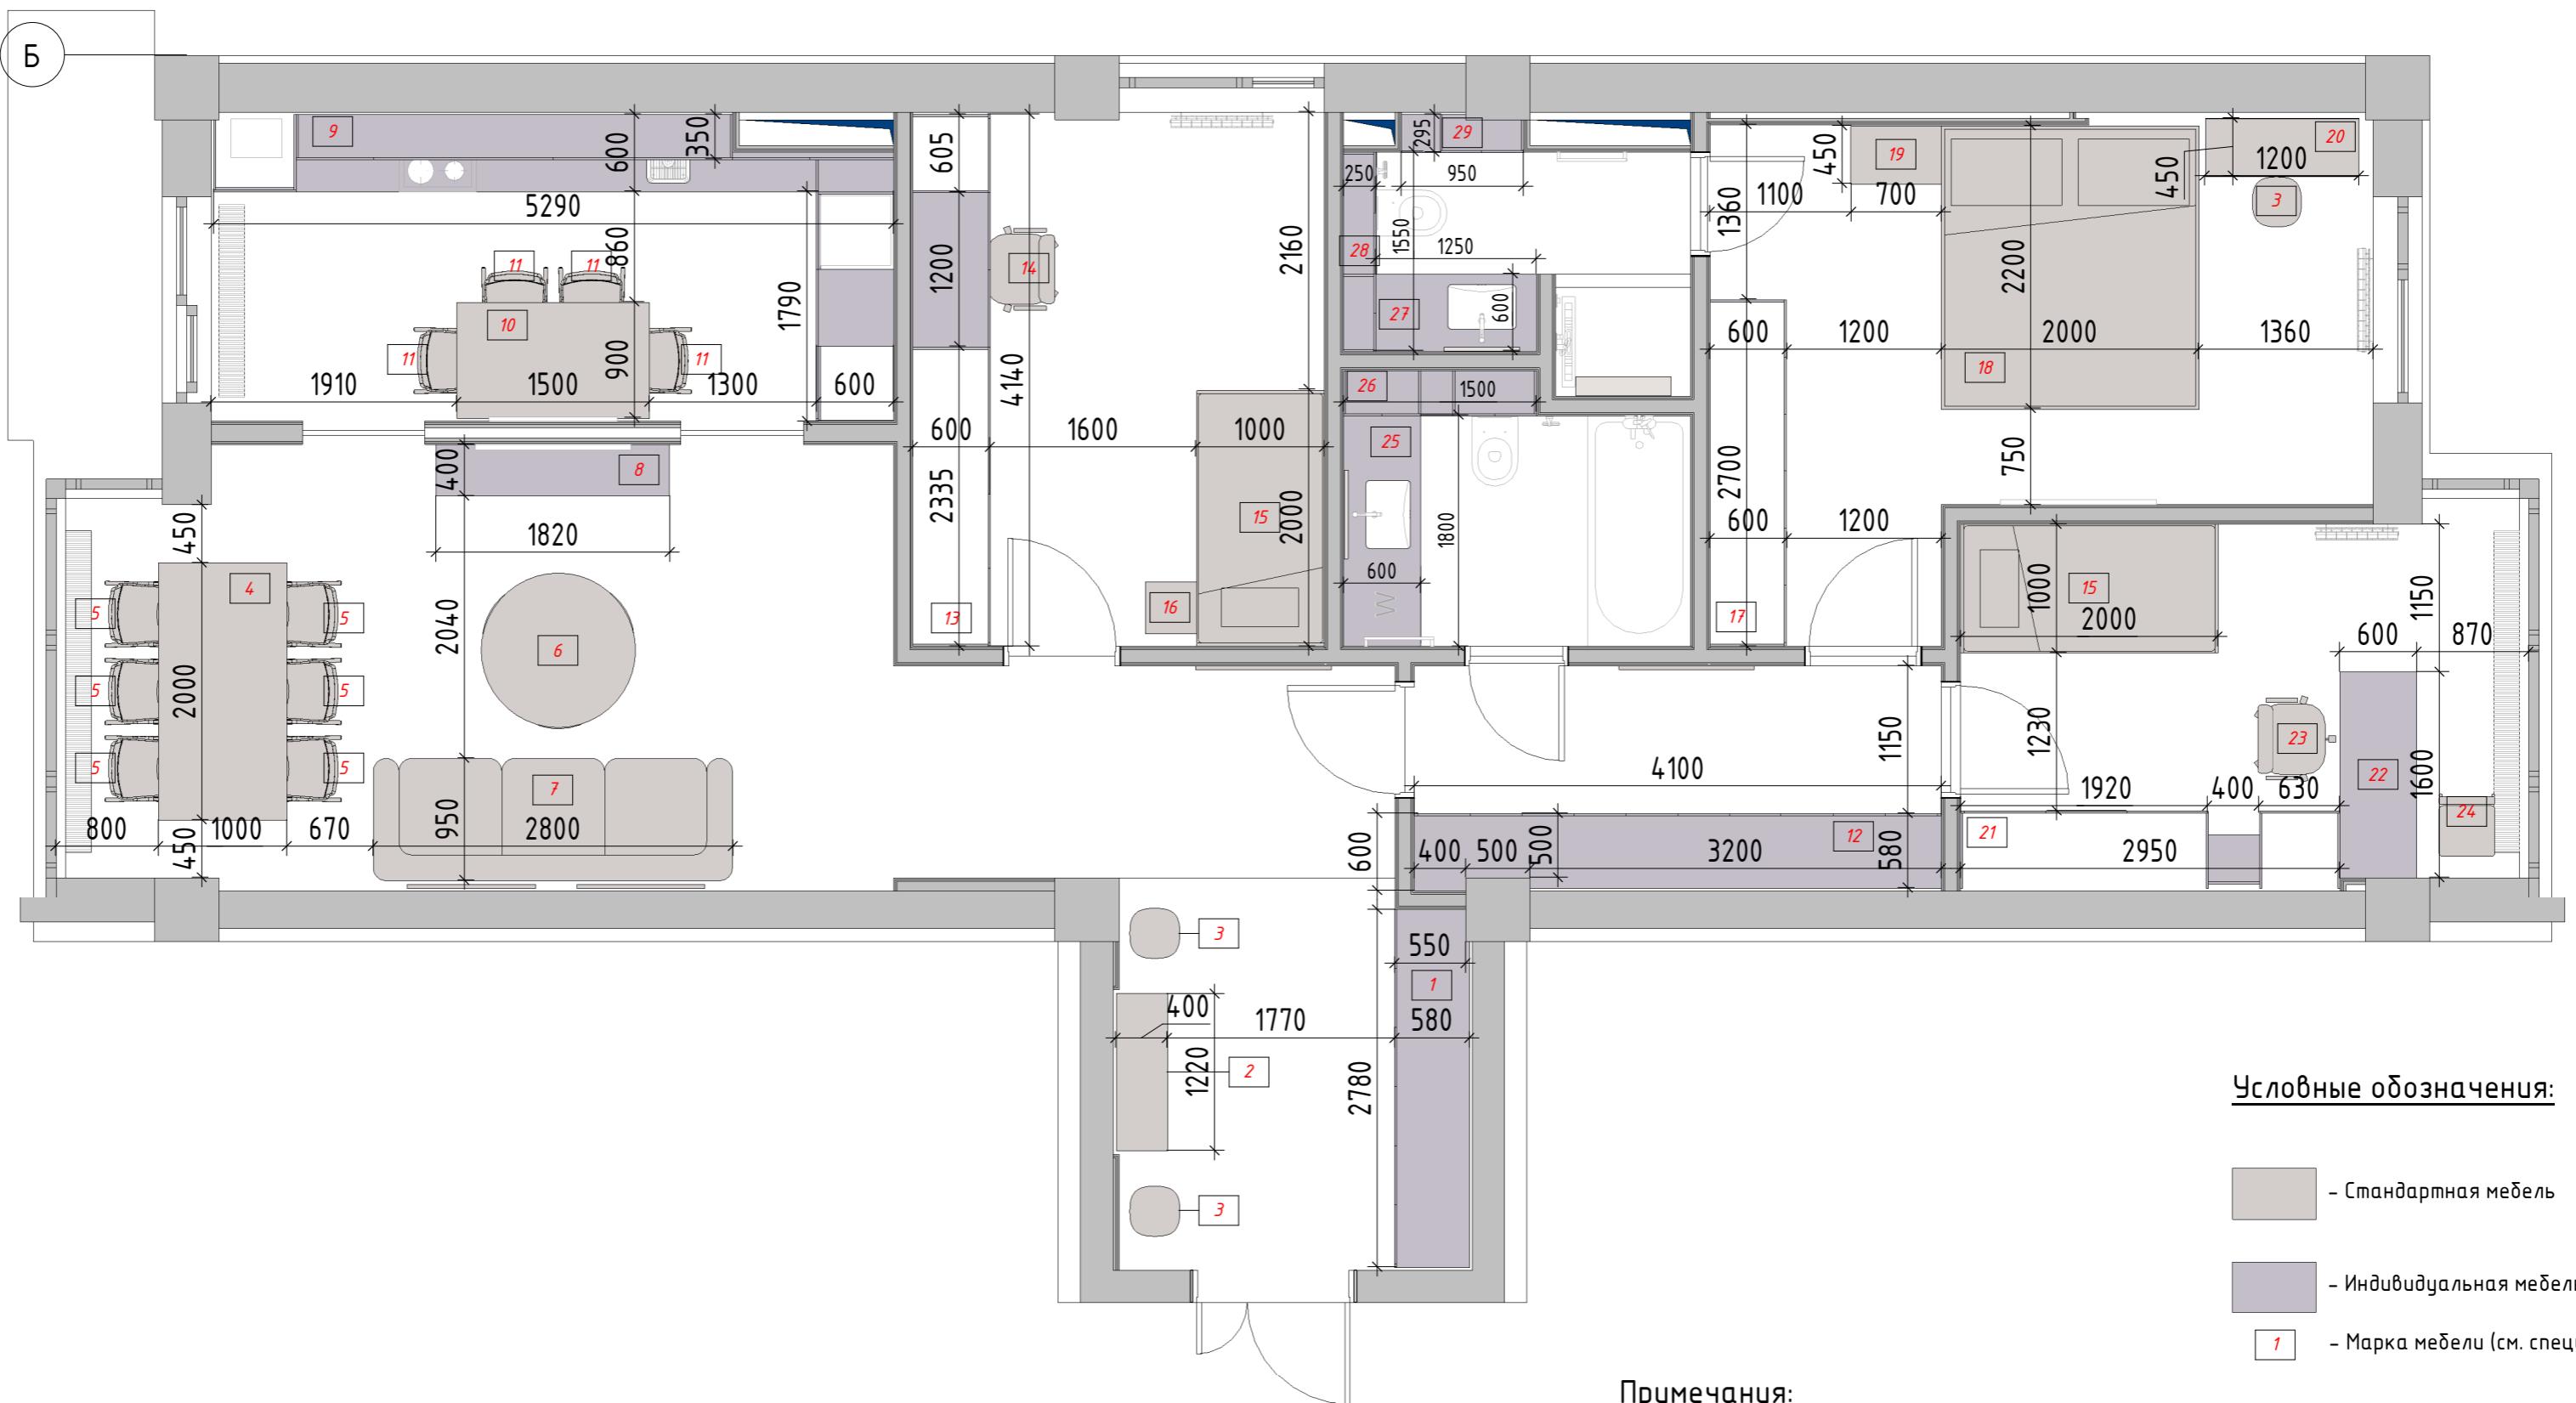

**Примечания:**

- За отметку 0.000 принята отметка чистого пола проектируемых помещений.
- Размеры указаны в миллиметрах.
- Размеры уточнять по месту.
- Смотреть совместно с развертками помещений.

Дизайнер			
Заказчик			


ПЛАН РАССТАНОВКИ МЕБЕЛИ  
С РАЗМЕРАМИ

Luxhouse\_studio


Формат: А3

Стадия	Лист	Листов
AI		


Расположение ВК\_Санузел №8

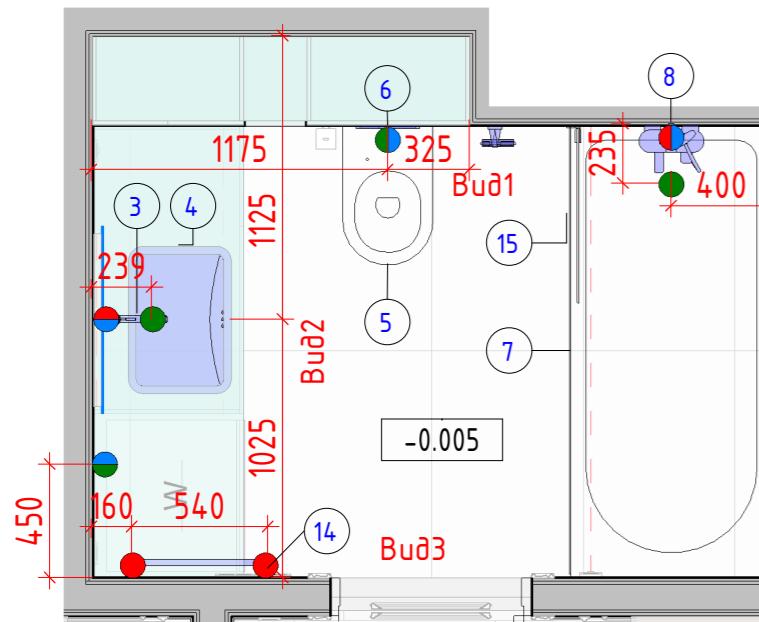


Вид 1

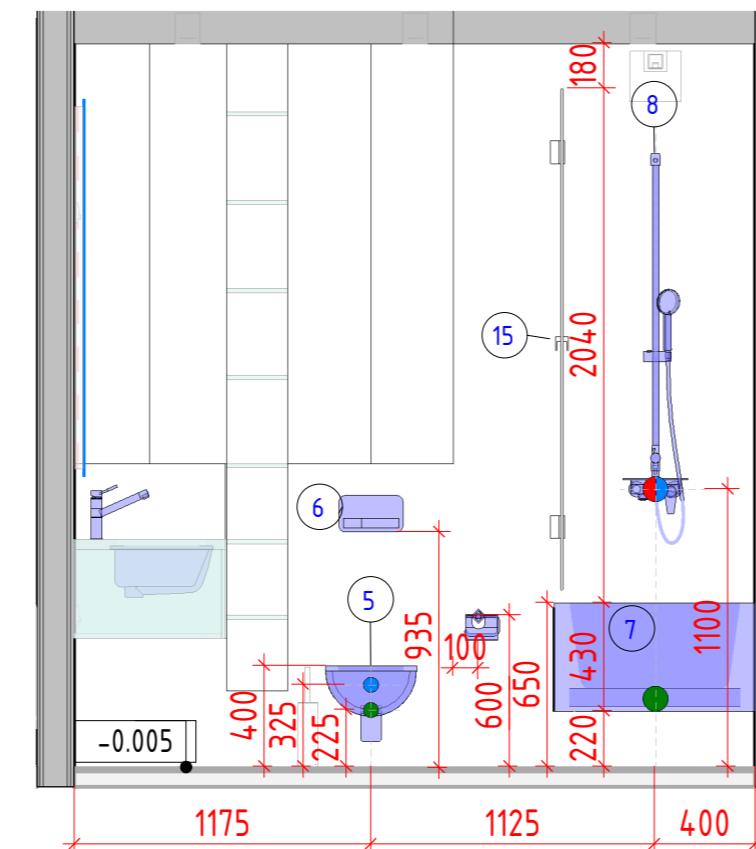



Вид 2

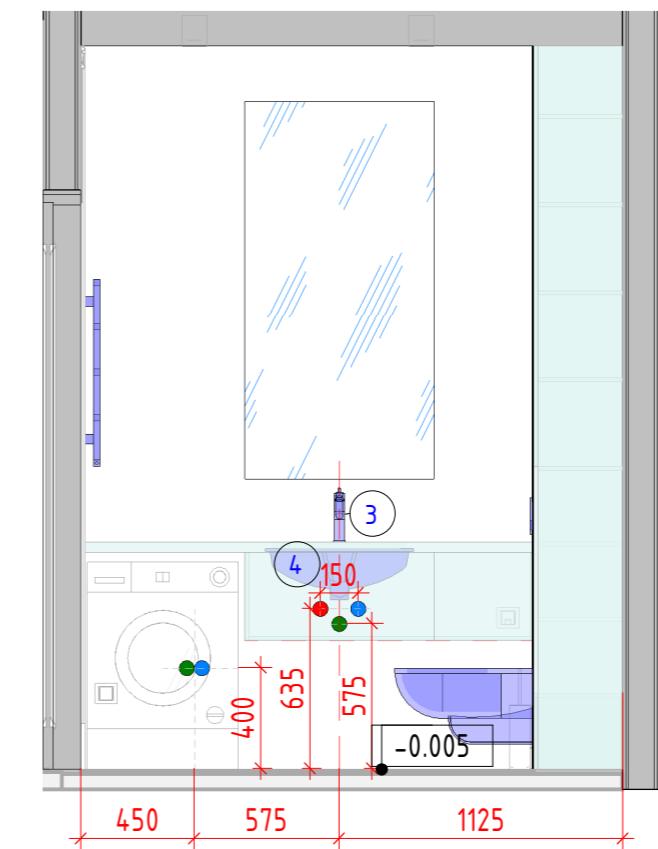

Вид 3

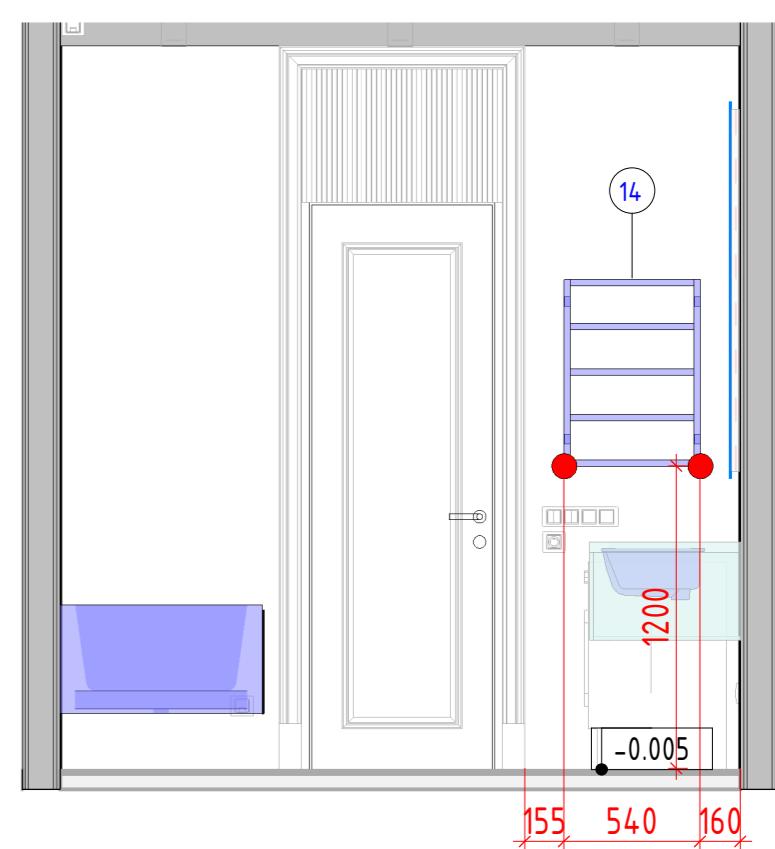

Расположение ВК\_Кухня

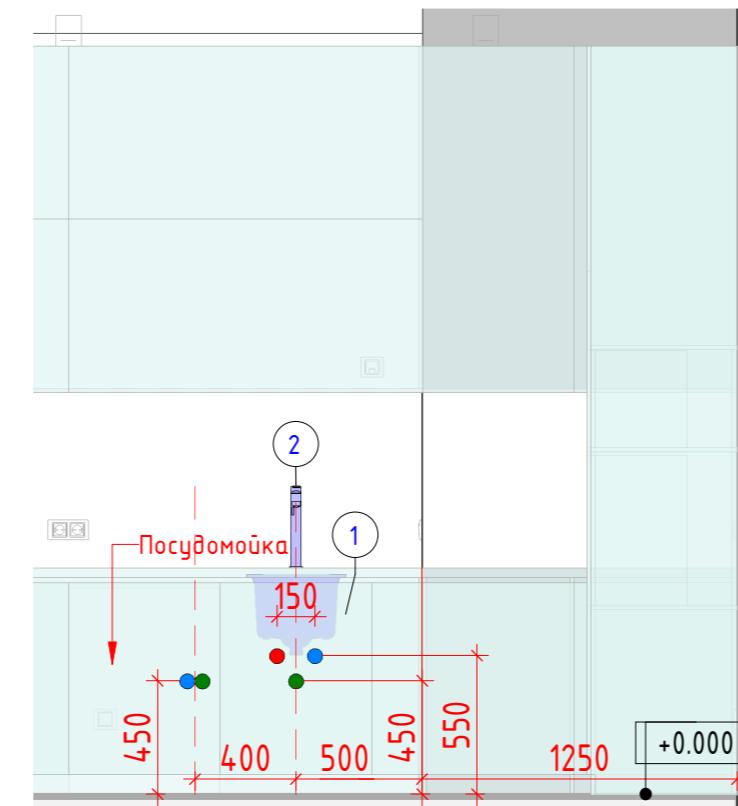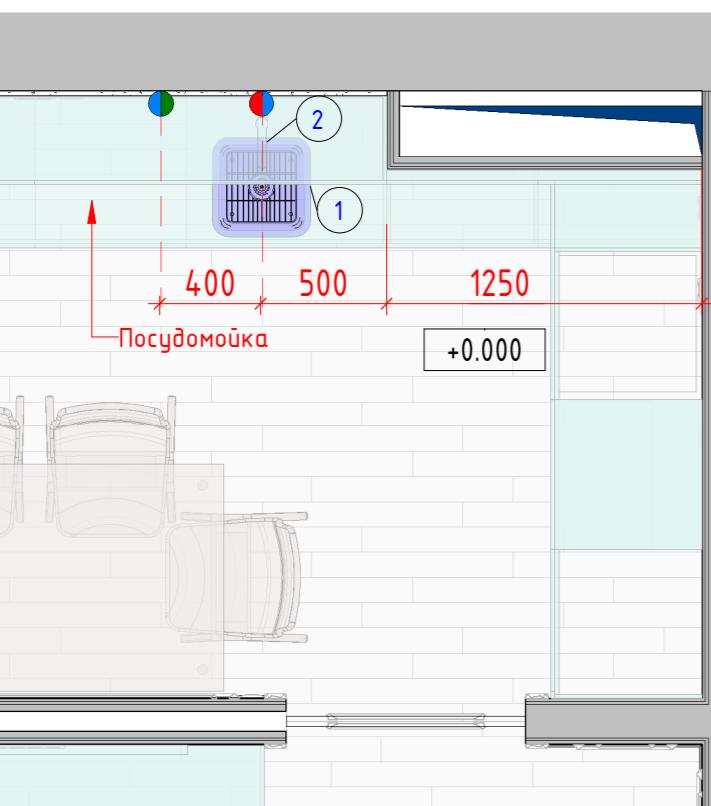

Числовые обозначения:

- ±0.000 — Высотная отметка
- № 150 м2 — Марка помещений
- (1) — Марка сантехнического оборудования
- — Марка сантехнических принадлежностей
- — Холодная вода
- — Горячая вода
- — Канализация


Примечание:

Расстояние между точками крепления полотенцесушителя зависит от выбранной модели


Дизайнер			
Заказчик			

РАСПОЛОЖЕНИЕ ВК КУХНЯ  
И САНУЗЕЛ


Расположение ВК\_Санузел №9

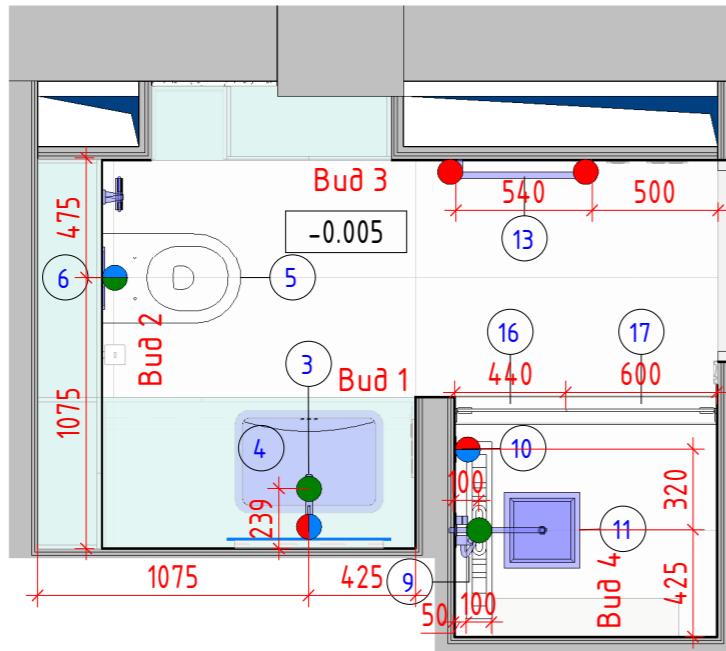



Вид 2

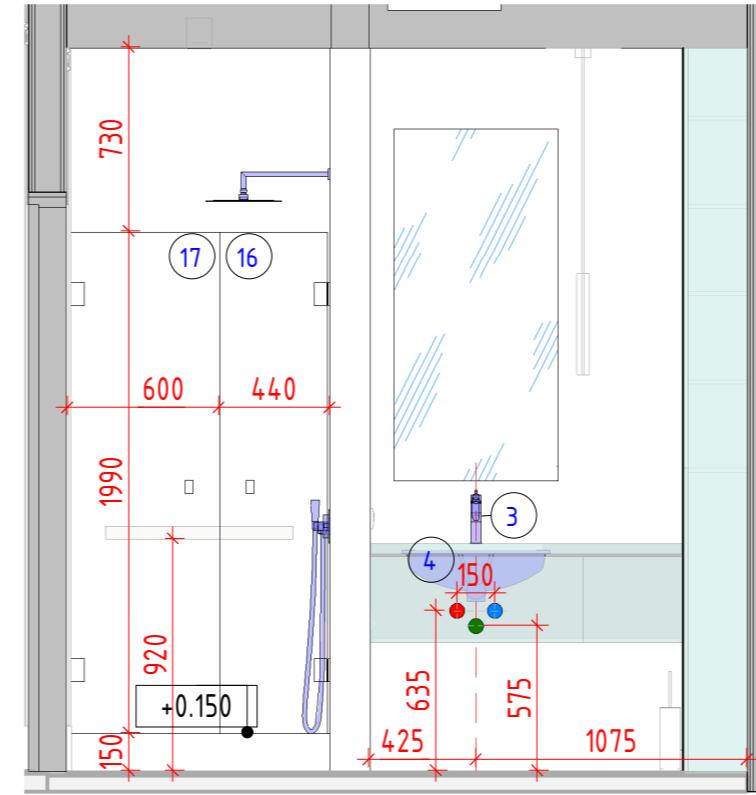

Вид 1

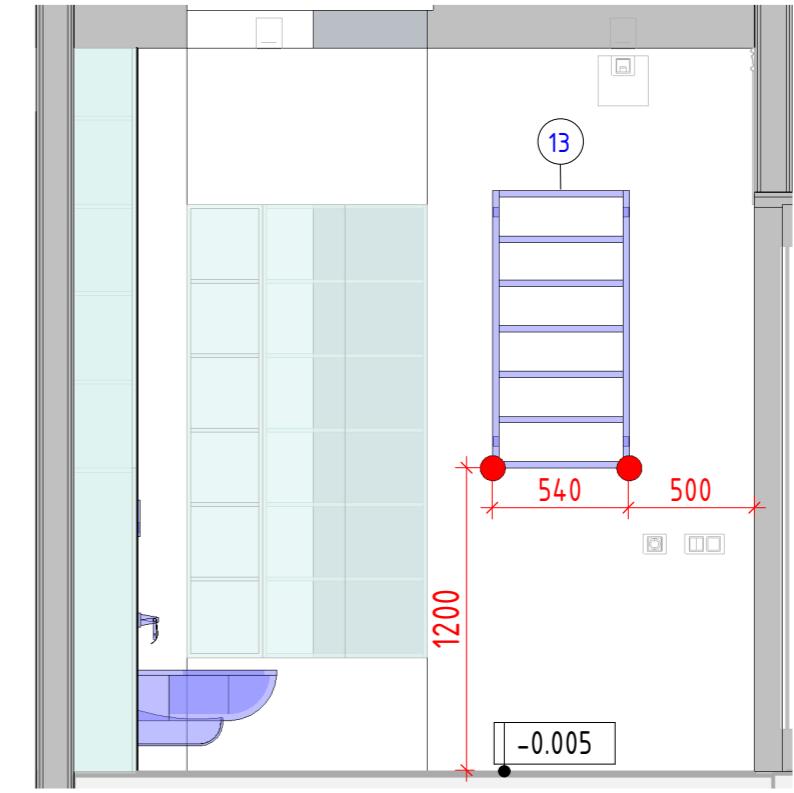

Вид 3

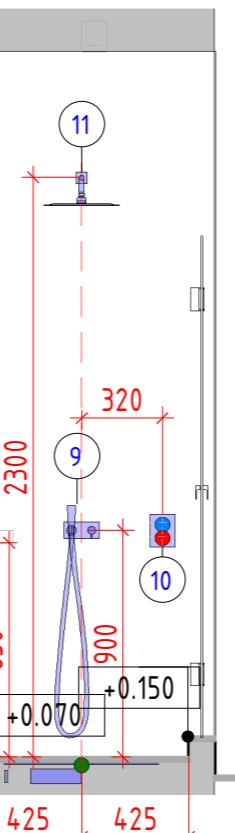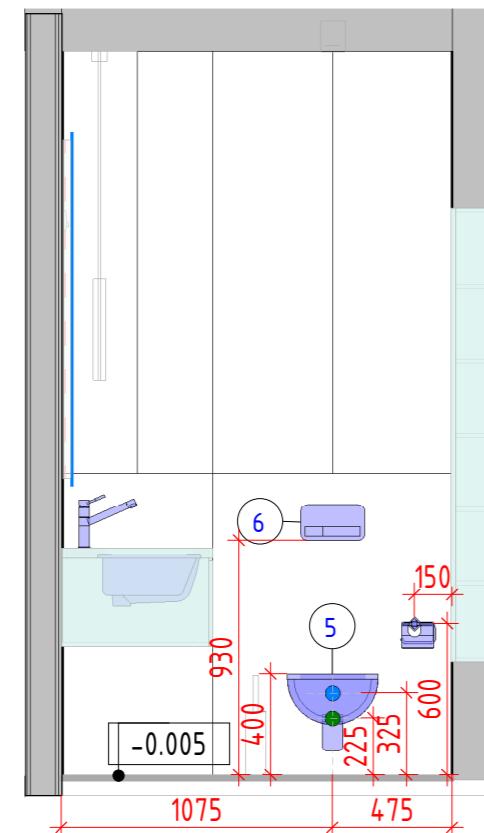

Вид 4

Черновые обозначения:

- $\pm 0.000$  — Высотная отметка
- № 150 м<sup>2</sup> — Марка помещений
- (1) — Марка сантехнического оборудования
- т1 — Марка сантехнических принадлежностей
- — Холодная вода
- — Горячая вода
- — Канализация

Примечание:


Расстояние между точками крепления полотенцесушителя зависит от выбранной модели

Дизайнер			
Заказчик			

Стадия	Лист	Листов
АИ		

РАСПОЛОЖЕНИЕ ВК КУХНЯ  
И САНУЗЕЛ


Luxhouse\_studio

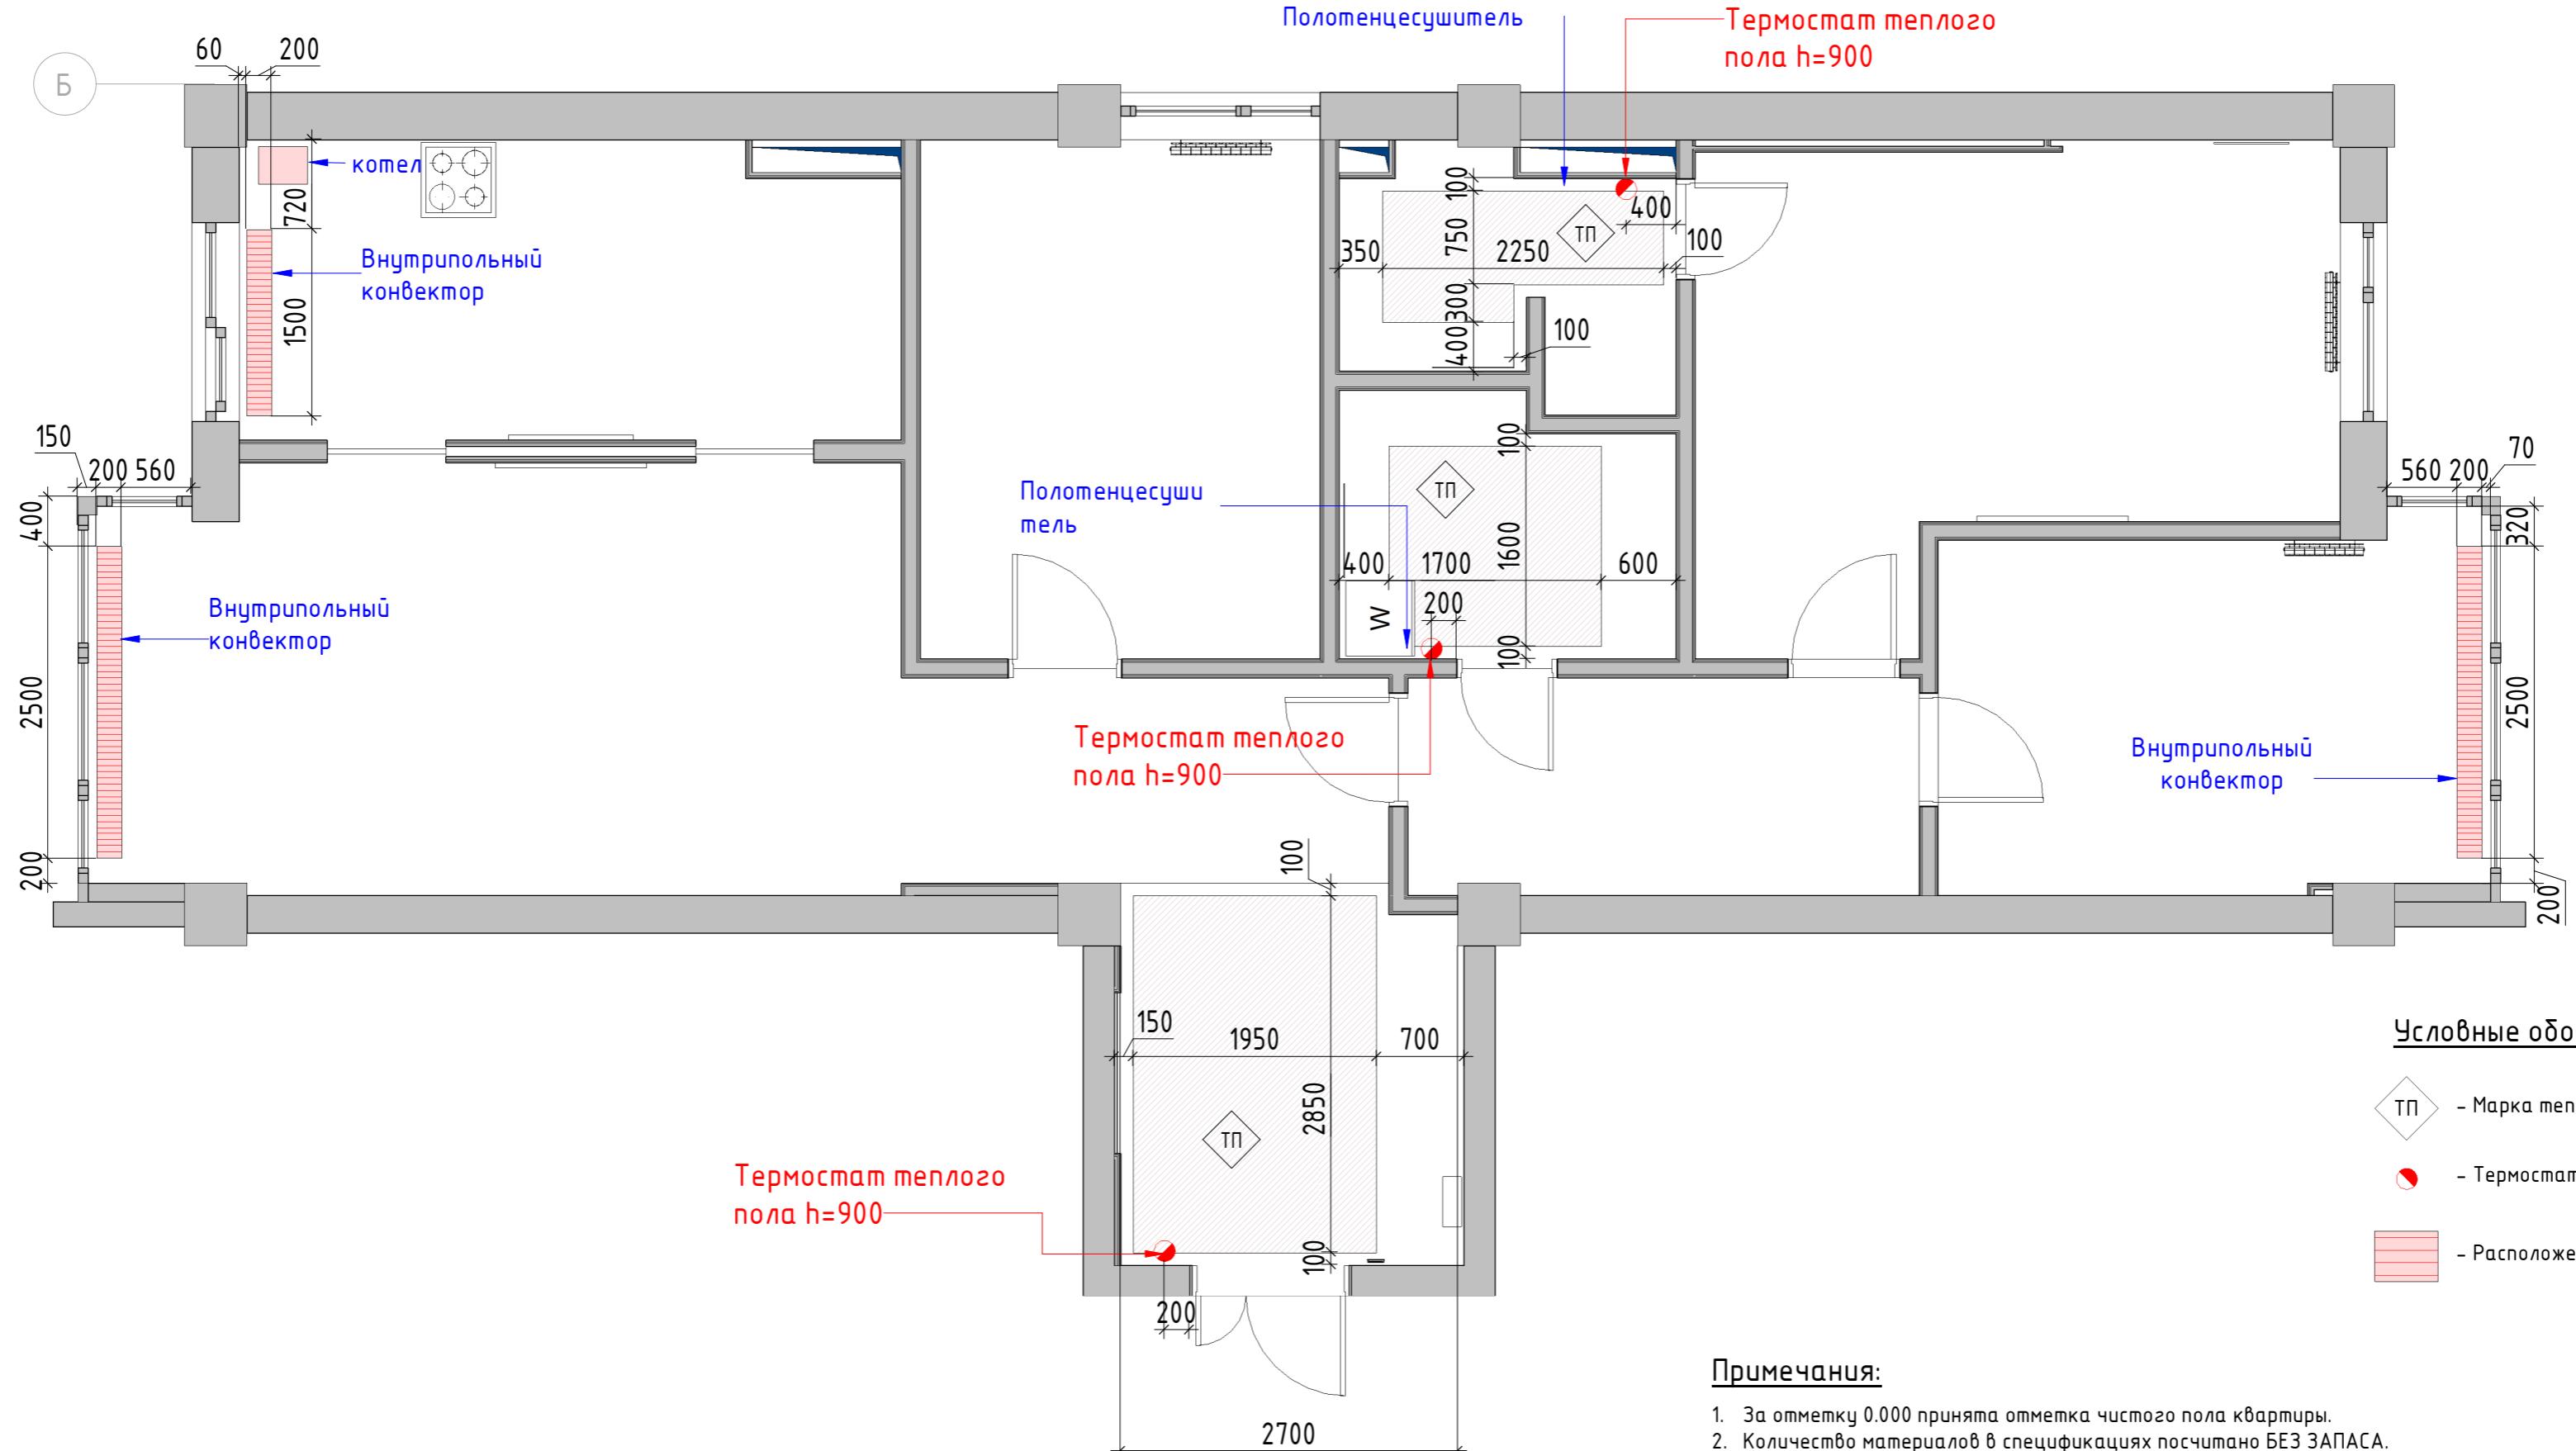


## Примечания:

1. За отметку 0.000 принята отметка чистого пола квартиры.
  2. Количество материалов в спецификациях посчитано БЕЗ ЗАПАСА.
  3. Все размеры уточняются по месту.
  4. Модель отопительных оборудований и разводок смотреть раздел ОВ

### Числовые обозначения:

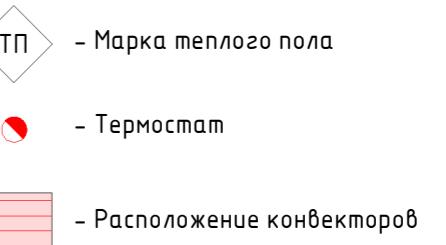

Стадия	Лист	Листов
АИ		
ПЛАН ОТОПЛЕНИЯ		
Luxhouse_studio		

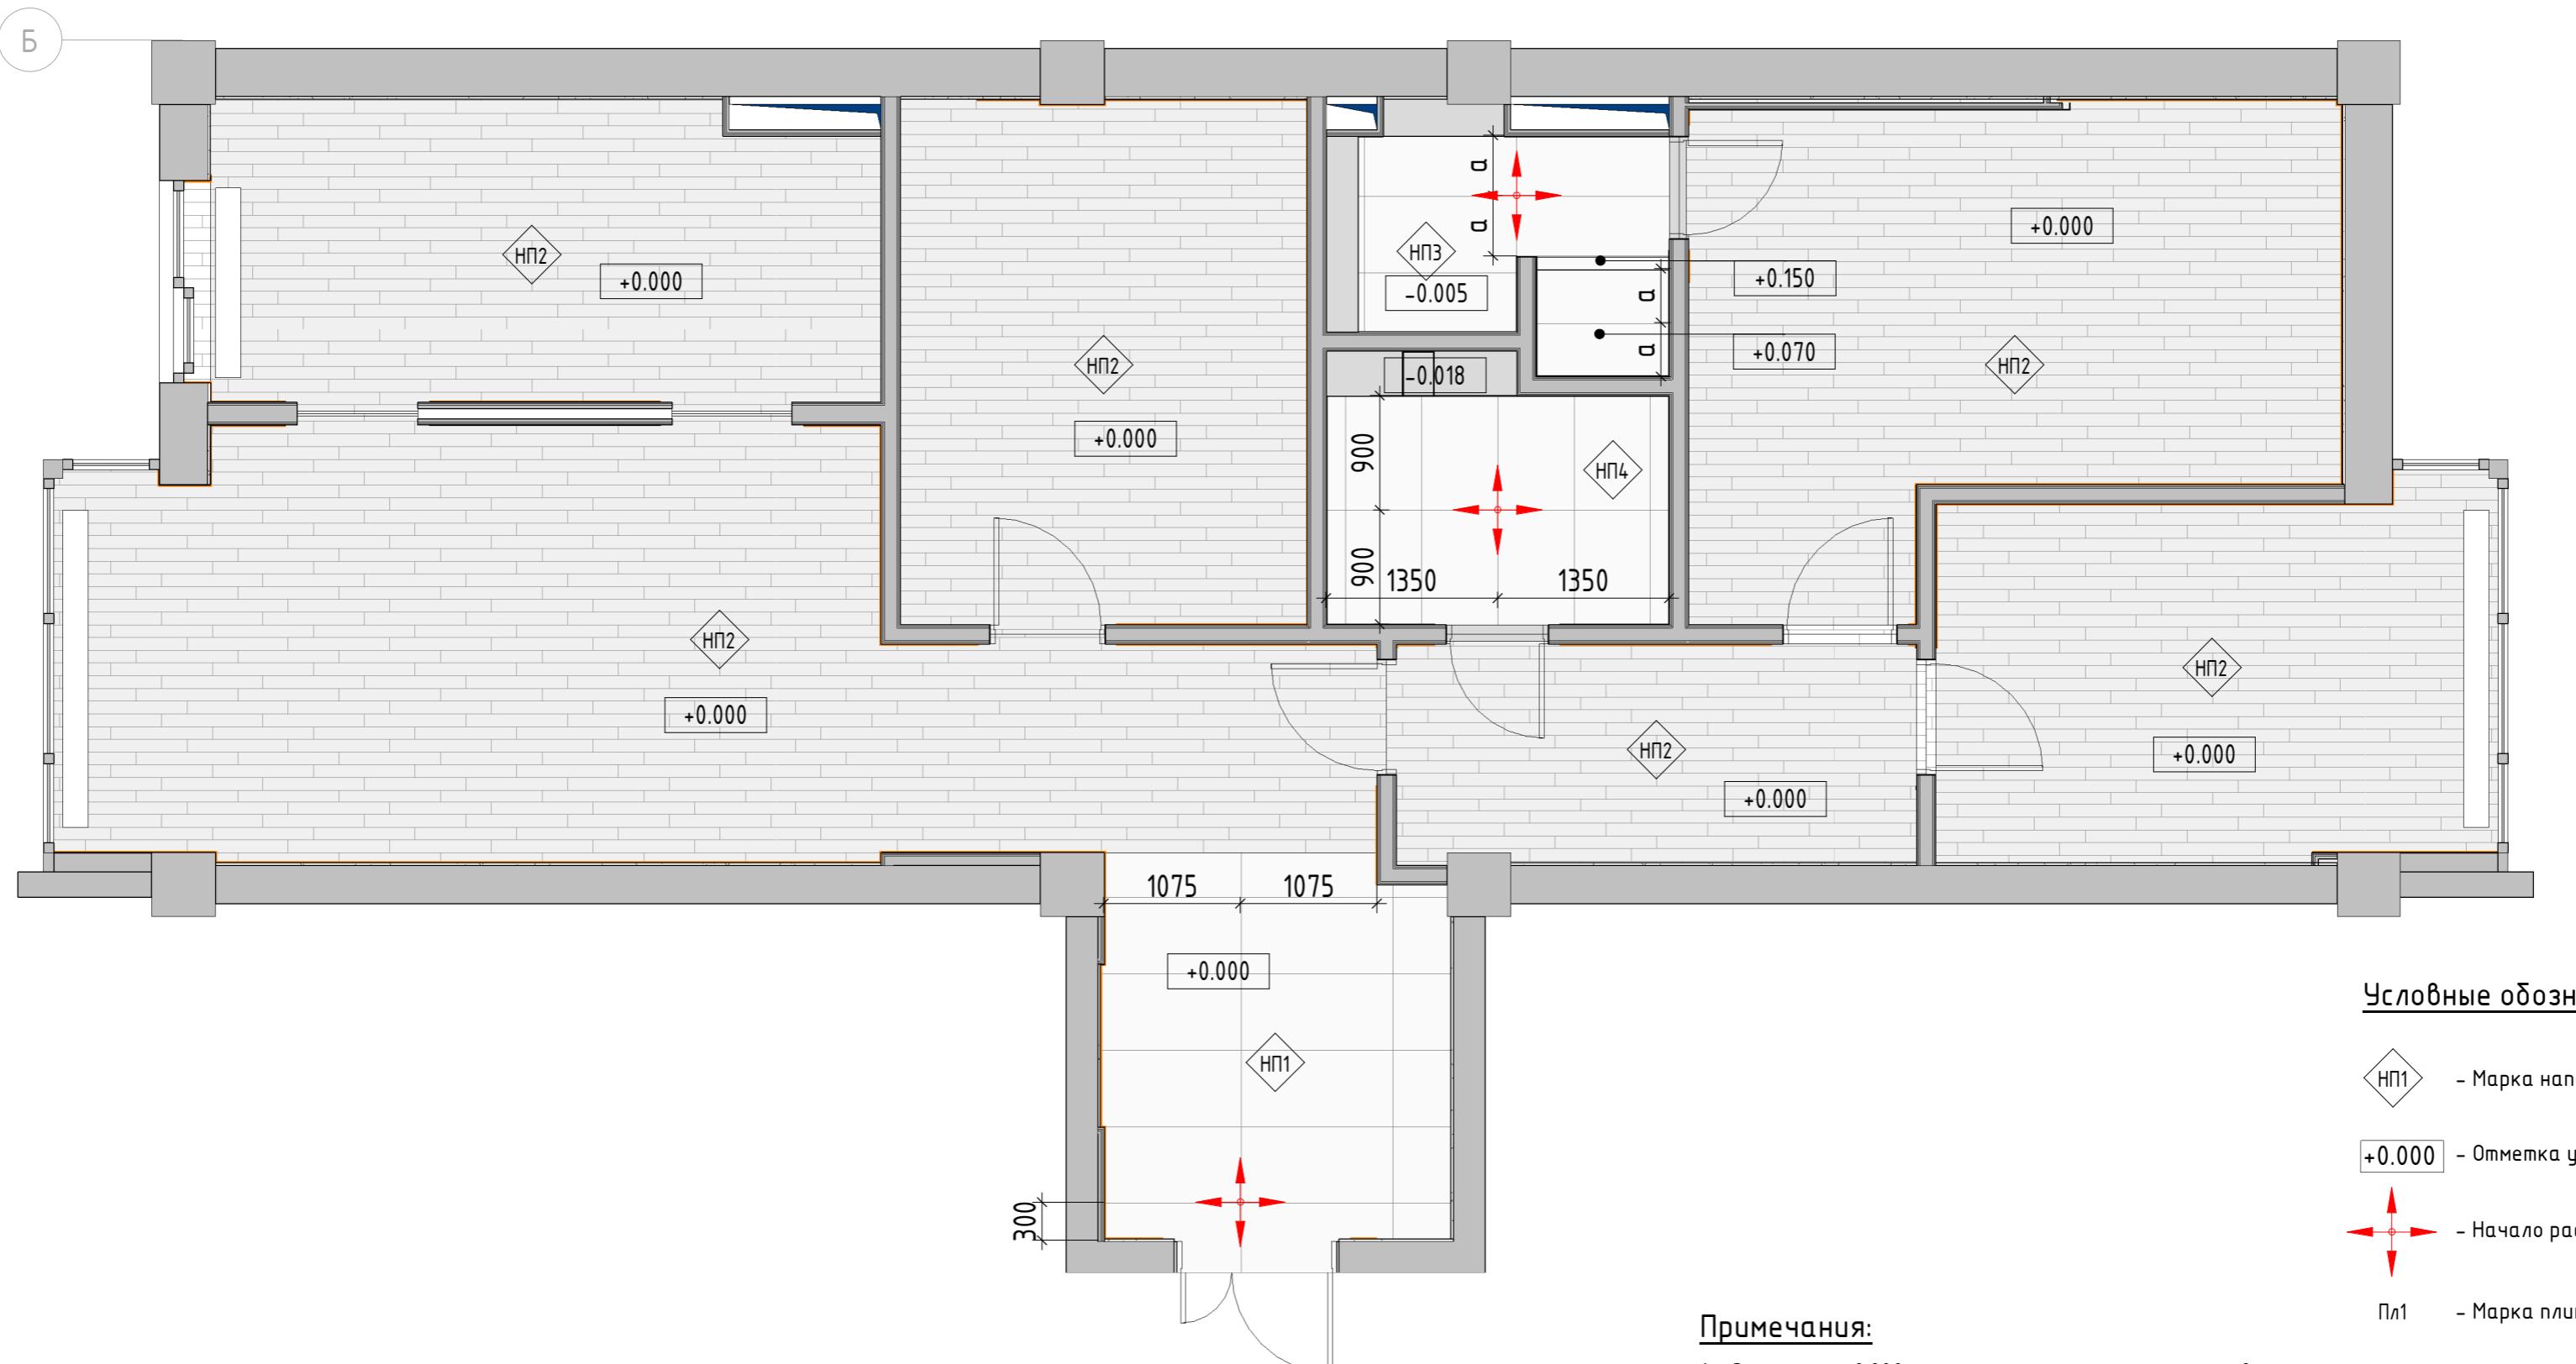

Примечания:



- За отметку 0.000 принята отметка чистого пола квартиры.
- Количество материалов в спецификациях посчитано БЕЗ ЗАПАСА.
- Все размеры уточняются по месту.
- Стыки разных типов покрытий должны производиться под полотном двери (по оси дверного полотна).

Дизайнер			
Заказчик			

ПЛАН НАПОЛЬНЫЙ ПОКРЫТИЙ

Стадия	Лист	Листов
АИ		

Luxhouse\_studio

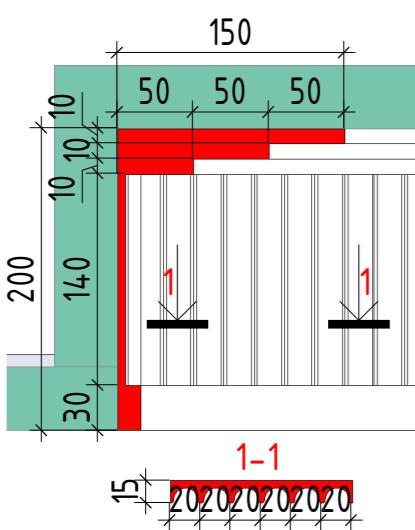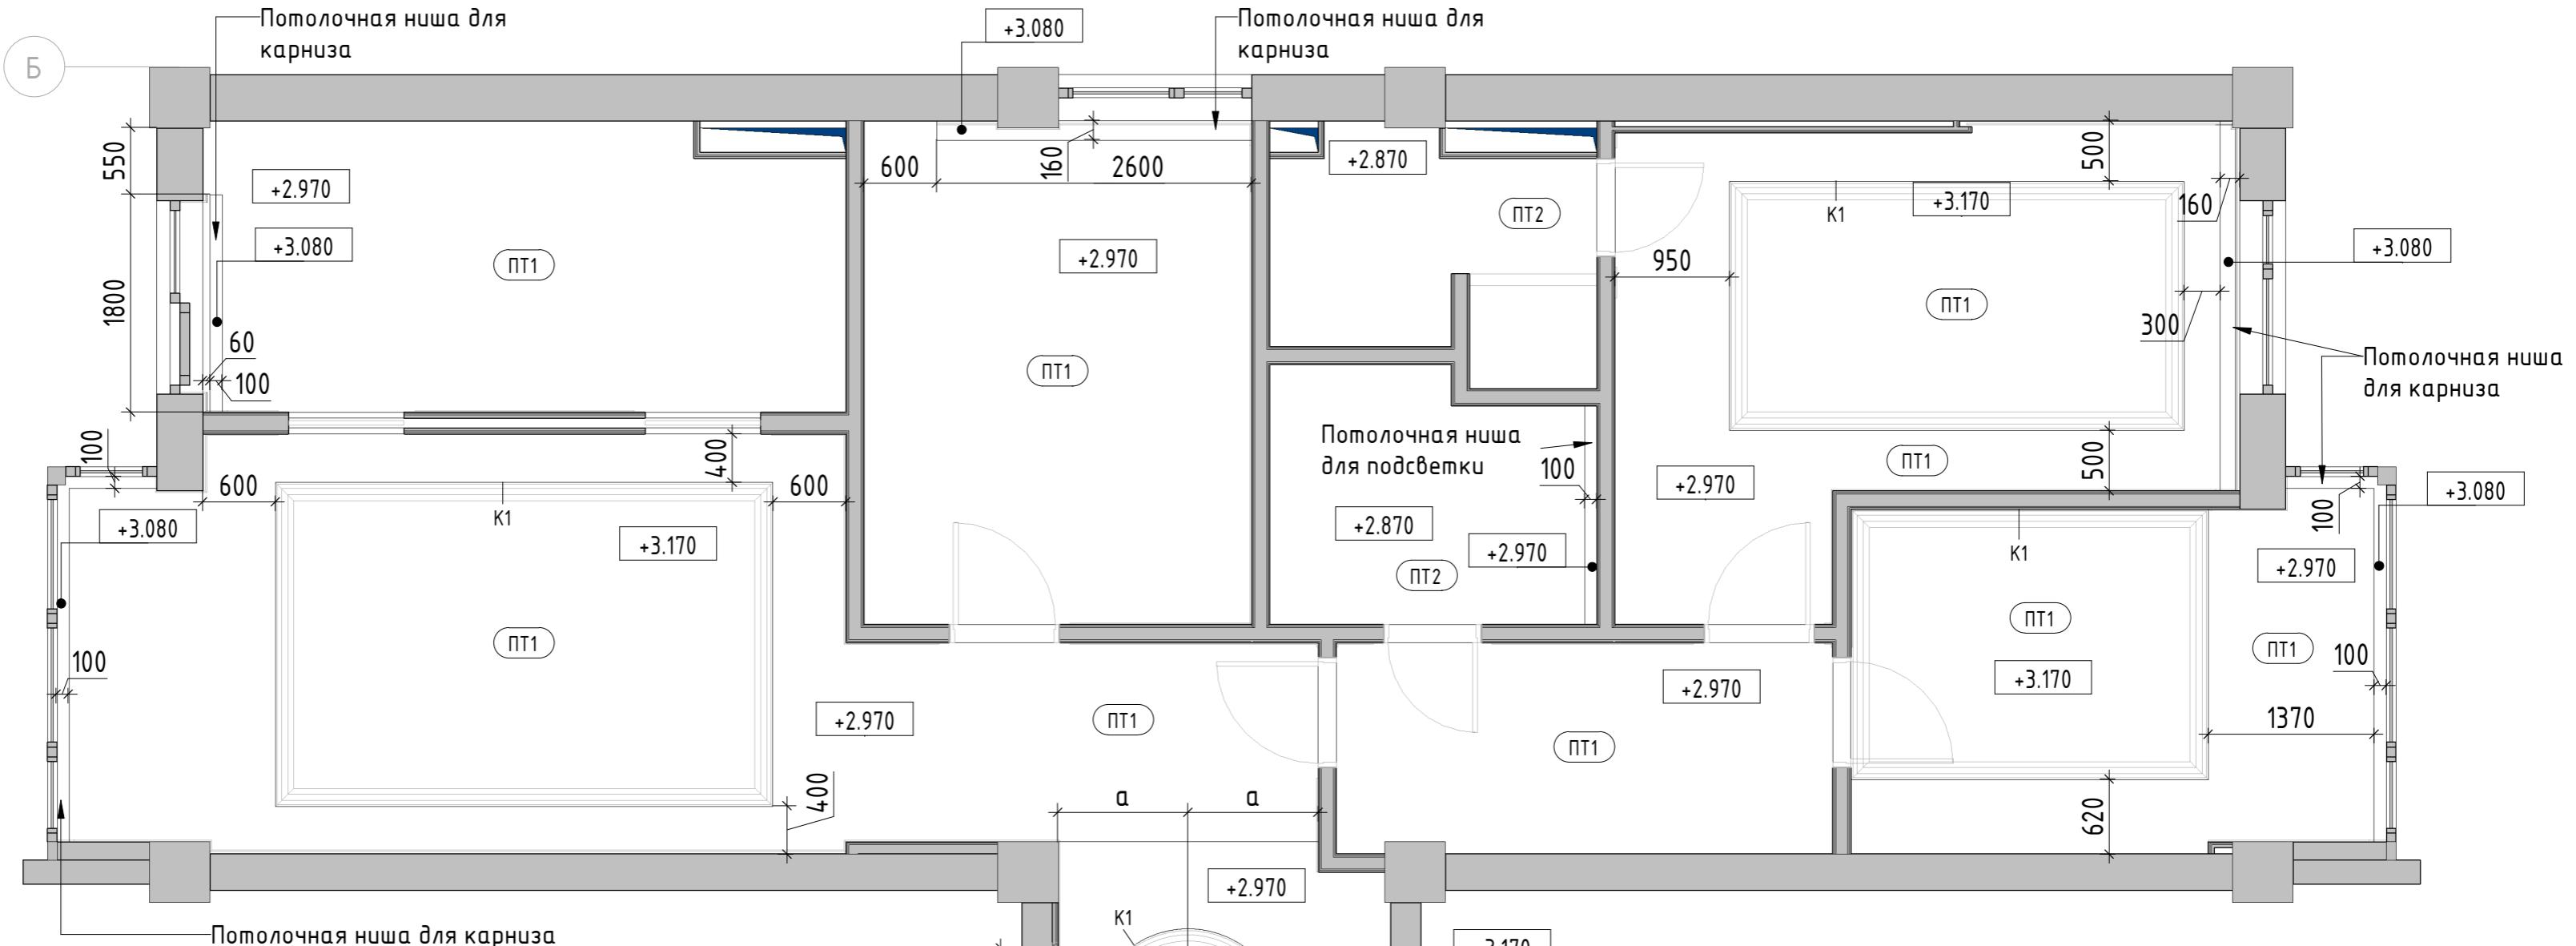

Technical drawing of a window frame with dimensions and annotations:

- Overall height: 350 mm
- Left vertical panel height: 240 mm
- Bottom horizontal panel height: 110 mm
- Left vertical panel thickness: 60 mm
- Bottom horizontal panel thickness: 40 mm
- Top horizontal panel thickness: 40 mm
- Right vertical panel thickness: 40 mm
- Bottom horizontal panel width: 110 mm
- Left vertical panel width: 40 mm
- Top horizontal panel width: 40 mm
- Right vertical panel width: 40 mm
- Overall width: +2,970 mm
- Annotation: ГКЛ 1 слой/Покраска (GKL 1 layer/Painting)
- Annotation: Карниз для штор (Curtain rail)
- Annotation: Сущ.пере (Actual position)


## Числовые обозначения:

1. За отметку 0.000 принятая отметка чистого пола квартиры.
  2. Количество материалов в спецификациях посчитано БЕЗ ЗАПАСА.
  3. Все размеры уточняются по месту.

Дизайнер			
Заказчик			

## Примечания:

ПЛАН ПОТОЛКА

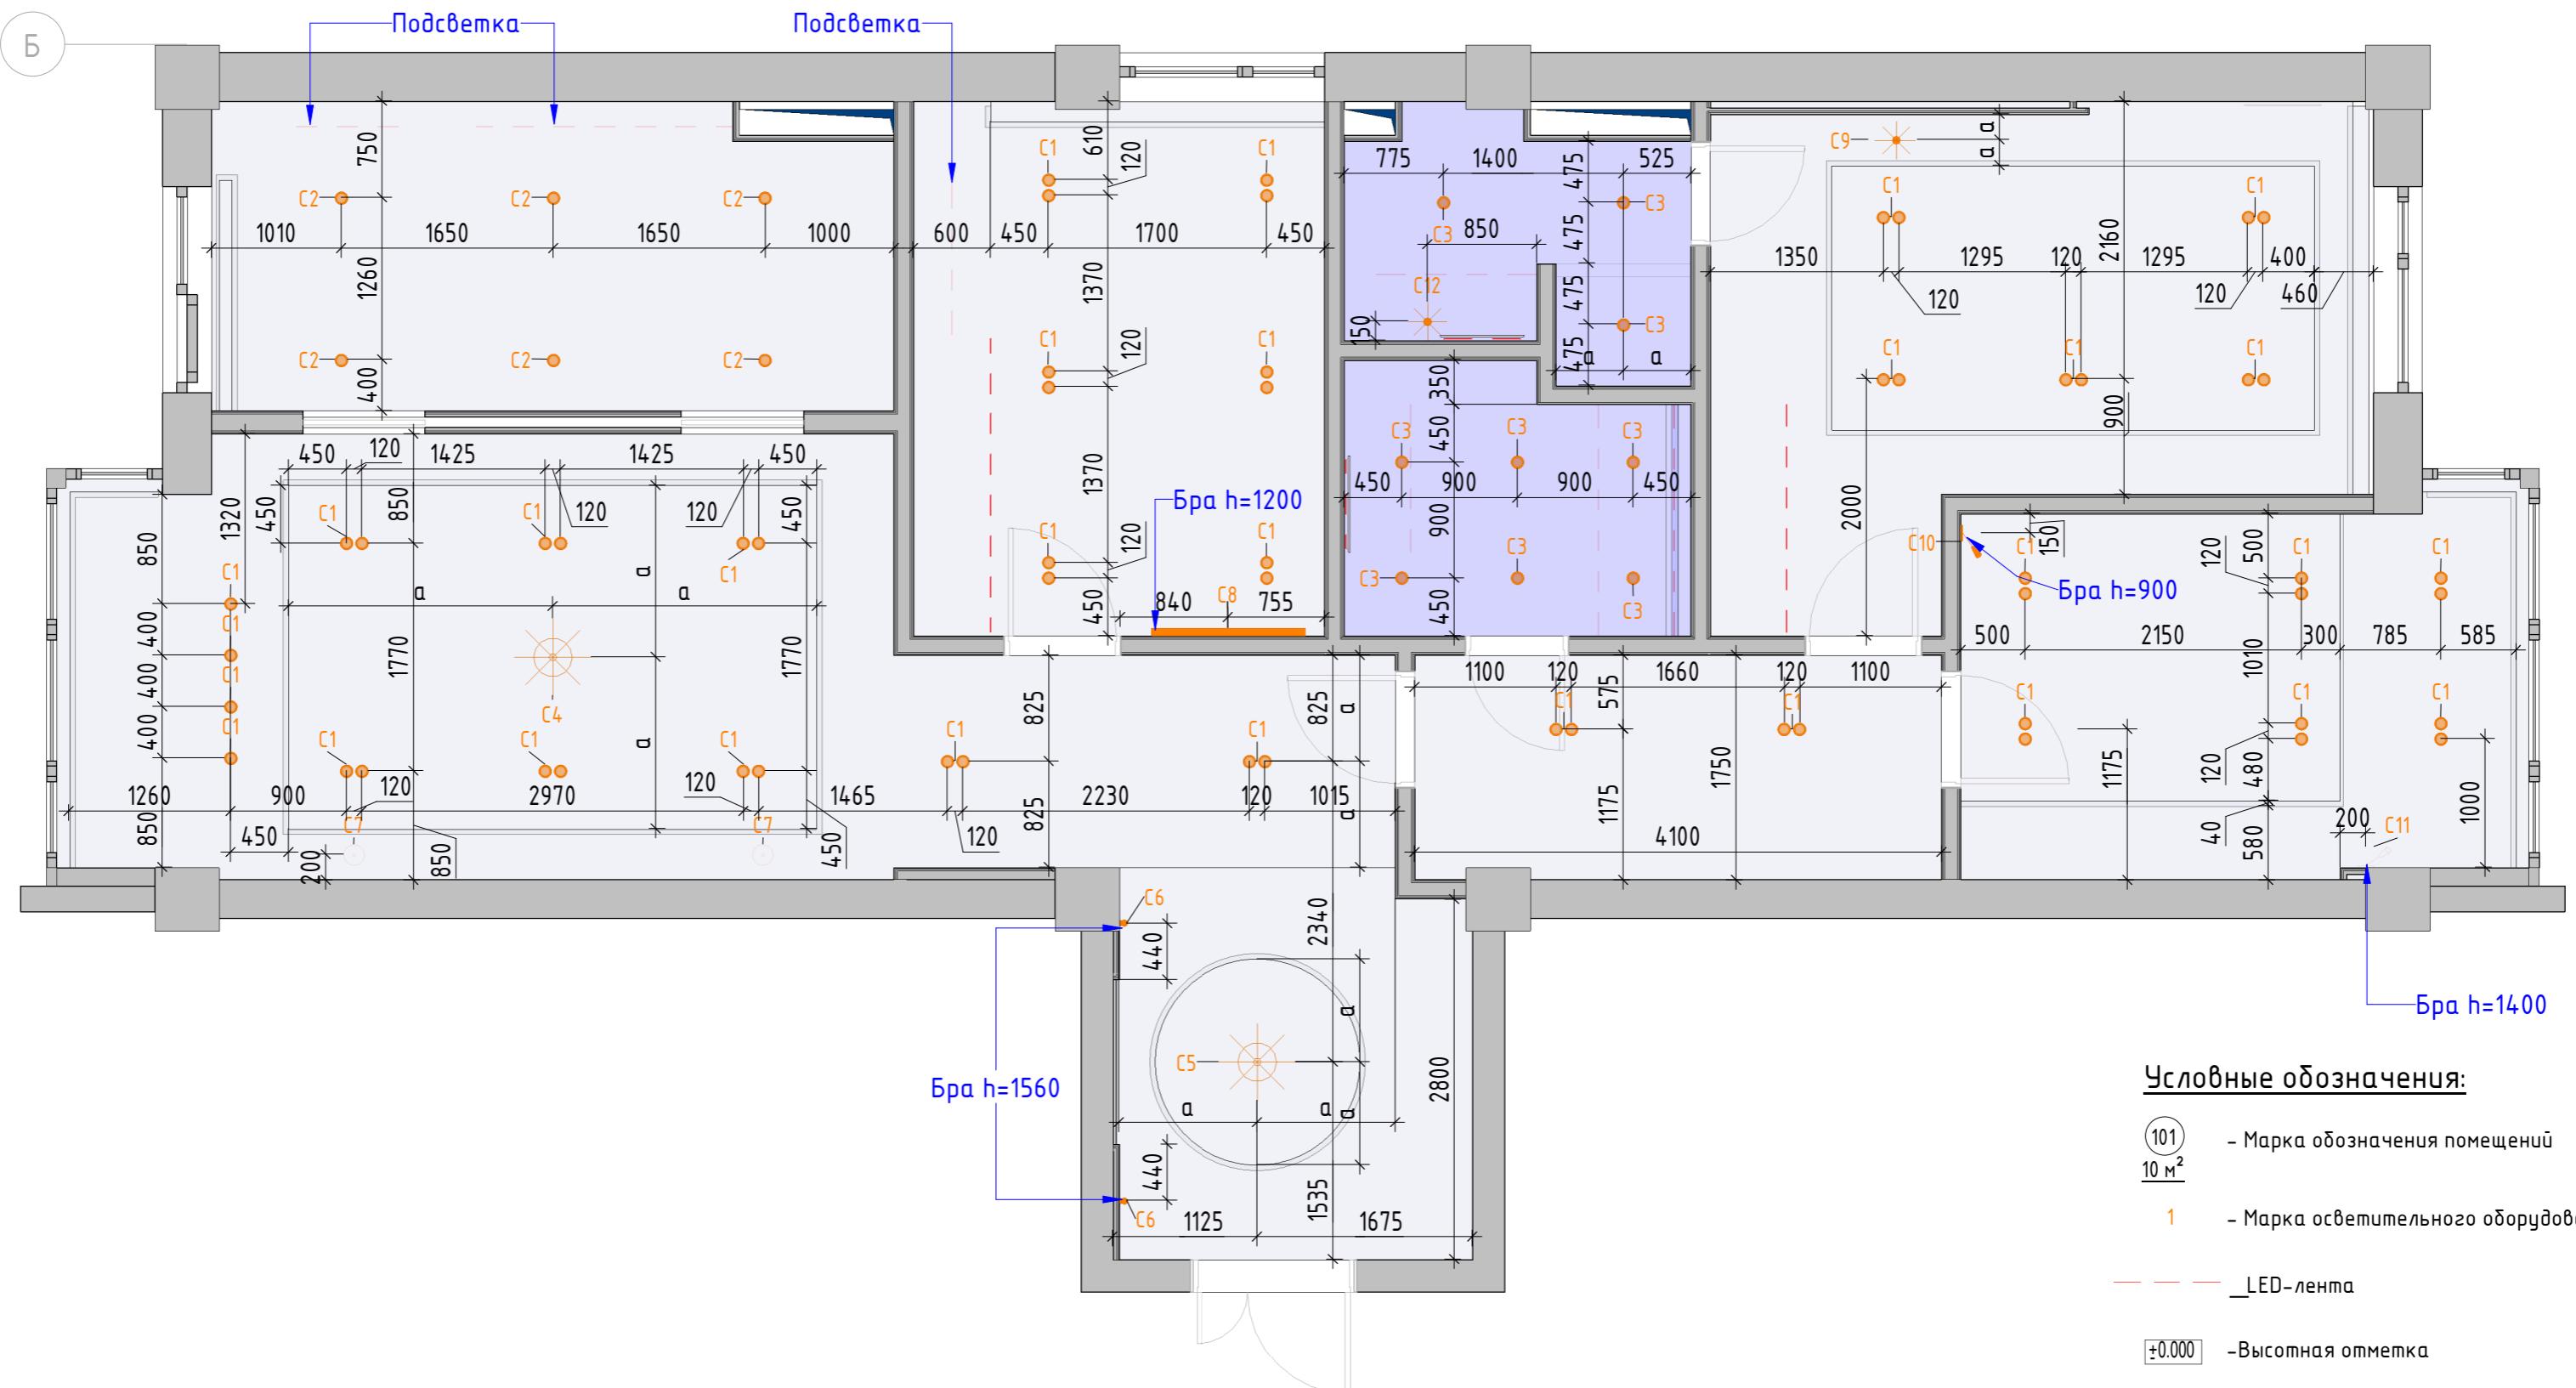

Примечания:

- За отметку 0.000 принята отметка чистого пола квартиры.
- Количество материалов в спецификациях посчитано БЕЗ ЗАПАСА.
- Все размеры уточняются по месту.

Дизайнер			
Заказчик			

ПЛАН РАССТАНОВКИ  
ОСВЕТИТЕЛЬНОГО ОБОРУДОВАНИЯ

Luxhouse\_studio


Формат: А3

Стадия

АИ

Лист


Листов

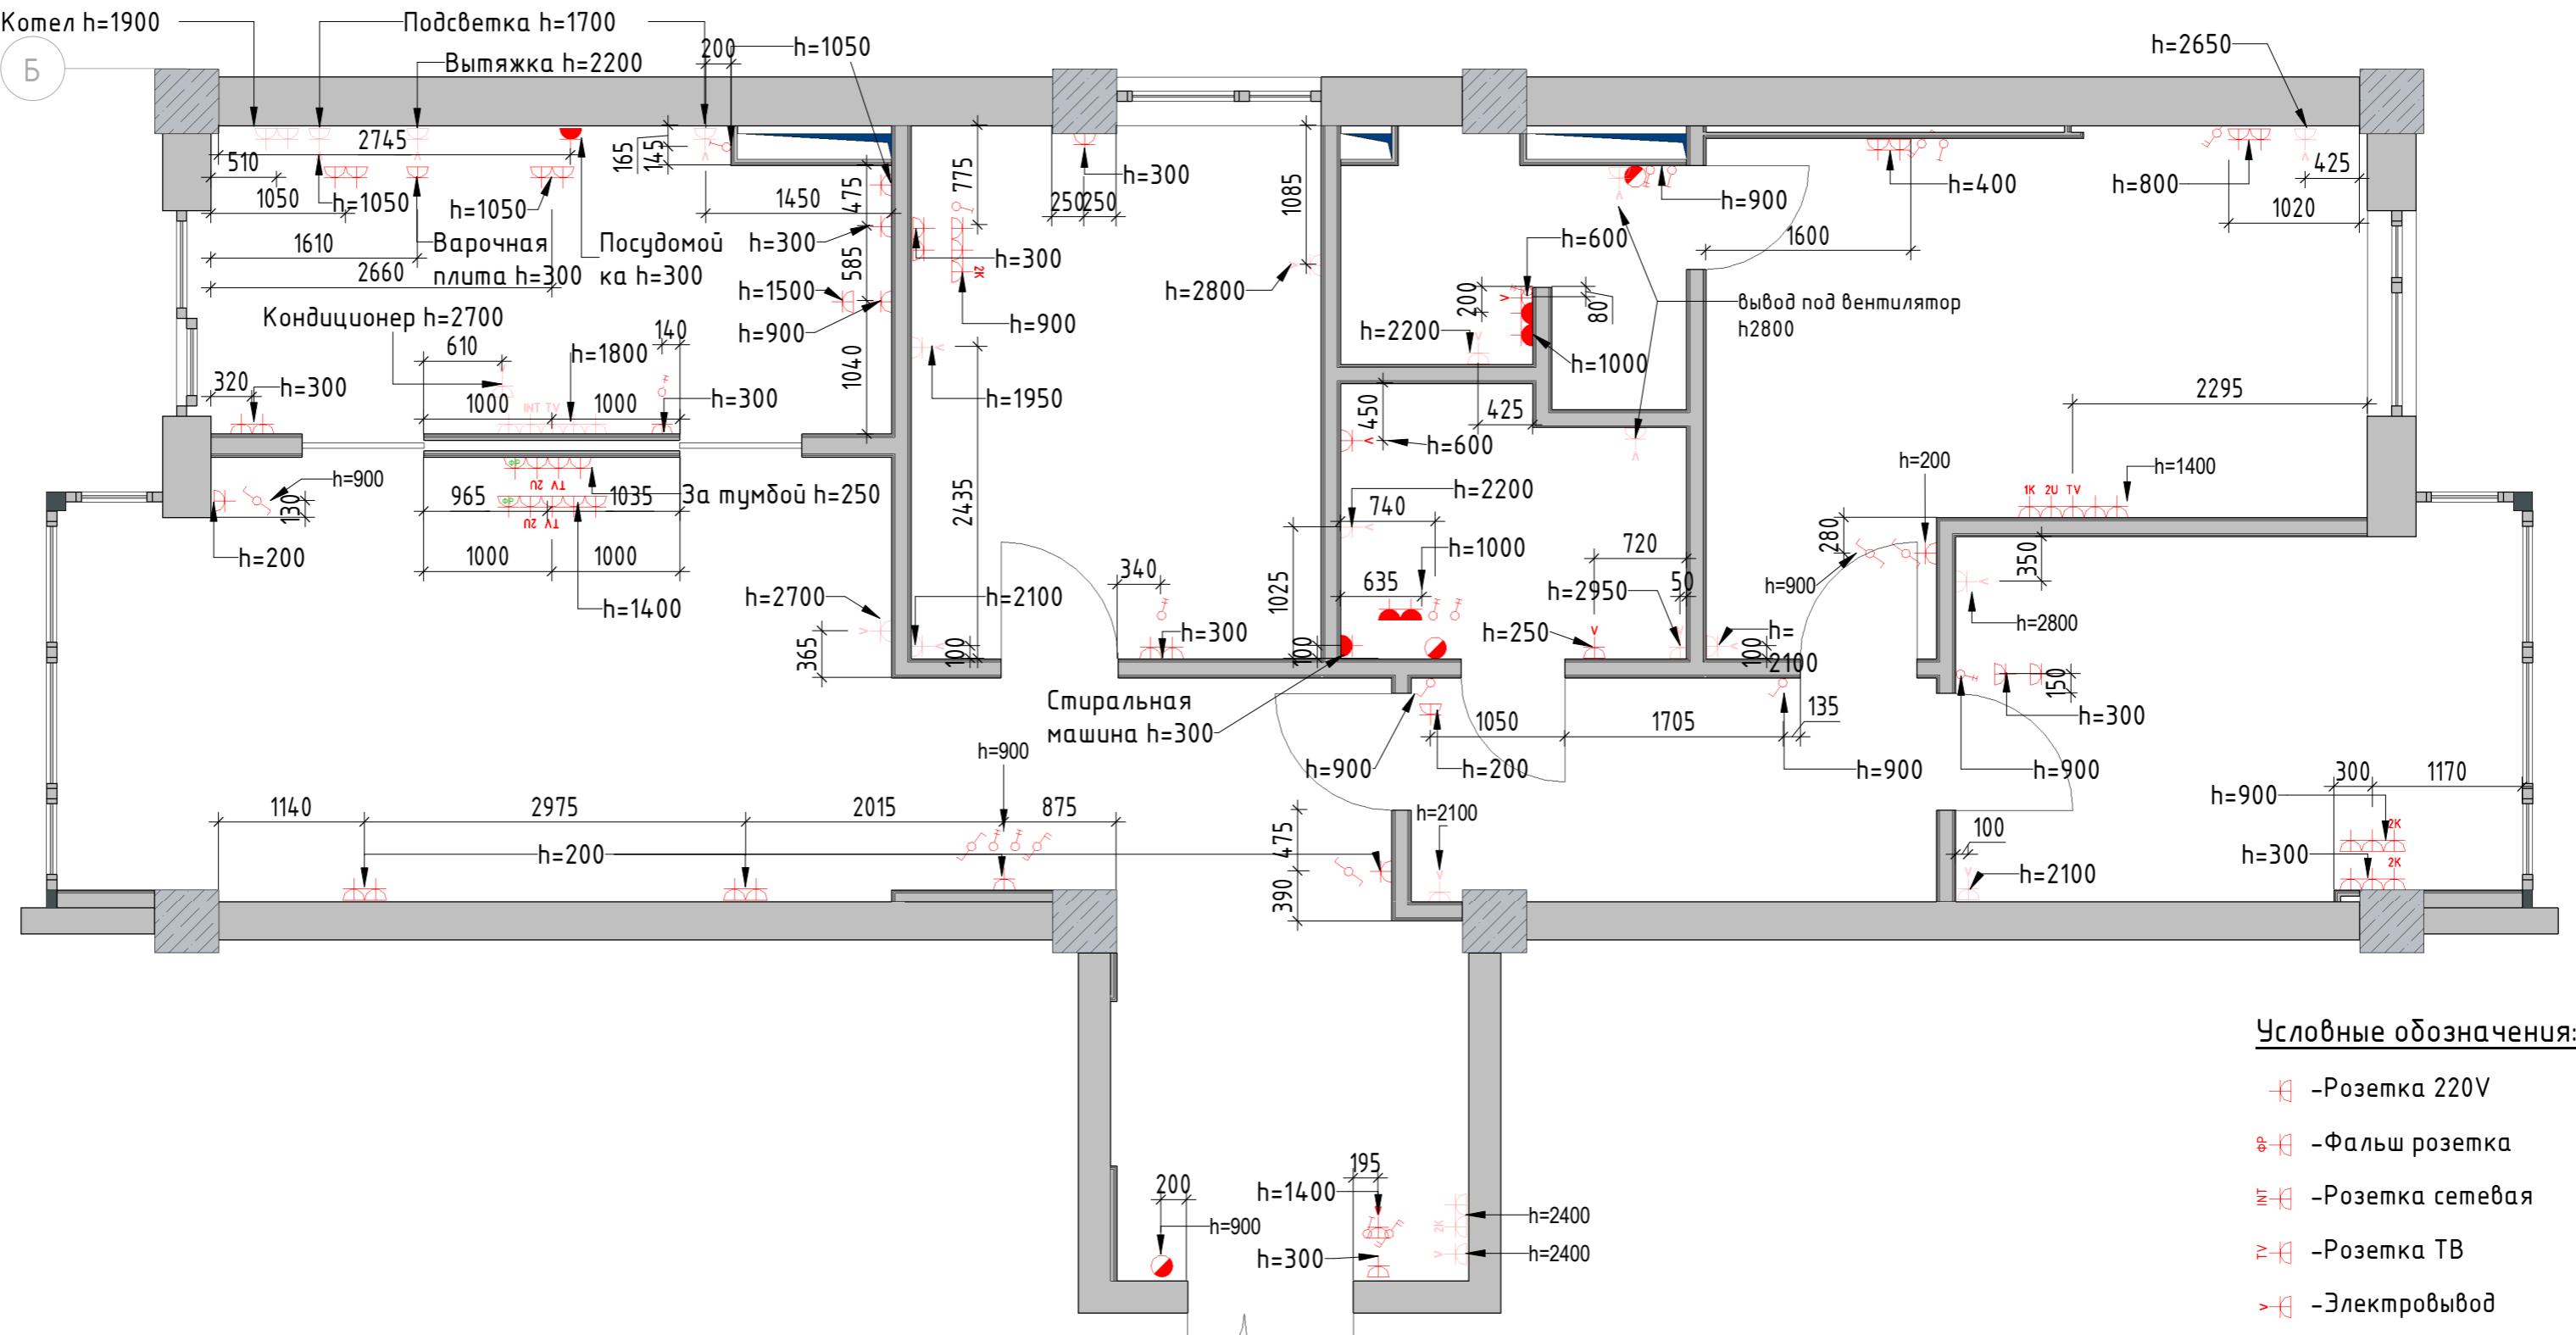

Примечания:

1. За отметку 0.000 принята отметка чистого пола квартиры.
2. Все размеры уточняются по месту.
3. Размеры даны до центра рамки.
4. Смотреть совместно с развертками.

Стадия	Лист	Листов
Дизайнер		
Заказчик	ПЛАН РАССТАНОВКИ РАЗЕТОК	
	Luxhouse_studio	


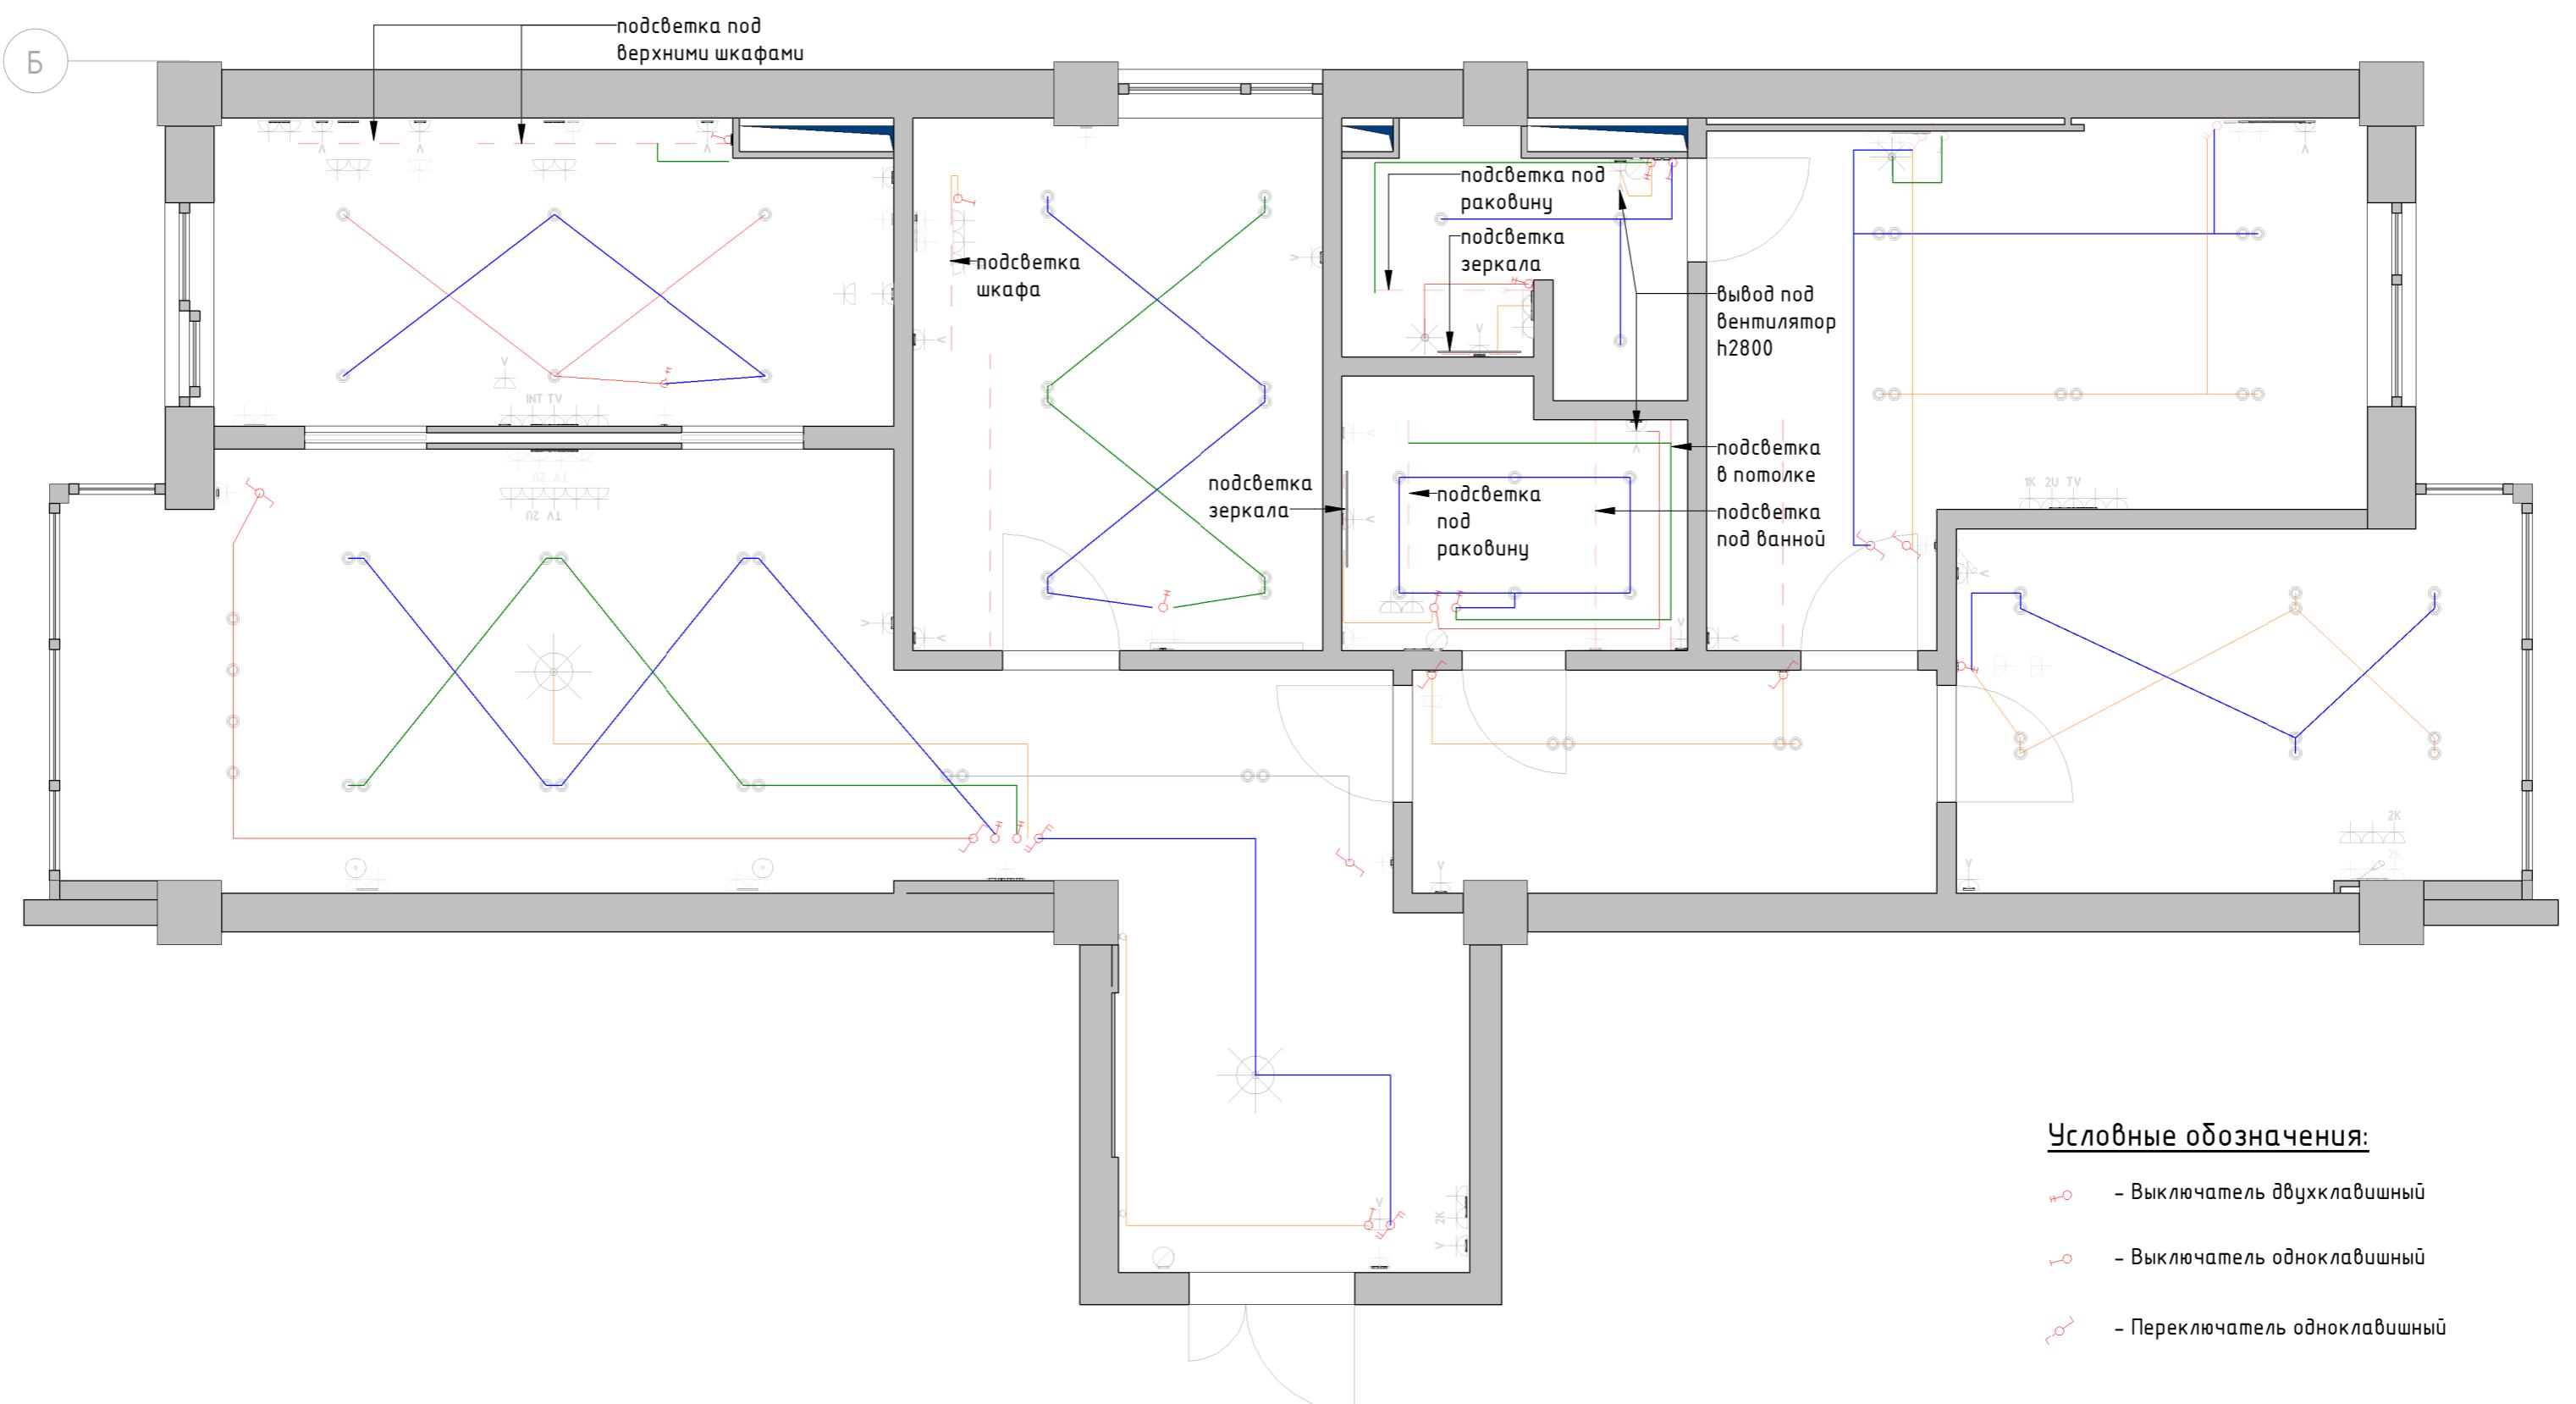







- Выключатель двуклавишный
  - Выключатель одноклавишный
  - Переключатель одноклавишный

#### **ЗАМЕЧАНИЯ:**

- За отметку 0.000 принята отметка чистого пола квартиры.  
Все размеры уточняются по месту.  
Размеры даны до центра рамки.  
Смотреть совместно с развертками.

Спецификация сантехнического оборудования и аксессуаров				
Тип	Изображение	Описание	Изготовитель	Кол-во, шт
1		Встраиваемая в столешницу раковина на кухню. Maris MRX 110-50, артикул 122.0543.996	Franke	1
2		Смеситель для кухонной мойки артикул 115.0569.461	Franke	1
3		Смеситель для раковины		2
4		Встраиваемая раковина для санузла		2
5		Чиназ, артикул 7082-0075	Vitra	2
6		Кнопка смыыва, артикул 740-0586	Vitra	2

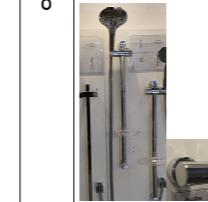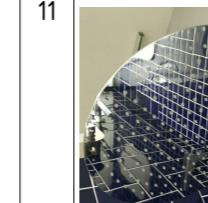
Спецификация сантехнического оборудования и аксессуаров				
Тип	Изображение	Описание	Изготовитель	Кол-во, шт
7		Акриловая ванна Raho Miami, габариты (дшг): 180x80x43 см	Нидерланды	1
8		Nest code 42242 Shine code 45628		1
9		Ручной душ, артикул 45683	Vitra	1
10		Термостат для душа, артикул 47025	Vitra	1
11		Верхний душ, артикул 45646	Vitra	1
12		Душевой лоток	Pestan, Confluo Frameless Line	1

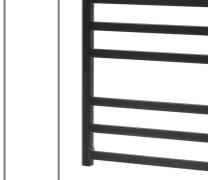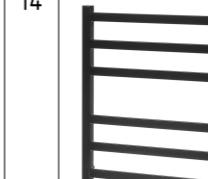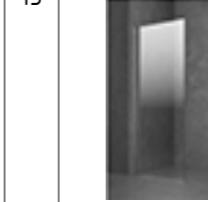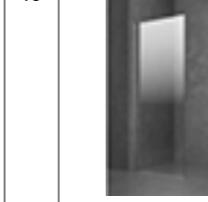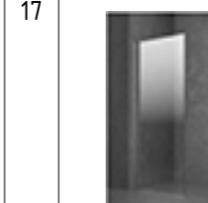Спецификация сантехнического оборудования и аксессуаров				
Тип	Изображение	Описание	Изготовитель	Кол-во, шт
13		Полотенцесушитель 600x1000 h		1
14		Полотенцесушитель 550x750 h		1
15		Стеклянная перегородка для душа. 700 x 2000 h		1
16		Стеклянная перегородка для душа. 440 x 2000 h		1
17		Стеклянная перегородка для душа - Дверца. 600 x 2000 h		1


Дизайнер	Заказчик	СПЕЦИФИКАЦИЯ САНТЕХНИЧЕСКОГО ОБОРУДОВАНИЯ			Стадия	Лист	Листов
					АИ		



**Облицовка из ГКЛ марка С 623**  
в соответствии с рекомендациями KNAUF  
серия 1.073.9-2.00.1-7

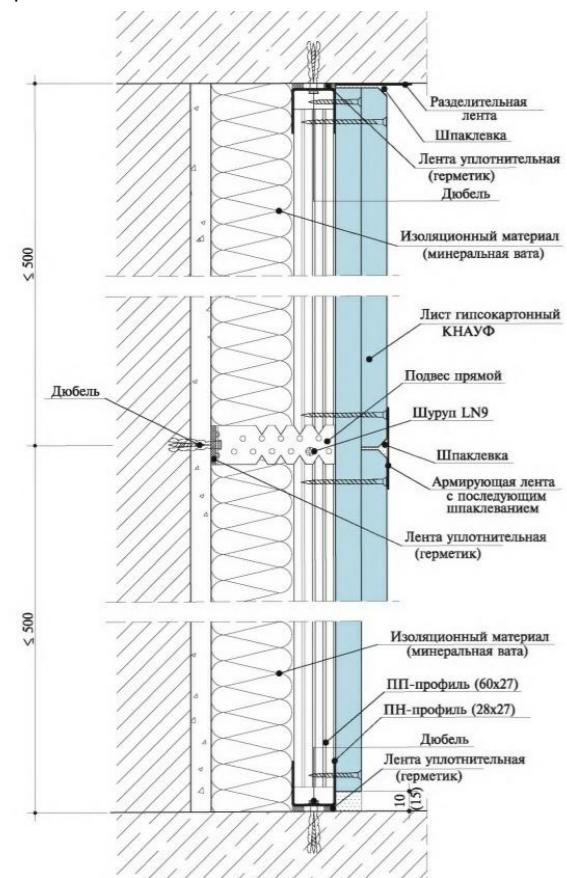

**Перегородка из ГКЛ марка С 112**  
в соответствии с рекомендациями KNAUF  
серия 1.031.9-2.07.2-3

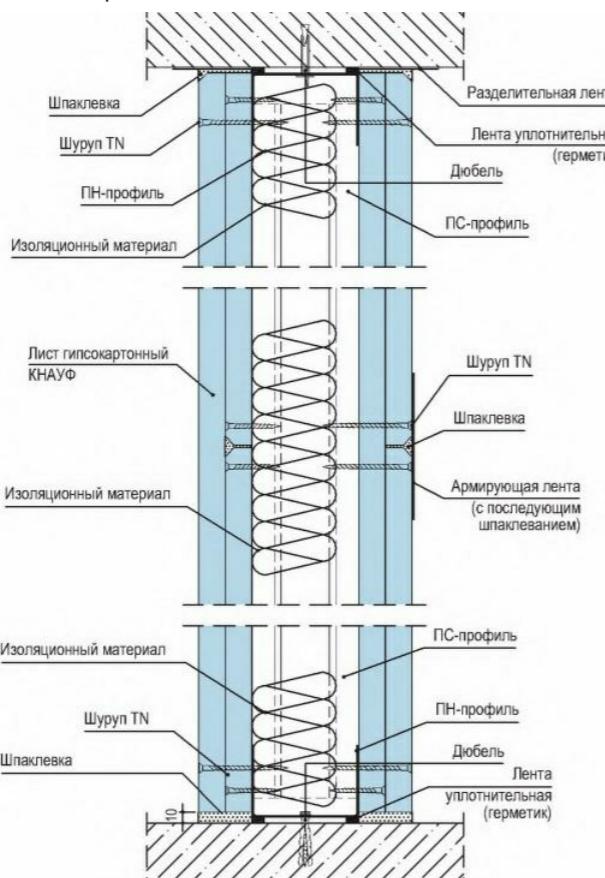

#### Ведомость перегородок и облицовок из ГКЛ

Изображение	Марка	Описание	Площадь
	0-1	Облицовка из ГКЛ марка С 623 в соответствии с рекомендациями KNAUF серия 1.073.9-2.00.1-7 . Двухслойная облицовка из ГКЛ-листов на металлическом каркасе, со звукоизоляцией, толщина (50мм)	32.81 м <sup>2</sup>
	0-2	Облицовка из ГКЛ марка С 623 в соответствии с рекомендациями KNAUF серия 1.073.9-2.00.1-7 . Двухслойная облицовка из ГКЛ-листов на металлическом каркасе, со звукоизоляцией, толщина (100мм)	4.23 м <sup>2</sup>
	П-1	Перегородка из ГКЛ марка С 112 в соответствии с рекомендациями KNAUF серия 1.031.9-2.07.2-3 . Двухслойная облицовка из ГКЛ-листов на металлическом каркасе с двух сторон, со звукоизоляцией, толщина (150мм)	59.85 м <sup>2</sup>
	П-2	Перегородка из ГКЛ марка С 112 в соответствии с рекомендациями KNAUF серия 1.031.9-2.07.2-3 . Двухслойная облицовка из ГКЛ-листов на металлическом каркасе с двух сторон, со звукоизоляцией, толщина (180мм)	4.78 м <sup>2</sup>

101.68  
м<sup>2</sup>

#### Ведомость перегородок и облицовок из ГКЛВ

Изображение	Марка	Описание	Площадь
	0-3	Облицовка из ГКЛ марка С 623 в соответствии с рекомендациями KNAUF серия 1.073.9-2.00.1-7 . Двухслойная облицовка из ГКЛВ-листов на металлическом каркасе, со звукоизоляцией, толщина (50мм)	12.62 м <sup>2</sup>
	П-3	Перегородка из ГКЛ марка С 112 в соответствии с рекомендациями KNAUF серия 1.031.9-2.07.2-3 . Двухслойная облицовка из ГКЛВ-листов на металлическом каркасе с двух сторон, со звукоизоляцией, толщина (150мм)	38.62 м <sup>2</sup>



51.24 м<sup>2</sup>

Стадия	Лист	Листов
Дизайнер		
Заказчик		

СПЕЦИФИКАЦИЯ ПЛАН  
МОНТАЖА ПЕРЕГОРОДОК

Luxhouse\_studio

Формат: А3

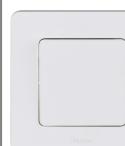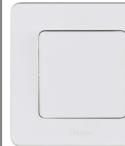Спецификация розеток и выключателей			
Изображение	Описание	Кол-во, шт	Производитель
	Выход кабеля	23	
	Выключатель двойхклавишный	9	Legrand
	Выключатель одноклавишный	5	Legrand
	Переключатель двойхклавишный	4	Legrand
	Переключатель одноклавишный	7	Legrand
	Розетка 2x USB	3	Legrand
	Розетка 220V	52	Legrand

Спецификация розеток и выключателей			
Изображение	Описание	Кол-во, шт	Производитель
	Розетка INT	1	Legrand
	Розетка IP44	6	Legrand
	Розетка TV	4	Legrand
	Розетка компьютерная 1x RJ45	1	Legrand
	Розетка компьютерная 2x RJ45	4	Legrand
	Термостат теплого пола	3	Legrand

Спецификация рамок			
Изображение	Описание	Кол-во, шт	Производитель
	Рамка на 1 пост	49	Legrand
	Рамка на 2 поста	13	Legrand
	Рамка на 3 поста	4	Legrand

Спецификация рамок			
Изображение	Описание	Кол-во, шт	Производитель
	Рамка на 4 поста	5	Legrand
	Рамка на 5 постов	3	Legrand

Стадия	Лист	Листов
Дизайнер		
Заказчик		
СПЕЦИФИКАЦИЯ РОЗЕТОК И ВЫКЛЮЧАТЕЛЕЙ		
Luxhouse_studio		

## СТЕНЫ

Отделка			
Тип	Изображение	Описание	Площадь
OC		Штукатурка	98.68 м <sup>2</sup>
OC1		Tikkurila_Y487 Piaccia	108.93 м <sup>2</sup>
OC2		Tikkurila_X487 Laasti_Раствор	21.21 м <sup>2</sup>
OC3		Tikkurila_X445 Lido_Лидо	6.53 м <sup>2</sup>
OC4		NOIR DESIR BOCCIARDATO	14.54 м <sup>2</sup>
OC5		BIANCO LASA BOCCIARDATO	5.41 м <sup>2</sup>

Отделка			
Тип	Изображение	Описание	Площадь
OC6		Белый керамогранит 1200x600, Vitra	4.21 м <sup>2</sup>
OC7		VERDERAME LUX	9.07 м <sup>2</sup>
OC8		ARVEN RECTIFIED PARLAK NANO 60X120 OT KUTAHYA	18.94 м <sup>2</sup>
OC9		55012910RL 60x120 ATLANTIS БЕЛЫЙ ЛАПАТИРОВАННЫЙ	10.79 м <sup>2</sup>
OC10		Фартук на кухне	3.65 м <sup>2</sup>

Подоконники:

Подоконник - 1600x250 2 шт.



Ведомость молдингов отделки стен		
Тип	Описание	Длина
Type-1	Молдинг 110x20	158.32
		158.32

Ведомость перегород и облицовок из ГКЛ			
Изображение	Марка	Описание	Площадь
	0-1	Облицовка из ГКЛ марка С 623 в соответствии с рекомендациями KNAUF серия 1.073.9-2.00.1-7 . Двухслойная облицовка из ГКЛ-листов на металлическом каркасе, со звукоизоляцией, толщина (50мм)	32.81 м <sup>2</sup>
	0-2	Облицовка из ГКЛ марка С 623 в соответствии с рекомендациями KNAUF серия 1.073.9-2.00.1-7 . Двухслойная облицовка из ГКЛ-листов на металлическом каркасе, со звукоизоляцией, толщина (100мм)	4.23 м <sup>2</sup>
	П-1	Перегородка из ГКЛ марка С 112 в соответствии с рекомендациями KNAUF серия 1.031.9-2.07.2-3 . Двухслойная облицовка из ГКЛ-листов на металлическом каркасе с двух сторон, со звукоизоляцией, толщина (150мм)	59.85 м <sup>2</sup>
	П-2	Перегородка из ГКЛ марка С 112 в соответствии с рекомендациями KNAUF серия 1.031.9-2.07.2-3 . Двухслойная облицовка из ГКЛ-листов на металлическом каркасе с двух сторон, со звукоизоляцией, толщина (180мм)	4.78 м <sup>2</sup>

101.68 м<sup>2</sup>

Ведомость перегород и облицовок из ГКЛВ			
Изображение	Марка	Описание	Площадь
	0-3	Облицовка из ГКЛ марка С 623 в соответствии с рекомендациями KNAUF серия 1.073.9-2.00.1-7 . Двухслойная облицовка из ГКЛВ-листов на металлическом каркасе, со звукоизоляцией, толщина (50мм)	12.62 м <sup>2</sup>
	П-3	Перегородка из ГКЛ марка С 112 в соответствии с рекомендациями KNAUF серия 1.031.9-2.07.2-3 . Двухслойная облицовка из ГКЛВ-листов на металлическом каркасе с двух сторон, со звукоизоляцией, толщина (150мм)	38.62 м <sup>2</sup>

51.24 м<sup>2</sup>

Стадия	Лист	Листов
Дизайнер		
Заказчик		
СПЕЦИФИКАЦИЯ СТЕН		
Luxhouse_studio		

Формат: А3

## ПОЛЫ

### Спецификация напольных покрытий в прихожей (плитки)

Тип	Условное изображение	Описание	Площадь, кв.м	Пирог пола	Данные элементов пола
НП1		600x1200, 55012906 Vitra	8.61 м <sup>2</sup>		1. Керамогранит - 8 мм 2. Клей - 5 мм 3. Цементно-песчанная стяжка - 67 мм 5. Существующее перекрытие - 200 мм

### Спецификация напольных покрытий (ламинат)

Тип	Условное изображение	Описание	Площадь, кв.м	Пирог пола	Данные элементов пола
НП2		Quick Step Castle CA 4160 Дуб капучино Класс 33 AC5 1200x396x8 мм	91.65 м <sup>2</sup>		1. Ламинат - 8 мм 2. Подложка - 3 мм 3. Цементно-песчаная стяжка - 69 мм 4. Существующее перекрытие - 200 мм

### Спецификация напольных покрытий в душевой (плитки НП3)

Тип	Условное изображение	Описание	Площадь, кв.м	Пирог пола	Данные элементов пола
НП3		600x1200, 55012923 Vitra	4.07 м <sup>2</sup>		1. Керамогранит - 8 мм 2. Клей - 5 мм 3. Цементно-песчаная стяжка - 62 мм 4. Гидроизоляция 5. Существующее перекрытие - 200 мм

### Спецификация напольных покрытий в душевой (плитки НП4)

Тип	Условное изображение	Описание	Площадь, кв.м	Пирог пола	Данные элементов пола
НП4		600x1200, 55012923 Vitra	4.86 м <sup>2</sup>		1. Керамогранит - 8 мм 2. Клей - 5 мм 3. Цементно-песчаная стяжка - 62 мм 4. Гидроизоляция 5. Существующее перекрытие - 200 мм

### Ведомость плинтусов

Тип	Изображение	Обозначение	Описание	Длина
Пл1		Tikkurila_G497 Hoyru_Пар	49.86	49.86

## ОТОПИТЕЛЬНЫЕ ПРИБОРЫ

Отопительные приборы			
Изображение	Число	Описание	Ссылка
	3	Горизонтальный радиатор	
	1	Внутрипольные конвекторы	<a href="https://www.jaga.com/en/products/trench-heating/micro-canal">https://www.jaga.com/en/products/trench-heating/micro-canal</a>
	2	Внутрипольные конвекторы	<a href="https://www.jaga.com/en/products/trench-heating/micro-canal">https://www.jaga.com/en/products/trench-heating/micro-canal</a>

## Теплый пол

Тип	Описание	Площадь, кв.м
ТП	Теплый пол	10.28 м <sup>2</sup>

## ПОТОЛКИ

Потолки			
Тип	Изображение	Описание	Площадь, кв.м
ПТ1		ГКЛ	99.91 м <sup>2</sup>
ПТ2		ГКЛВ	10.21 м <sup>2</sup>

### Ведомость карнизов

Тип	Обозначение	Описание	Длина
K1		Карниз 150x200h	40.57 40.57

### Спецификация покраски потолка

Описание	Площадь, кв.м
Покраска V503 Зима,Tikkurala	110.11 м <sup>2</sup>

Стадия	Лист	Листов
Дизайнер		
Заказчик		
АИ		
ОБЩАЯ СПЕЦИФИКАЦИЯ		Luxhouse_studio

Сантехнические оборудование и аксессуары				
Тип	Изображение	Описание	Изготовитель	Кол-во, шт
1		Встраиваемая в столешницу раковина на кухню Maris MRX 110-50, артикул 122.0543.996	Franke	1
2		Смеситель для кухонной мойки артикул 115.0569.461	Franke	1
3		Смеситель для раковины		2
4		Встраиваемая раковина для санузла		2
5		Унитаз, артикул 7082-0075	Vitra	2
6		Кнопка смыва, артикул 740-0586	Vitra	2
7		Акриловая ванна Riho Miami, габариты (дшв): 180x80x43 см	Нидерланды	1
8		Nest code 42242 Shine code 45628		1
9		Ручной душ, артикул 45683	Vitra	1
10		Термостат для душа, артикул 47025	Vitra	1


Сантехнические оборудование и аксессуары				
Тип	Изображение	Описание	Изготовитель	Кол-во, шт
11		Верхний душ, артикул 45646	Vitra	1
12		Душевой лоток Pestan, Confluo Frameless Line		1
13		Полотенцесушитель 600x1000 h		1
14		Полотенцесушитель 550x750 h		1
15		Стеклянная перегородка для душа. 700 x 2000 h		1
16		Стеклянная перегородка для душа. 440 x 2000 h		1
17		Стеклянная перегородка для душа - Дверца. 600 x 2000 h		1

Ведомость акрила для столешницы		
Изображение	Описание	Площадь
	AS642 Aspen Seashell	8.51 м <sup>2</sup>

Стадия	Лист	Листов
Дизайнер		
Заказчик		
СПЕЦИФИКАЦИЯ САНТЕХНИЧЕСКОГО ОБОРУДОВАНИЯ		

Luxhouse\_studio

## ЭЛЕКТРИКА

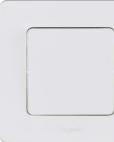
Розетки и выключатели			
Изображение	Описание	Кол-во, шт	Производитель
	Выход кабеля	23	
	Выключатель двухклавишный	9	Legrand
	Выключатель одноклавишный	5	Legrand
	Переключатель двухклавишный	4	Legrand
	Переключатель одноклавишный	7	Legrand
	Розетка 2x USB	3	Legrand
	Розетка 220V	52	Legrand
	Розетка INT	1	Legrand
	Розетка IP44	6	Legrand
	Розетка TV	4	Legrand

Розетки и выключатели			
Изображение	Описание	Кол-во, шт	Производитель
	Розетка компьютерная 1x RJ45	1	Legrand
	Розетка компьютерная 2x RJ45	4	Legrand
	Термостат теплого пола	3	Legrand

Спецификация LED для мебели			
Тип	Изображение	Усл.обозначение	Длина, мм
C14			22.14

Ведомость бытовой техники	
Название	Кол-во

Handsfree video entry phones for IP360 systems, 5" IP	1
Logamax U072-24K (Комел)	1
Wi-Fi роутер	1
Варочная панель 600x600	1
Вентилятор для санузла - Диаметр 100 мм	2
Вытяжка 600x300x330h	1
Духовая печь 600x400x600h	1
Кондиционер тип 1	2
Кондиционер тип 2	3
Микроволновая печь 600x400x400h	1
Посудомоечная машина 600x570x800h	1
Стиральная машина 600x450	1
Телевизор - Диагональ 46	1
Телевизор - Диагональ 55	2
Холодильник 600x540x1800h	1
Электроощит	1

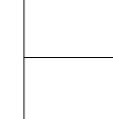Рамки			
Изображение	Описание	Кол-во, шт	Производитель
	Рамка на 1 пост	49	Legrand
	Рамка на 2 поста	13	Legrand
	Рамка на 3 поста	4	Legrand
	Рамка на 4 поста	5	Legrand
	Рамка на 5 постов	3	Legrand

Стадия	Лист	Листов
Дизайнер		
Заказчик		
СПЕЦИФИКАЦИЯ РАЗЕТОК И ВЫКЛЮЧАТЕЛЕЙ		Luxhouse_studio




Осветительные приборы						
Тип	Изображение	Описание	Кол-во, шт	Кельвин	Вт	Ссылка
C1		Артикул: DL18413/11WW-R White	58	3500	10	
C2		Артикул: DL18413/11WW-R White	6	3500	15	
C3		Артикул: DL18413/11WW-R White	9	3500	7	
C4		Milky Gold Trees Chandelier Главная/Люстры Артикул L1314	1			<a href="https://lampsshop.ru/?store-page=Milky-Gold-Trees-Chandelier-p229342405">https://lampsshop.ru/?store-page=Milky-Gold-Trees-Chandelier-p229342405</a>
C5		Люстра Bond Современные люстры Артикул L1323	1	3500		<a href="https://lampsshop.ru/?store-page=%D0%9B%D1%8E%D1%81%D1%82%D1%80%D0%B0-Bond-p234774662">https://lampsshop.ru/?store-page=%D0%9B%D1%8E%D1%81%D1%82%D1%80%D0%B0-Bond-p234774662</a>
C6		Настенный светильник ForkWal. Артикул: 13027-7l	2	3000-6000	25	<a href="https://glode.ru/catalog/product/331976600-485436027791-nastennii-svetilnik-for-kwall">https://glode.ru/catalog/product/331976600-485436027791-nastennii-svetilnik-for-kwall</a>
C7		Торшер Simplumen. Артикул: 00001-2	2			<a href="https://glode.ru/catalog/product/334660034-836381128431-torsher-simplumen">https://glode.ru/catalog/product/334660034-836381128431-torsher-simplumen</a>
C8		Настенный светильник OmniWall. Артикул: 13034-2	1	3000-6000	25	<a href="https://glode.ru/catalog/product/331976600-555954115711-nastennii-svetilnik-omni-wall">https://glode.ru/catalog/product/331976600-555954115711-nastennii-svetilnik-omni-wall</a>
C9		Подвесной светильник из серии Perfection Подвесные светильники Артикул PDL2191	1	3000	25	<a href="https://lampsshop.ru">https://lampsshop.ru</a>

Осветительные приборы						
Тип	Изображение	Описание	Кол-во, шт	Кельвин	Вт	Ссылка
C10		Настенный светильник KAA Артикул W111043/1 white	1	3000	3	<a href="https://www.donolux.ru/produktsiya/Nastennyie-svetilniki/KAA">https://www.donolux.ru/produktsiya/Nastennyie-svetilniki/KAA</a>
C11		Бра Loft A Артикул В4283а	1	3000	5	<a href="https://lampsshop.ru/?store-page=%D0%99%D1%80%D0%BD-A-Loft-A-p349213495&amp;offset=36">https://lampsshop.ru/?store-page=%D0%99%D1%80%D0%BD-A-Loft-A-p349213495&amp;offset=36</a>
C12		Подвесной светильник Heyday. Артикул PDL2194b	1	3000	5	<a href="https://lampsshop.ru">https://lampsshop.ru</a>

Стадия	Лист	Листов
Дизайнер		
Заказчик		
СПЕЦИФИКАЦИЯ ОСВЕТИТЕЛЬНОГО ПРИБОРОВ		



Спецификация мебели				
Тип	Наименование	Габариты	Кол-во, шт	Изображение
1	Шкаф гардеробный в прихожей	b=580 l=2780 h=2970	1	
2	Тумба в прихожей	b=400 l=1200 h=750	1	
3	Пуф		3	
4	Стол столовый в гостиной	b=1000 l=2000 h=800	1	
5	Стул столовый в гостиной		6	
6	Журнальный столик		1	
7	Диван	b=950 l=2800 h=250	1	
8	Тумба консольная под ТВ в гостиной	b=400 l=1820 h=250	1	
9	Кухонный гарнитур	b=600 l=7080 h=2970	1	
10	Стол столовый на кухне	b=900 l=1500 h=800	1	

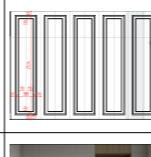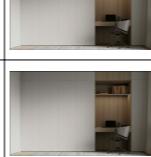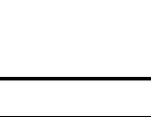Спецификация мебели				
Тип	Наименование	Габариты	Кол-во, шт	Изображение
11	Стул столовый на кухне		4	
12	Шкаф гардеробный в коридоре	b=600 l=4100 h=2970	1	
13	Шкаф комбинированный	b=600 l=4140 h=2970	1	
14	Кресло рабочее		1	
15	Кровать односпальная	b=1000 l=2000	2	
16	Тумба прикроватная	b=400 l=400	1	
17	Шкаф гардеробный в спальне	b=600 l=2700 h=2970	1	 
18	Кровать двуспальная	b=2000 l=2200	1	
19	Тумба прикроватная	b=450 l=700 h=350	1	
20	Столик косметический	b=450 l=1200 h=750	1	
21	Шкаф комбинированный	b=600 l=2950 h=2970	1	

Спецификация мебели				
Тип	Наименование	Габариты	Кол-во, шт	Изображение
22	Стол рабочий	b=600 l=1600 h=750	1	
23	Кресло рабочее		1	
24	Кресло мешок		1	
25	Шкаф под раковиной	b=600 l=1800 h=390	1	
26	Шкаф с унитазом	b=350 l=1500 h=2970	1	
27	Шкаф под раковиной	b=600 l=1250 h=390	1	
28	Шкаф с унитазом	b=250 l=1550 h=2970	1	
29	Шкаф в санузле	b=295 l=950 h=1800	1	

Дизайнер	Заказчик	Стадия	Лист	Листов
АИ				

СПЕЦИФИКАЦИЯ МЕБЕЛИ

Luxhouse\_studio

Спецификация напольных покрытий в душевой (плитки НП3)					
Тип	Условное изображение	Описание	Площадь, кв.м	Пирог пола	Данные элементов пола
НП3		600x1200, 55012923 Vitra	4.07 м <sup>2</sup>		1. Керамогранит – 8 мм 2. Клей – 5 мм 3. Цементно-песчанная стяжка – 62 мм 4. Гидроизоляция 5. Существующее перекрытие – 200 мм

Спецификация напольных покрытий (ламинат)					
Тип	Условное изображение	Описание	Площадь, кв.м	Пирог пола	Данные элементов пола
НП2		Quick Step Castle CA 4160 Дуб капучино Класс 33 AC5 1200x396x8 мм	91.65 м <sup>2</sup>		1. Ламинат – 8 мм 2. Подложка – 3 мм 3. Цементно-песчаная стяжка – 69 мм 4. Существующее перекрытие – 200 мм

Спецификация напольных покрытий в душевой (плитки НП4)					
Тип	Условное изображение	Описание	Площадь, кв.м	Пирог пола	Данные элементов пола
НП4		600x1200, 55012923 Vitra	4.86 м <sup>2</sup>		1. Керамогранит – 8 мм 2. Клей – 5 мм 3. Цементно-песчаная стяжка – 62 мм 4. Гидроизоляция 5. Существующее перекрытие – 200 мм

Ведомость плинтусов				
Тип	Изображение	Обозначение	Описание	Длина
Пл1			Tikkurila_G497 Hoogu_Пар	49.86
				49.86

Спецификация напольных покрытий в прихожей (плитки)					
Тип	Условное изображение	Описание	Площадь, кв.м	Пирог пола	Данные элементов пола
НП1		600x1200, 55012906 Vitra	8.61 м <sup>2</sup>		1. Керамогранит – 8 мм 2. Клей – 5 мм 3. Цементно-песчаная стяжка – 67 мм 4. Существующее перекрытие – 200 мм

Стадия	Лист	Листов
Дизайнер		
Заказчик		
СПЕЦИФИКАЦИЯ НАПОЛЬНОГО ПОКРЫТИЯ		
Luxhouse_studio		

Спецификация осветительных приборов						
Тип	Изображение	Описание	Кол-во, шт	Кельвин	Вт	Ссылка
C1		Артикул: DL18413/11WW-R White	58	3500	10	
C2		Артикул: DL18413/11WW-R White	6	3500	15	
C3		Артикул: DL18413/11WW-R White	9	3500	7	
C4		Milky Gold Trees Chandelier Гла8ная/Люстры Артикул L1314	1			<a href="https://lampsshop.ru/?store-page=Milky-Gold-Trees-Chandelier-p229342405">https://lampsshop.ru/?store-page=Milky-Gold-Trees-Chandelier-p229342405</a>
C5		Люстра Bond Современные люстры Артикул L1323	1	3500		<a href="https://lampsshop.ru/?store-page=%D0%9B%D1%8E%D1%81%D1%82%D1%80%D0%B0-Bond-p234774662">https://lampsshop.ru/?store-page=%D0%9B%D1%8E%D1%81%D1%82%D1%80%D0%B0-Bond-p234774662</a>
C6		Настенный светильник ForkWal. Артикул: 13027-71	2	3000-6000	25	<a href="https://glode.ru/catalog/product/331976600-485436027791-nastennii-svetilnik-forkwall">https://glode.ru/catalog/product/331976600-485436027791-nastennii-svetilnik-forkwall</a>

Спецификация осветительных приборов						
Тип	Изображение	Описание	Кол-во, шт	Кельвин	Вт	Ссылка
C7		Торшер SimpLumen. Артикул: 00001-2	2			<a href="https://glode.ru/catalog/product/334660034-836381128431-torsher-simplumen">https://glode.ru/catalog/product/334660034-836381128431-torsher-simplumen</a>
C8		Настенный светильник OmniWall. Артикул: 13034-2	1	3000-6000	25	<a href="https://glode.ru/catalog/product/331976600-555954115711-nastennii-svetilnik-omniwall">https://glode.ru/catalog/product/331976600-555954115711-nastennii-svetilnik-omniwall</a>
C9		Подвесной светильник из серии Perfection Подвесные светильники Артикул PDL2191	1	3000	25	<a href="https://lampsshop.ru">https://lampsshop.ru</a>
C10		Настенный светильник KAA Артикул W111043/1 white	1	3000	3	<a href="https://www.donolux.ru/produktsiya/Nastennyie-svetilniki/KA-A">https://www.donolux.ru/produktsiya/Nastennyie-svetilniki/KA-A</a>
C11		Бра Loft A Артикул B4283a	1	3000	5	<a href="https://lampsshop.ru/?store-page=%D0%91%D1%80%D0%B0-Loft-A-p349213495&amp;offset=36">https://lampsshop.ru/?store-page=%D0%91%D1%80%D0%B0-Loft-A-p349213495&amp;offset=36</a>
C12		Подвесной светильник Heyday. Артикул PDL2194b	1	3000	5	<a href="https://lampsshop.ru">https://lampsshop.ru</a>

Спецификация LED для мебели			
Тип	Изображение	Условозначение	Длина, мм
C14		—	22.14

Стадия	Лист	Листов
Дизайнер		
Заказчик		
СПЕЦИФИКАЦИЯ ОСВЕТИТЕЛЬНЫХ ПРИБОРОВ		Luxhouse_studio



Дизайнер			
Заказчик			

	Стадия	Лист	Листов
АИ			
МУДБОРД			Luxhouse_studio




Дизайнер			
Заказчик			

МУДБОРД

Luxhouse\_studio

Формат: А3

Стадия	Лист	Листов
АИ		

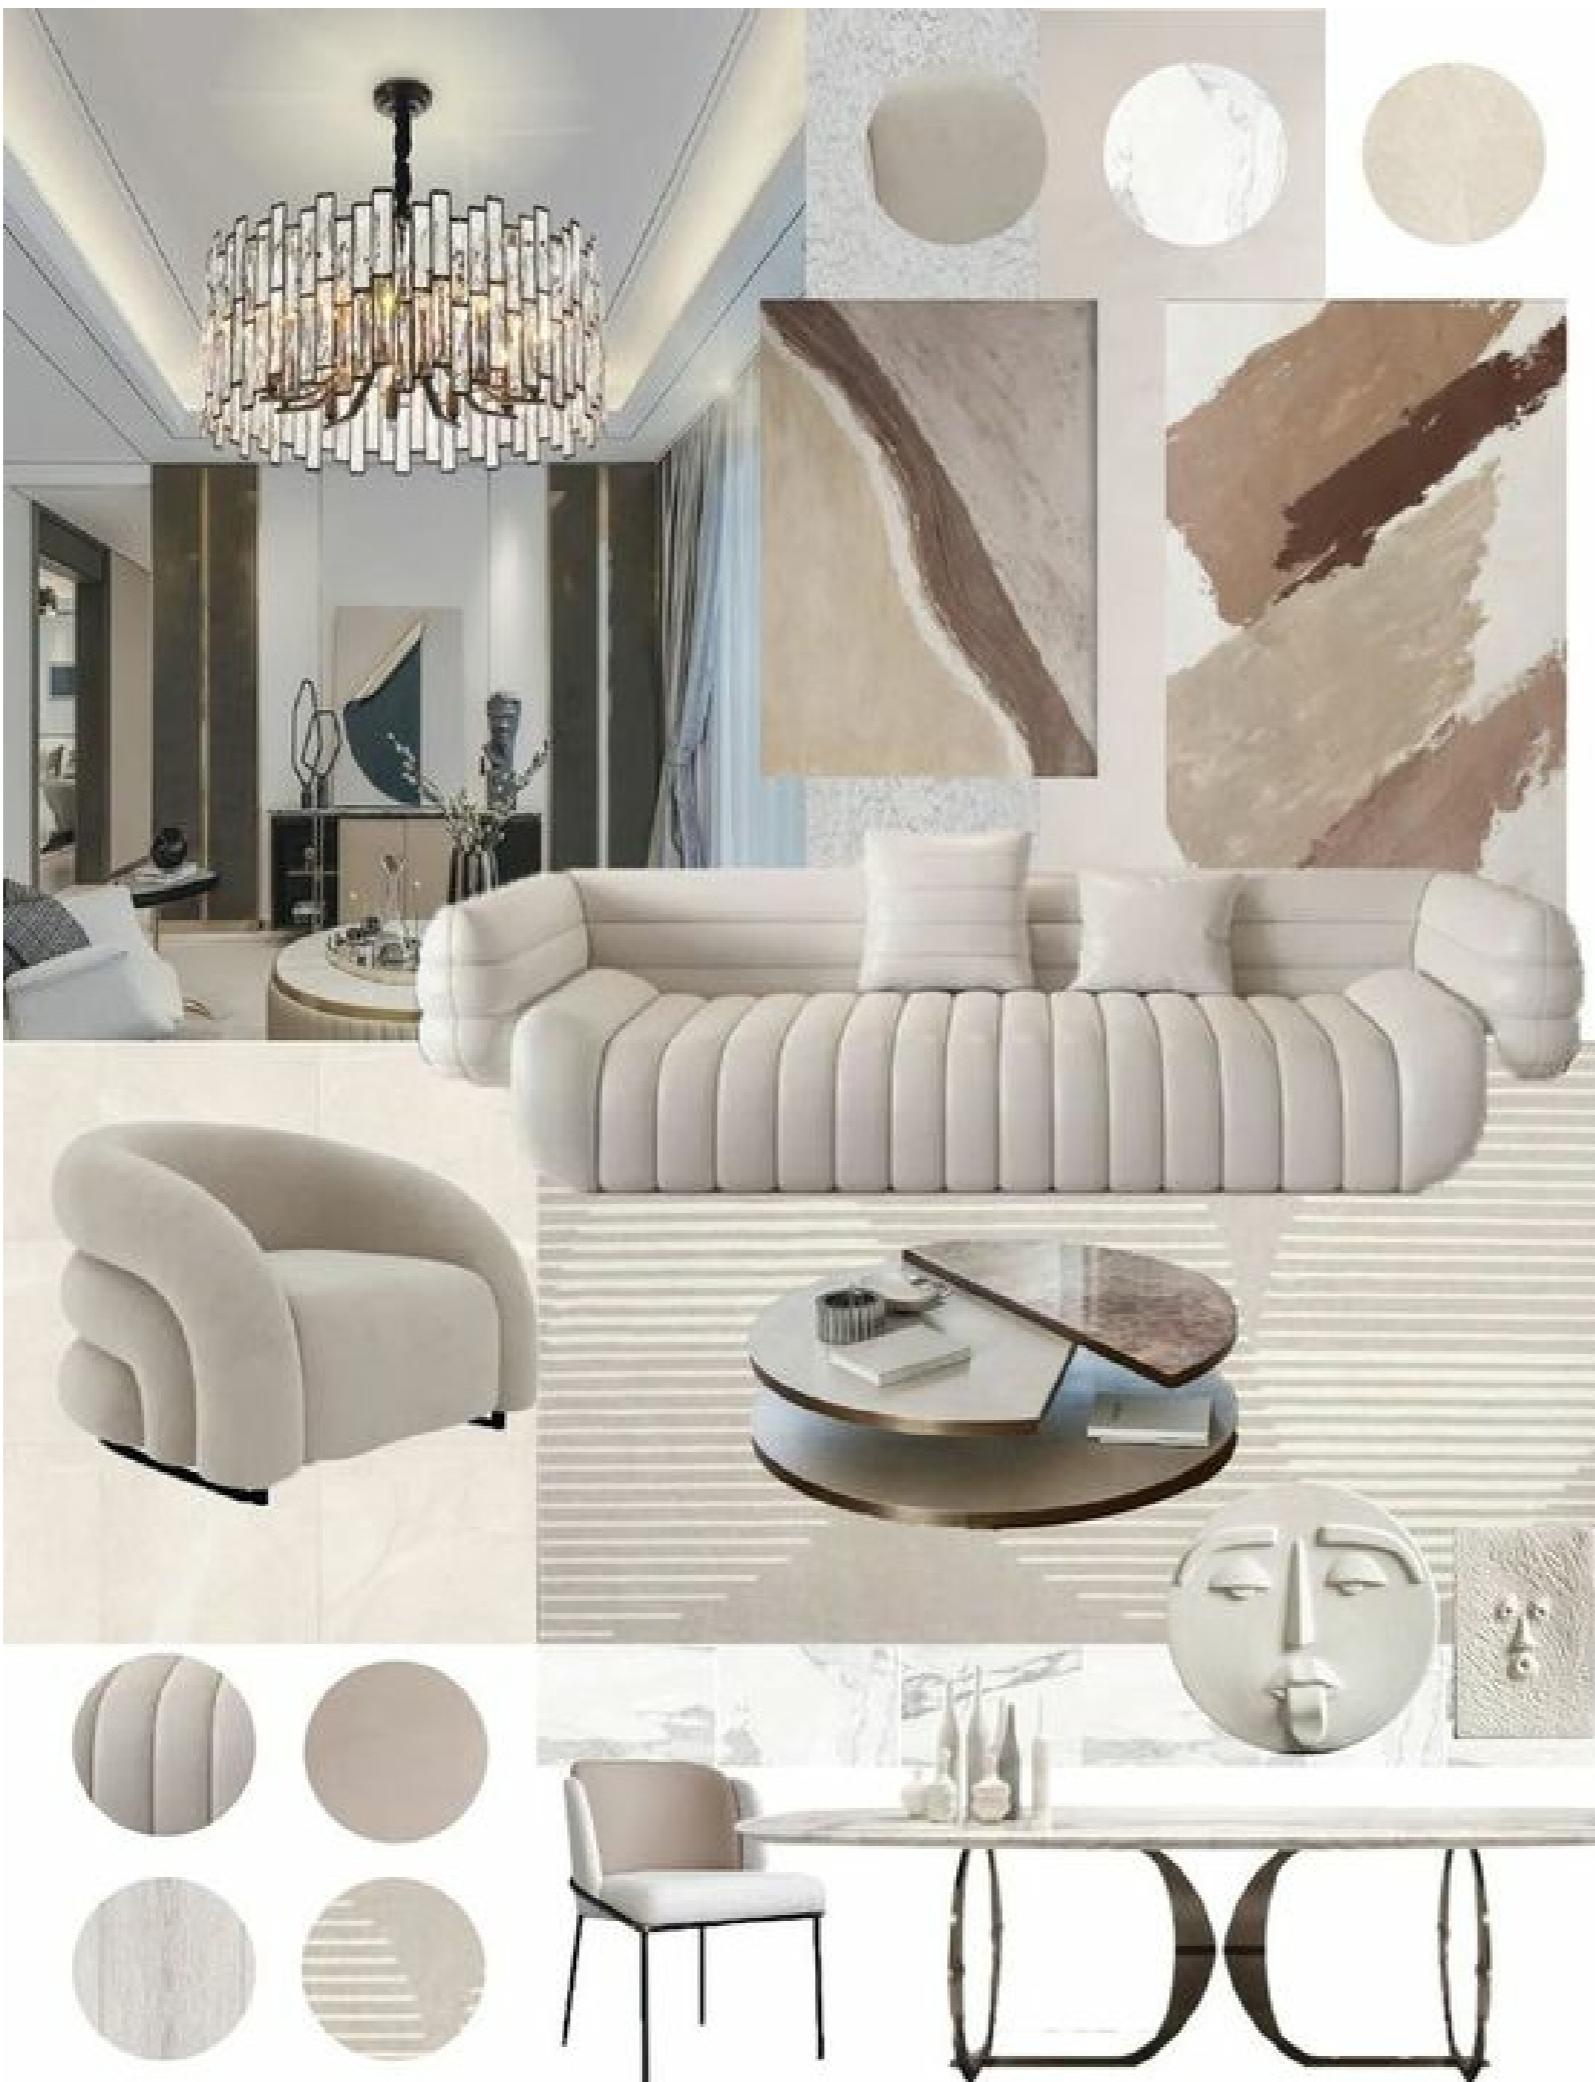

Дизайнер			
Заказчик			

МУДБОРД

Стадия	Лист	Листов
АИ		



Luxhouse\_studio

Формат: А3