


Ведомость рабочих чертежей		
Лист	Наименование	Примечание
0	Ведомость рабочих чертежей	
1	Обмерный план	
2	План демонтажа перегородок	
3	План монтажа перегородок	
4	3D Вид монтажа	
5	План расположения мебели	
6	План расположения мебели 3D	
7	План расположения мебели с размерами	
8	План расположения осветительного оборудования	
9	План привязки приборов освещения к выключателям	
10	План расположения розеток	

Стадия	Лист	Листов
Дизайнер		
Заказчик		
ВЕДОМОСТЬ РАБОЧИХ ЧЕРТЕЖЕЙ		Luxhouse_studio

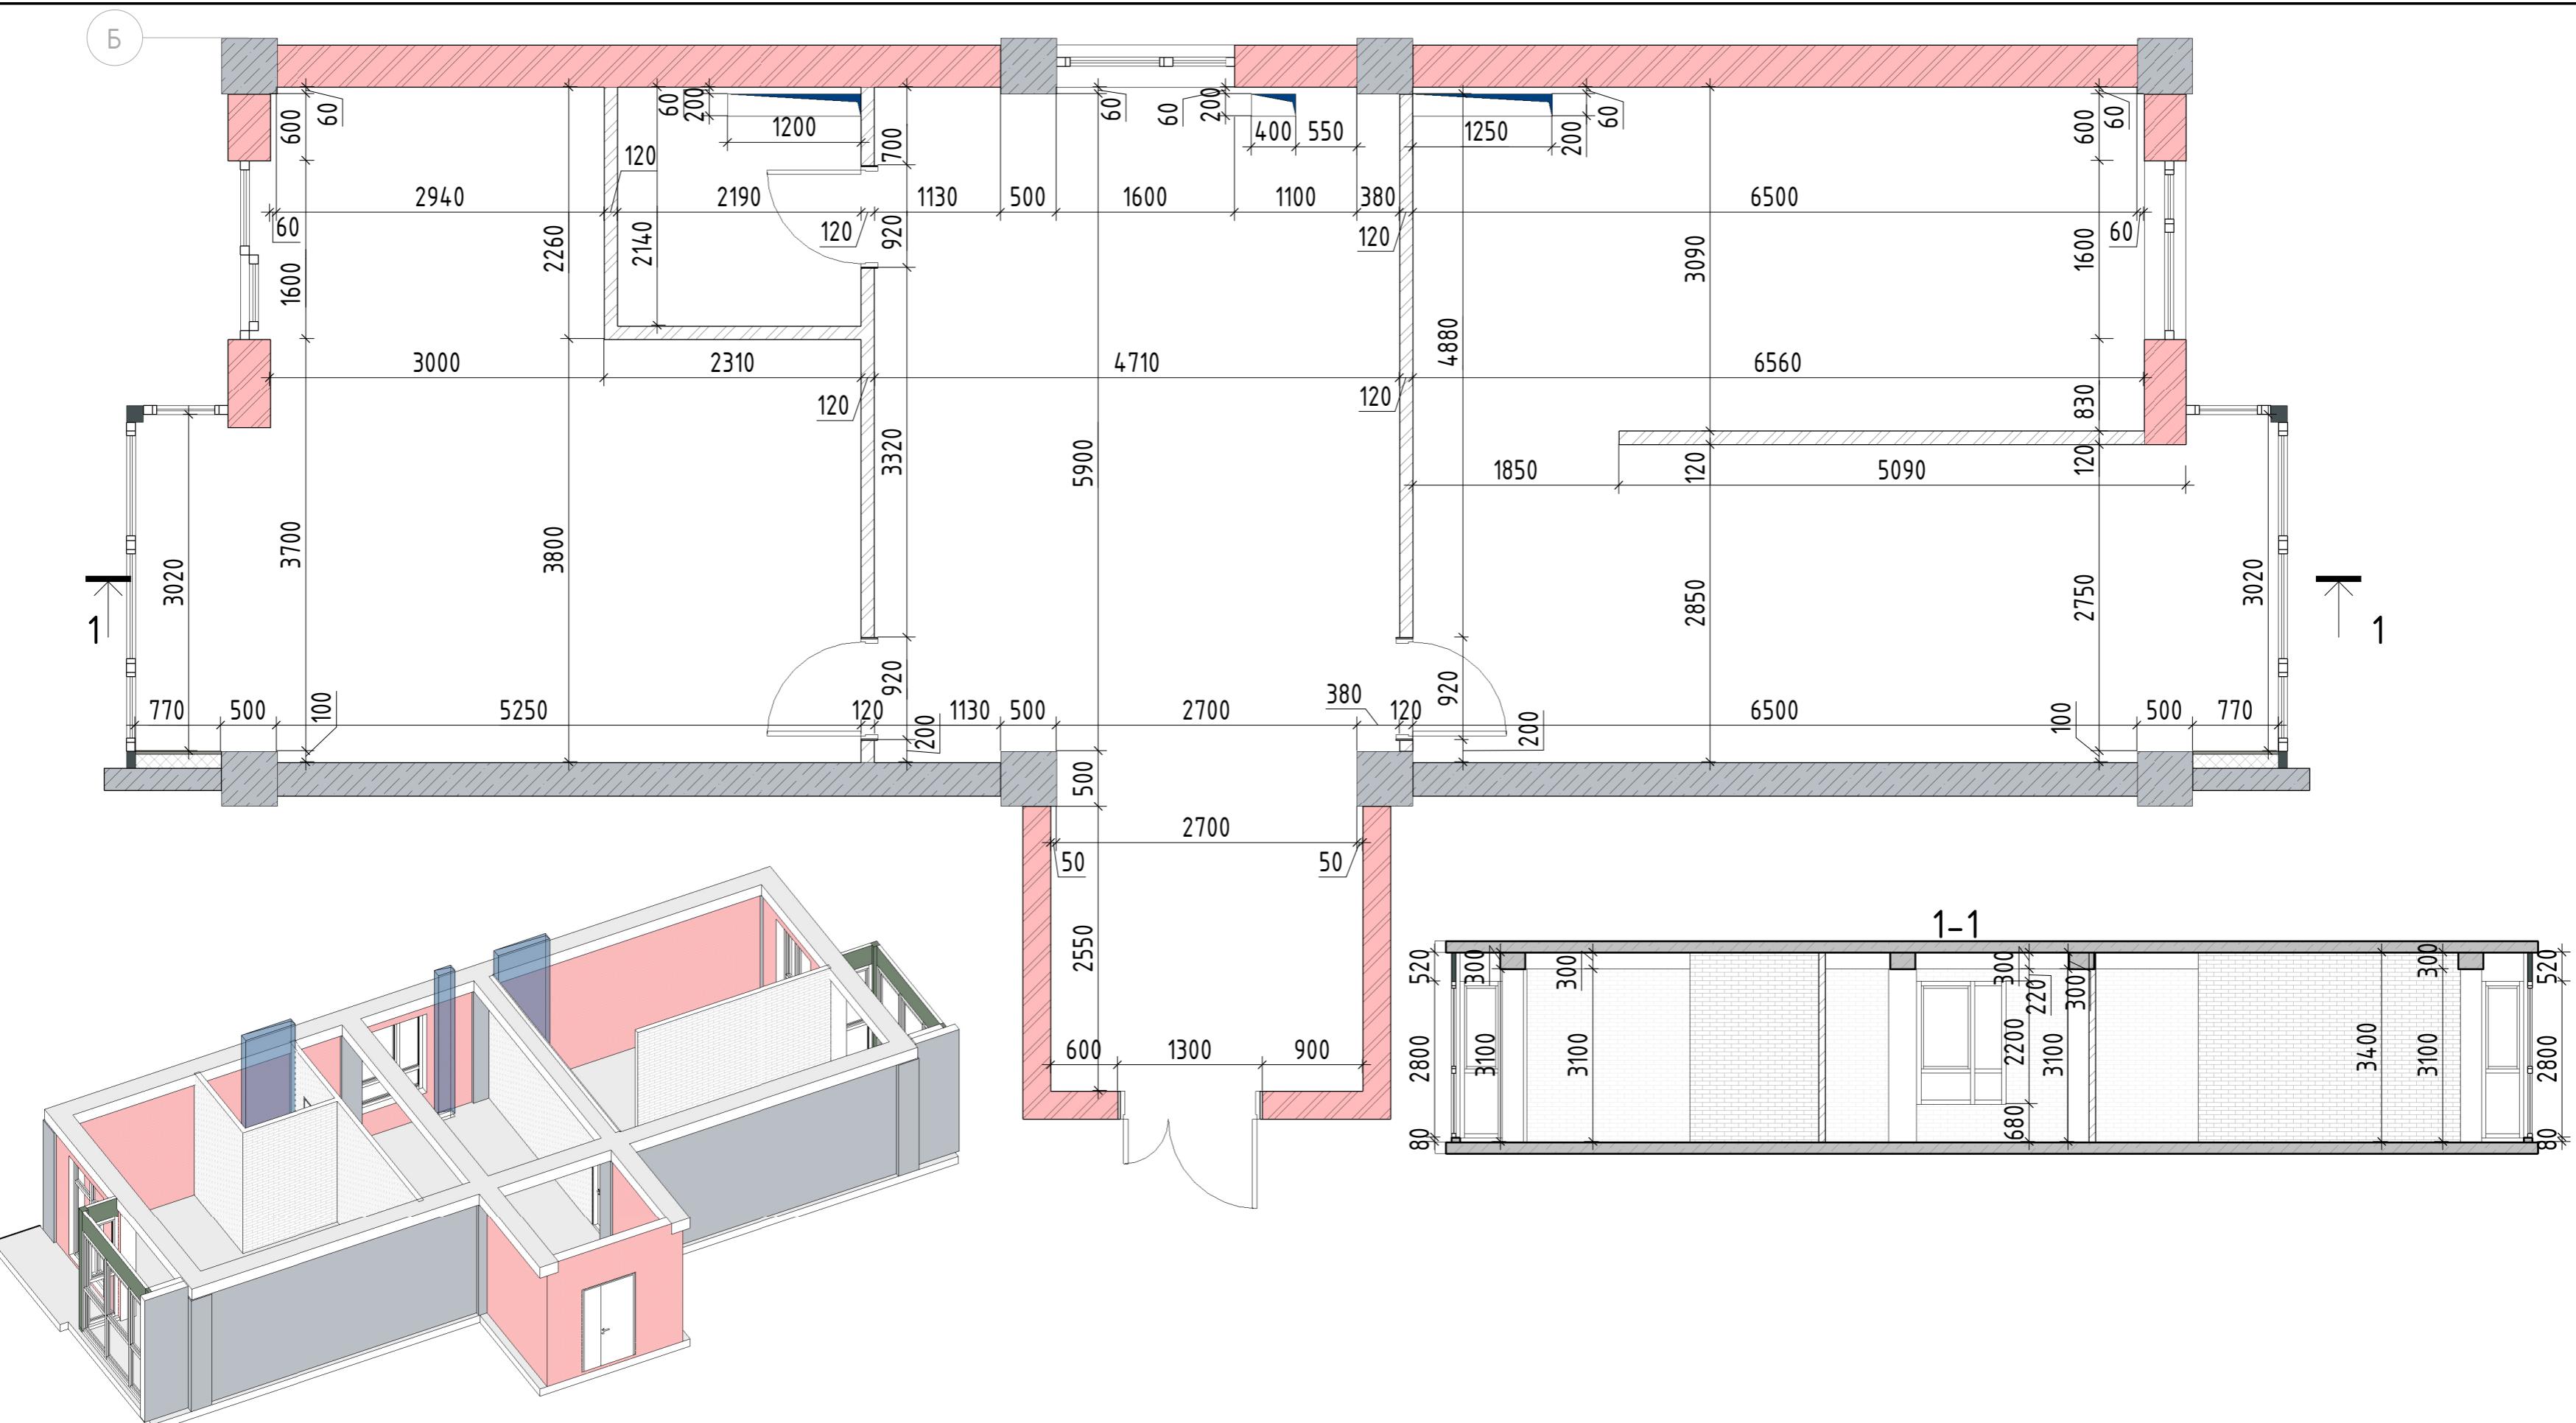



Примечания:

1. За отмечку 0.000 принята отмечка чистого пола проектируемых помещений.
2. Размеры указаны в миллиметрах.
3. Размеры уточнять по месту.

Дизайнер			
Заказчик			

ОБМЕРНЫЙ ПЛАН

Б

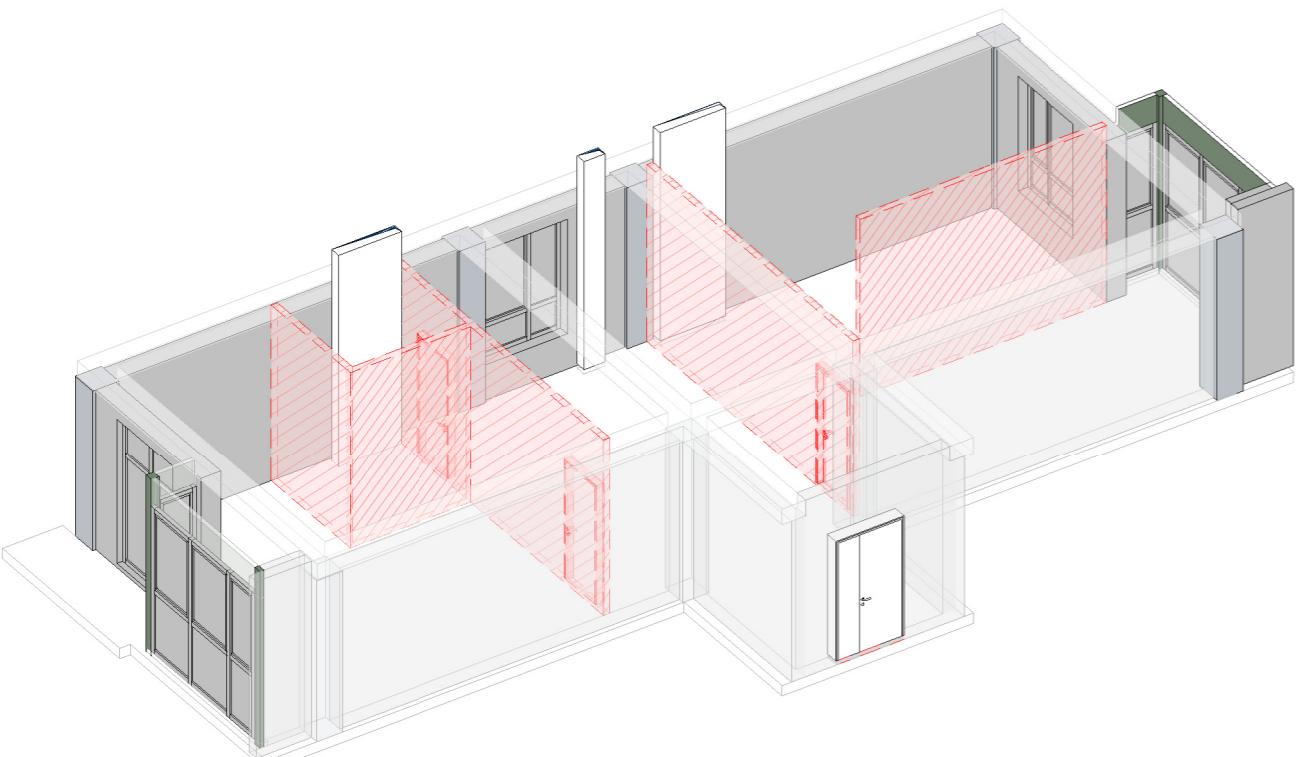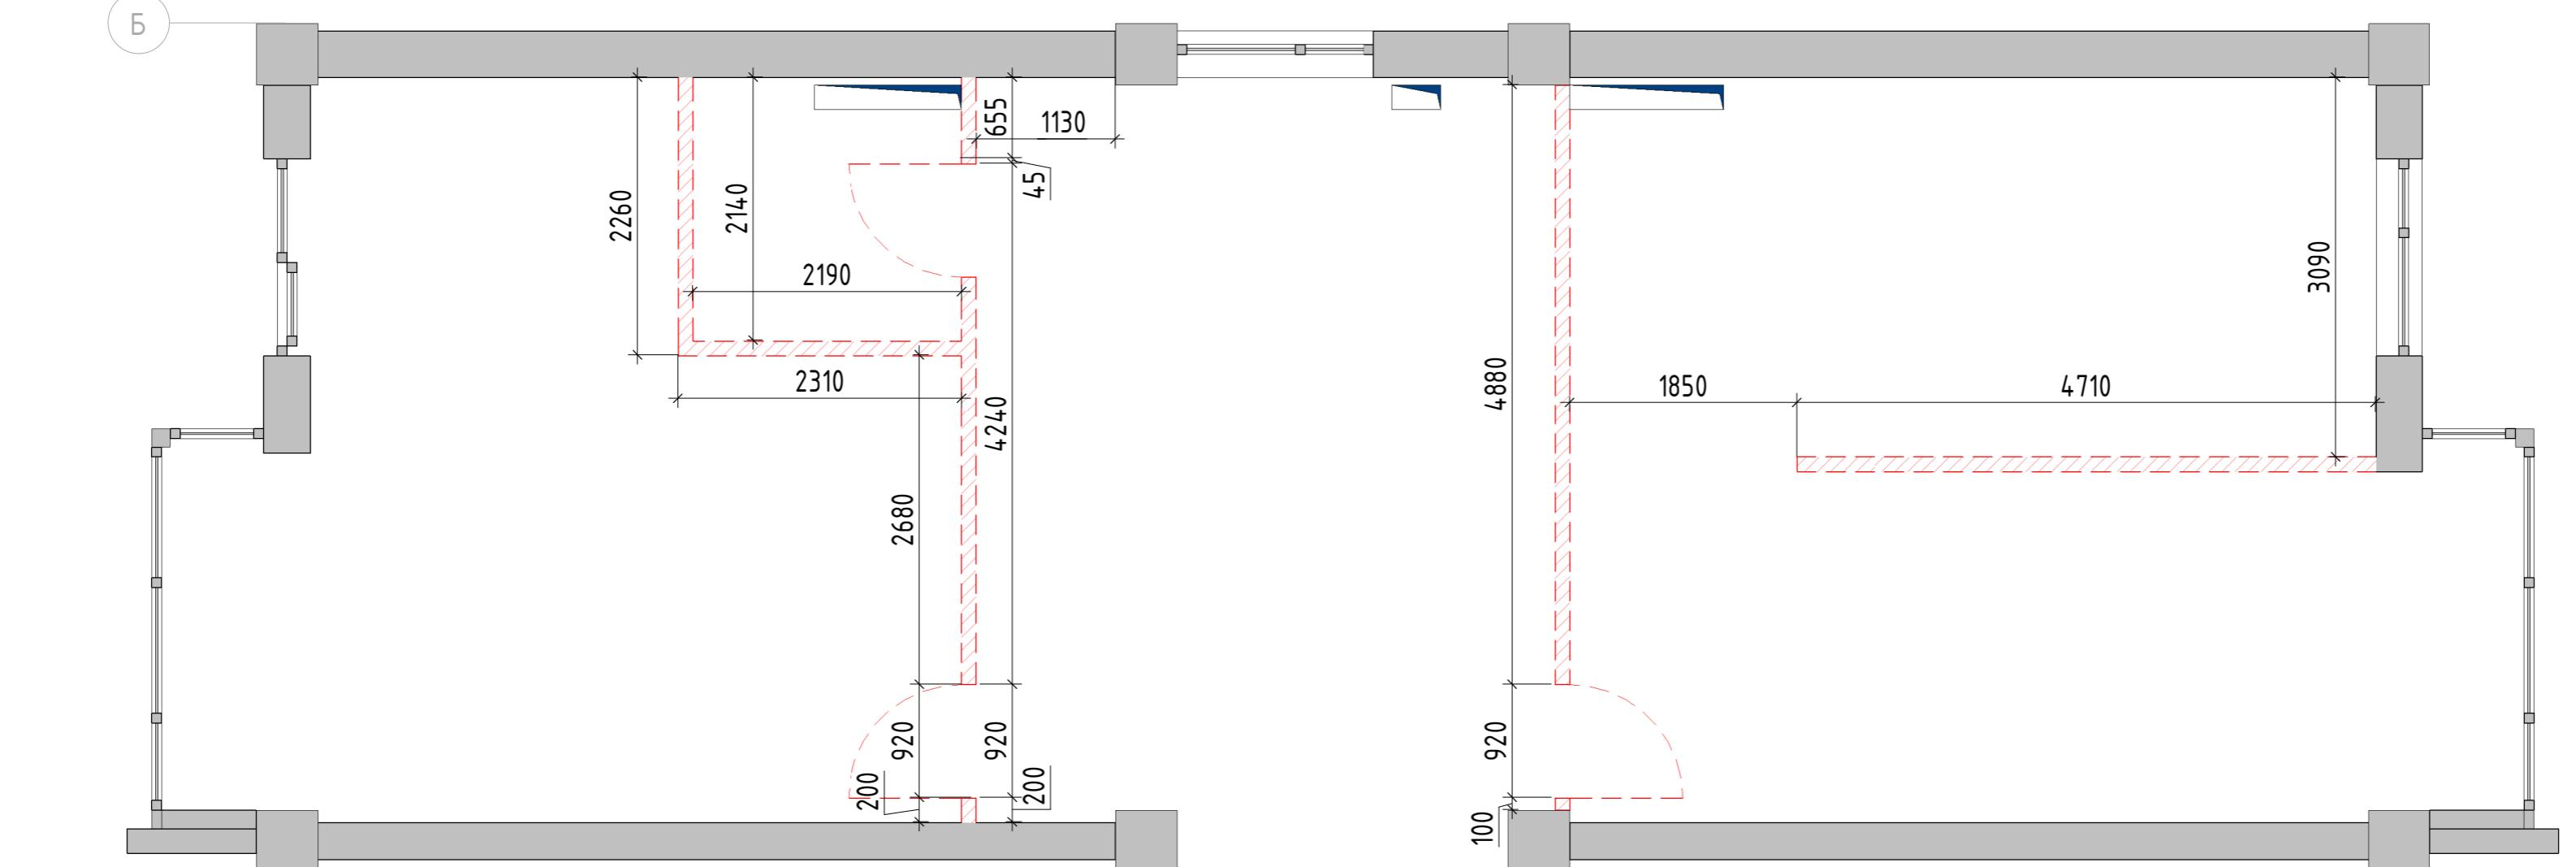

#### Условные обозначения:

- Существующие стены
- Демонтируемые перегородки

#### Примечания:

1. За отметку 0.000 принята отметка чистого пола проектируемых помещений.
2. Высота потолков \_\_\_\_\_.
3. Размеры даны в миллиметрах.
4. Фактические размеры могут незначительно отличаться. Проверить по месту.

Дизайнер			
Заказчик			

ПЛАН ДЕМОНТАЖА  
ПЕРЕГОРОДОК

Luxhouse\_studio


Формат: А3

Стадия

Лист

Листов

АИ

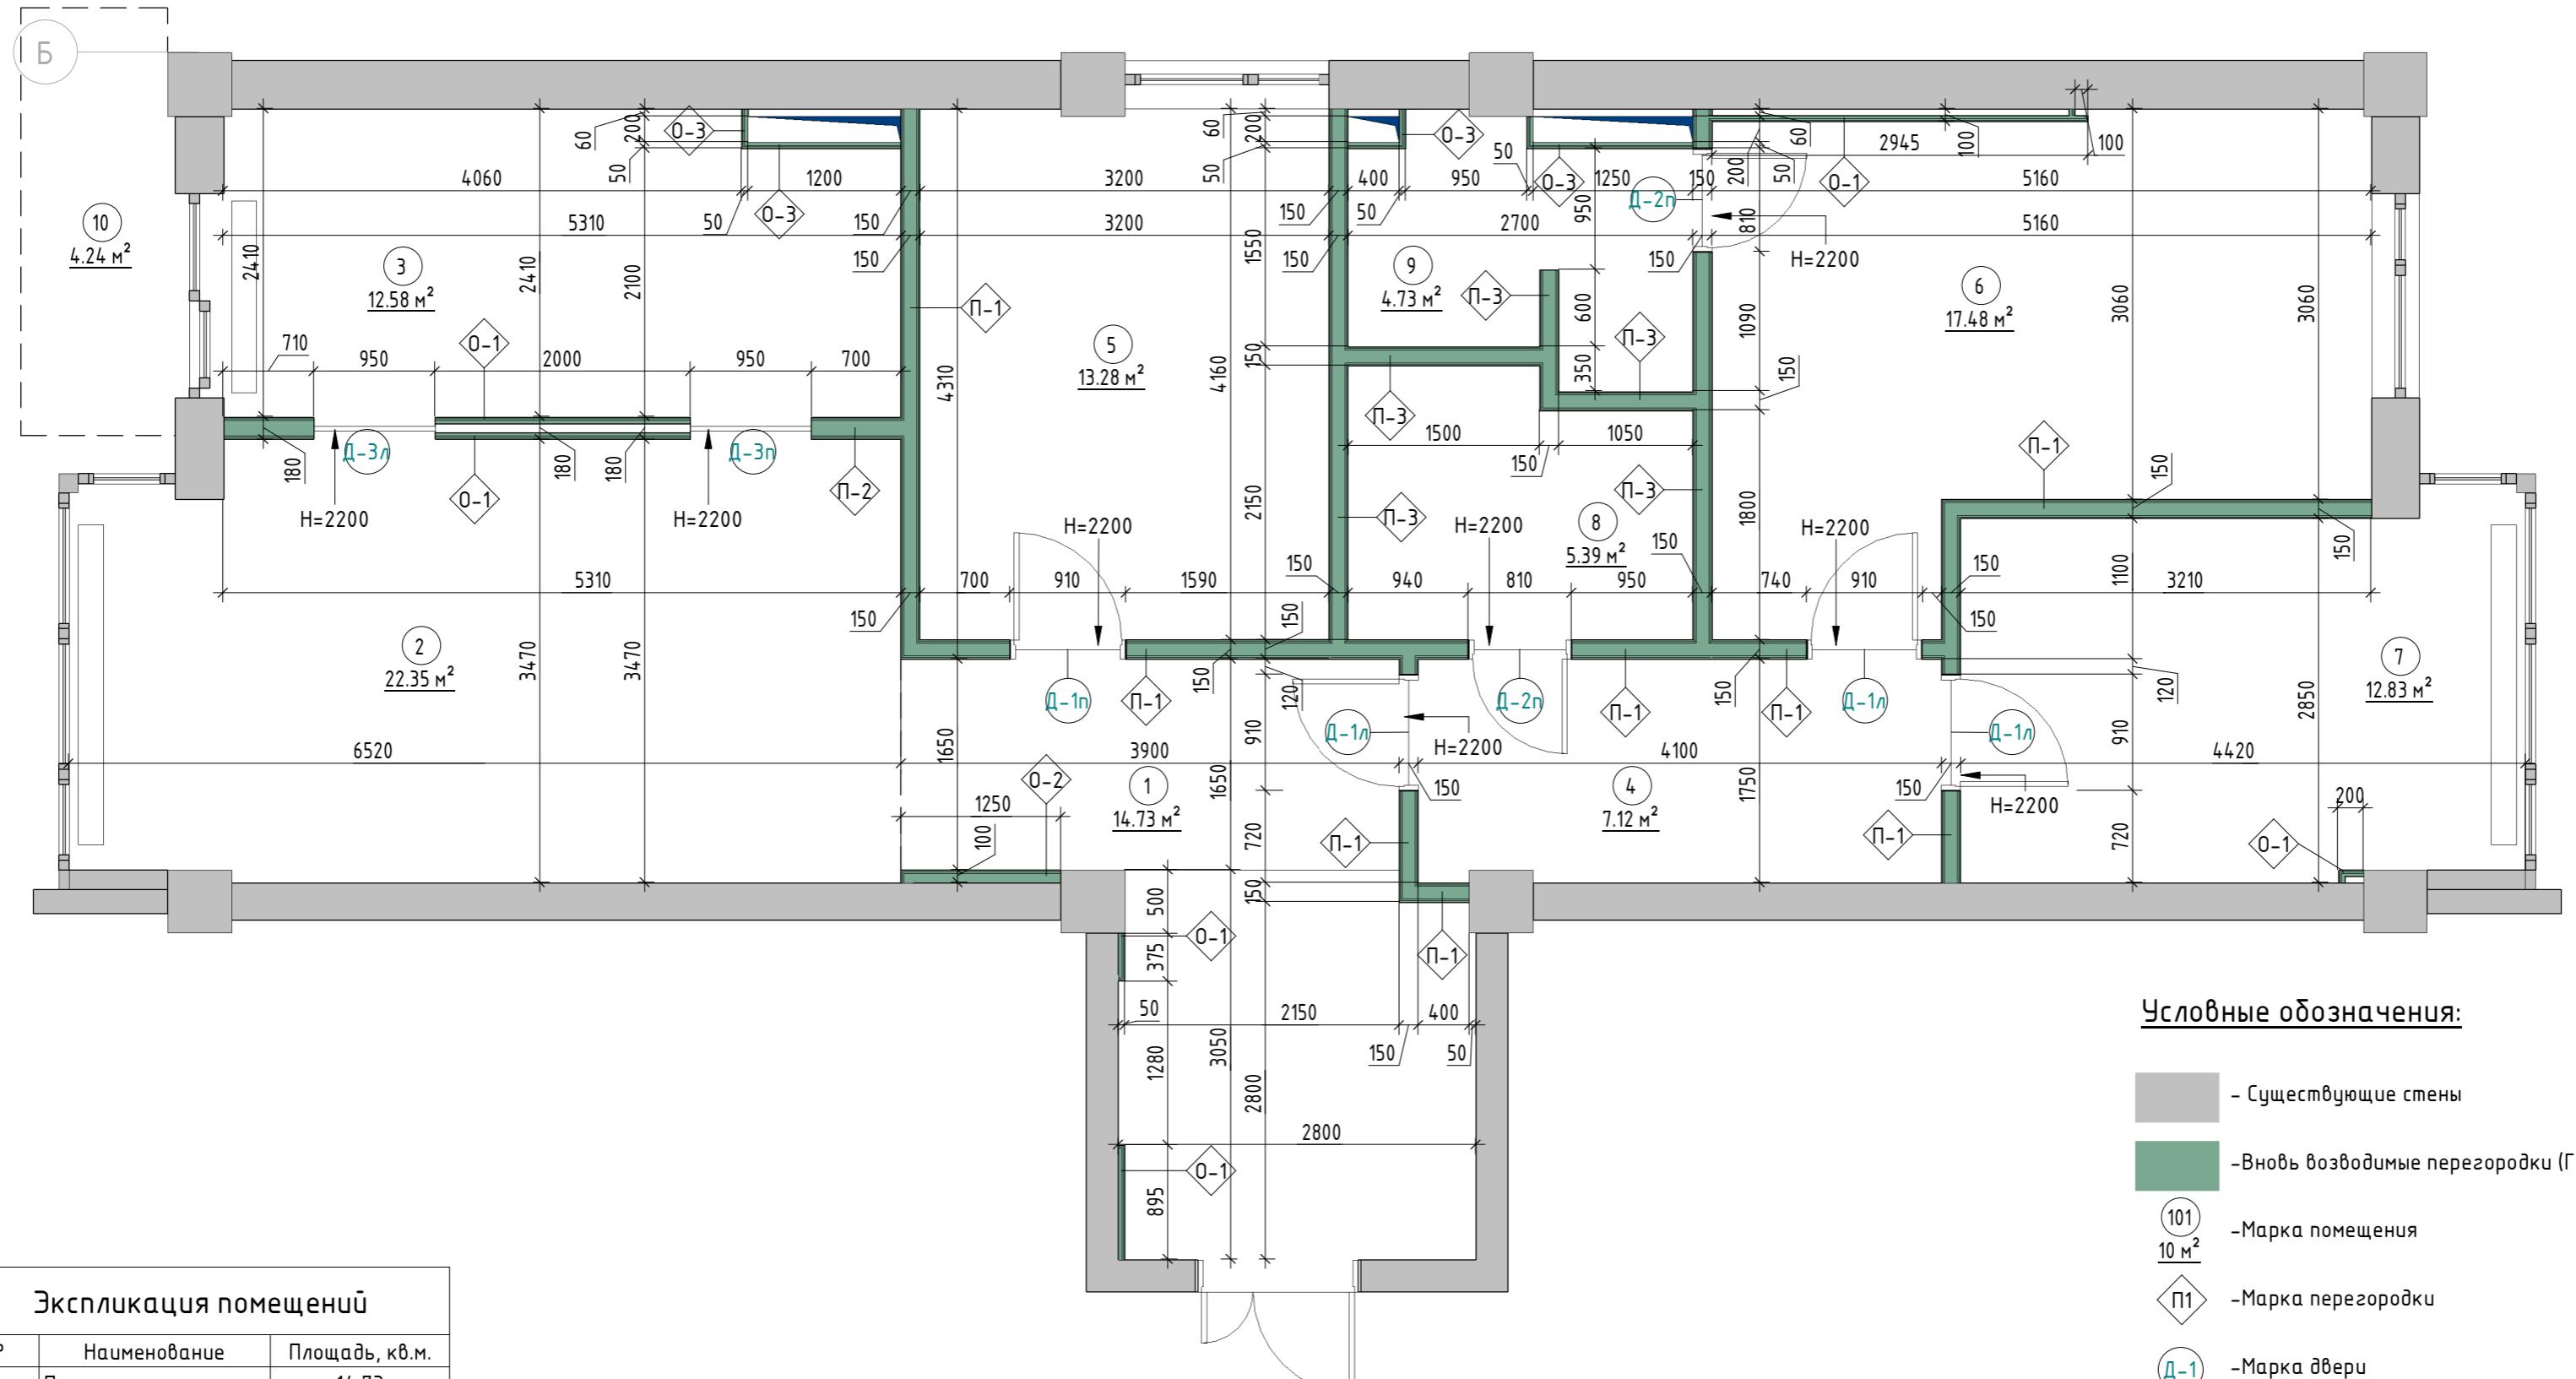

Экстракция волчаника

Экспликация помещений		
№	Наименование	Площадь, кв.м.
1	Прихожая	14.73
2	Гостиная	22.35
3	Кухня	12.58
4	Коридор	7.12
5	Спальня	13.28
6	Спальня	17.48
7	Спальня	12.83
8	Санузел	5.39
9	Санузел	4.73
10	Балкон	4.24
		114.73

## Условные обозначения:

- Существующие стены
  - Вновь возводимые перегородки (ГКЛ)
    - Марка помещения
    - Марка перегородки
    - Марка двери

### Примечания:



1. За отметку 0.000 принята отметка чистого пола проектируемых помещений.
  2. Размеры указаны в миллиметрах.
  3. Размеры точняться по месту.

Дизайнер			
Заказчик			

## ПЛАН МОНТАЖА ПЕРЕГОРОДОК



Luxhouse studio

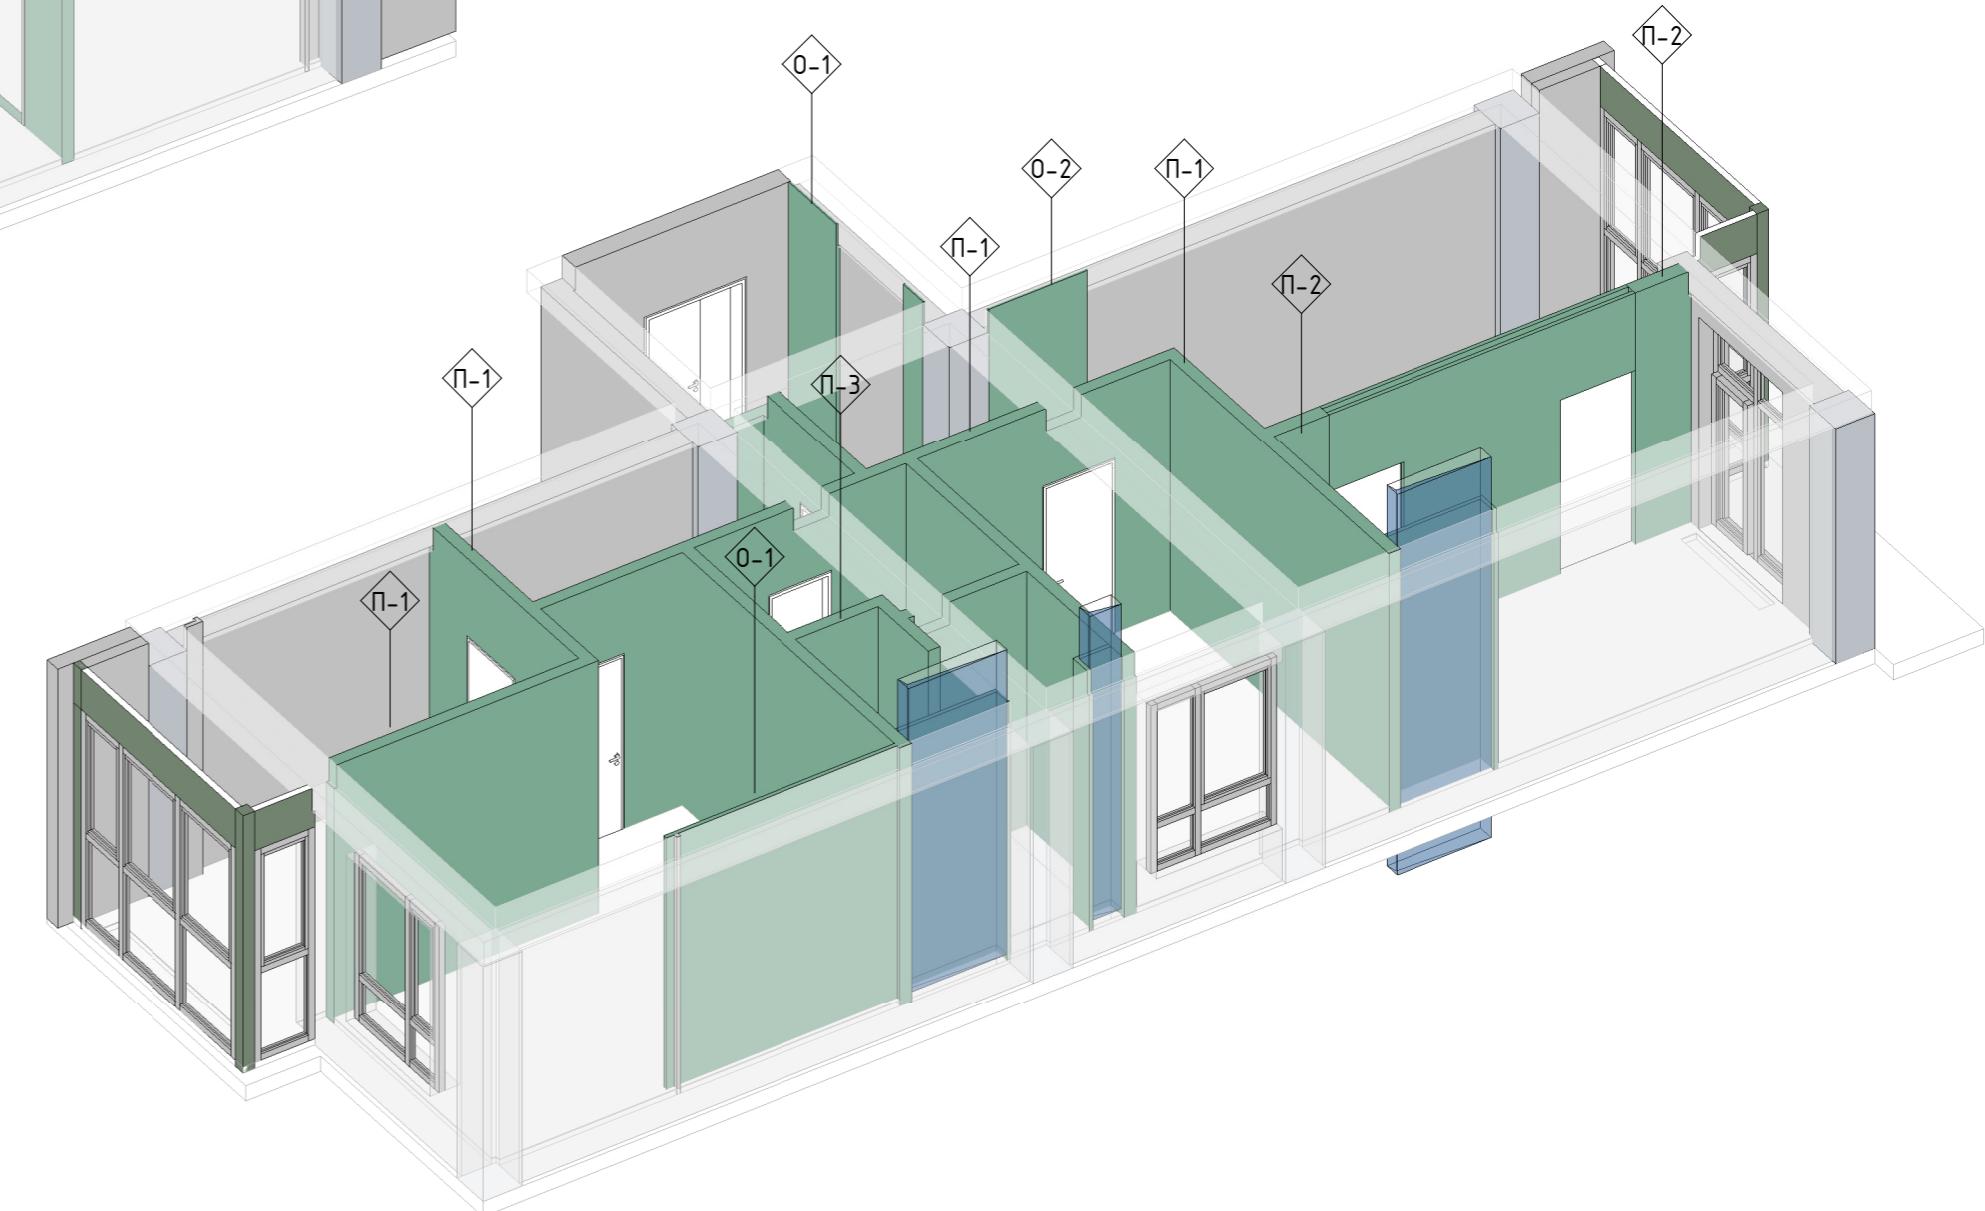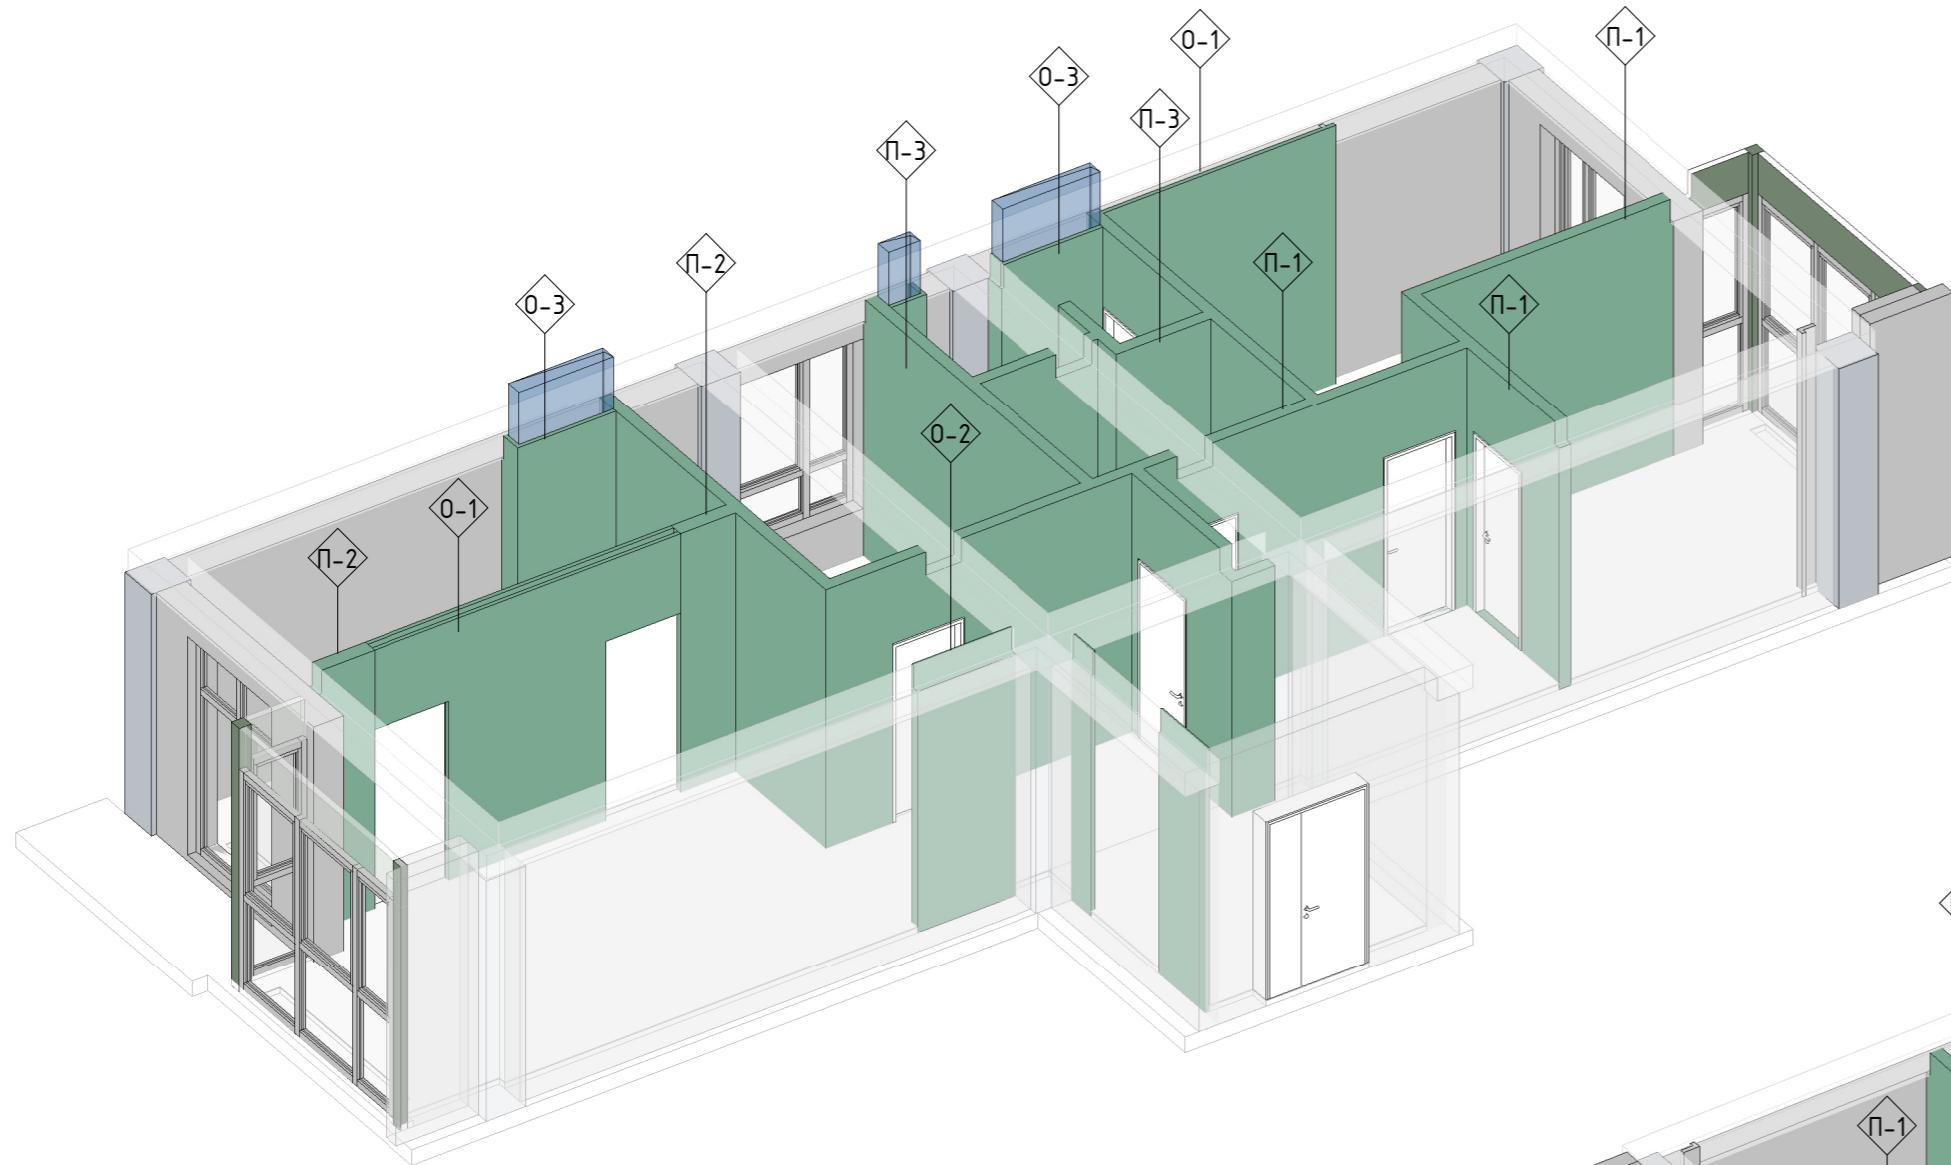


Условные обозначения:

- Существующие стены
- Вновь возводимые перегородки (ГКЛ)
- (101)  
10 м<sup>2</sup> — Марка помещения
- П-1 — Марка перегородки
- Д-1 — Марка двери

Дизайнер			
Заказчик			

3D ВИД ПЛАН МОНТАЖА  
ПЕРЕГОРОДОК

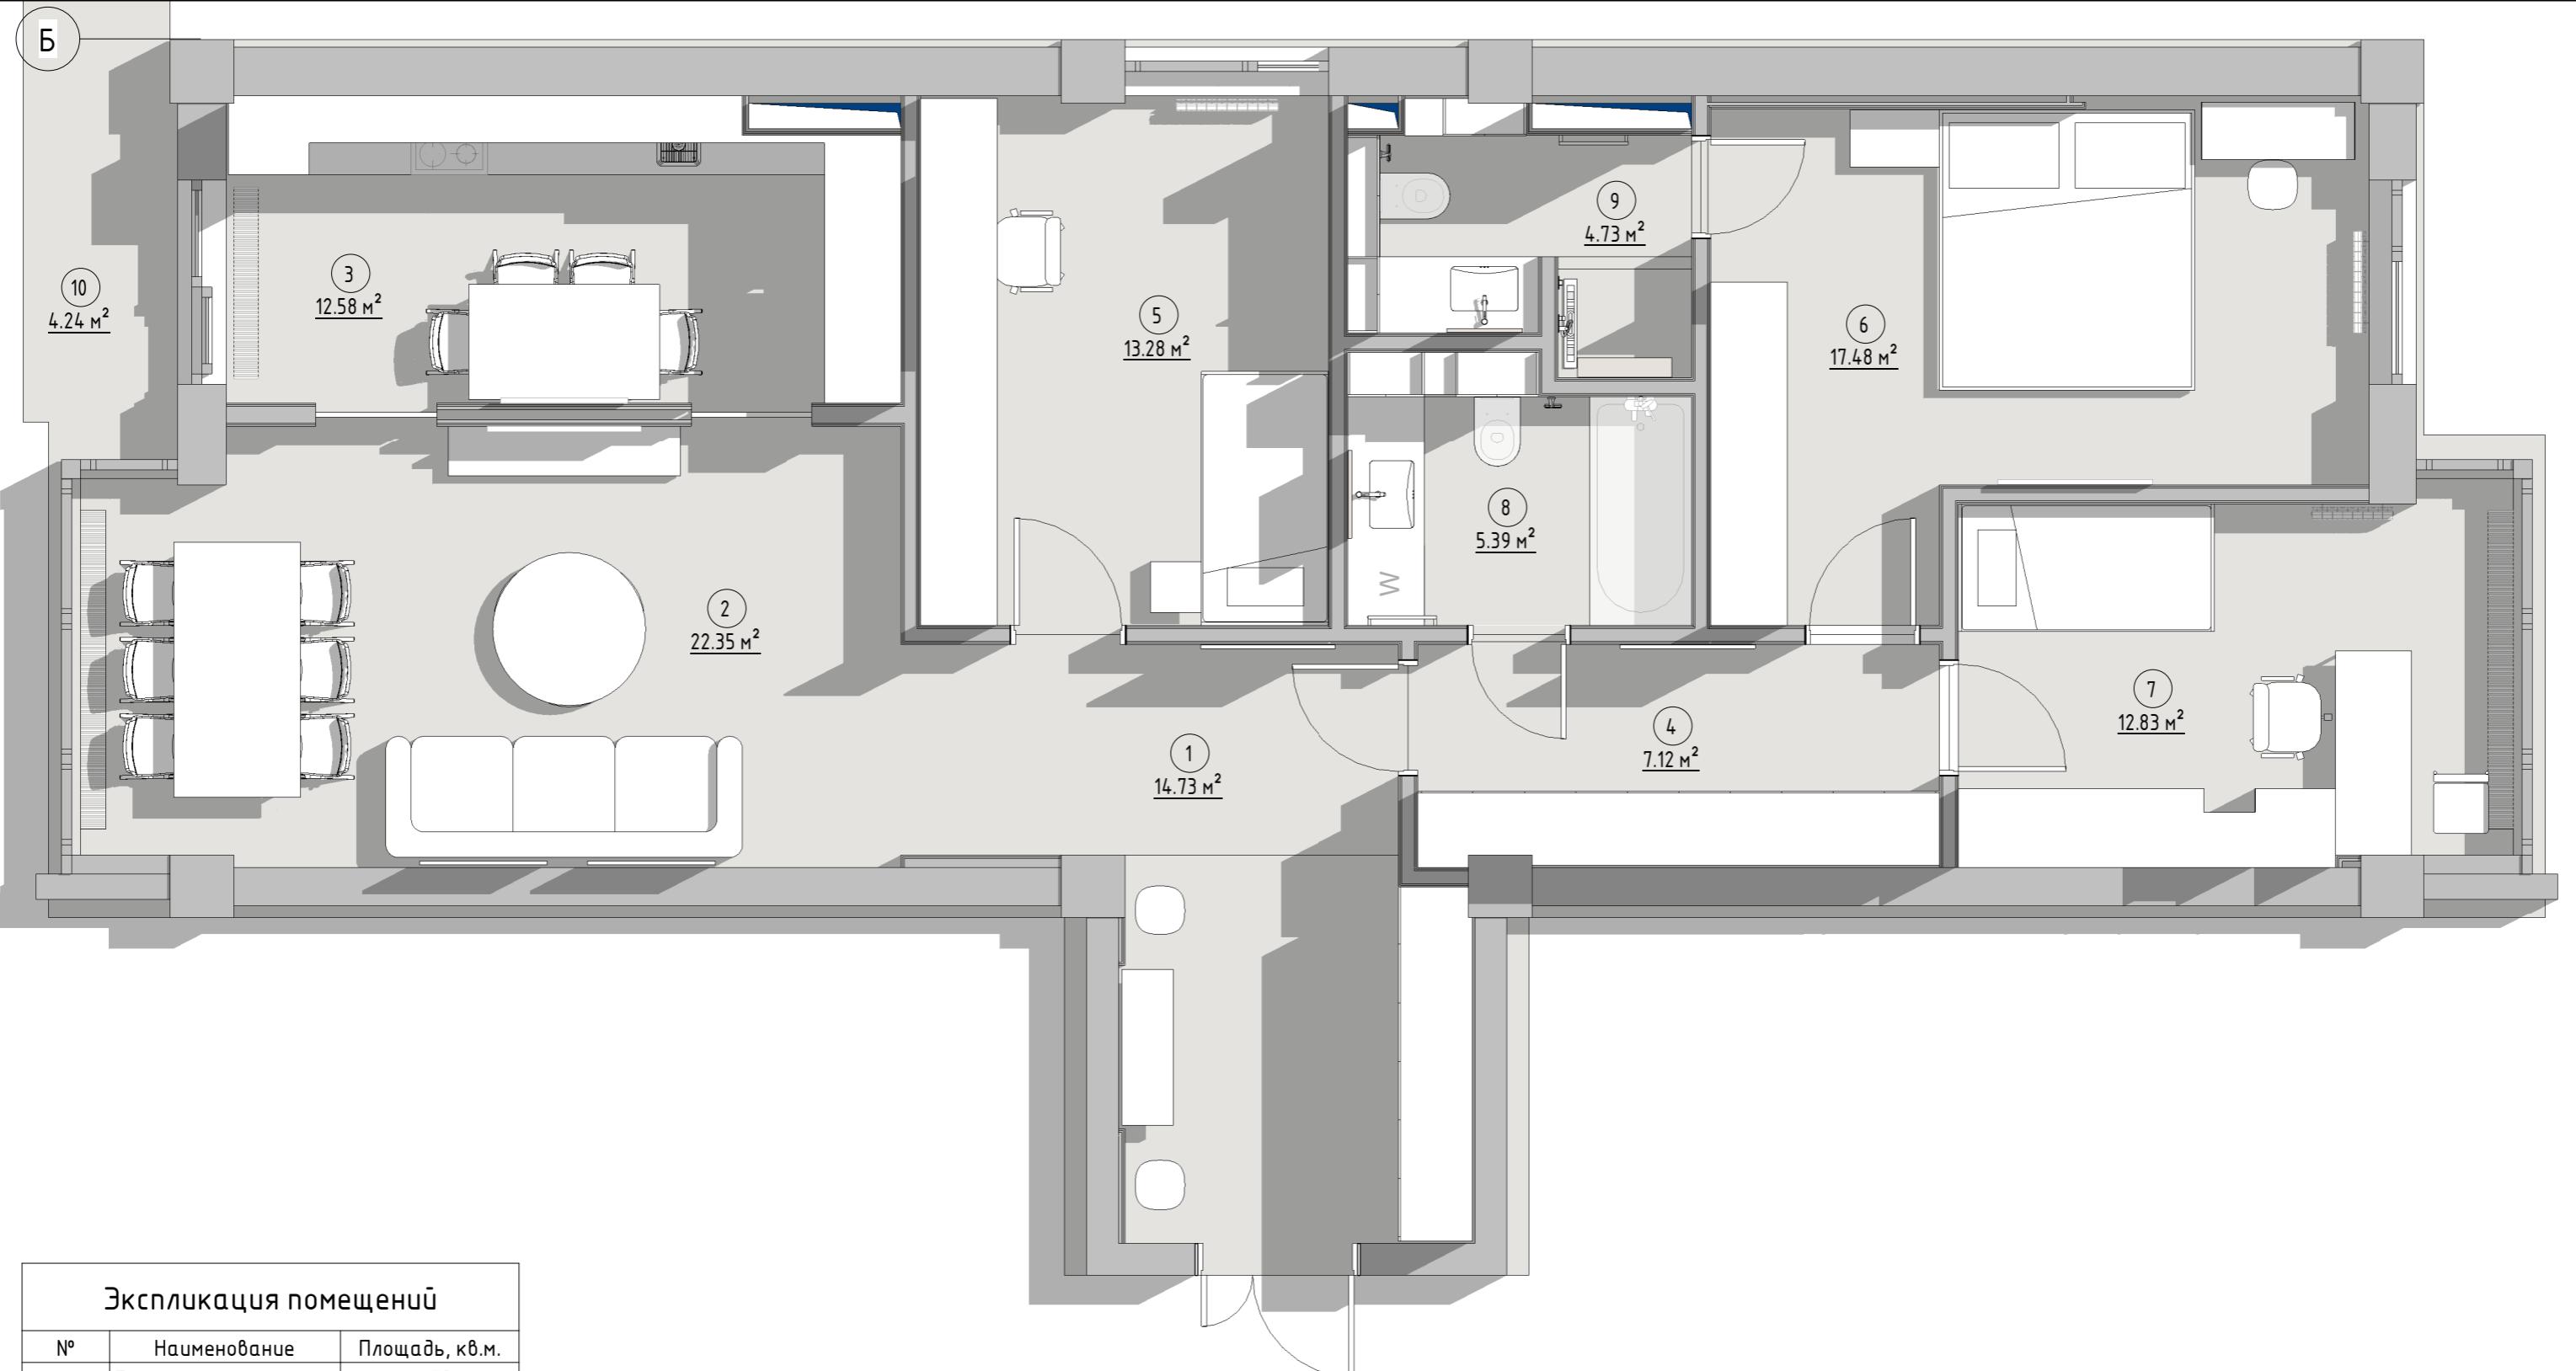


#### Экспликация помещений

№	Наименование	Площадь, кв.м.
1	Прихожая	14.73
2	Гостиная	22.35
3	Кухня	12.58
4	Коридор	7.12
5	Спальня	13.28
6	Спальня	17.48
7	Спальня	12.83
8	Санузел	5.39
9	Санузел	4.73
10	Балкон	4.24
		114.73

Стадия	Лист	Листов
Дизайнер		
Заказчик		
АИ		

ПЛАН РАССТАНОВКИ МЕБЕЛИ

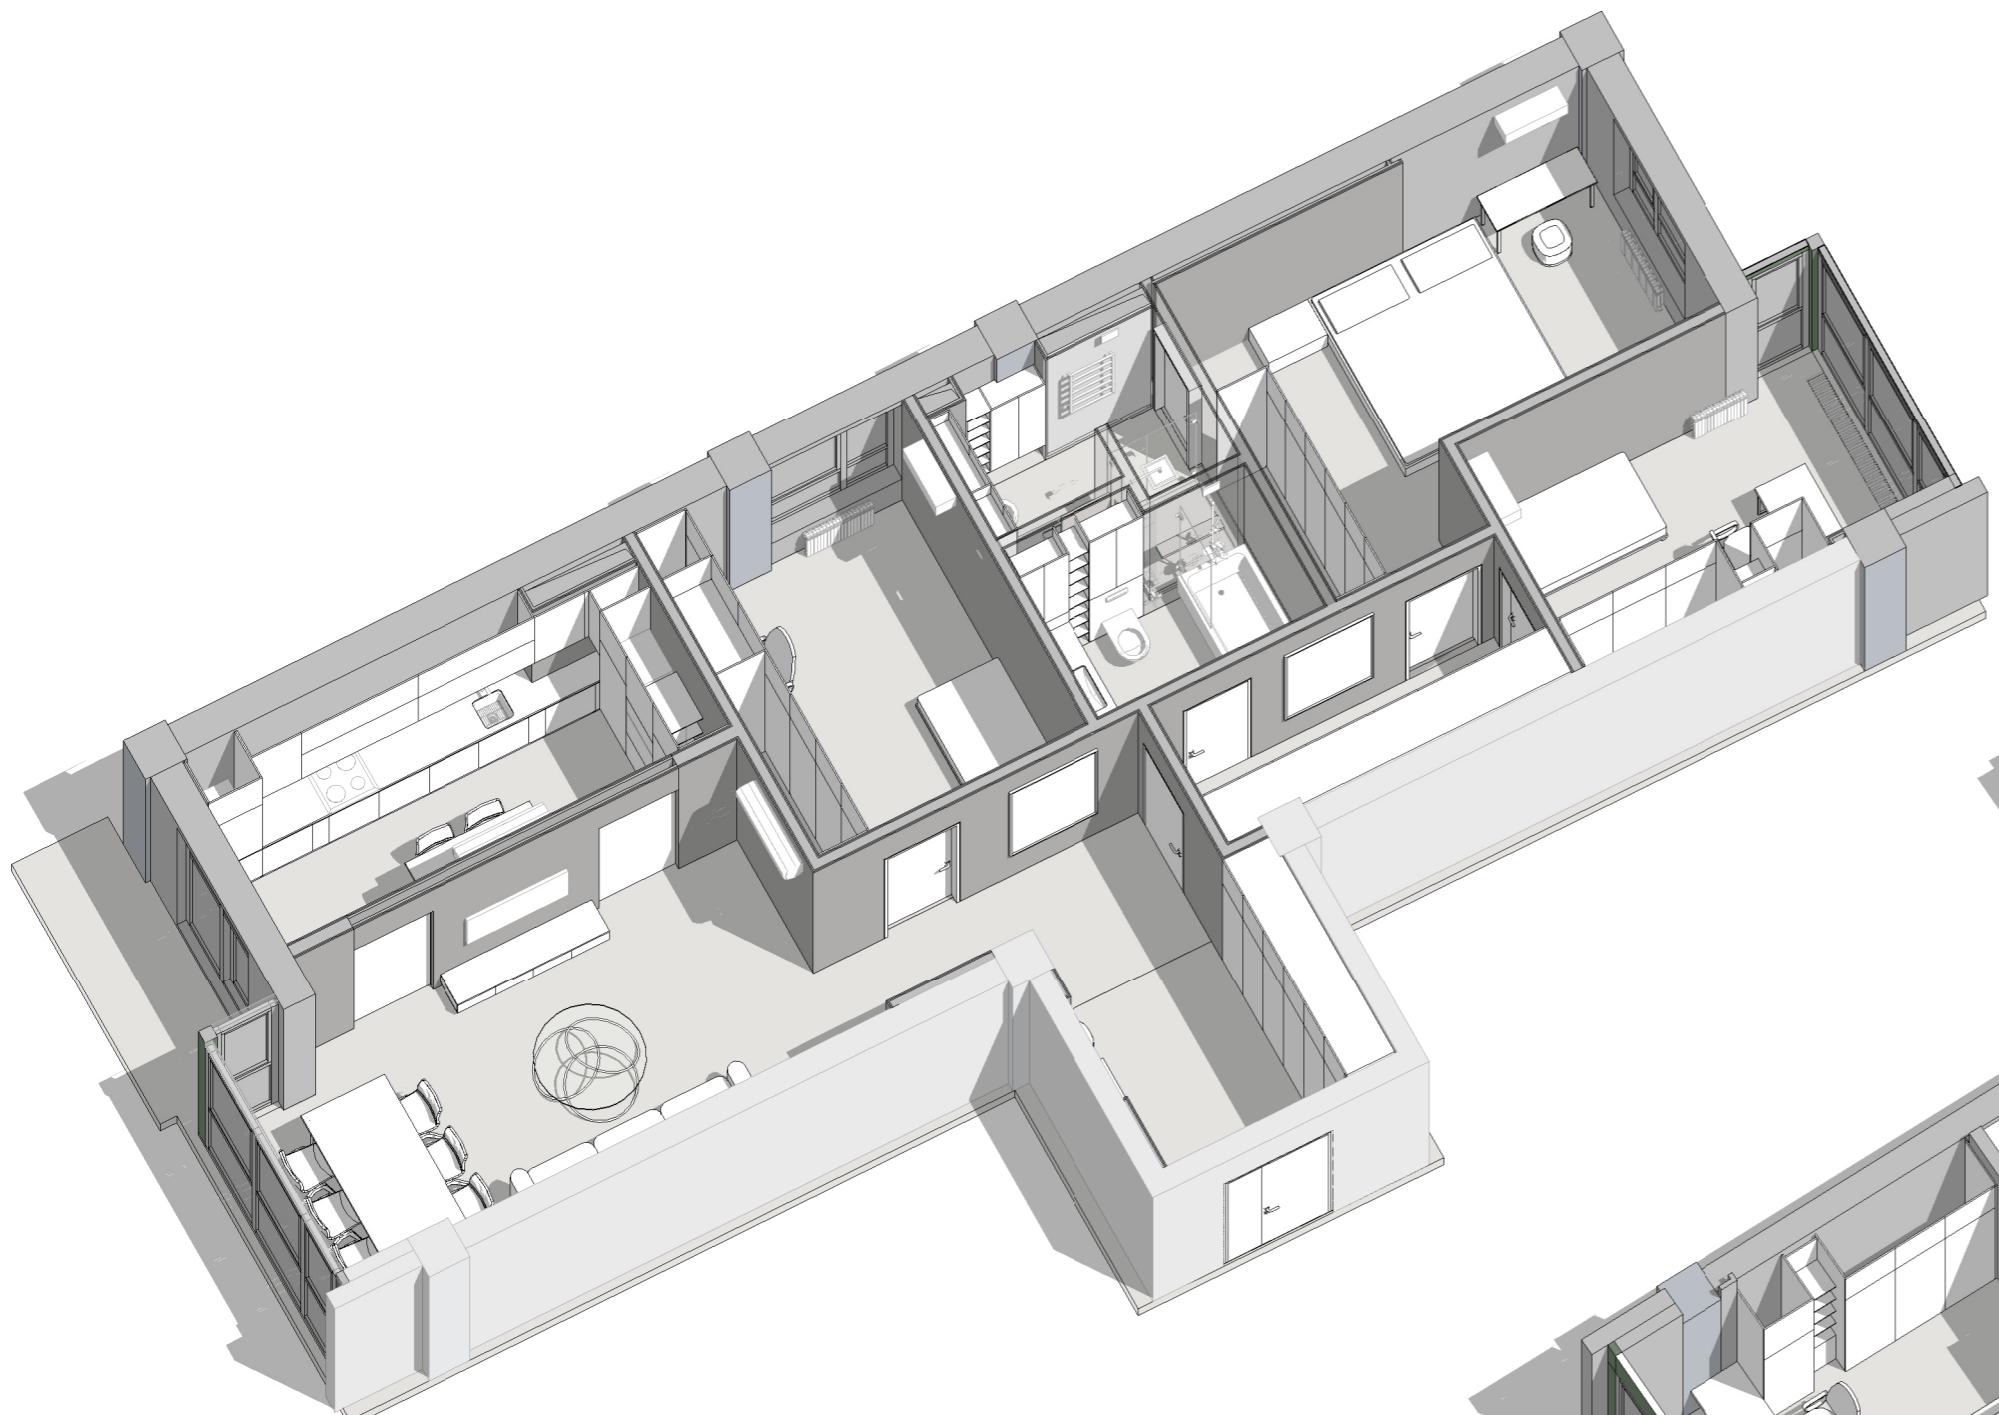

Дизайнер			
Заказчик			


3D ВИД РАССТАНОВКИ  
МЕБЕЛИ

Luxhouse\_studio

Формат: А3

Стадия      Лист      Листов

АИ

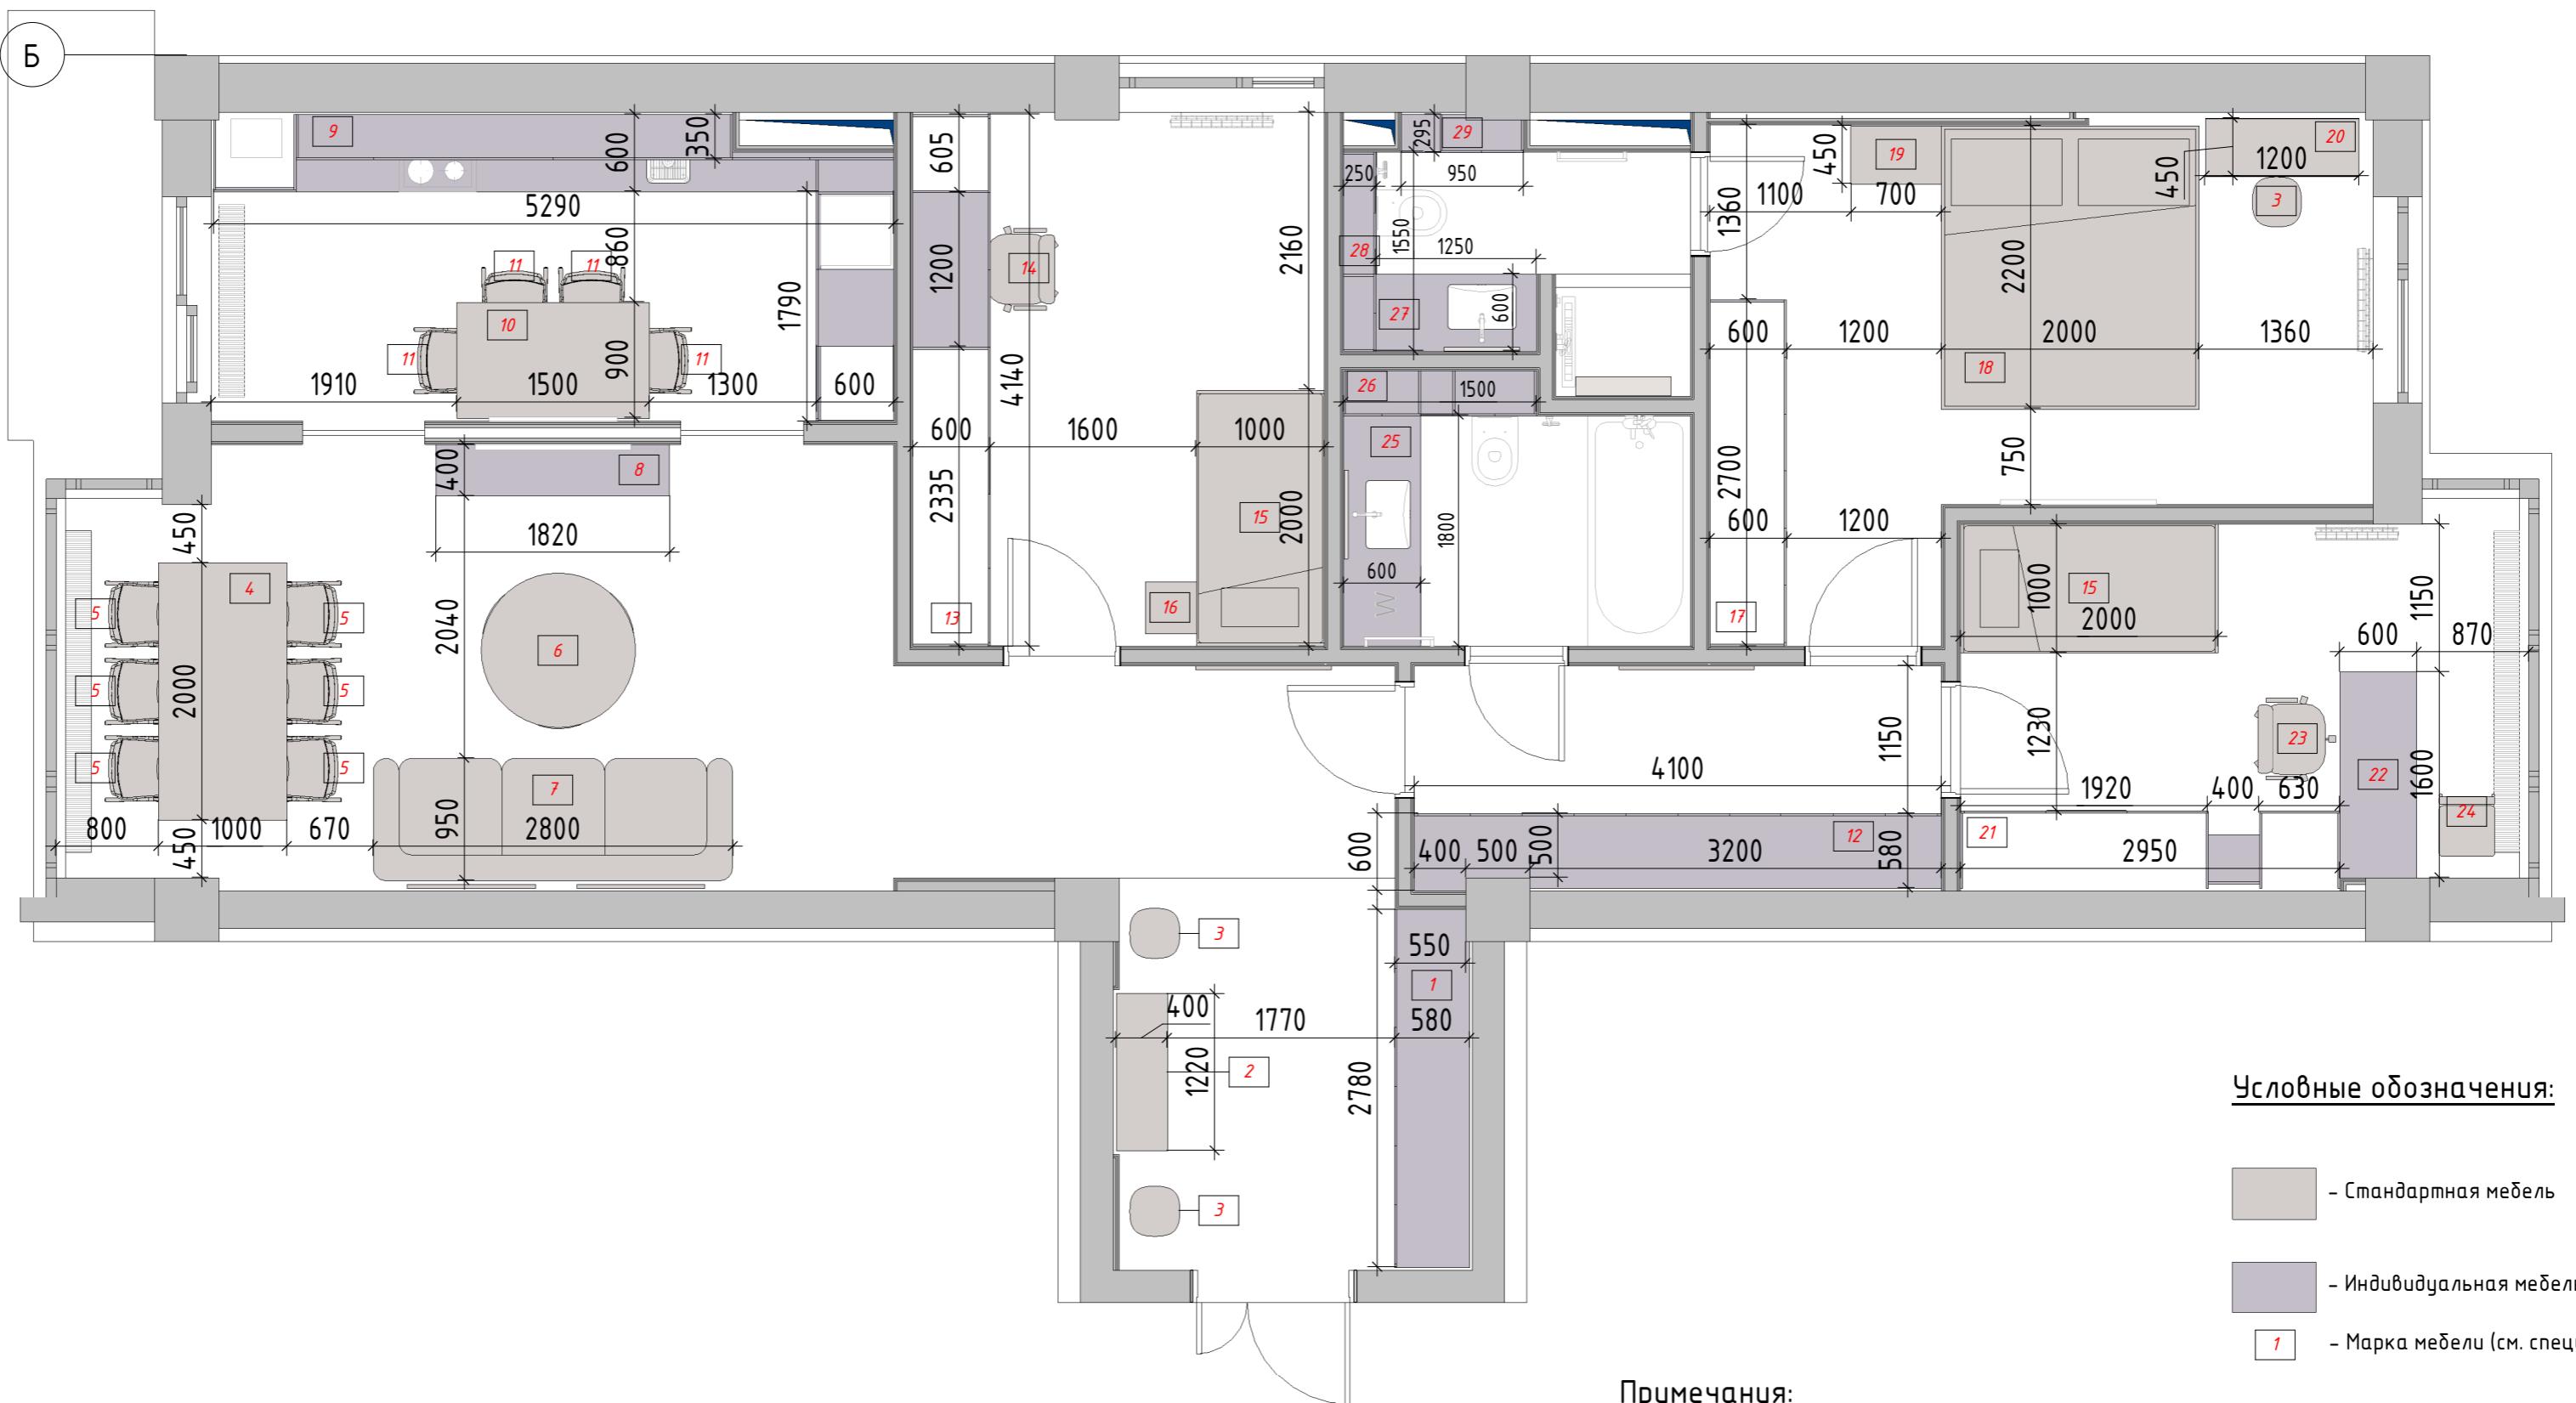

**Примечания:**

- За отметку 0.000 принята отметка чистого пола проектируемых помещений.
- Размеры указаны в миллиметрах.
- Размеры уточнять по месту.
- Смотреть совместно с развертками помещений.

Дизайнер			
Заказчик			

ПЛАН РАССТАНОВКИ МЕБЕЛИ  
С РАЗМЕРАМИ

Luxhouse\_studio


Формат: А3

Стадия


Лист

Листов

АИ

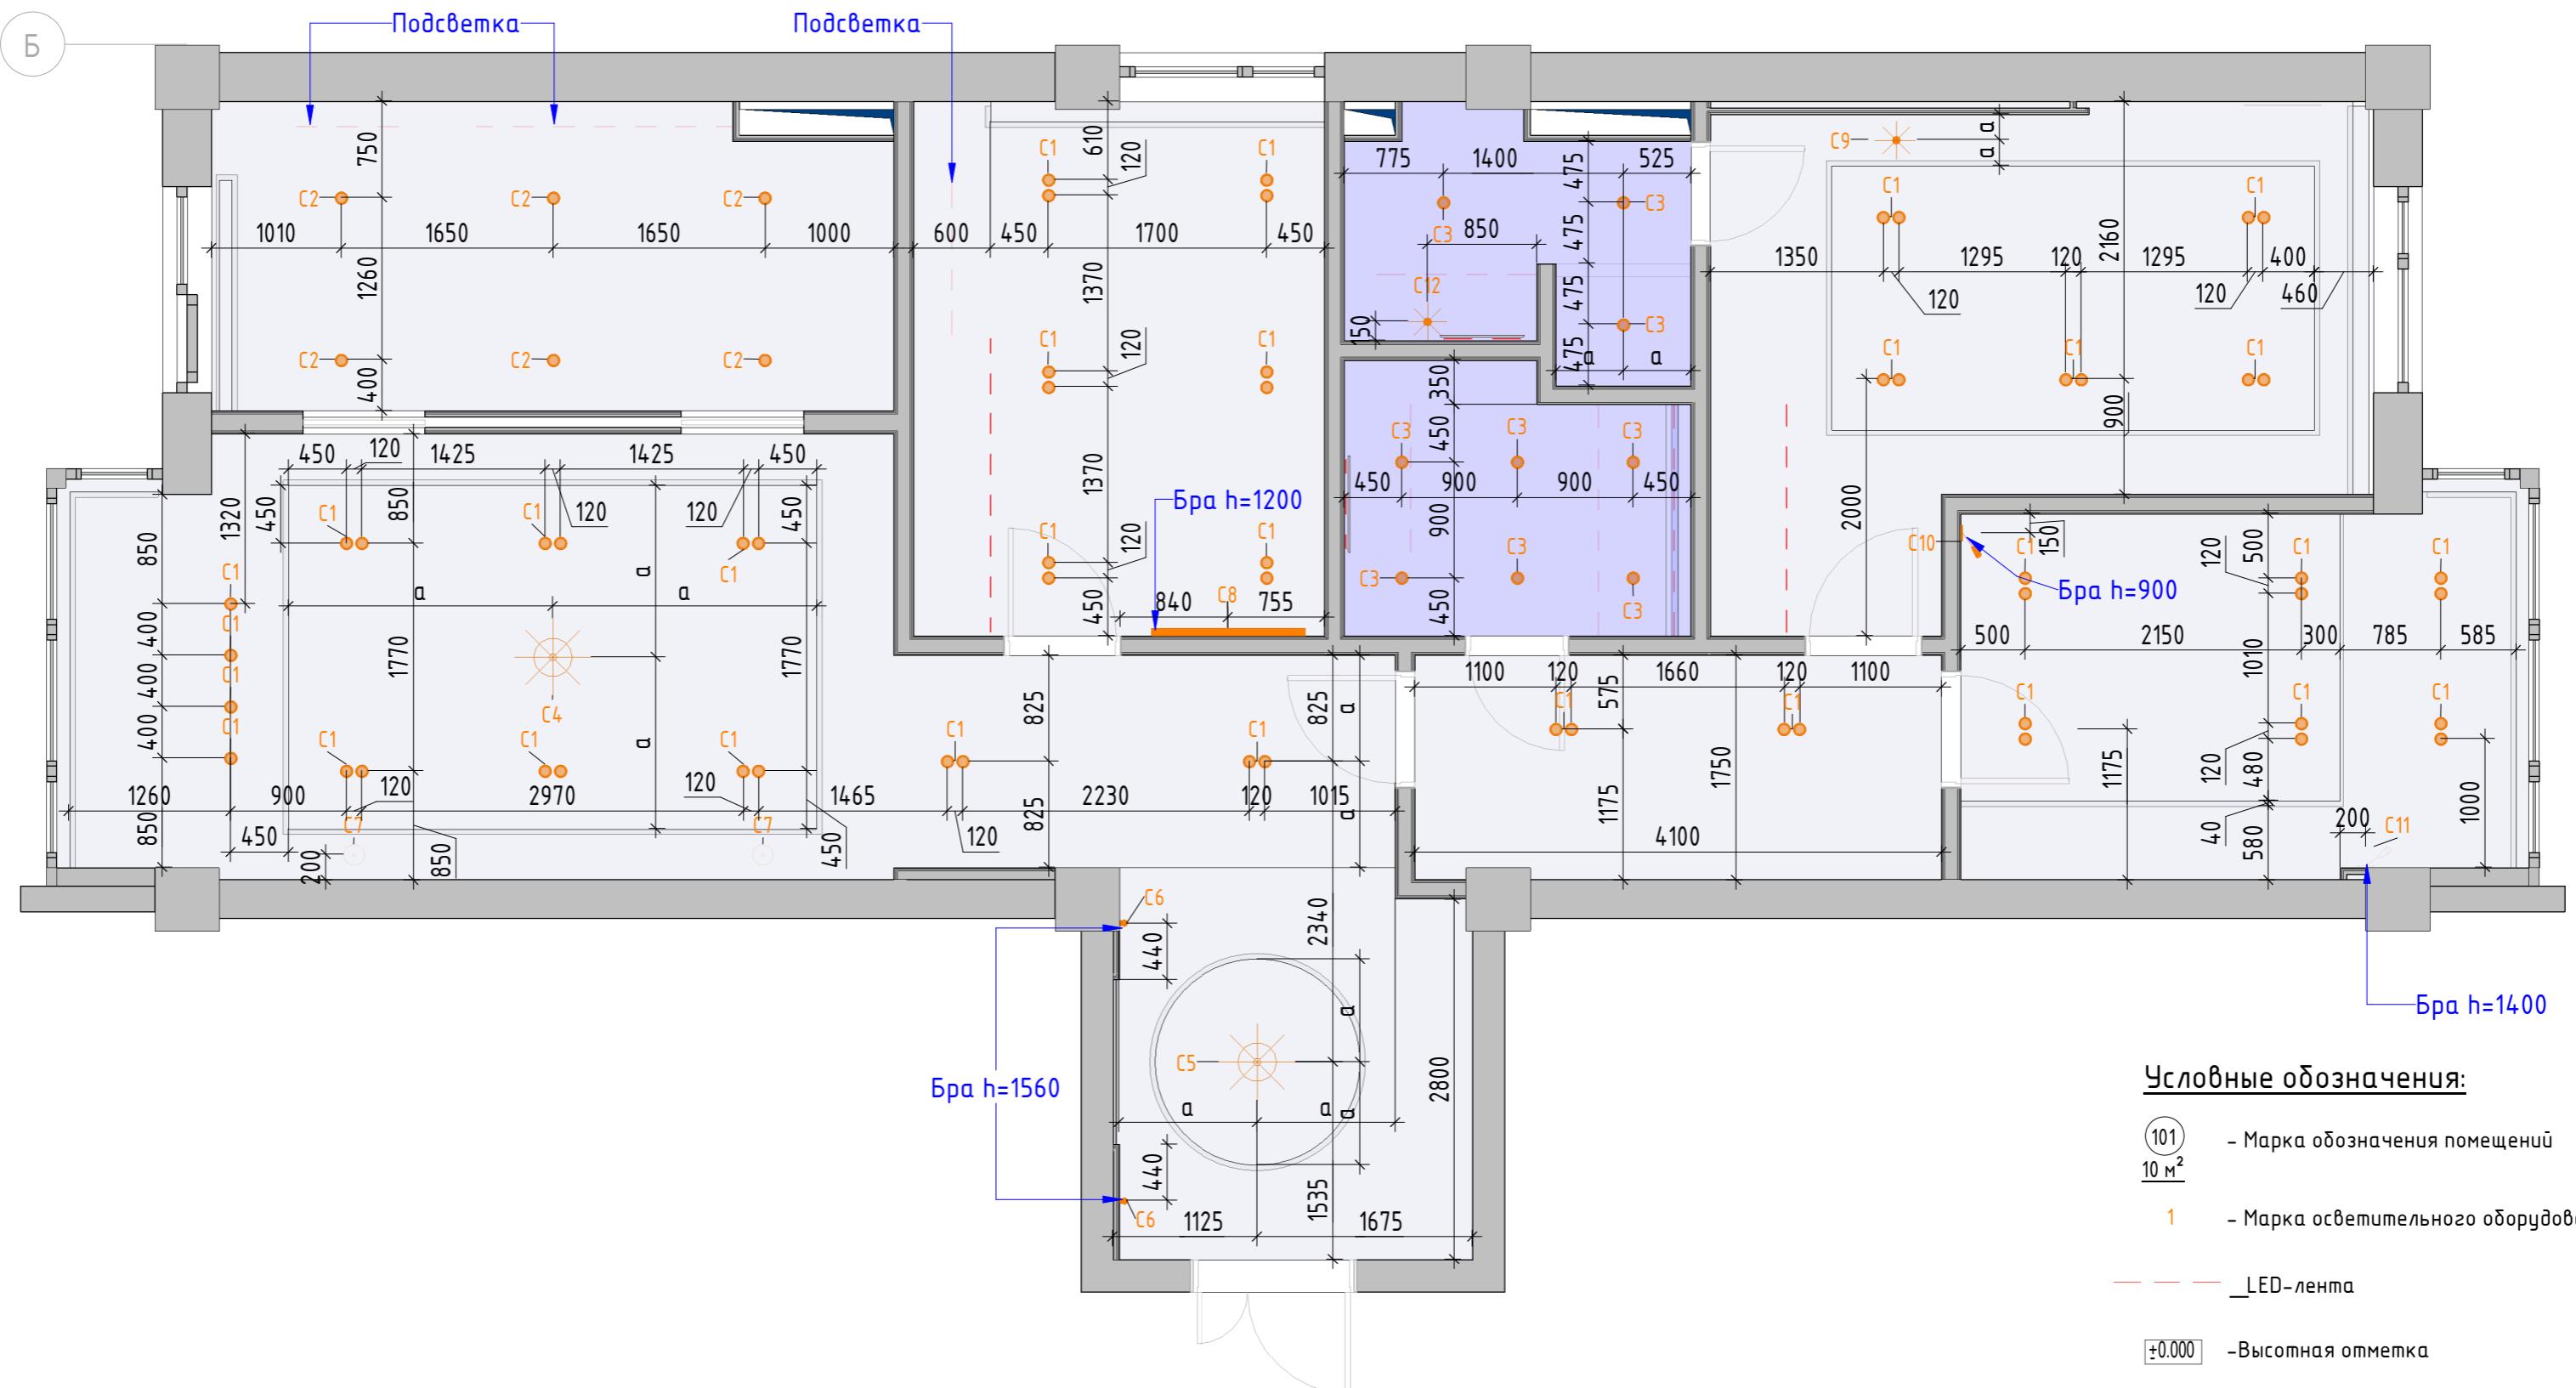

Стадия	Лист	Листов
АИ		
ПЛАН РАССТАНОВКИ ОСВЕТИТЕЛЬНОГО ОБОРУДОВАНИЯ		
Luxhouse_studio		

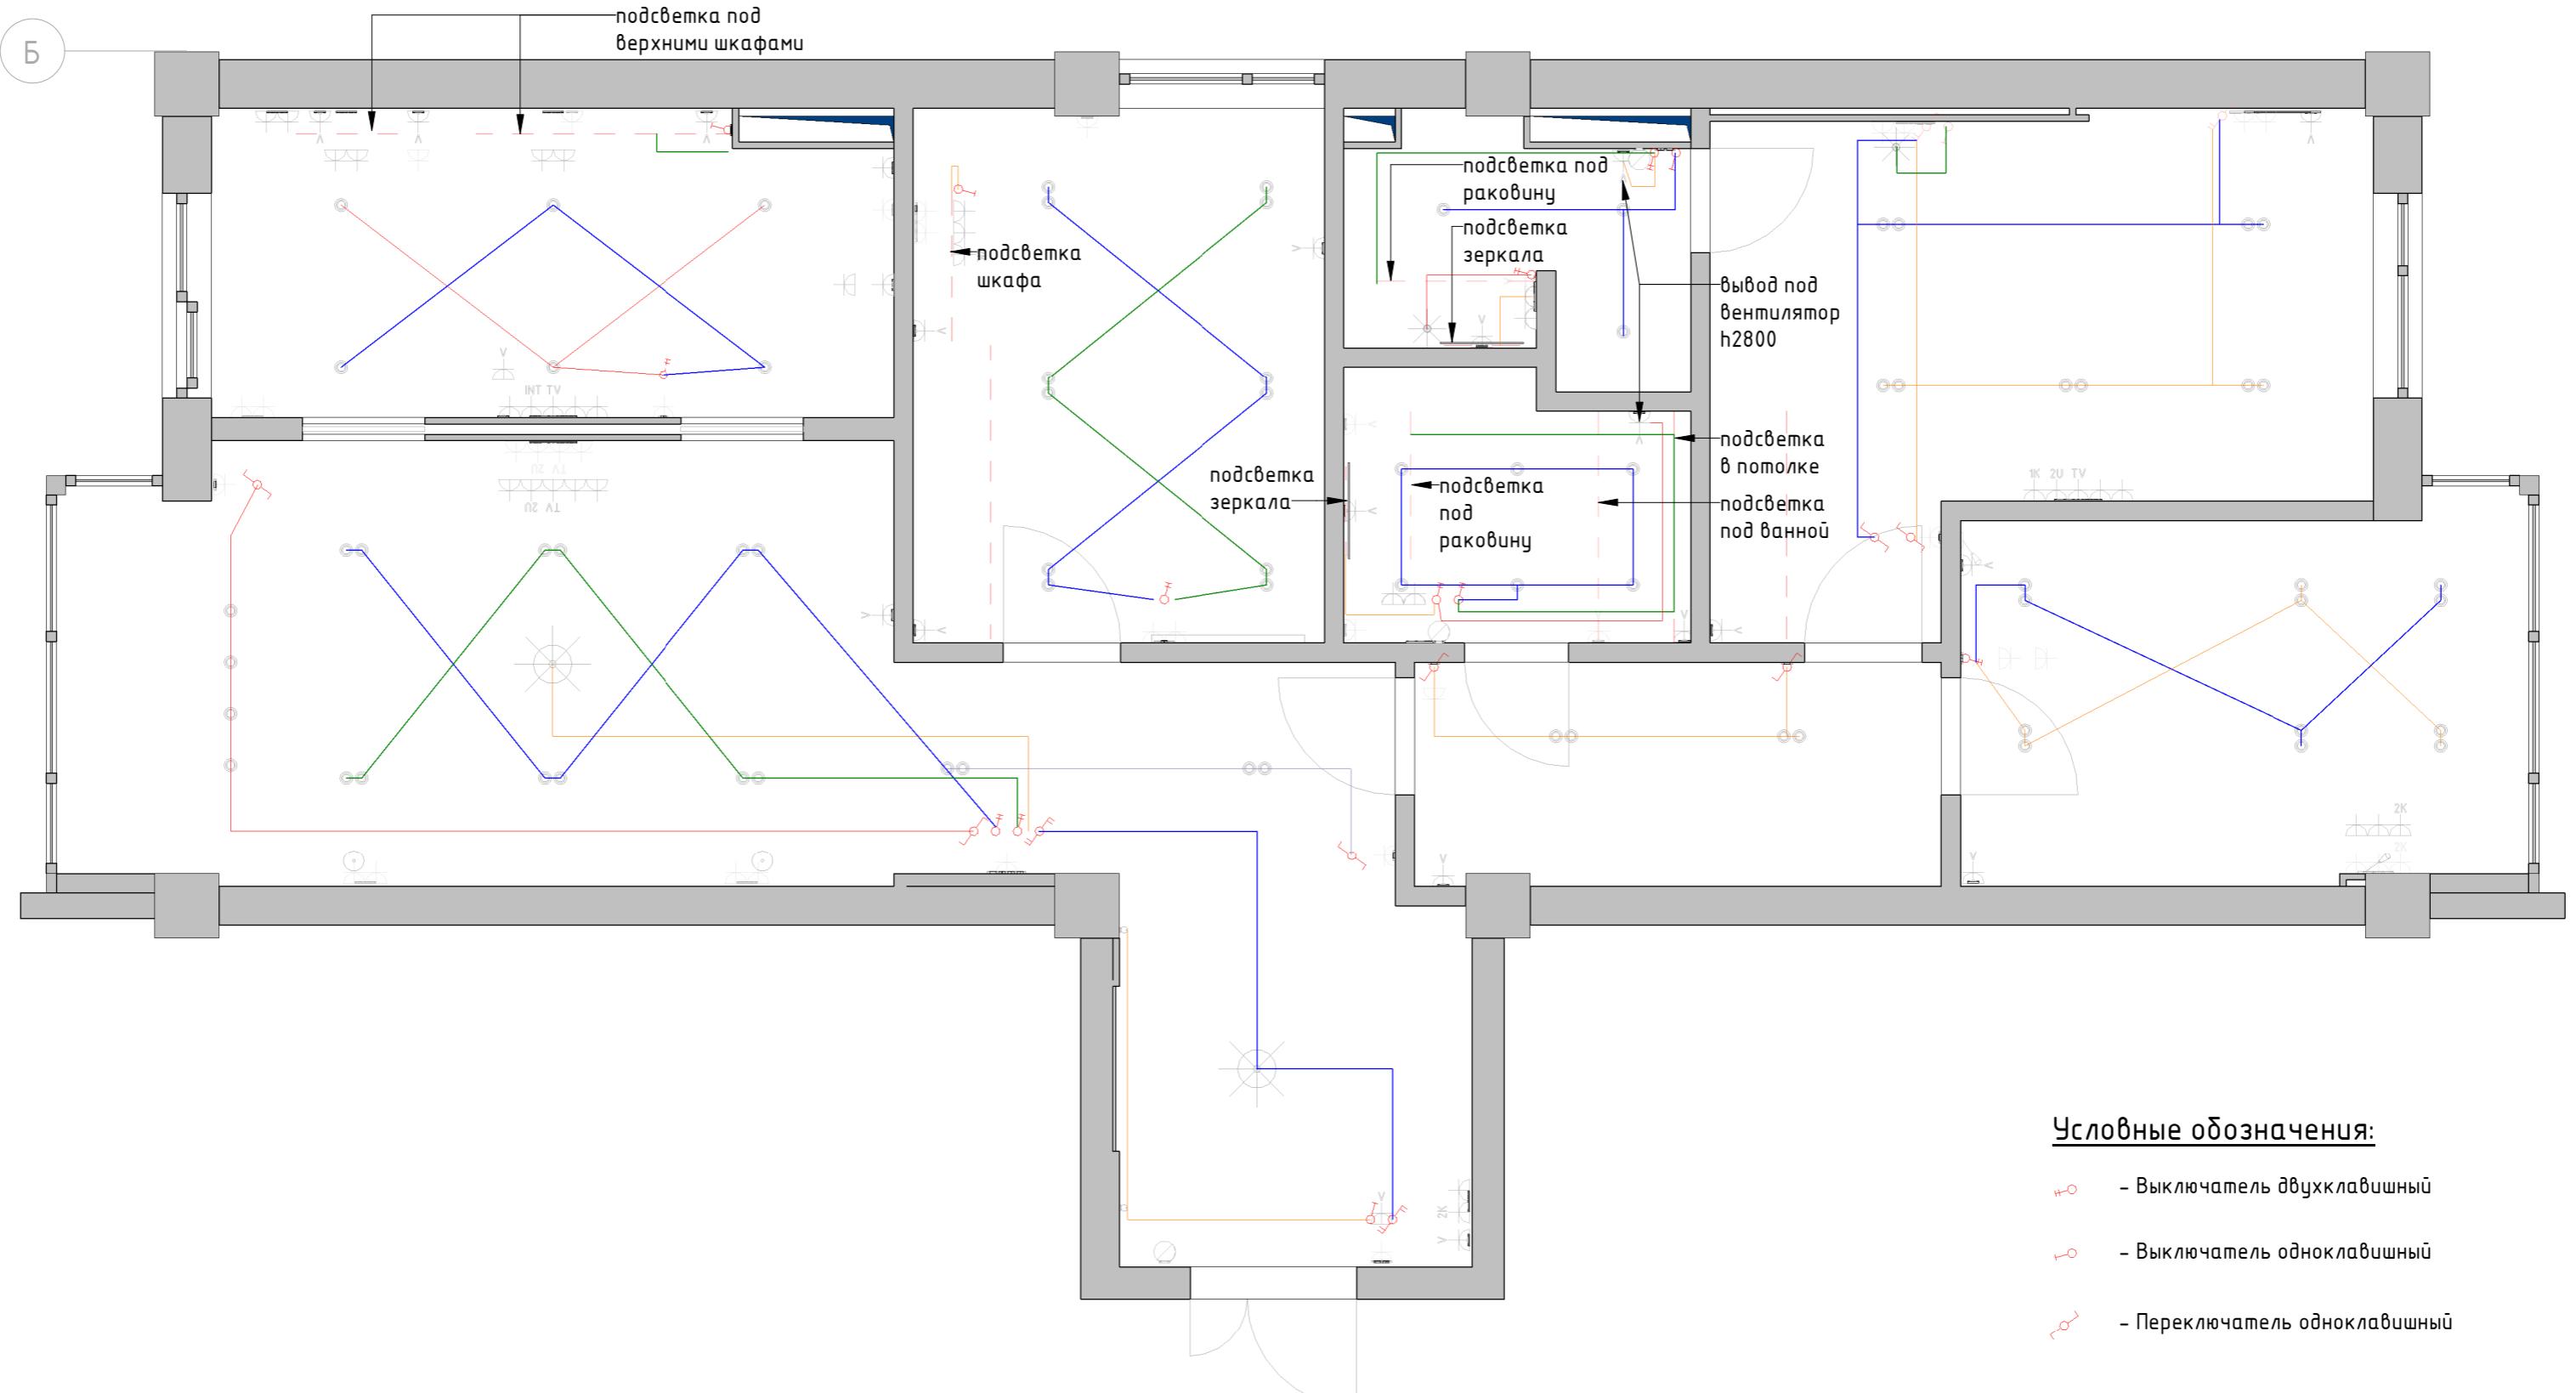

#### Примечание:

Каждая бытовая техника и кондиционеры должны иметь свой самостоятельный провод идущий к электрощиту

#### Условные обозначения:

- Выключатель двухклавишный
- Выключатель одноклавишный
- Переключатель одноклавишный


#### Примечания:

- За отметку 0.000 принята отметка чистого пола квартиры.
- Все размеры уточняются по месту.
- Размеры даны до центра рамки.
- Смотреть совместно с развертками.

Стадия	Лист	Листов
АИ		

ПЛАН ПРИВЯЗКИ ПРИБОРОВ  
ОСВЕЩЕНИЯ К ВЫКЛЮЧАТЕЛЯМ

Luxhouse\_studio

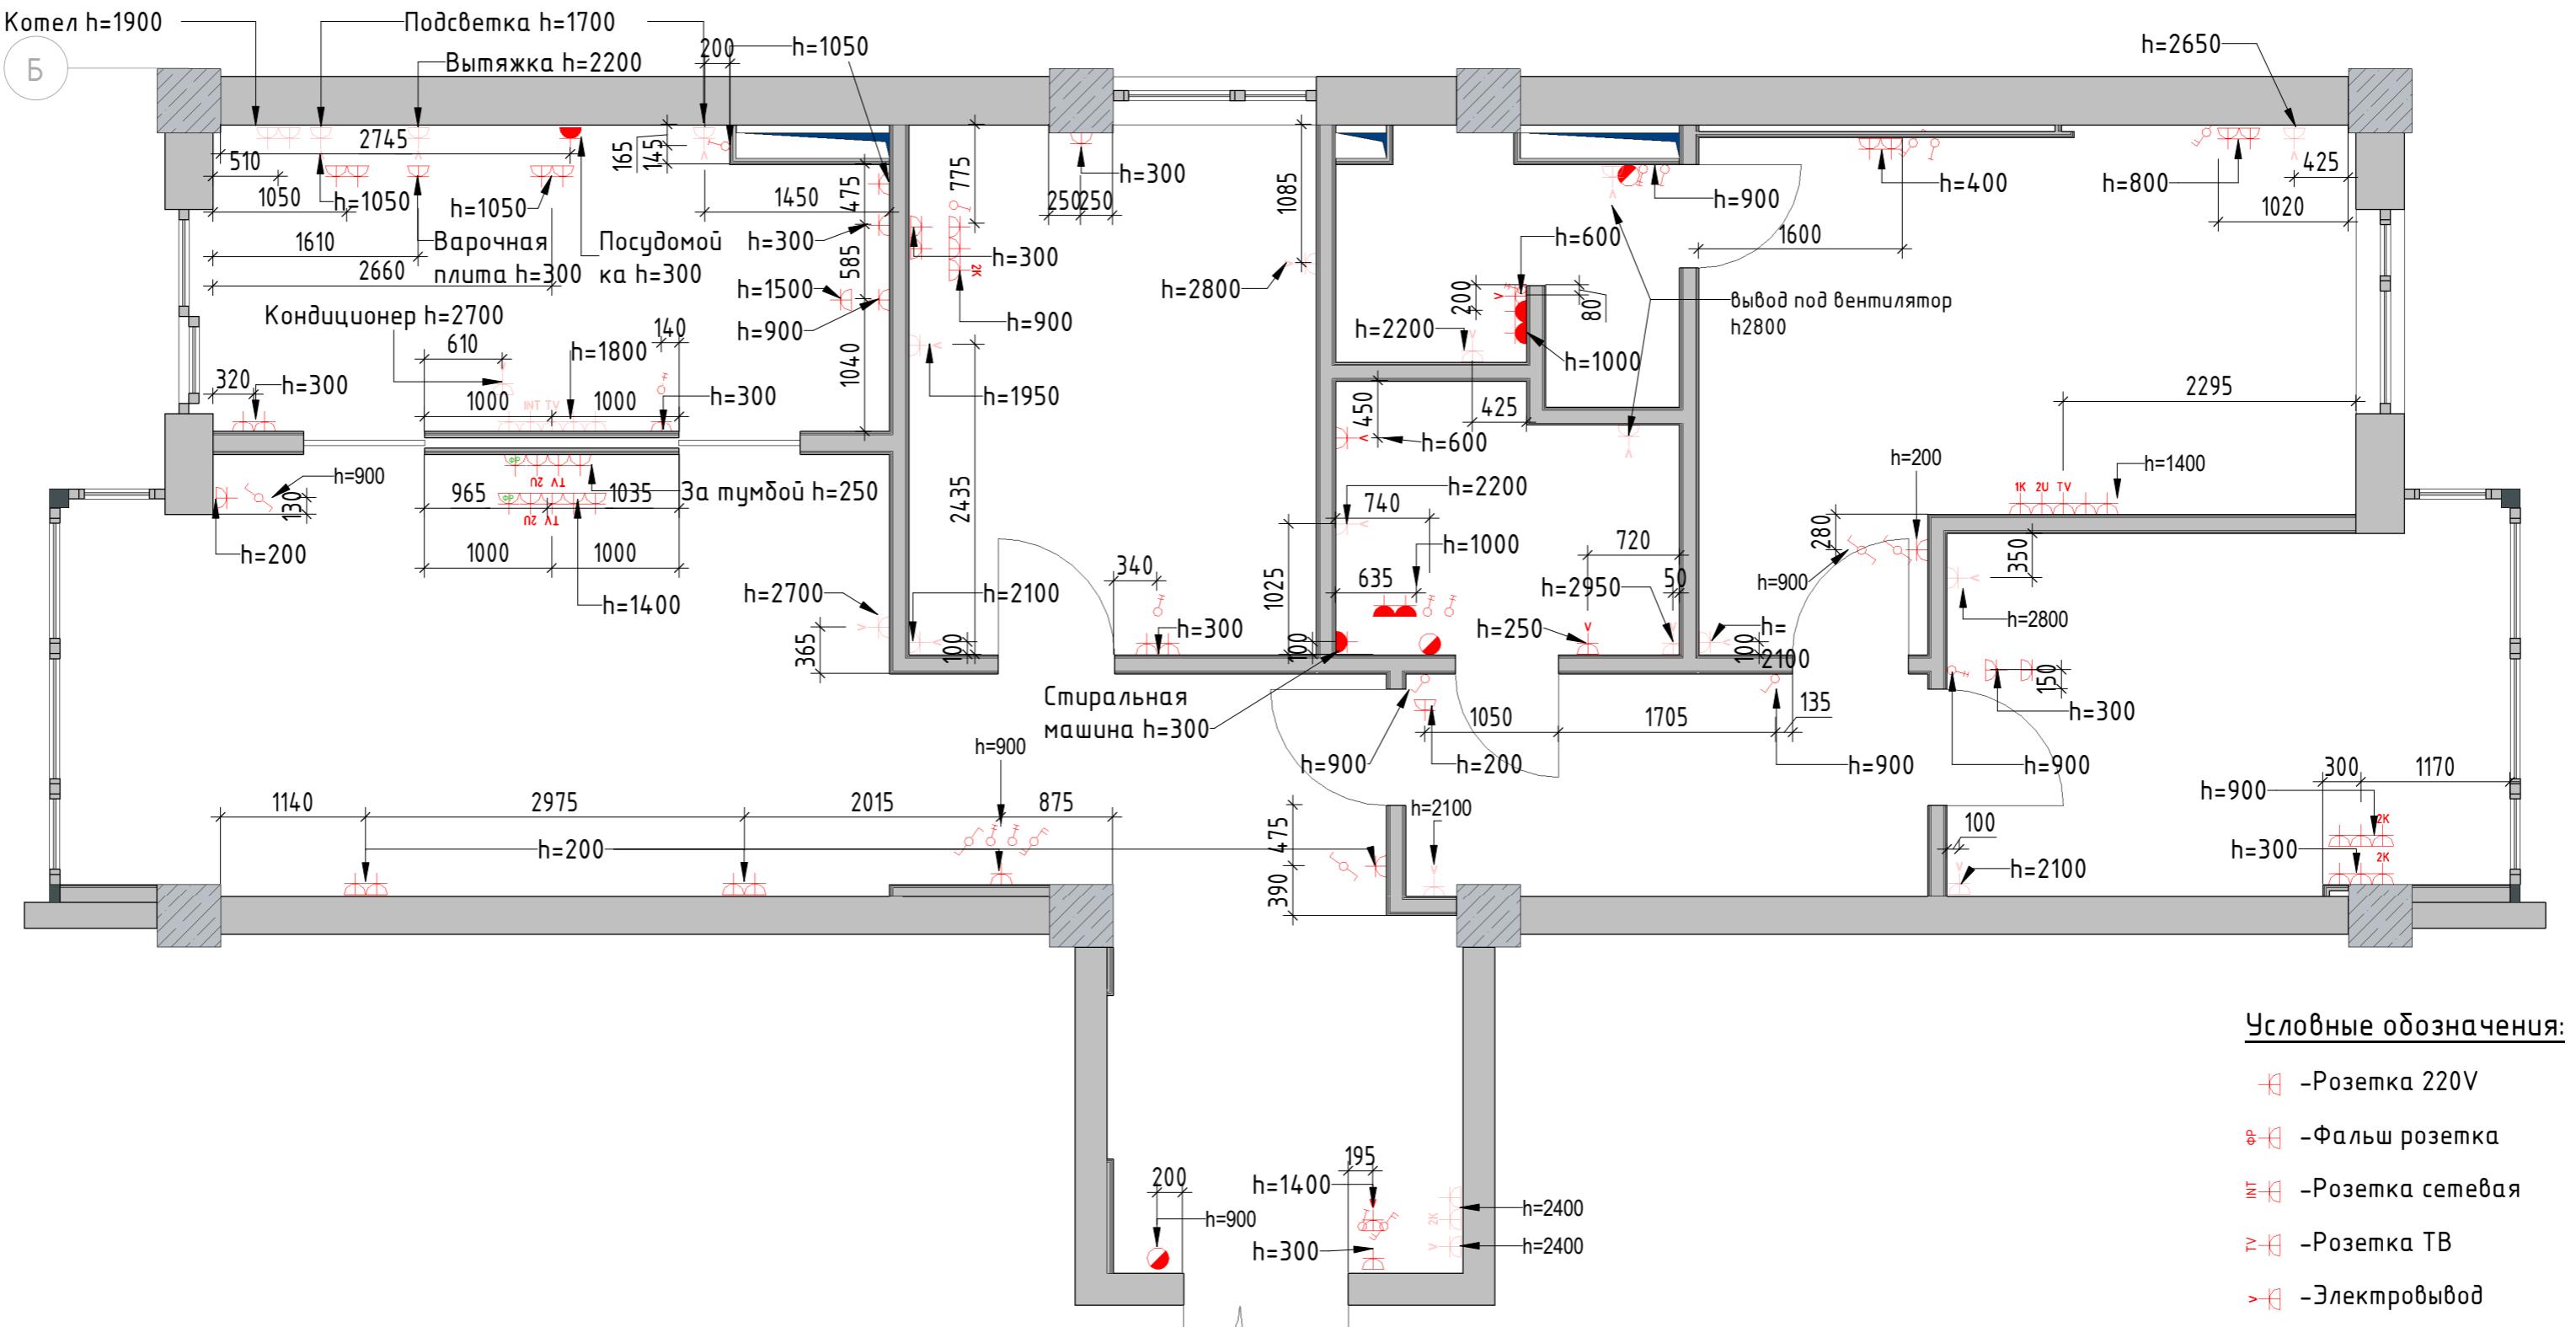

### Примечания:

1. За отметку 0.000 принята отметка чистого пола квартиры.
  2. Все размеры уточняются по месту.
  3. Размеры даны до центра рамки.
  4. Смотреть совместно с развертками.

Стадия	Лист	Листовъ
Дизайнер		
Заказчик		
ПЛАН РАССТАНОВКИ РАЗЕТОК		Luxhouse_studio